

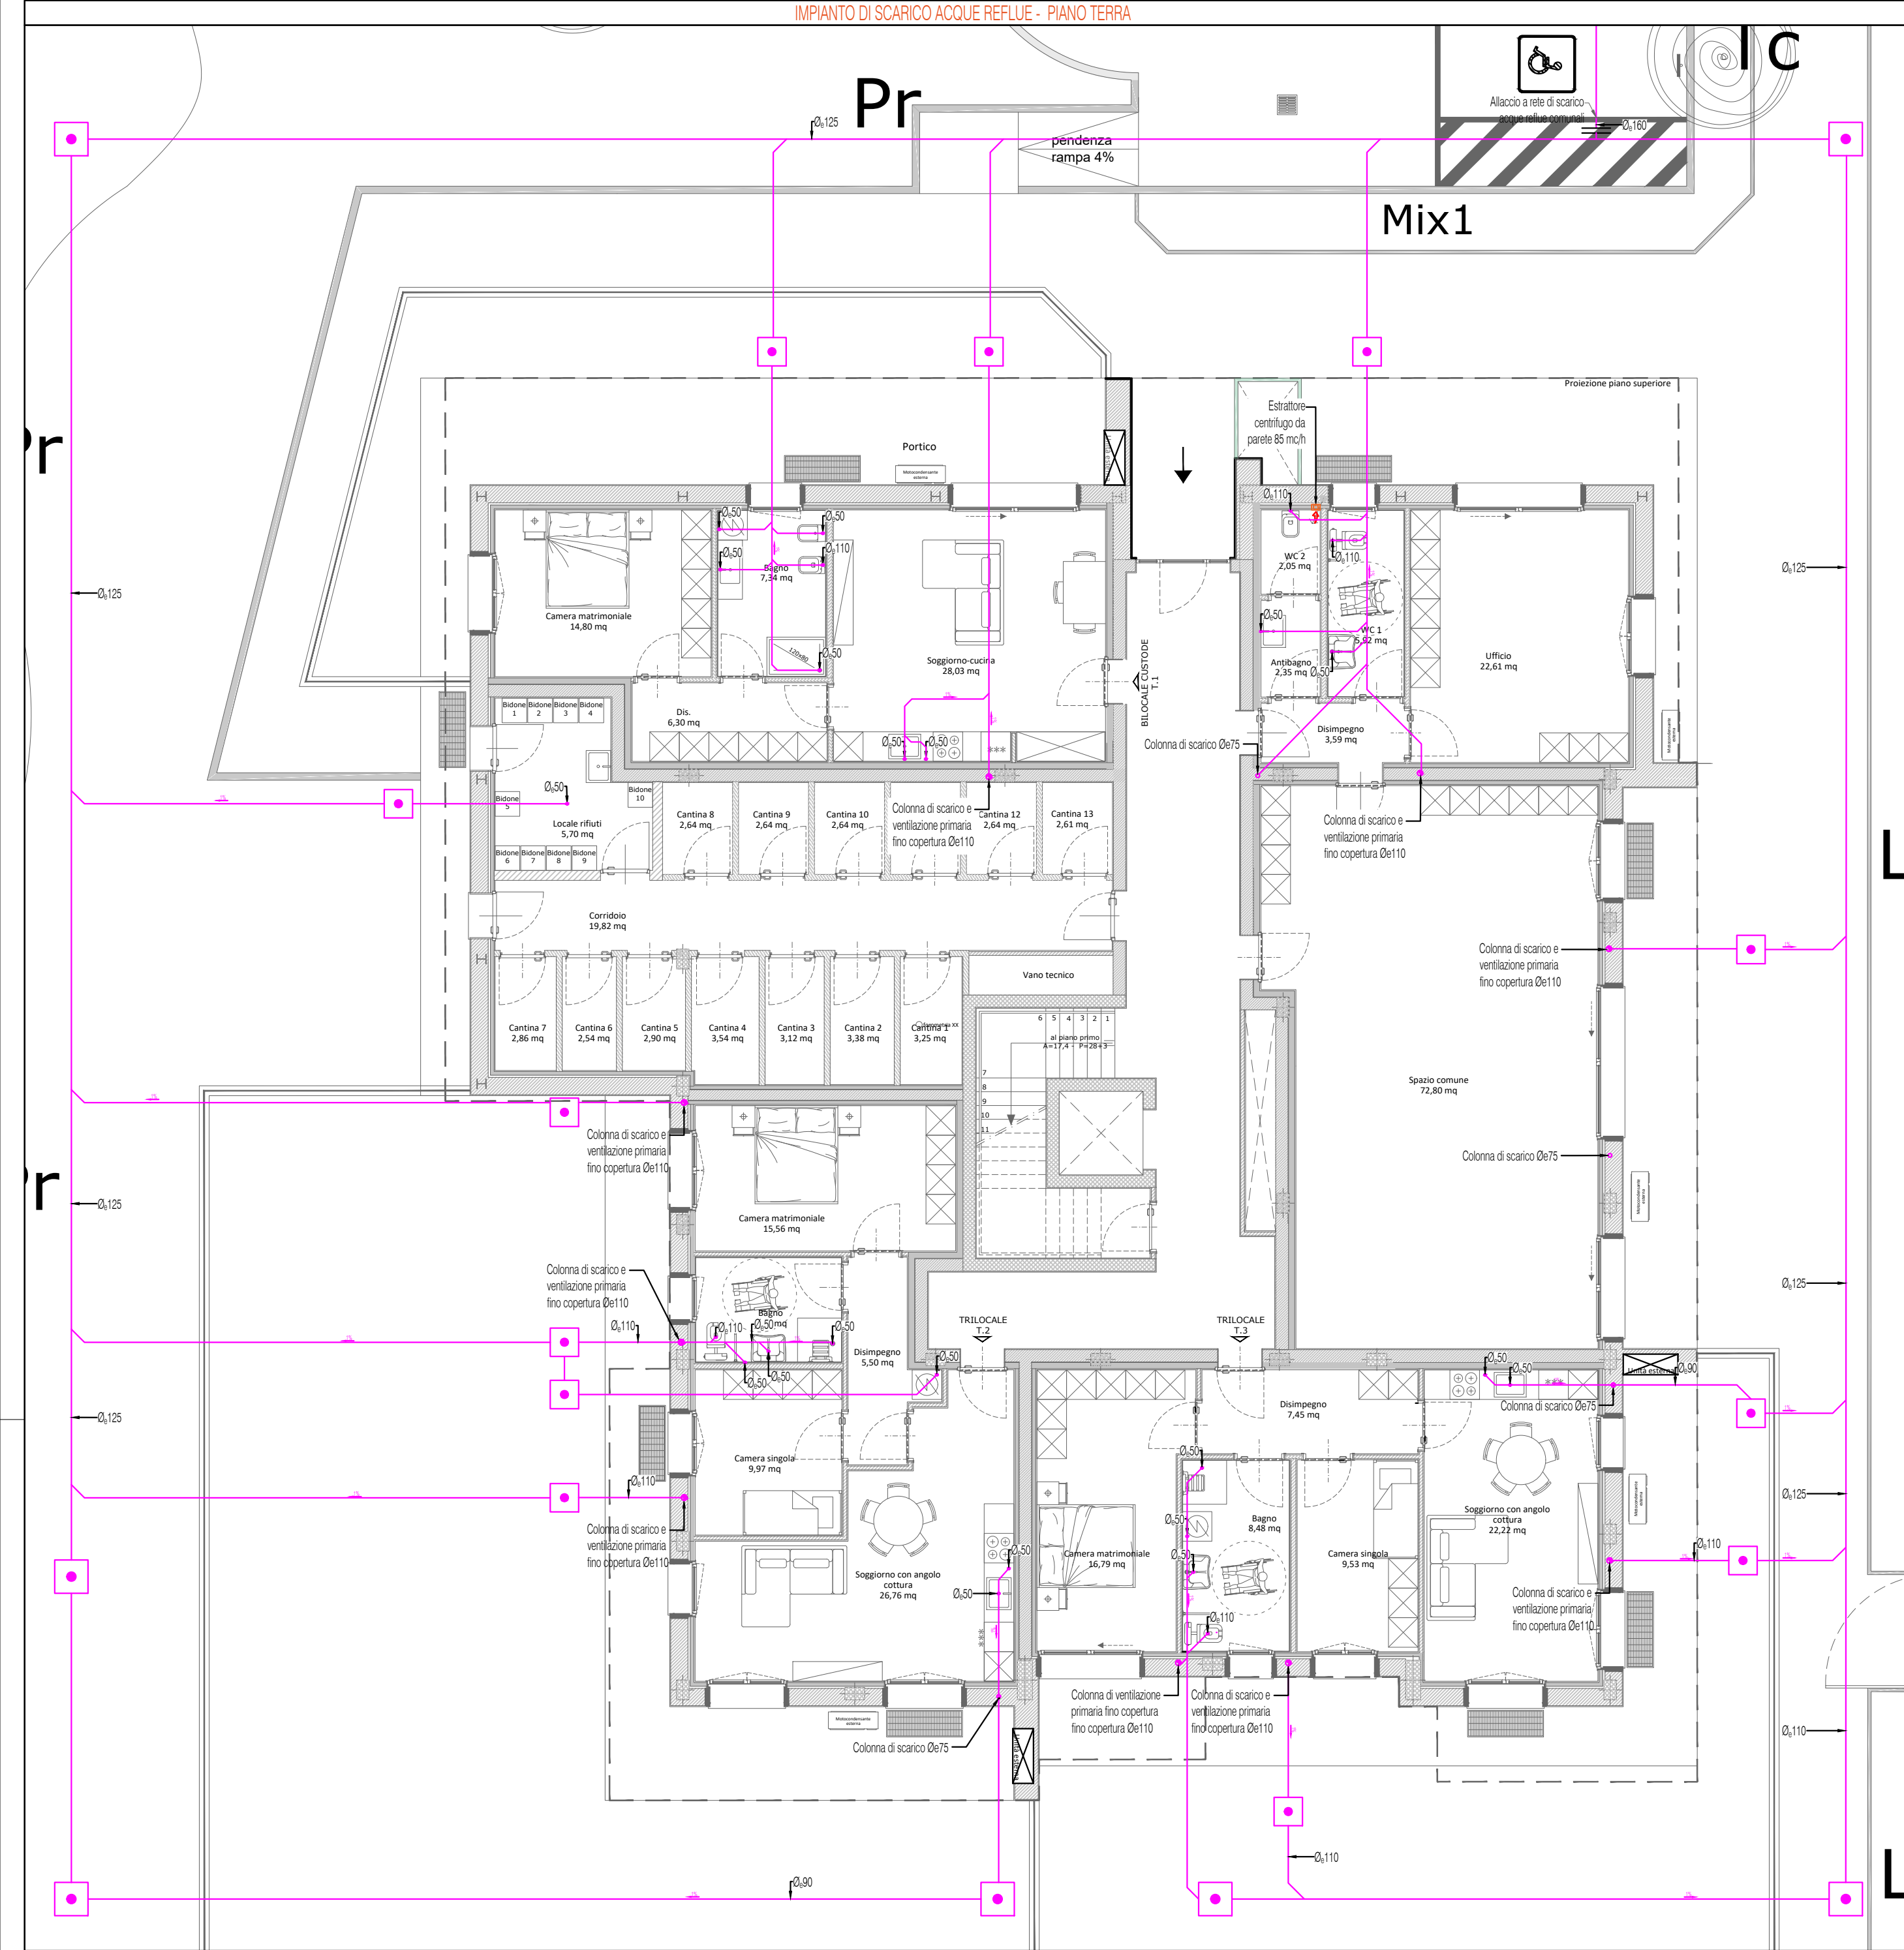


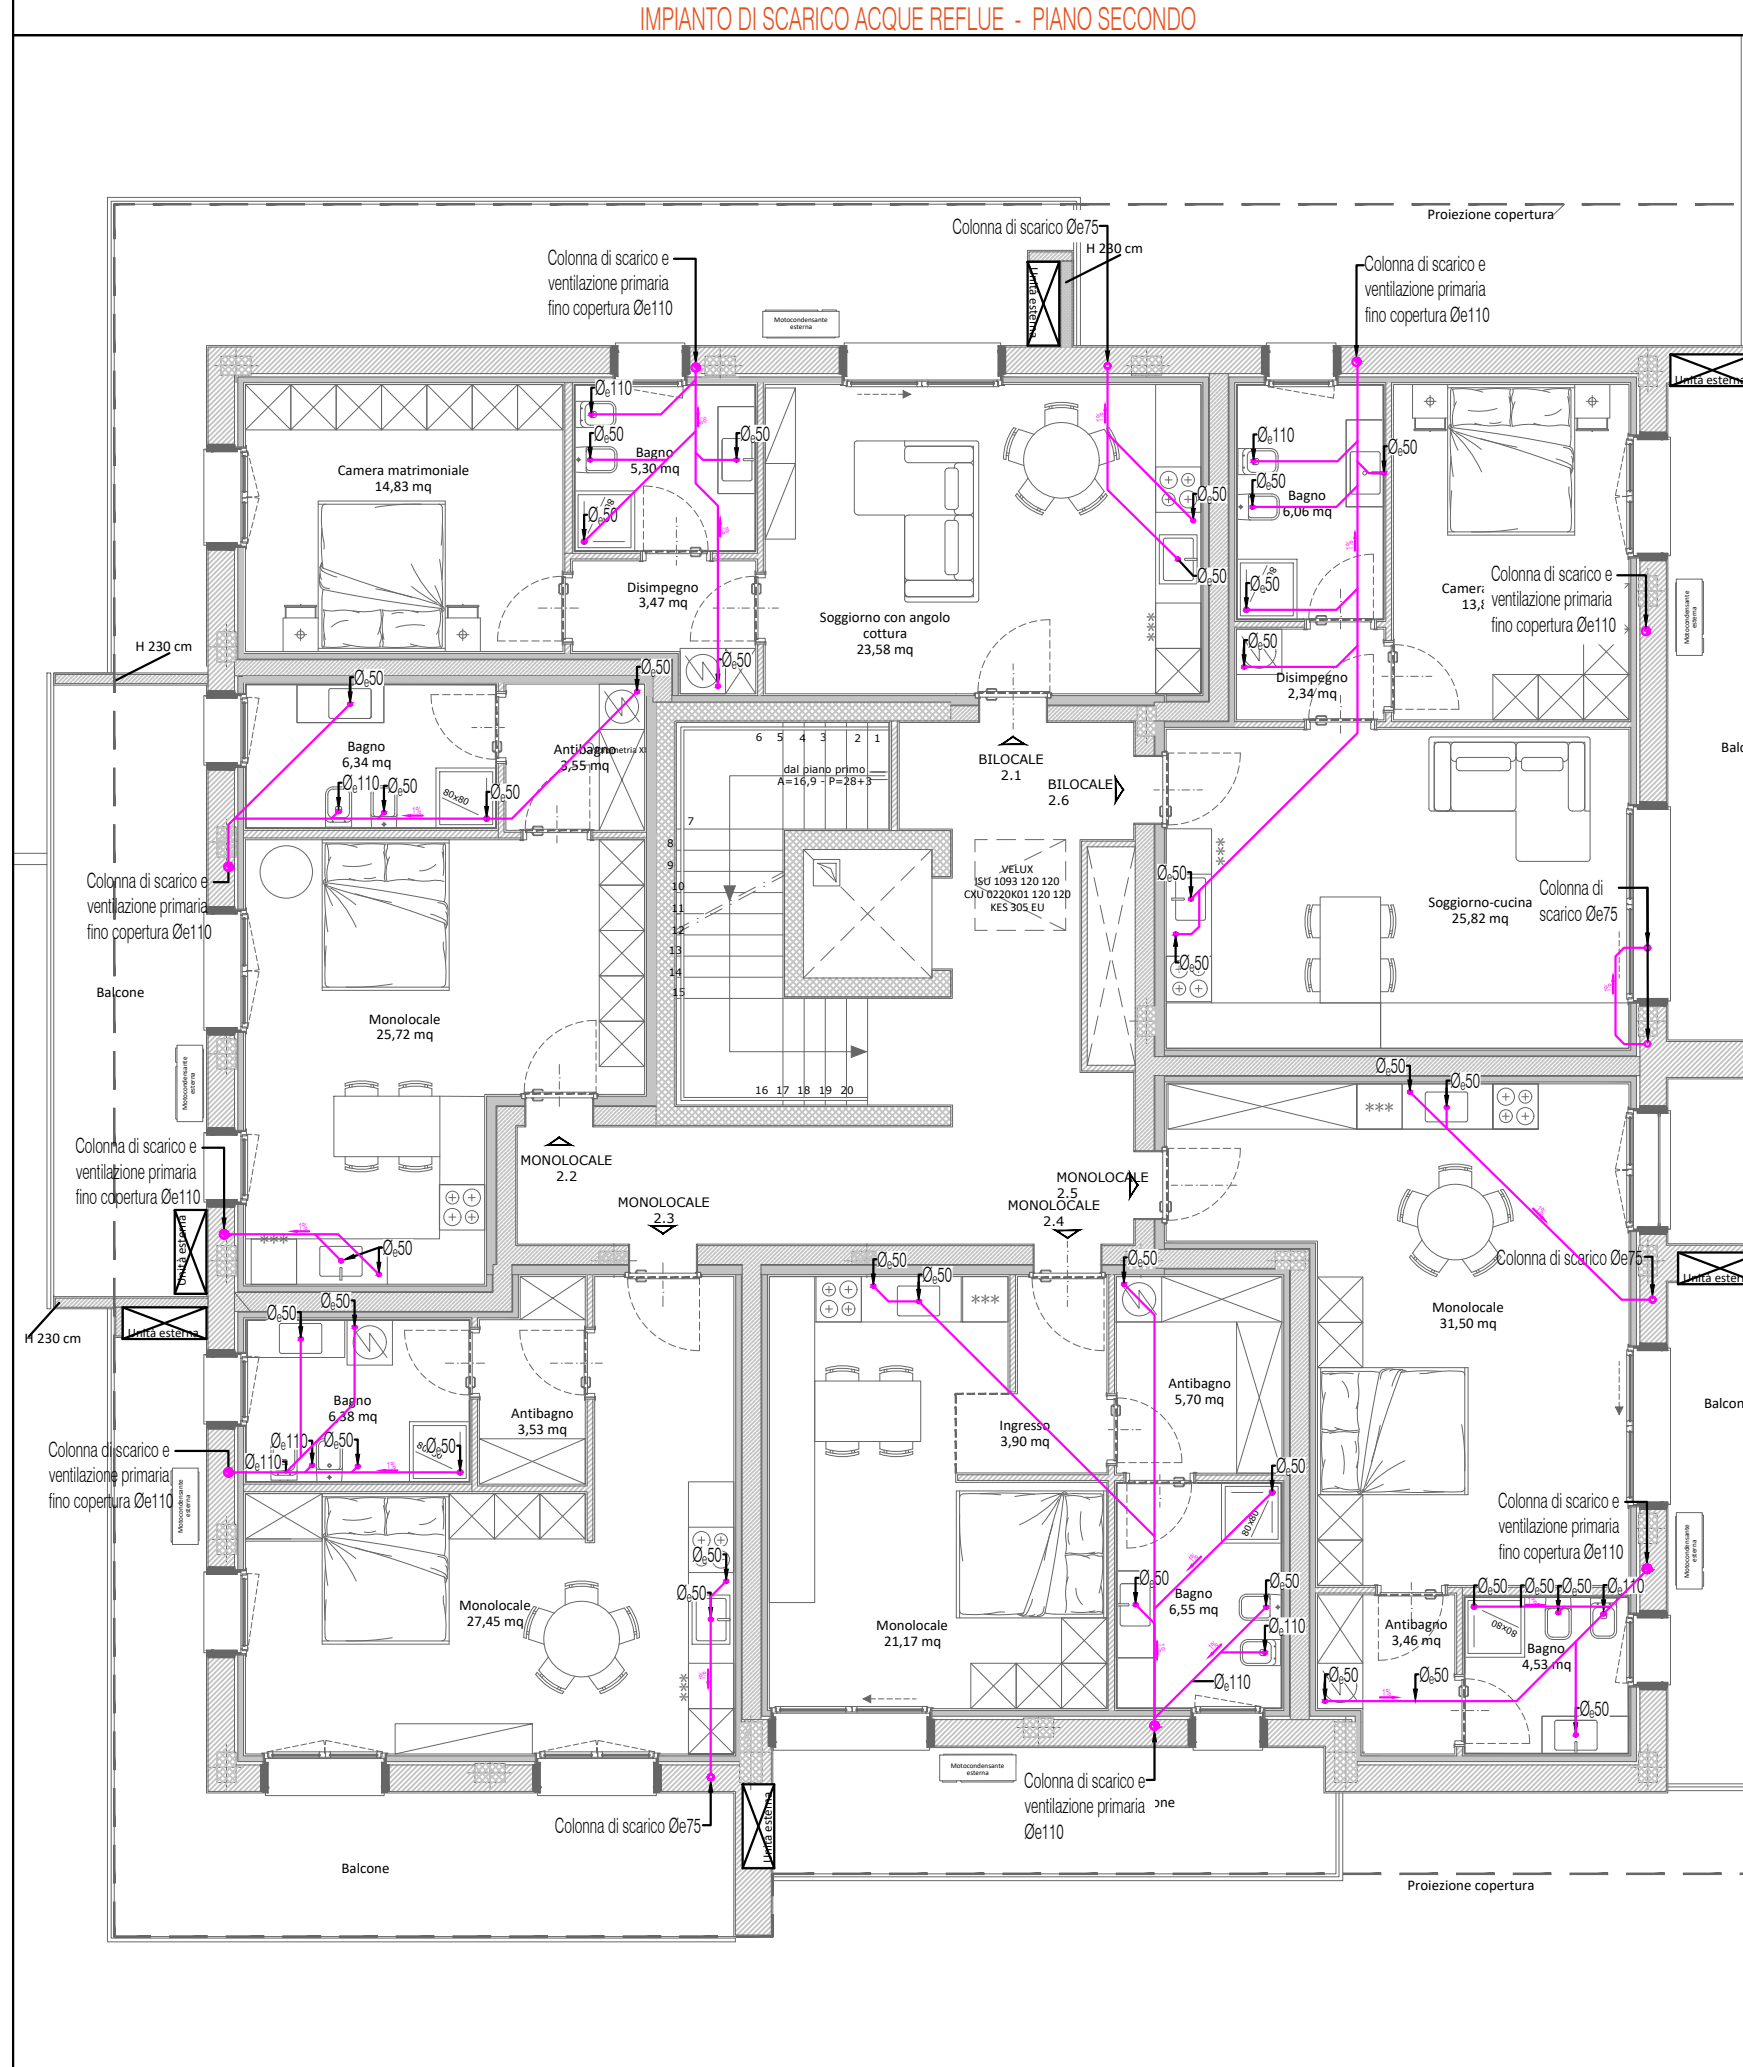

TIPICI DI APPARECCHI SANITARI	USCITA DAL SIFONE ø in millimetri	CONDOTTA DALLACCIAMENTO ø in millimetri
LAVABO, LAVABANDO	40	50
BIDET	40	50
ORINATOIO	40	50
PIATTO DOCCIA	40	50
SIFONE A PAVIMENTO ø60	50	50
SIFONE A PAVIMENTO ø63	63	63
SIFONE A PAVIMENTO ø75	75	75
WC CON RISCACQIO DA Ø8	110	110
WC CON RISCACQIO DA Ø8	110	110

PARTICOLARE TIPICO ESALAZIONE COLONNA DI SCARICO

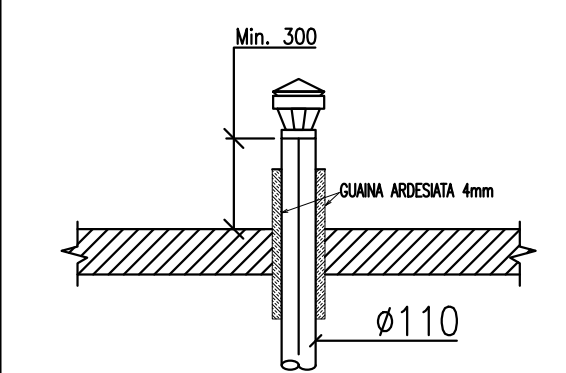

LEGENDA IMPIANTO DI SCARICO

- COLLETTORE SCARICO ACQUE NERE
- RETE DI VENTILAZIONE
- COLONNA DI SCARICO ACQUE NERE
- COLONNA DI SCARICO ACQUE NERE CON VENTILAZIONE PRIMARIA
- PUNTO DI SCARICO SINGOLO UTILIZZATORE
- POZZETTO DI ISPEZIONE
- ESTRAITTORE DA PARETE

NB:
LA RETE ESTERNA DEGLI SCARICHI E' PRESENTE ALL'INTERNO DEL COMPUTO METRICO DEDICATO ALLE OPERE ESTERNE. NON OGGETTO DI COMPUTAZIONE DEL MECCANICO.

NB:
L'ESATTO POSIZIONAMENTO DEI PUNTI DI SCARICO ED IL PASSAGGIO DELLE TUBAZIONI DI SCARICO E VENTILAZIONE ALL'INTERNO DEI CONTROSOFITTI, NEI VESPAI O A PAVIMENTO, DOVRANNO ESSERE SOTTOPOSTI DALL'IMPRESA ESECUTRICE DEI LAVORI ALLA D.L. ANCHE IN RELAZIONE AL LAY-OUT ESECUTIVO ARCHITETTONICO.

NB:
ESEGUIRE GLI SCARICHI CON PENDENZE MINIME PARI A 1.0% NEI TRATTI COMPRESI TRA UTILIZZATORE E DORSALI. PENDENZE MINIME DEL 1.0% PER I COLLETTORI INTERNI, SALVO DIVERSAMENTE SPECIFICATO IN PROGETTO. ESEGUIRE ISPEZIONI OGNI 10 METRI DI SVILUPPO E AL PIEDE DI OGNI COLONNA MONTANTE.

NB:
NELL'ATTRAVERSAMENTO DI EVENTUALI COMPARTIMENTAZIONI PREVEDERE IDONEO MATERIALE/APPARECCHIATURE AL FINE DI GARANTIRE LA CONTINUITA' DELLA COMPARTIMENTAZIONE.

NB:
IL PROGETTO IMPIANTISTICO HA VALENZA PER QUANTO RIGUARDA GLI ASPETTI LEGATI AGLI IMPIANTI STESSI. PER TUTTE LE CARATTERISTICHE E LE MISURE ARCHITETTONICHE E/O STRUTTURALI FANNO FEDE I DISegni DI COMPETENZA.



Dabster srl
Via Sommacampagna 63/H - 37137 Verona
P. IVA 04464890239
mail: mail@dabster.it

COMUNE DI COLOGNO MONZESE (MI)
AREA Ex TORRIANI ARAS 01
PROGETTO ESECUTIVO
Progetto Servizi Abitativi Pubblici di via Pergolesi

N°	DATA	DESCRIZIONE MOTIVAZIONE DELL'AGGIORNAMENTO	STUDIO	DIS.
00	16/01/2026	Prima emissione	G.B.&P.	L.M.

Il Progettista



Progetto
PROGETTO ESECUTIVO
Servizi Abitativi Pubblici
Comune di Cologno Monzese(MI)

Proponente
Officine Mak S.r.l.
Corso Europa, 10
Milano 20122

Scala
1:100
Data
23/01/2026

Tipo tavola
IMPIANTI
Serie
PROGETTO ESECUTIVO
Titolo
IMPIANTI MECCANICI - IMPIANTO DI SCARICO

Tavola nr.
Tipo
Tavola
Sigla /
Serie
Numero /
Variante
Agg.
IMP
ES
02
00

