
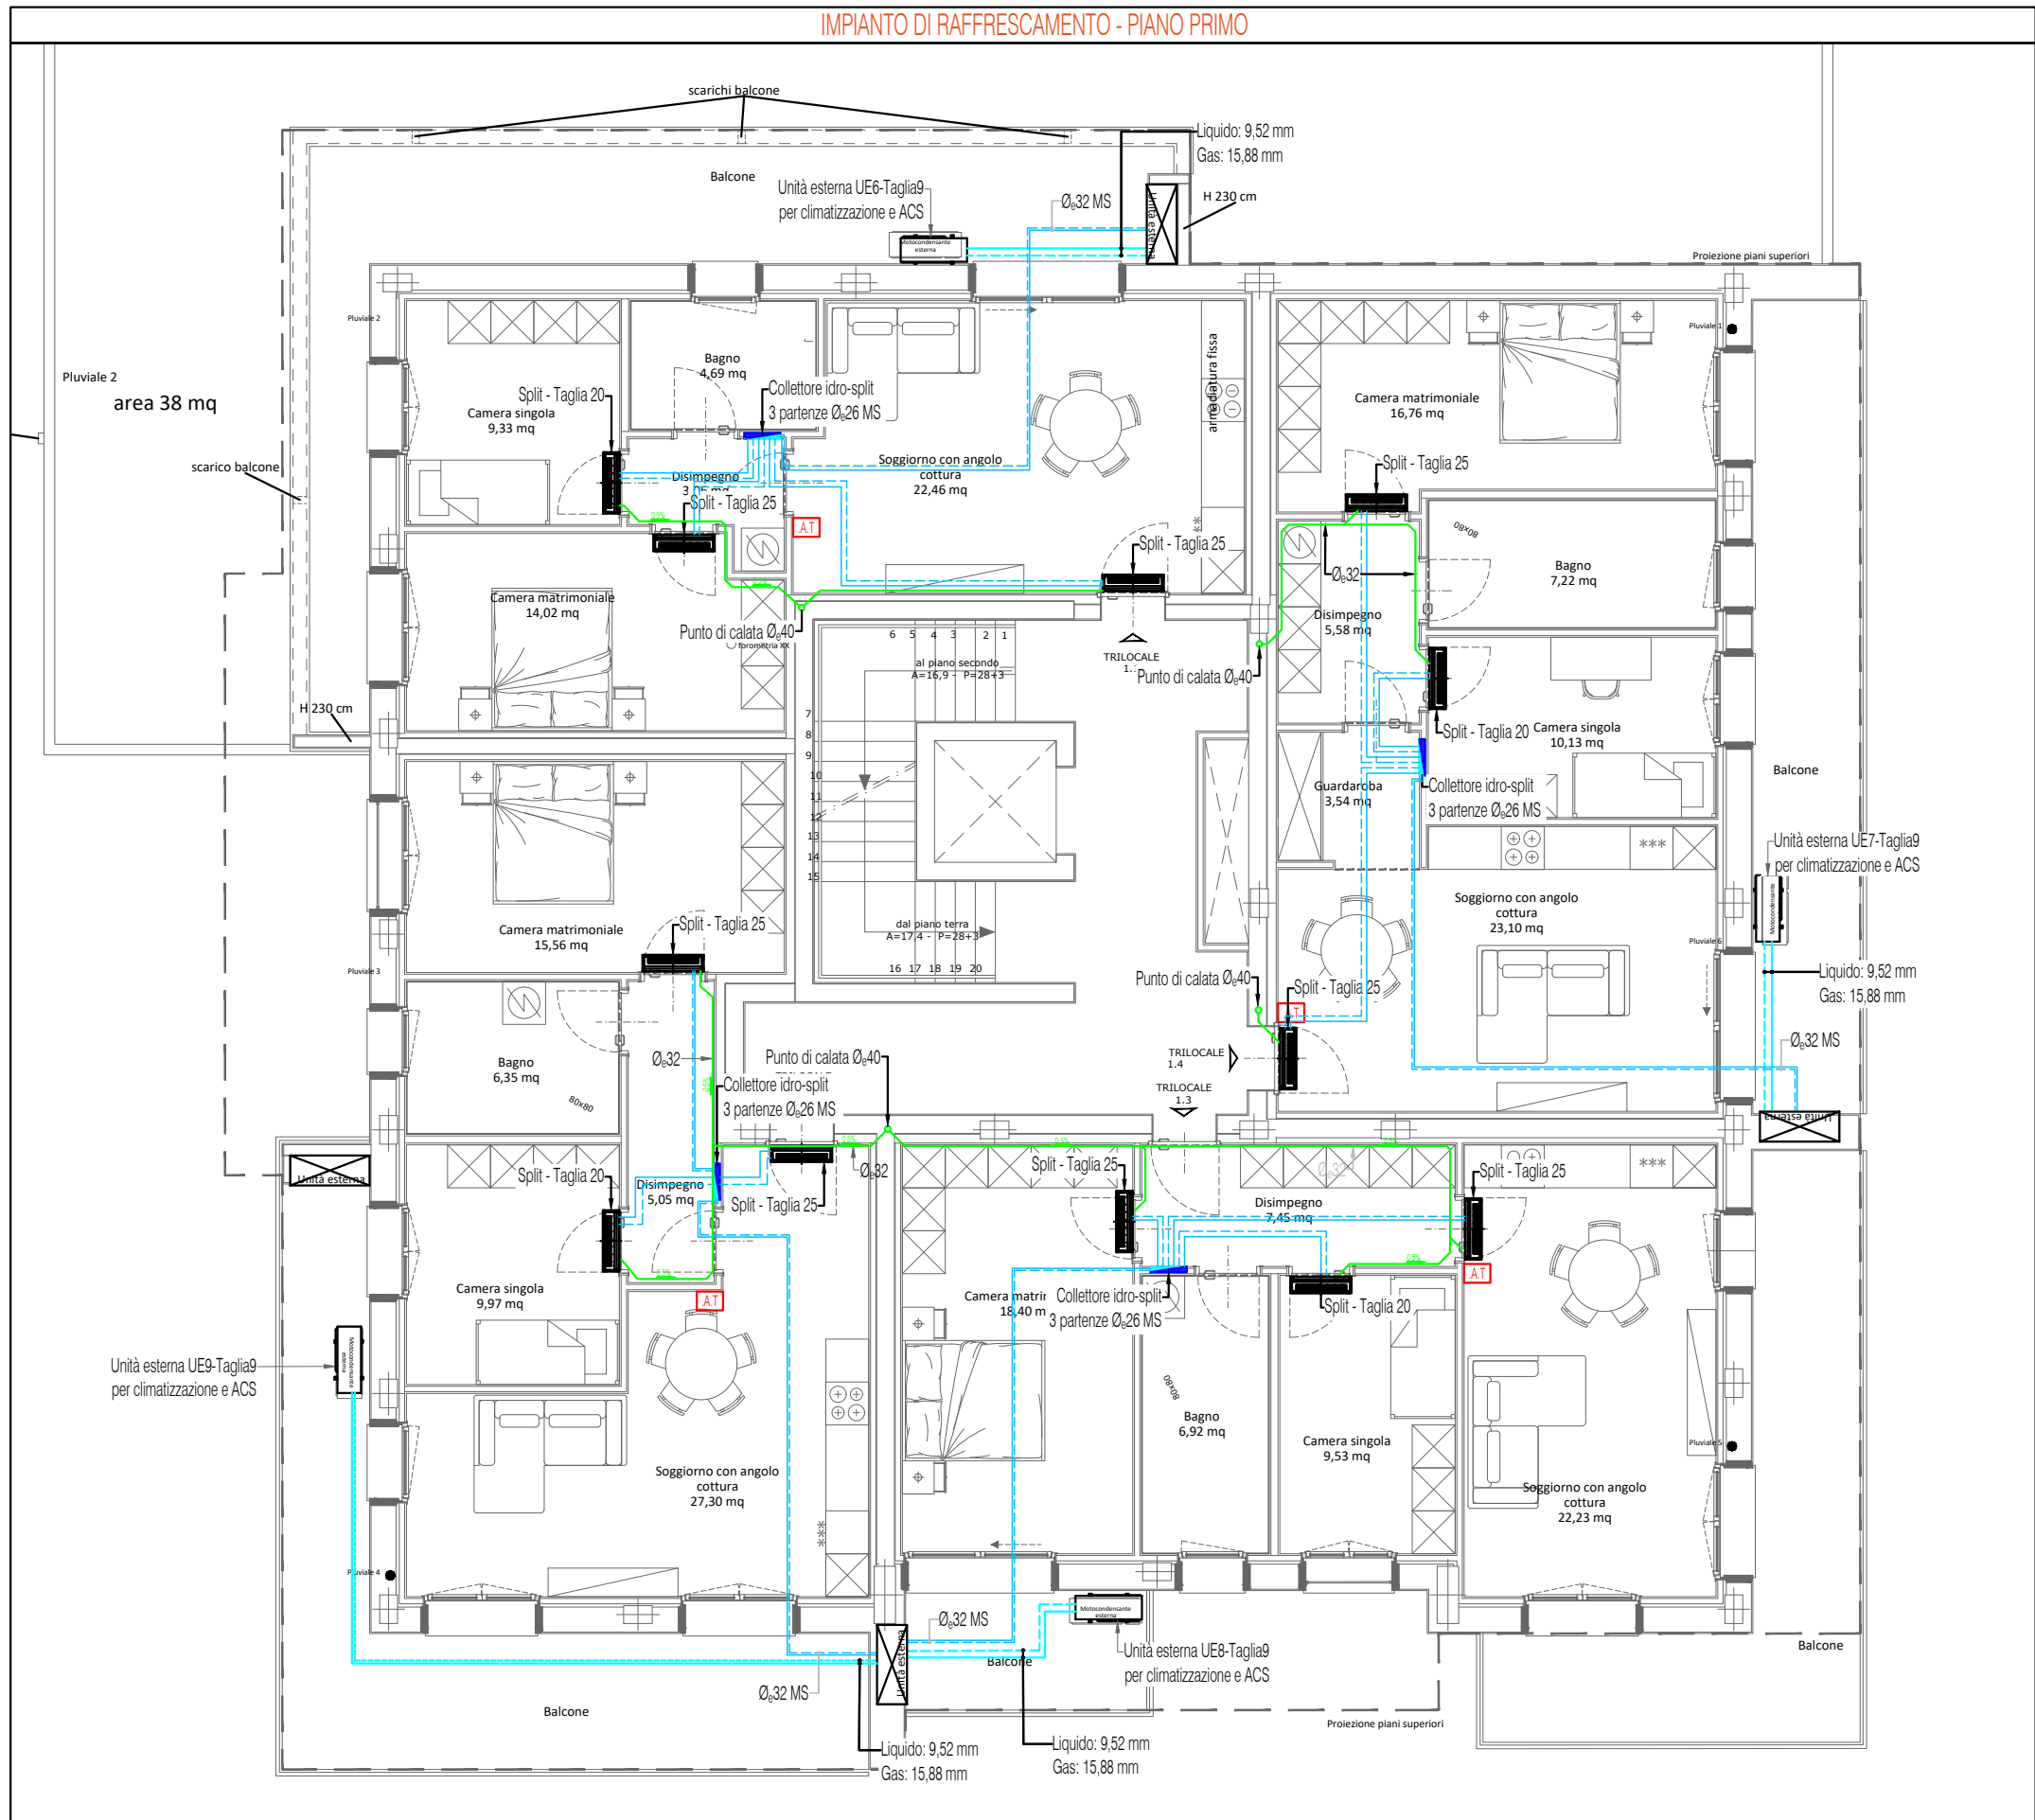


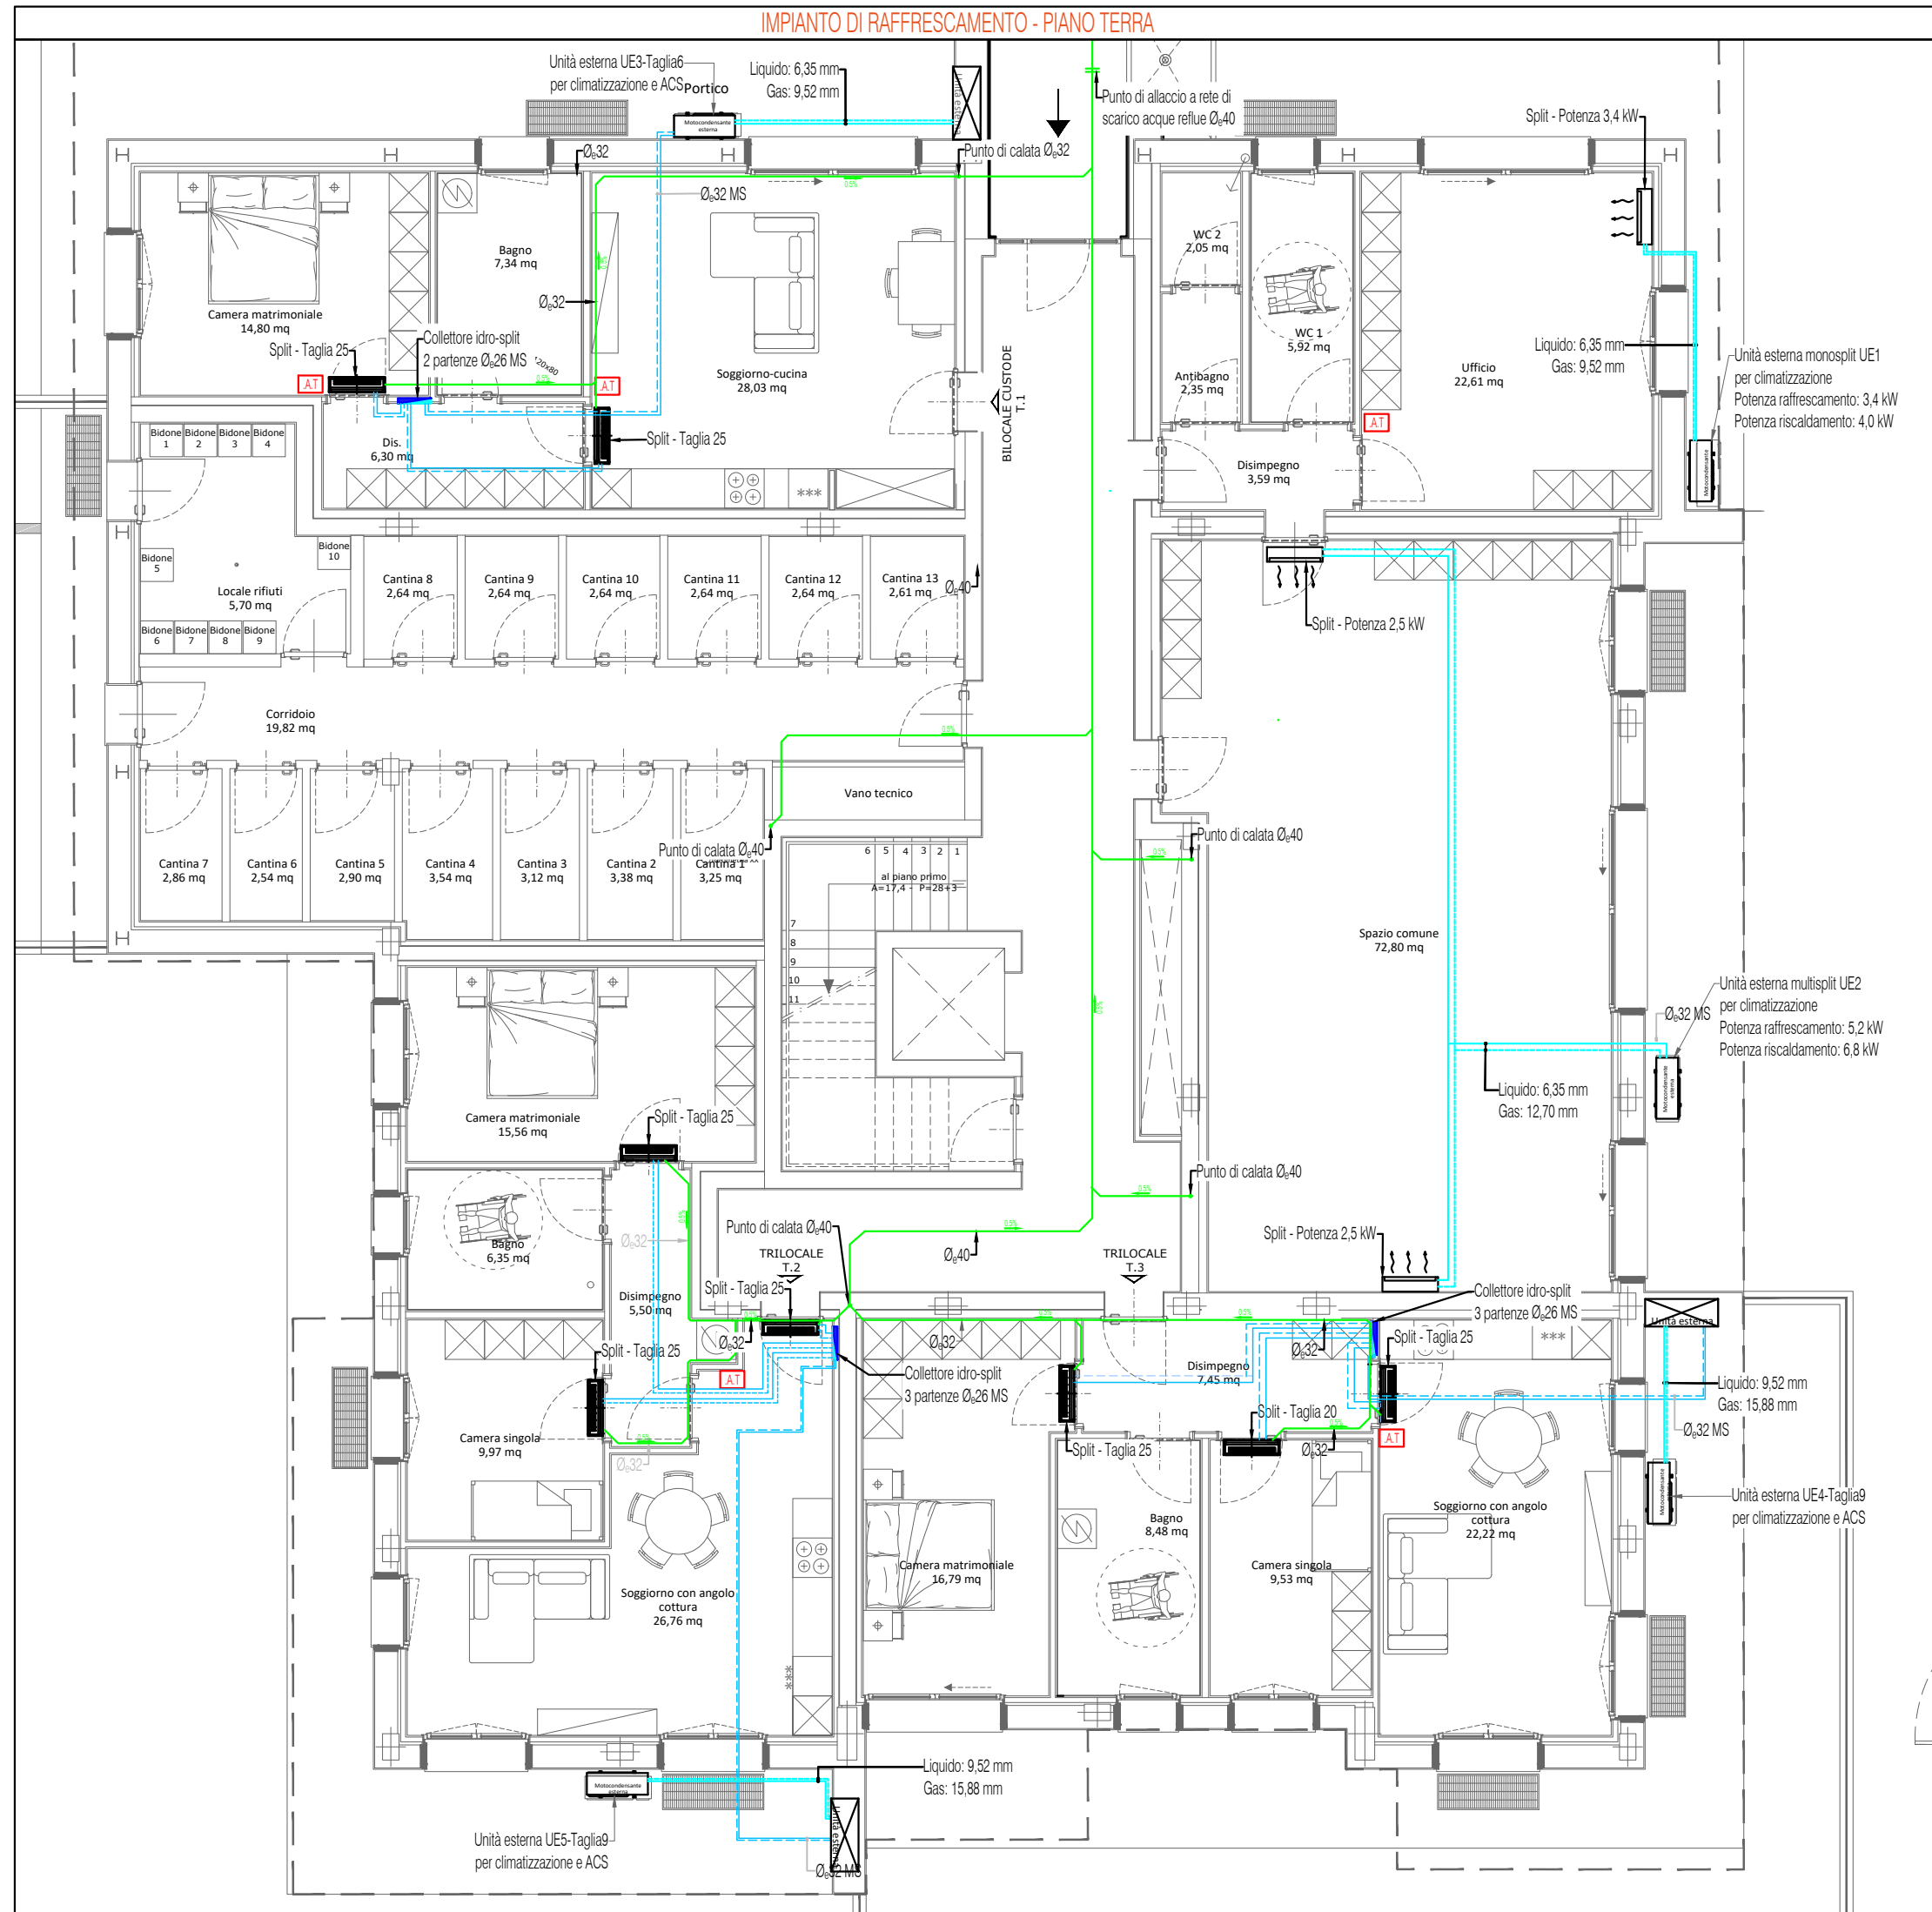

IL PROGETTO IMPIANTISTICO HA VALENZA PER QUANTO RIGUARDA GLI ASPETTI LEGATI AGLI IMPIANTI STESSI. PER TUTTE LE CARATTERISTICHE E LE MISURE ARCHITETTONICHE E CO-STRUTTURALI FANNO FEDE I DISegni DI COMPETENZA.

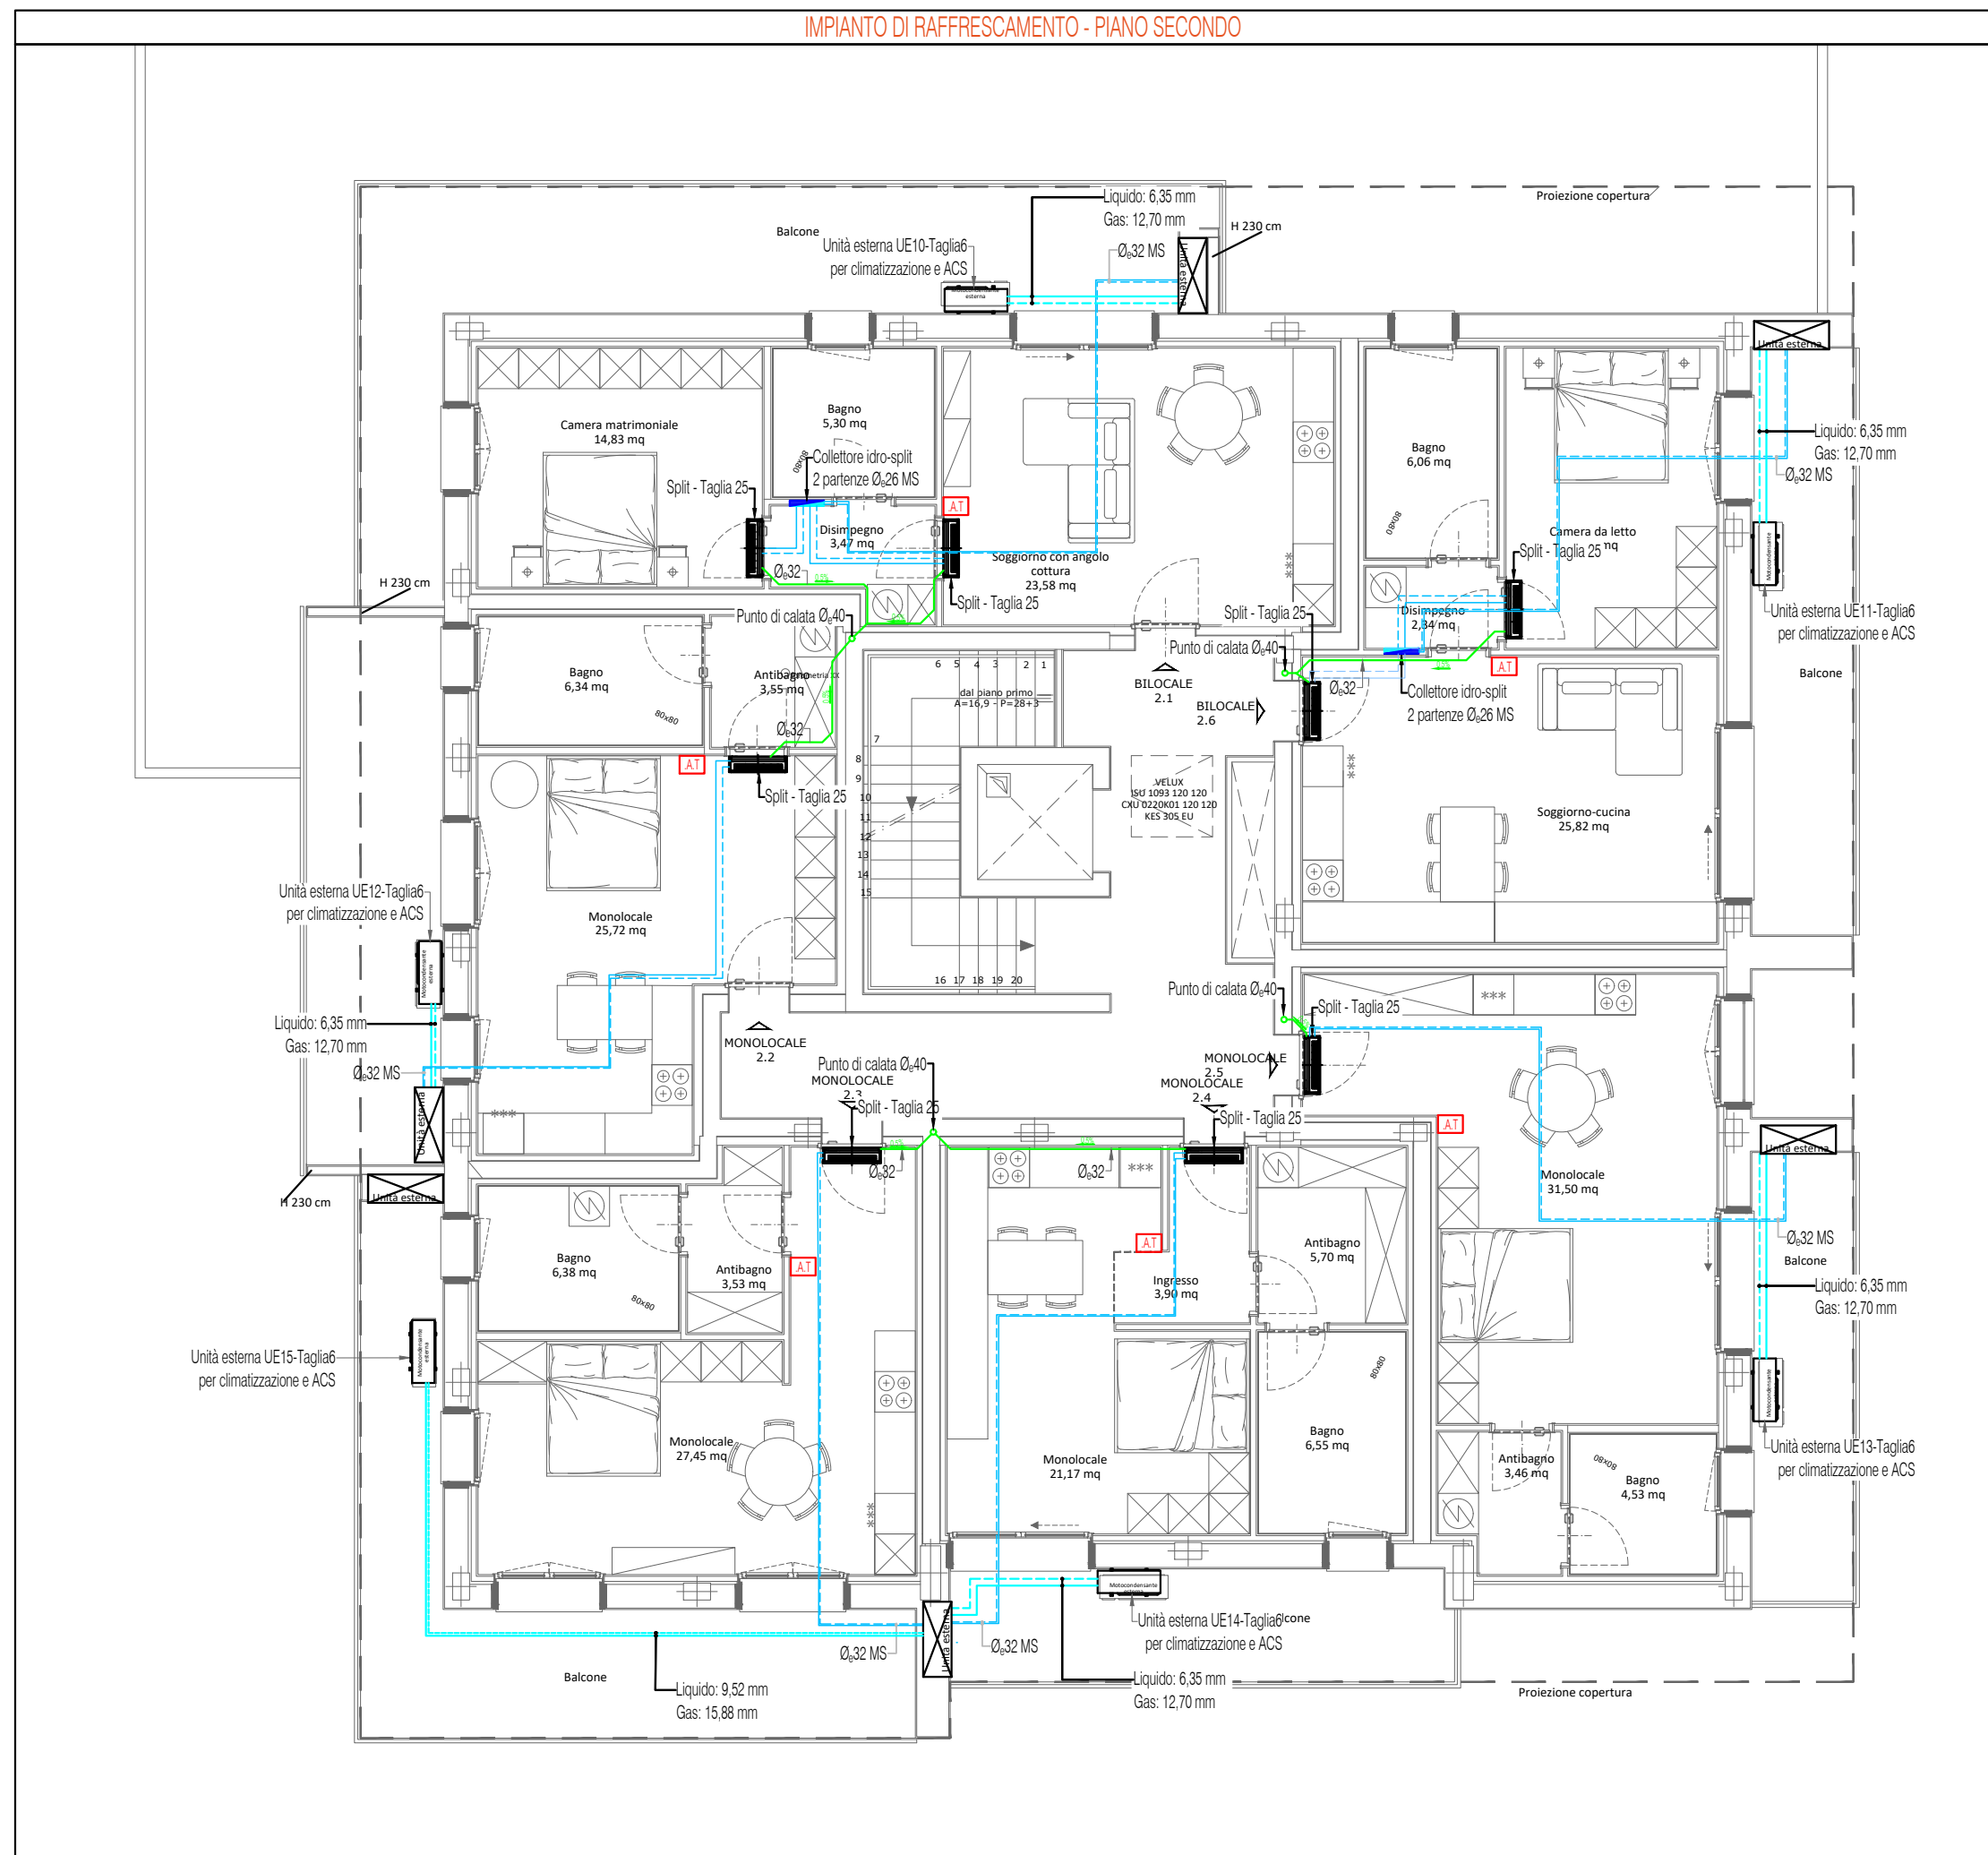


TABELLA CARATTERISTICHE TUBAZIONI IMPIEGATE

MULTISTRATO				
diam. ø	diam. DN	diam. esterno ø e (mm)	Spessore s (mm)	diam. interno ø i (mm)
3/8"	DN 12	16,0	2,25	11,5
1/2"	DN 15	20,0	2,50	15,0
3/4"	DN 20	26,0	3,00	20,0
1"	DN 25	32,0	3,00	26,0
1 1/4"	DN 32	40,0	3,50	33,0
1 1/2"	DN 40	50,0	4,00	42,0
2"	DN 50	63,0	4,50	54,0

TABELLA CARATTERISTICHE TUBAZIONI IMPIEGATE

RAME (impianti espansione diretta)		
diam. esterno ø e (mm)	Spessore s (mm)	diam. interno ø i (mm)
6.4	0.80	4.80
9.5	0.80	7.90
12.7	0.80	11.10
15.9	1.00	13.90
19.1	0.80	16.00
22.2	0.80	17.50
28.6	1.00	26.60
34.9	1.21	32.50
41.3	1.43	38.44

GB&PARTNERS
SERVIZI E PROGETTI IMMOBILIARI

dabster
ENGINEERING

Progetto impianti

COMUNE DI COLOGNO MONZESE (MI)
AREA Ex TORRIANI ARAS 01
PROGETTO ESECUTIVO
Progetto Servizi Abitativi Pubblici di via Pergolesi

N° DATA DESCRIZIONE MOTIVAZIONE DELL'AGGIORNAMENTO STUDIO DIS.

00 16/01/2026 Prima emissione G.B.&P. L.M.

Progetto
PROGETTO ESECUTIVO
Servizi Abitativi Pubblici
Comune di Cologno Monzese(MI)

Proponente
Officine Mak S.r.l.
Corso Europa, 10
Milano 20122

Scala
1:100
Data
23/01/2026

Tipo tavola
IMPIANTI
Serie
PROGETTO ESECUTIVO
Titolo
IMPIANTI MECCANICI -
IMPIANTO DI RAFFRESCAMENTO

Tavola nr.
IMP
Sigla / Serie
ES
Numero / Variante
02
Agg.
00

Orientamento

N