
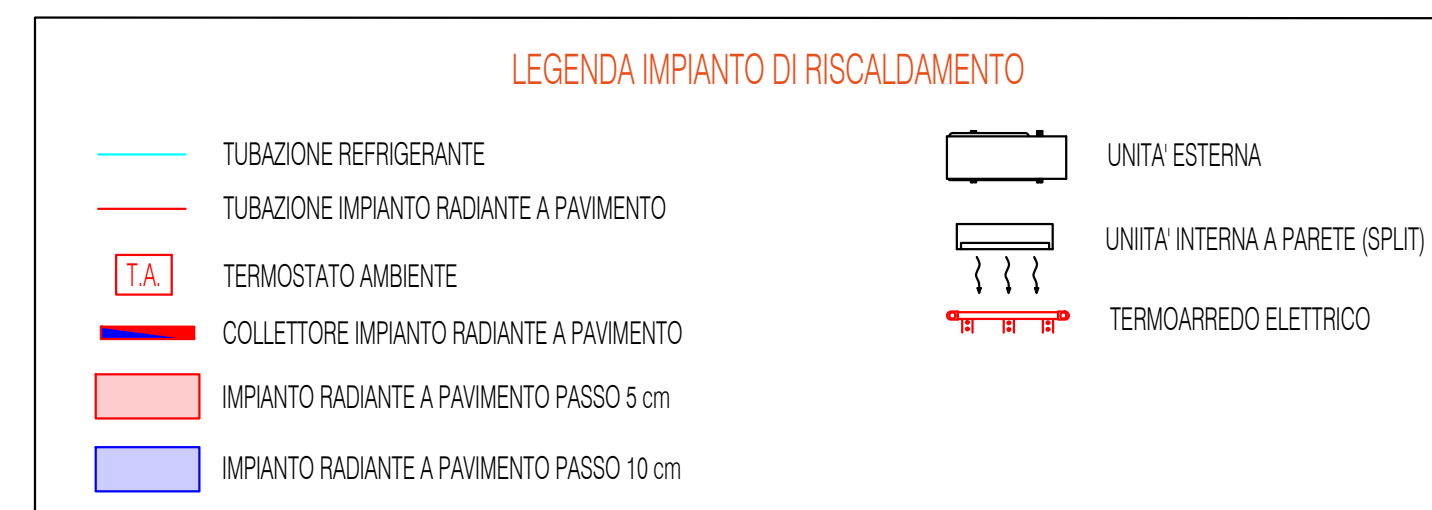
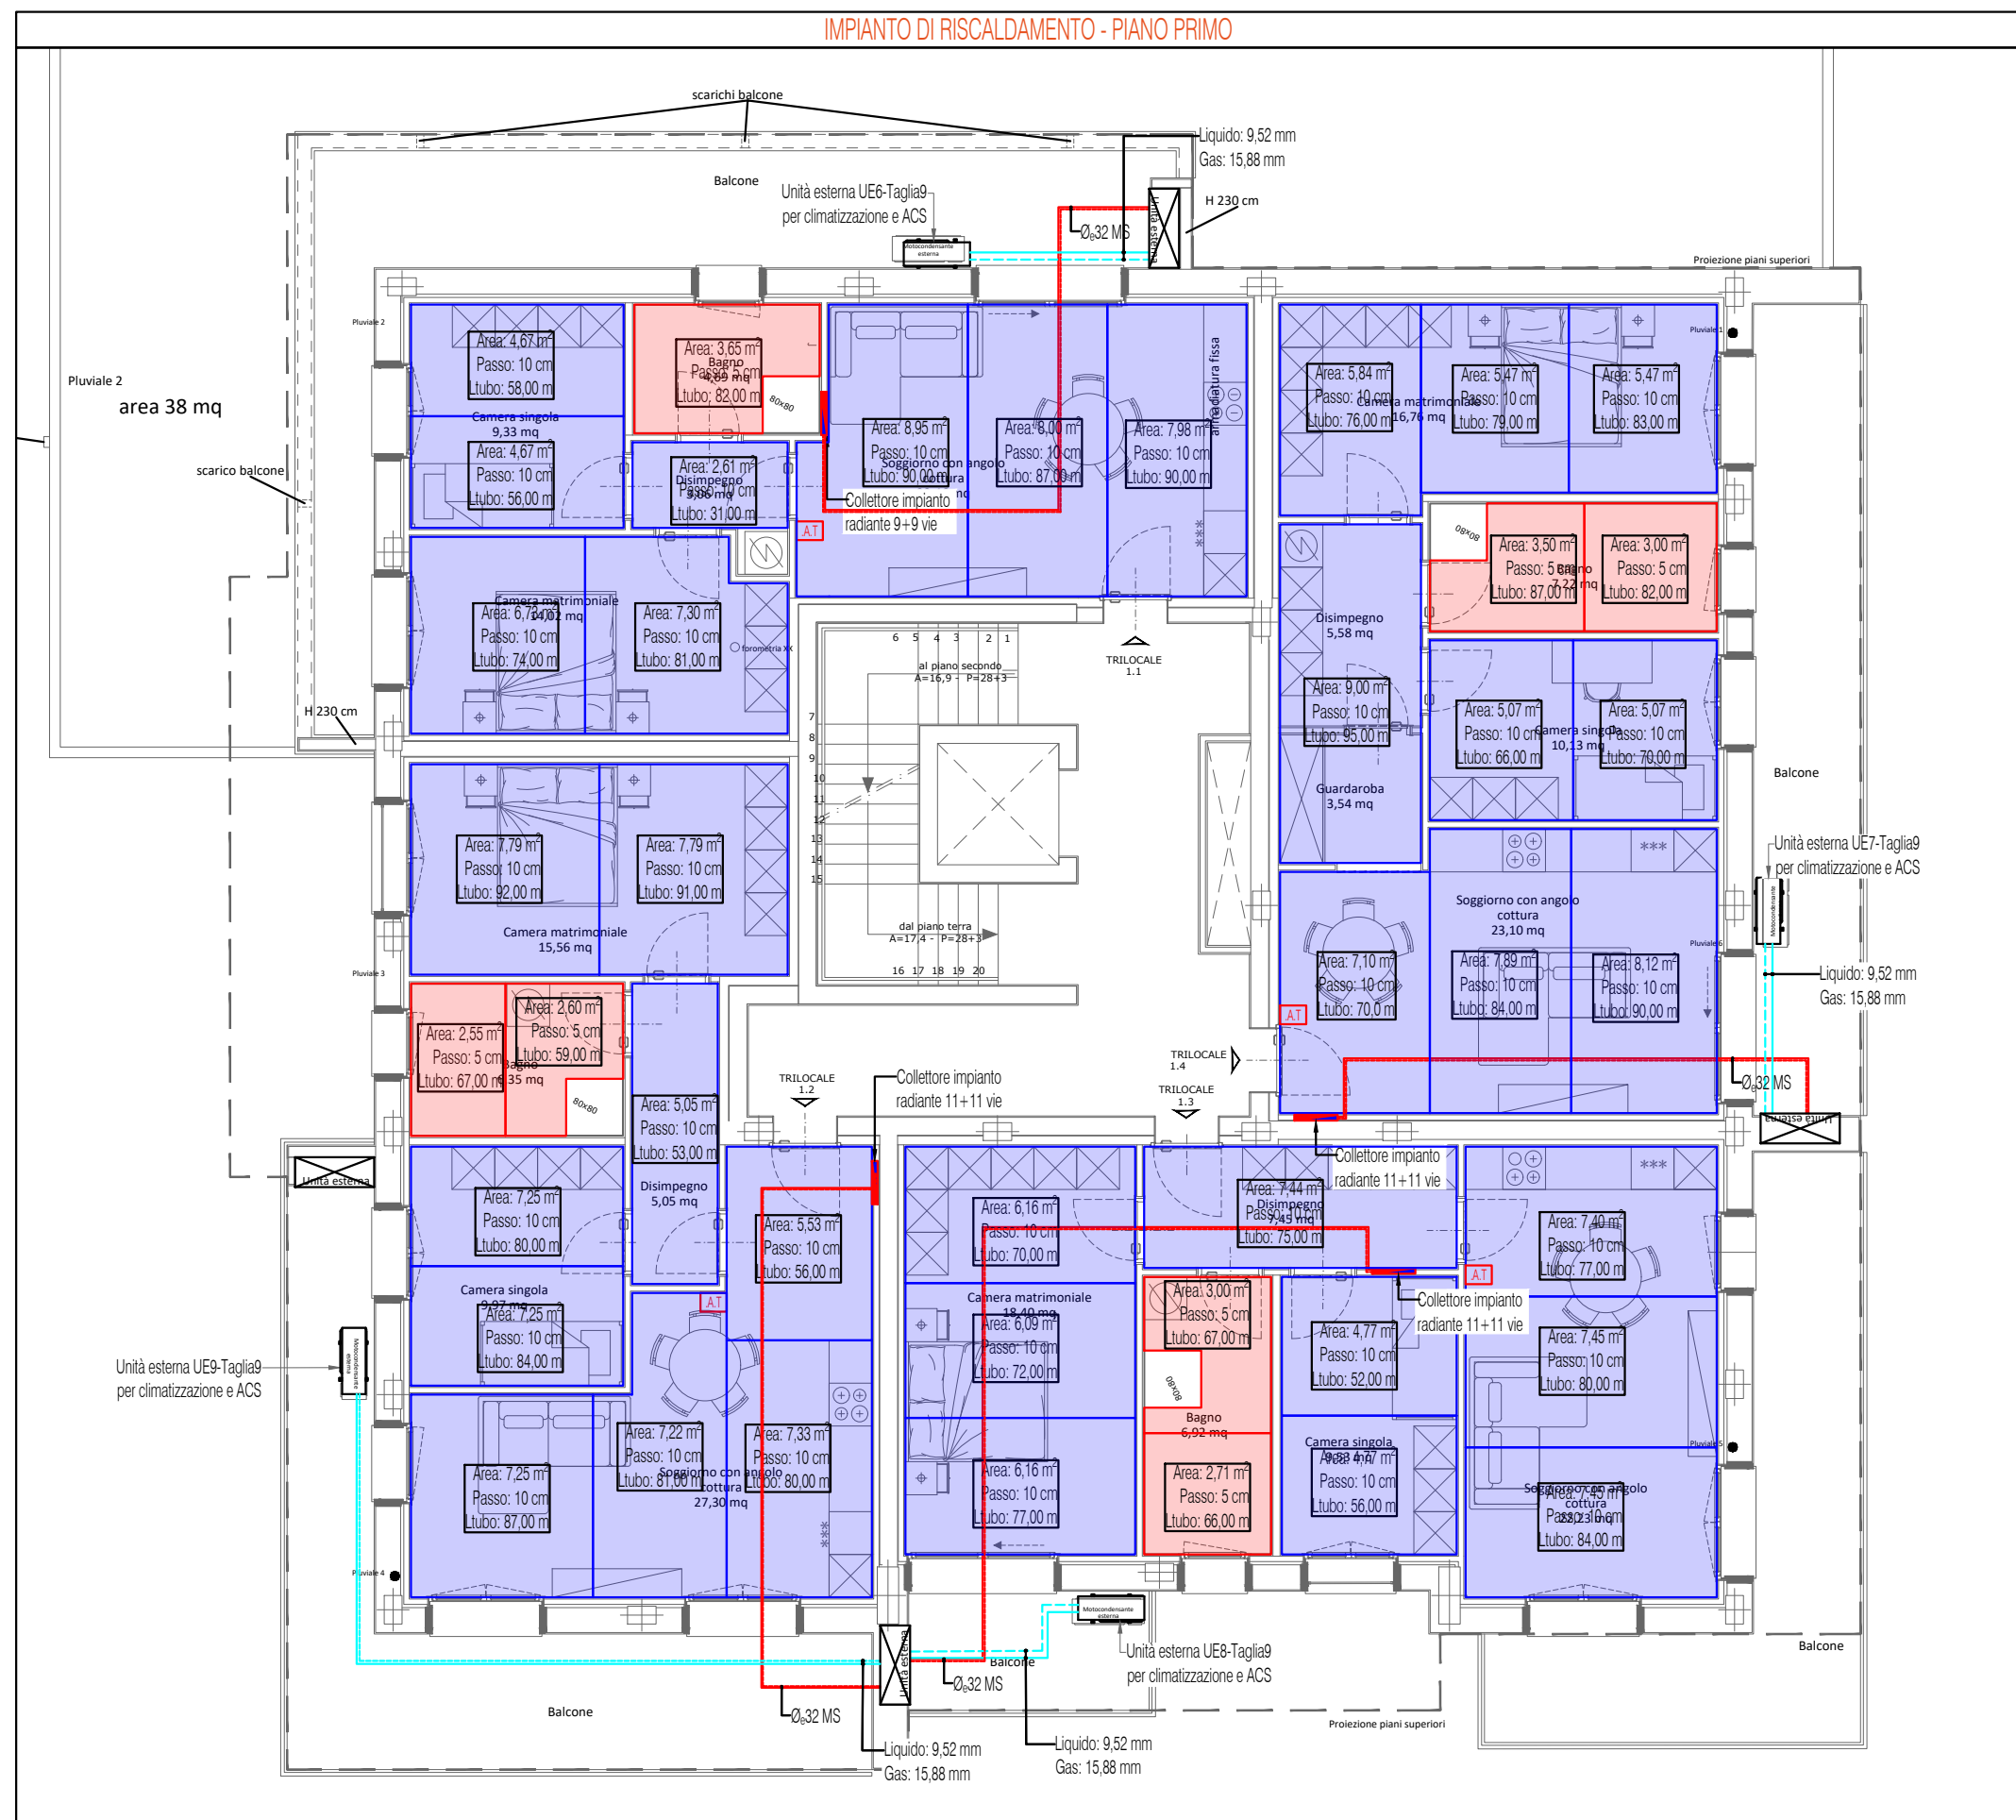


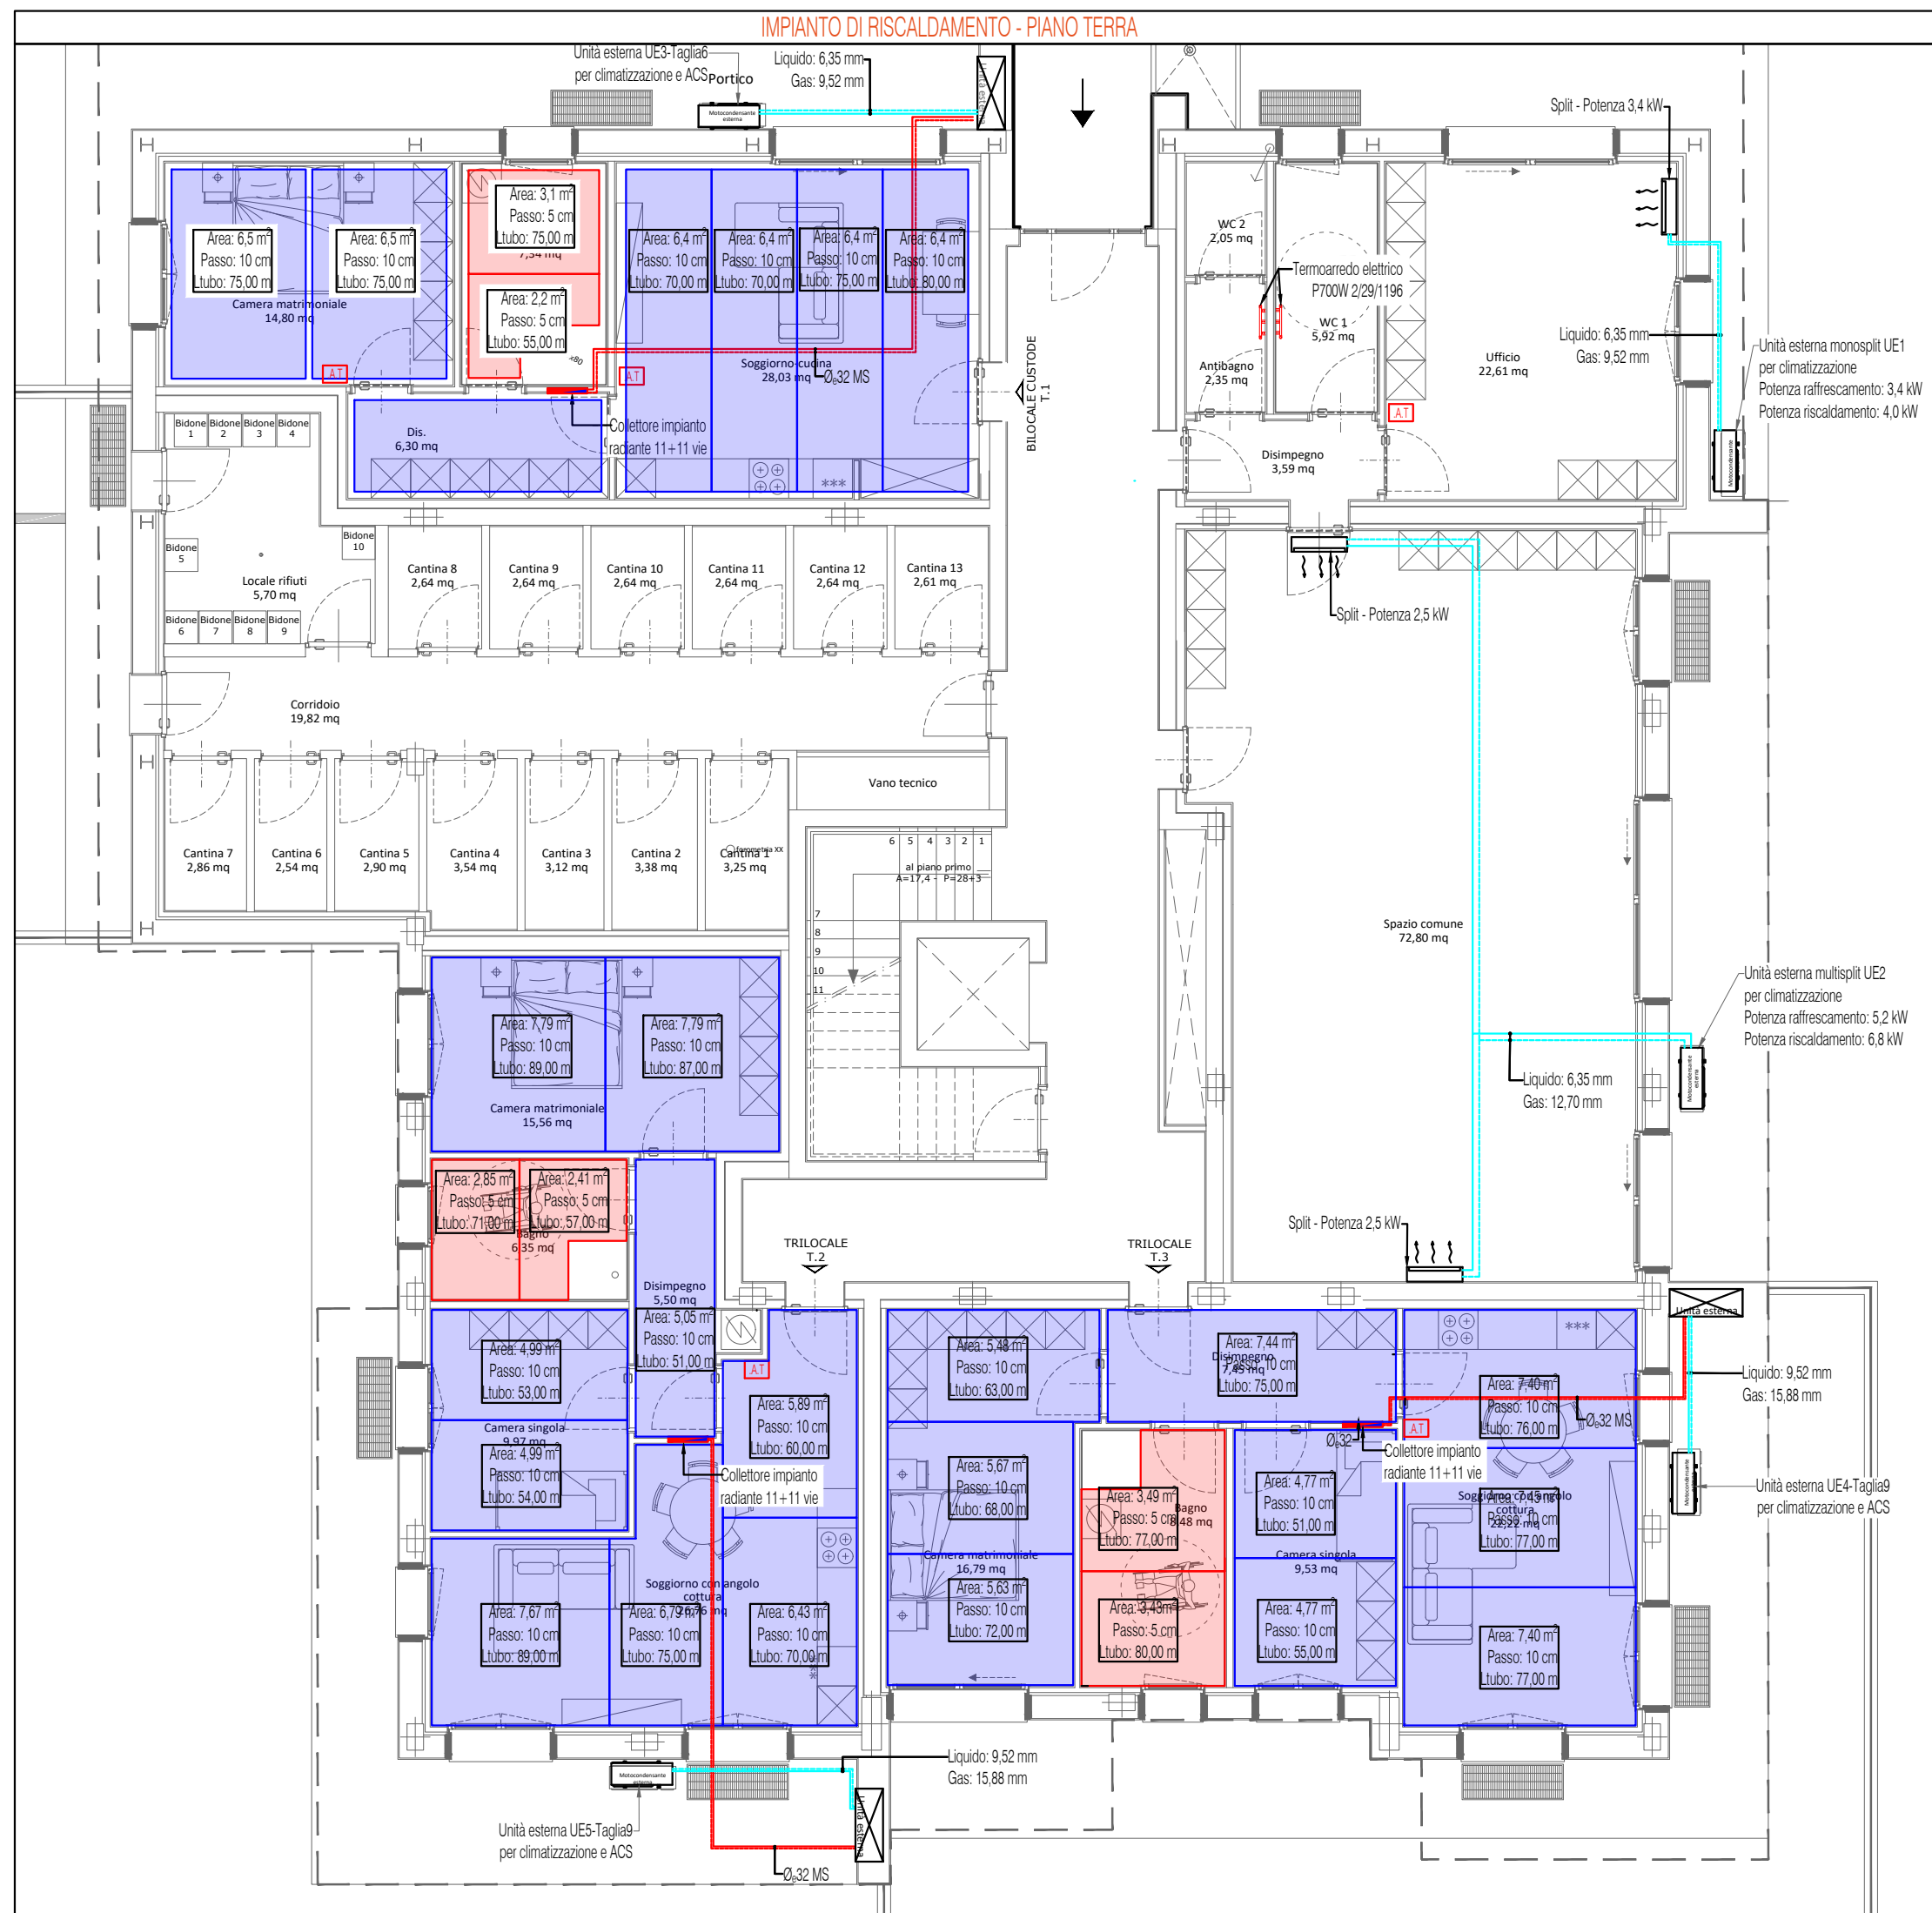

IL PROGETTO IMPIANTISTICO HA VALENZA PER QUANTO RIGUARDA GLI ASPETTI LEGATI AGLI IMPIANTI STESSI PER TUTTE LE CARATTERISTICHE E LE MISURE ARCHITETTONICHE E/O STRUTTURALI. FANNO FEDE I DISEGNI DI COMPETENZA.


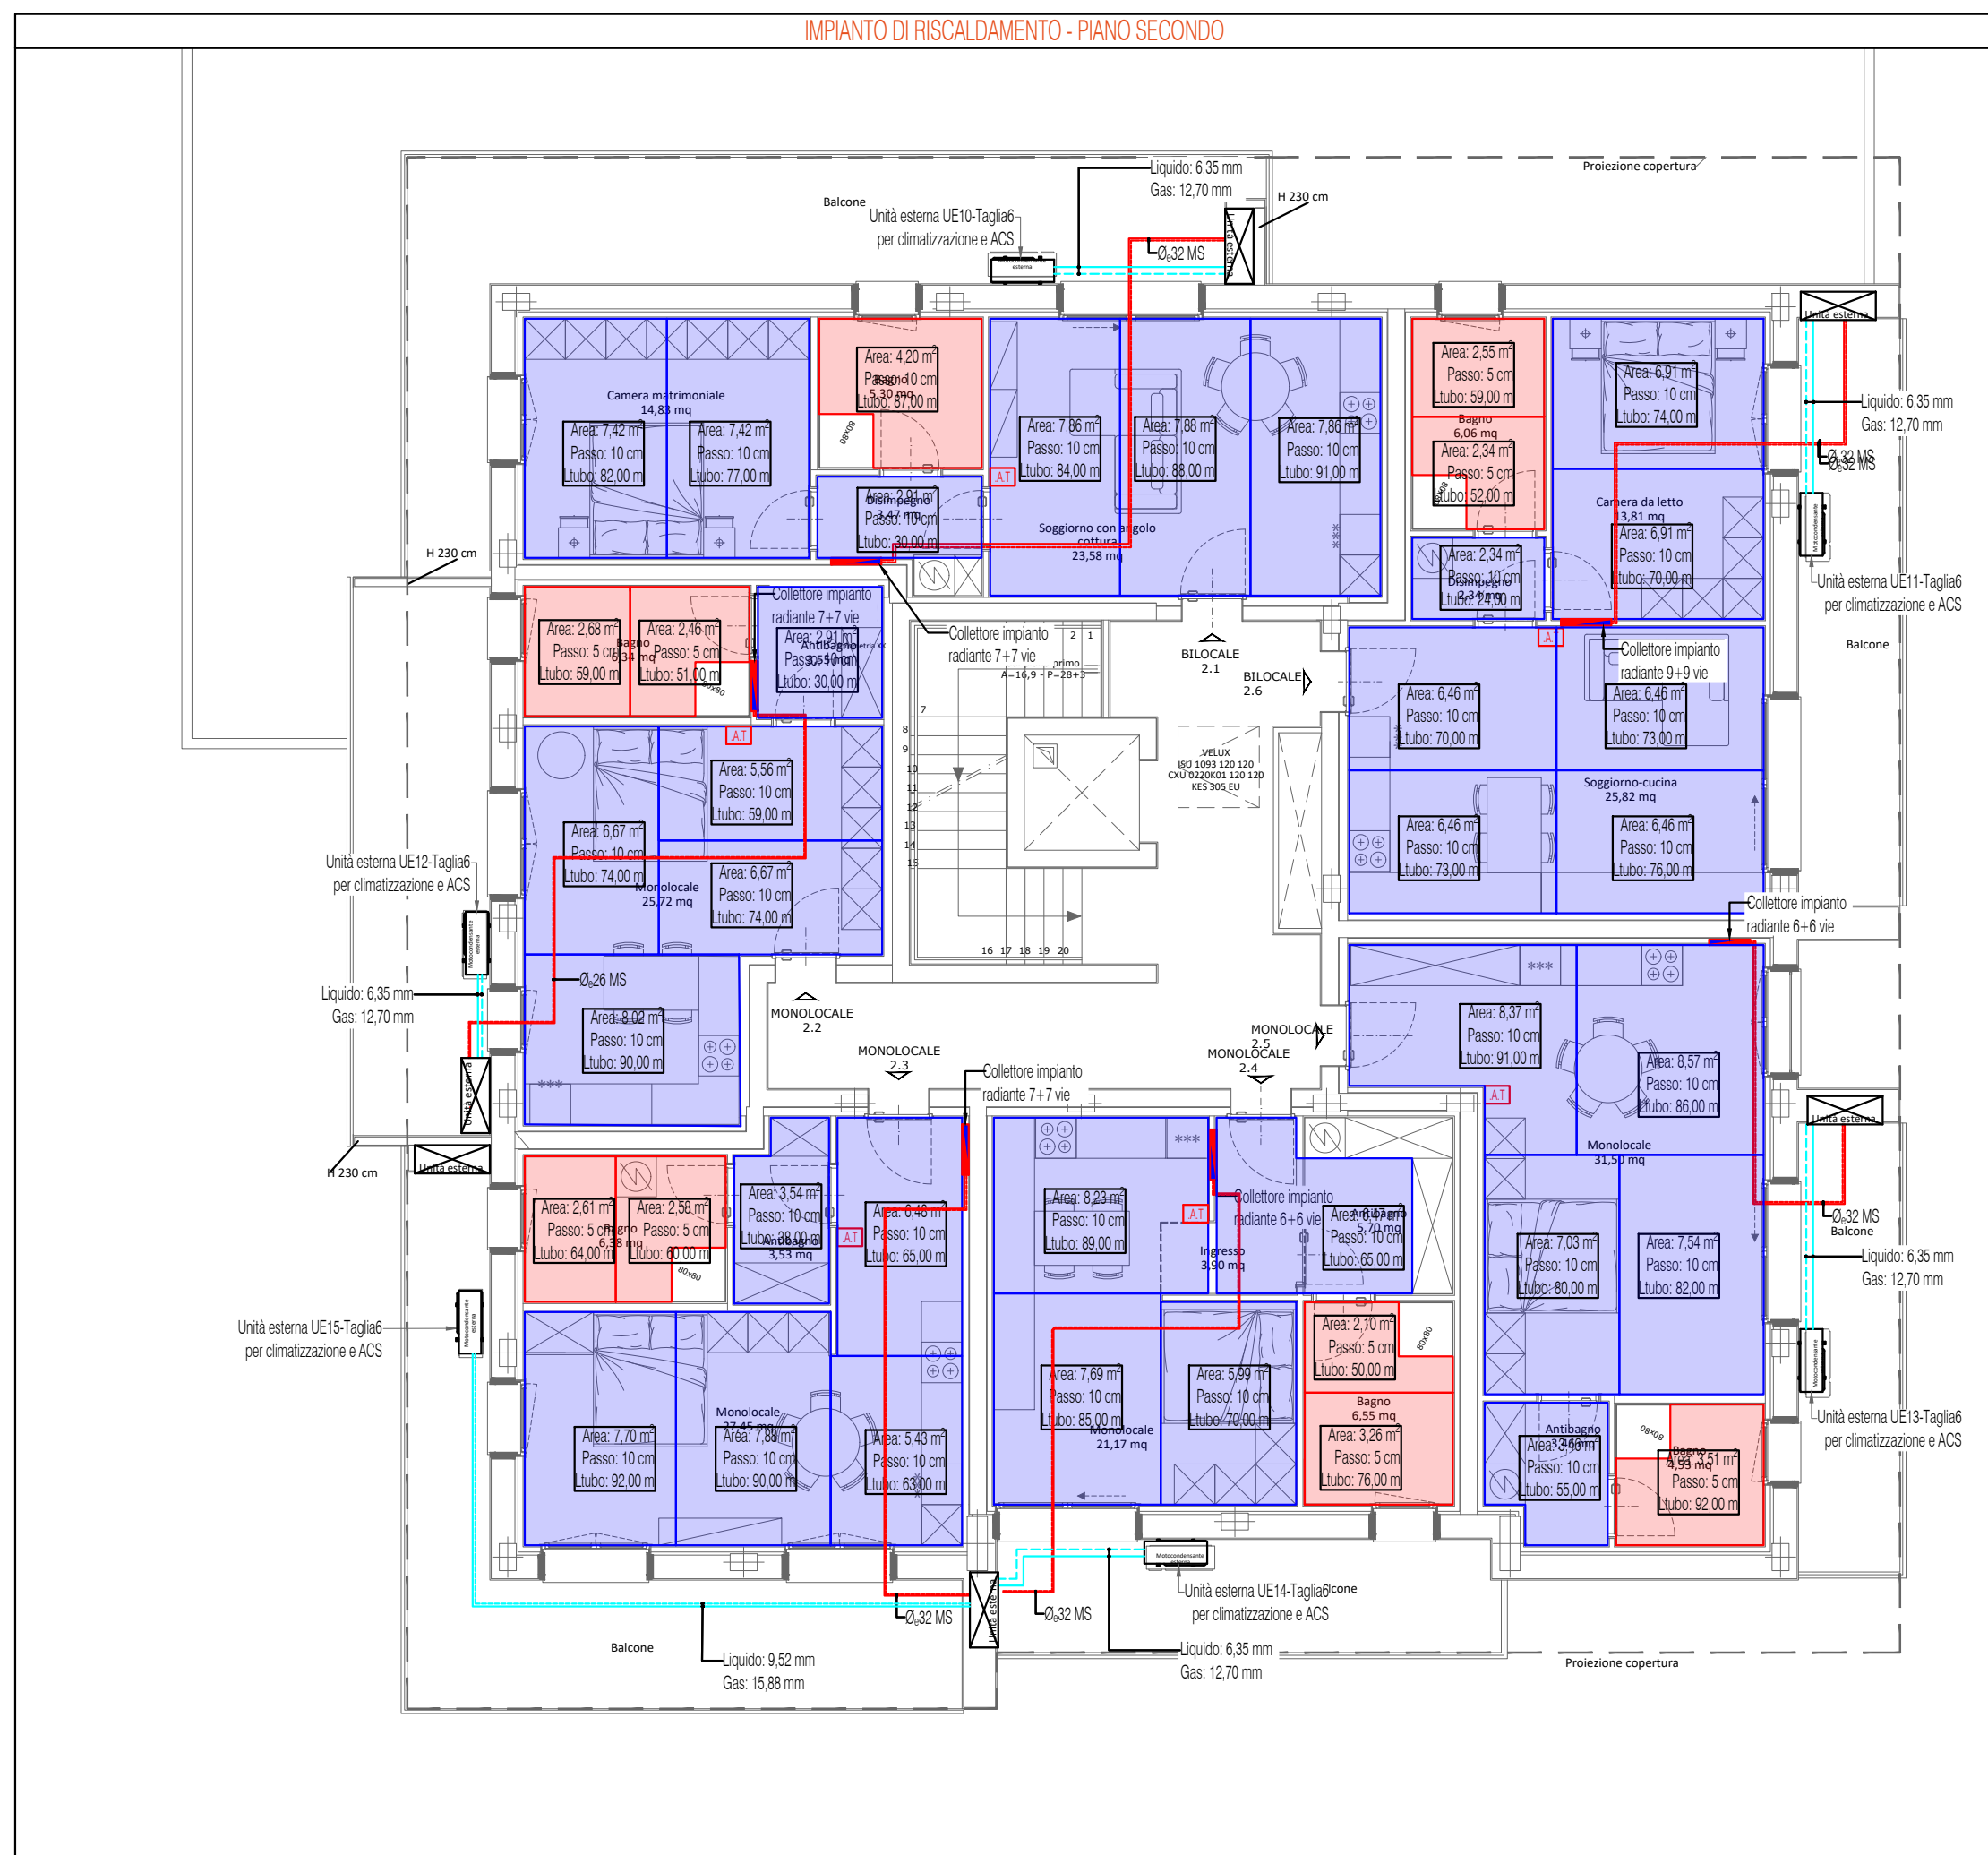


TABELLA CARATTERISTICHE TUBAZIONI IMPIEGATE

diam. ø	diam. DN	diam. esterno ø e (mm)	Spessore s (mm)	diam. interno ø i (mm)
3/8"	DN 12	16,0	2,25	11,5
1/2"	DN 15	20,0	2,50	15,0
3/4"	DN 20	26,0	3,00	20,0
1"	DN 25	32,0	3,00	26,0
1 1/4"	DN 32	40,0	3,50	33,0
1 1/2"	DN 40	50,0	4,00	42,0
2"	DN 50	63,0	4,50	54,0

ESEMPIO COLLETTORE DI DISTRIBUZIONE

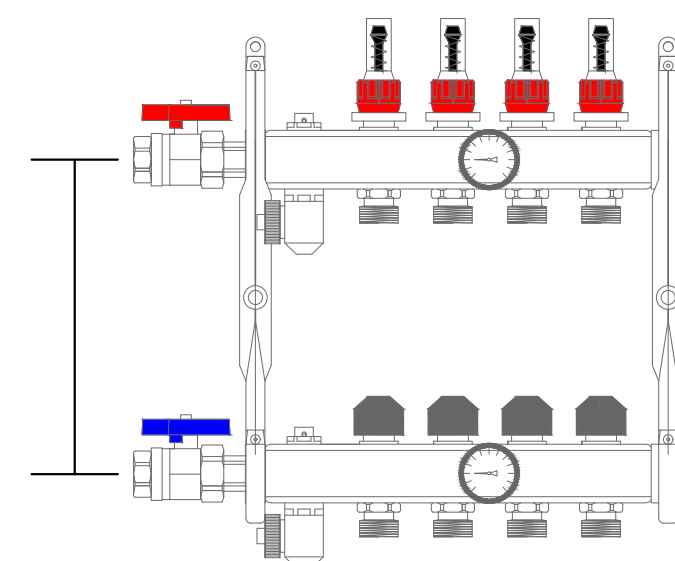


Collettore in acciaio inox completo di:

- 2 attacchi principali
- attacchi circuiti radianti
- 2 valvole di riempimento
- 2 valvole manuali di sfogo
- valvole motorizzabili sul ritorno
- contatori di regolazione di portata sulla mandata
- Attuatori elettotermici

ACCORGIMENTI PRATICI PER LA POSA DEI GIUNTI


Il giunto di dilatazione deve essere previsto quando si supera una superficie di 40mq (8m x 5m). Il taglio deve risultare netto fino a raggiungere il pannello. La zona di taglio deve essere riempita con materiale plastico (es. schiuma poliuretana) che permetta la dilatazione. In prossimità del taglio, il tubo del riscaldamento a pavimento deve essere ricoperto con una guaina coniugata che permetta la dilatazione del massetto senza danneggiare il tubo.

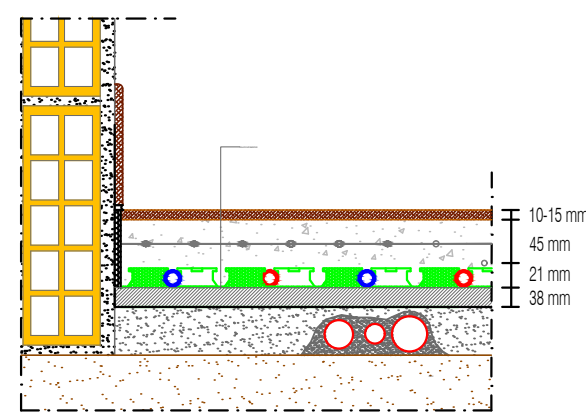

SEZIONE PANNELLO PREFORMATO PIANO TERRA

ACCORGIMENTI PRATICI PER LA POSA DEI GIUNTI

Il giunto di dilatazione deve essere previsto quando si supera una superficie di 40mq (8m x 5m). Il taglio deve risultare netto fino a raggiungere il pannello. La zona di taglio deve essere riempita con materiale plastico (es. schiuma poliuretana) che permetta la dilatazione. In prossimità del taglio, il tubo del riscaldamento a pavimento deve essere ricoperto con una guaina coniugata che permetta la dilatazione del massetto senza danneggiare il tubo.

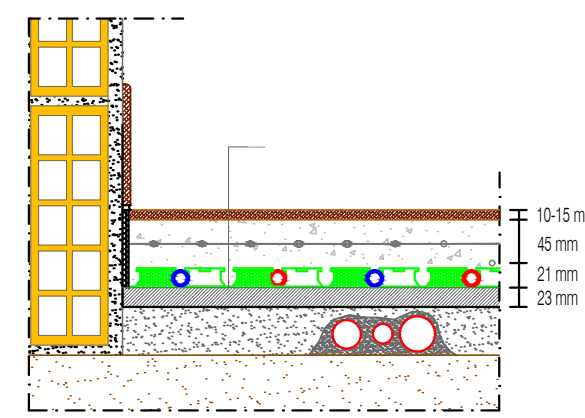

SEZIONE PANNELLO PREFORMATO PIANI INTERMI

GB&PARTNERS SERVIZI E PROGETTI IMMOBILIARI

dabster ENGINEERING

Dabster srl
Via Sommacampagna 63/H - 37137 Verona
P.IVA 04464890239
mail: mail@dabster.it

COMUNE DI COLOGNO MONZESE (MI)
AREA Ex TORRIANI ARAS 01
PROGETTO ESECUTIVO
Progetto Servizi Abitativi Pubblici di via Pergolesi

N°	DATA	DESCRIZIONE	MOTIVAZIONE DELL'AGGIORNAMENTO	STUDIO	DIS.
00	16/01/2026	Prima emissione		G.B.&P.	L.M.

Il Progettista

Collegio Provinciale
Geometri e Geometri Laureati
di Lodi
Ing. Gianpiero Bianchi
N. 297



Progetto
PROGETTO ESECUTIVO
Servizi Abitativi Pubblici
Comune di Cologno
Monzese(MI)

Proponente
Officine Mak S.r.l.
Corso Europa, 10
Milano 20122

Scala
1:100
Data
23/01/2026

Tipo tavola
IMPIANTI
Serie
PROGETTO ESECUTIVO
Titolo
**IMPIANTI MECCANICI -
IMPIANTO DI RISCALDAMENTO**

Tavola nr.
Tipo
Tavola
Sigla /
Serie
Numero /
Variante
Agg.

Orientamento

