
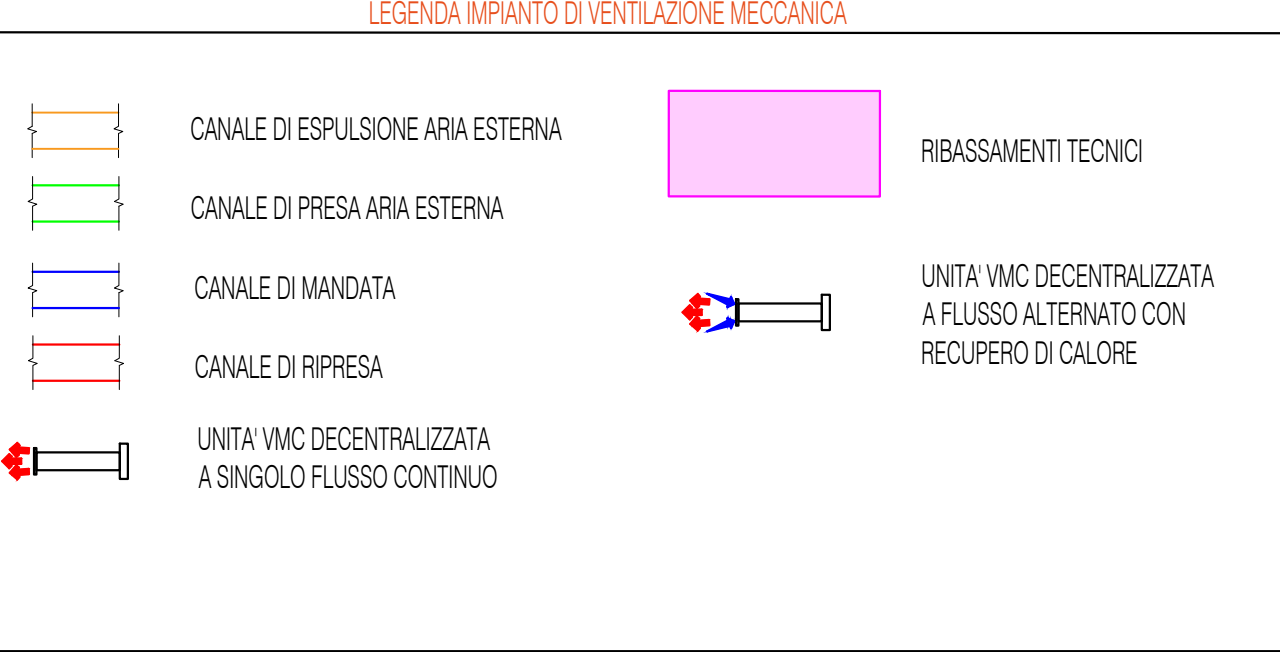
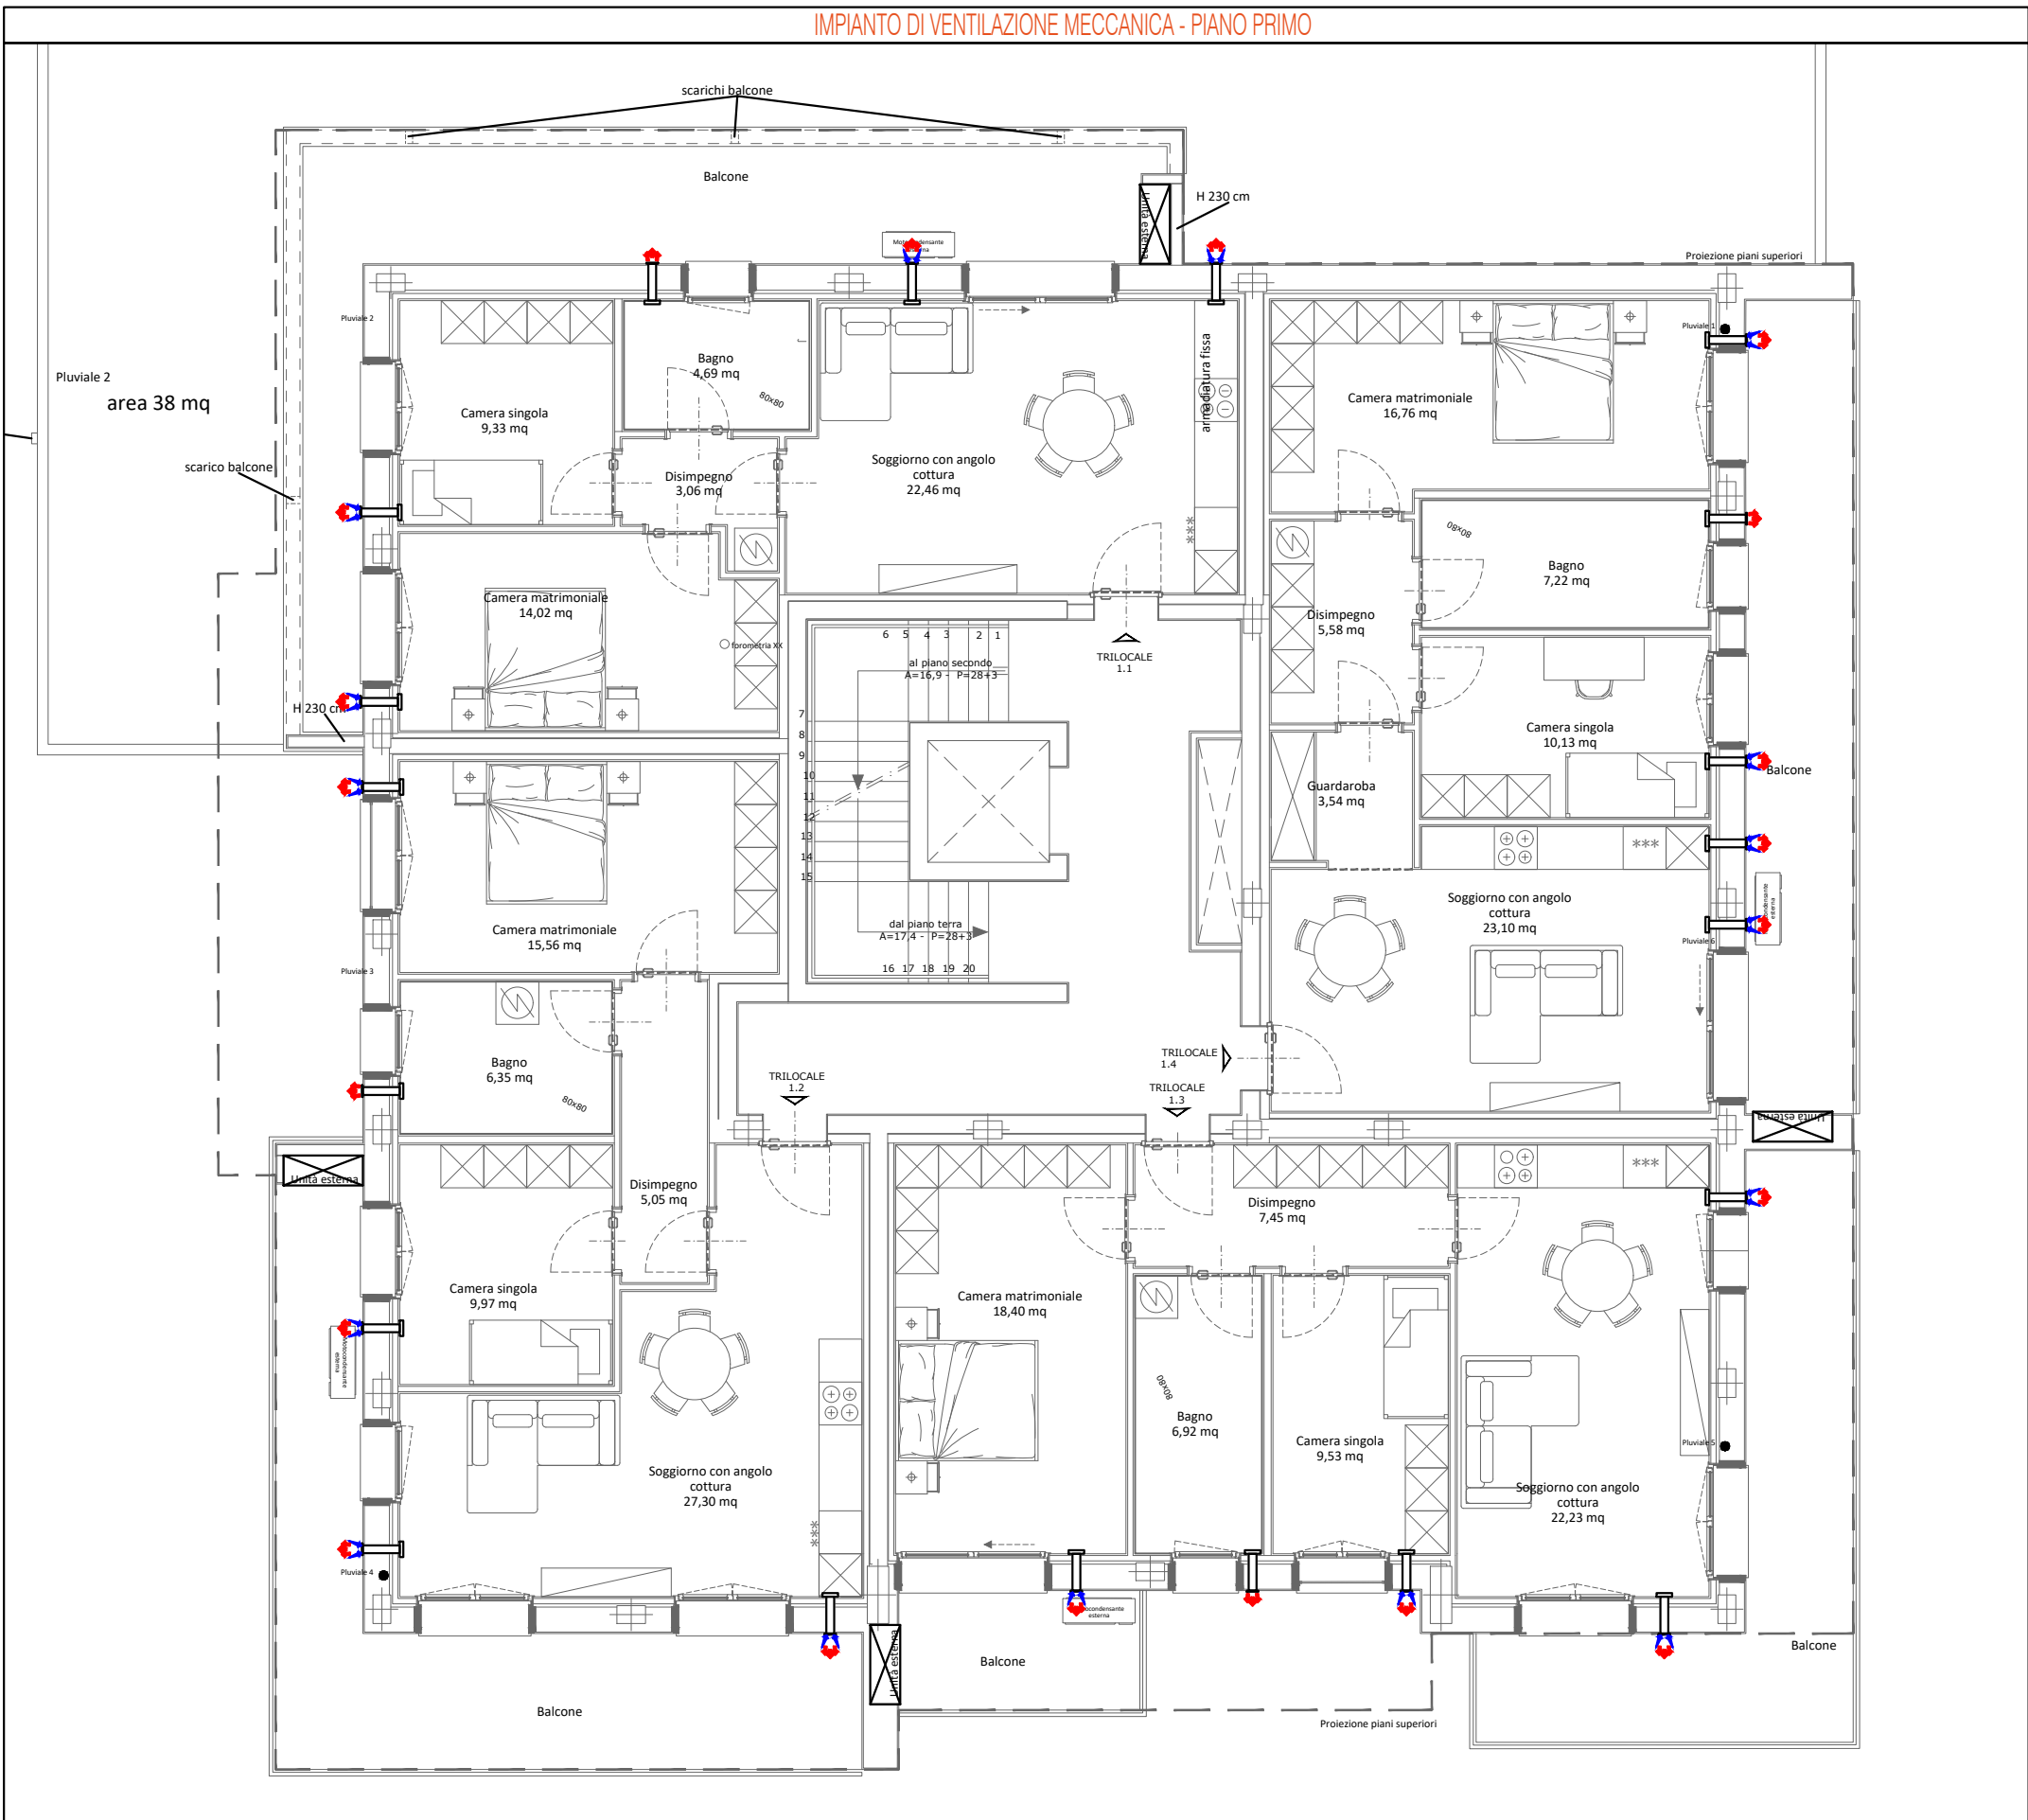


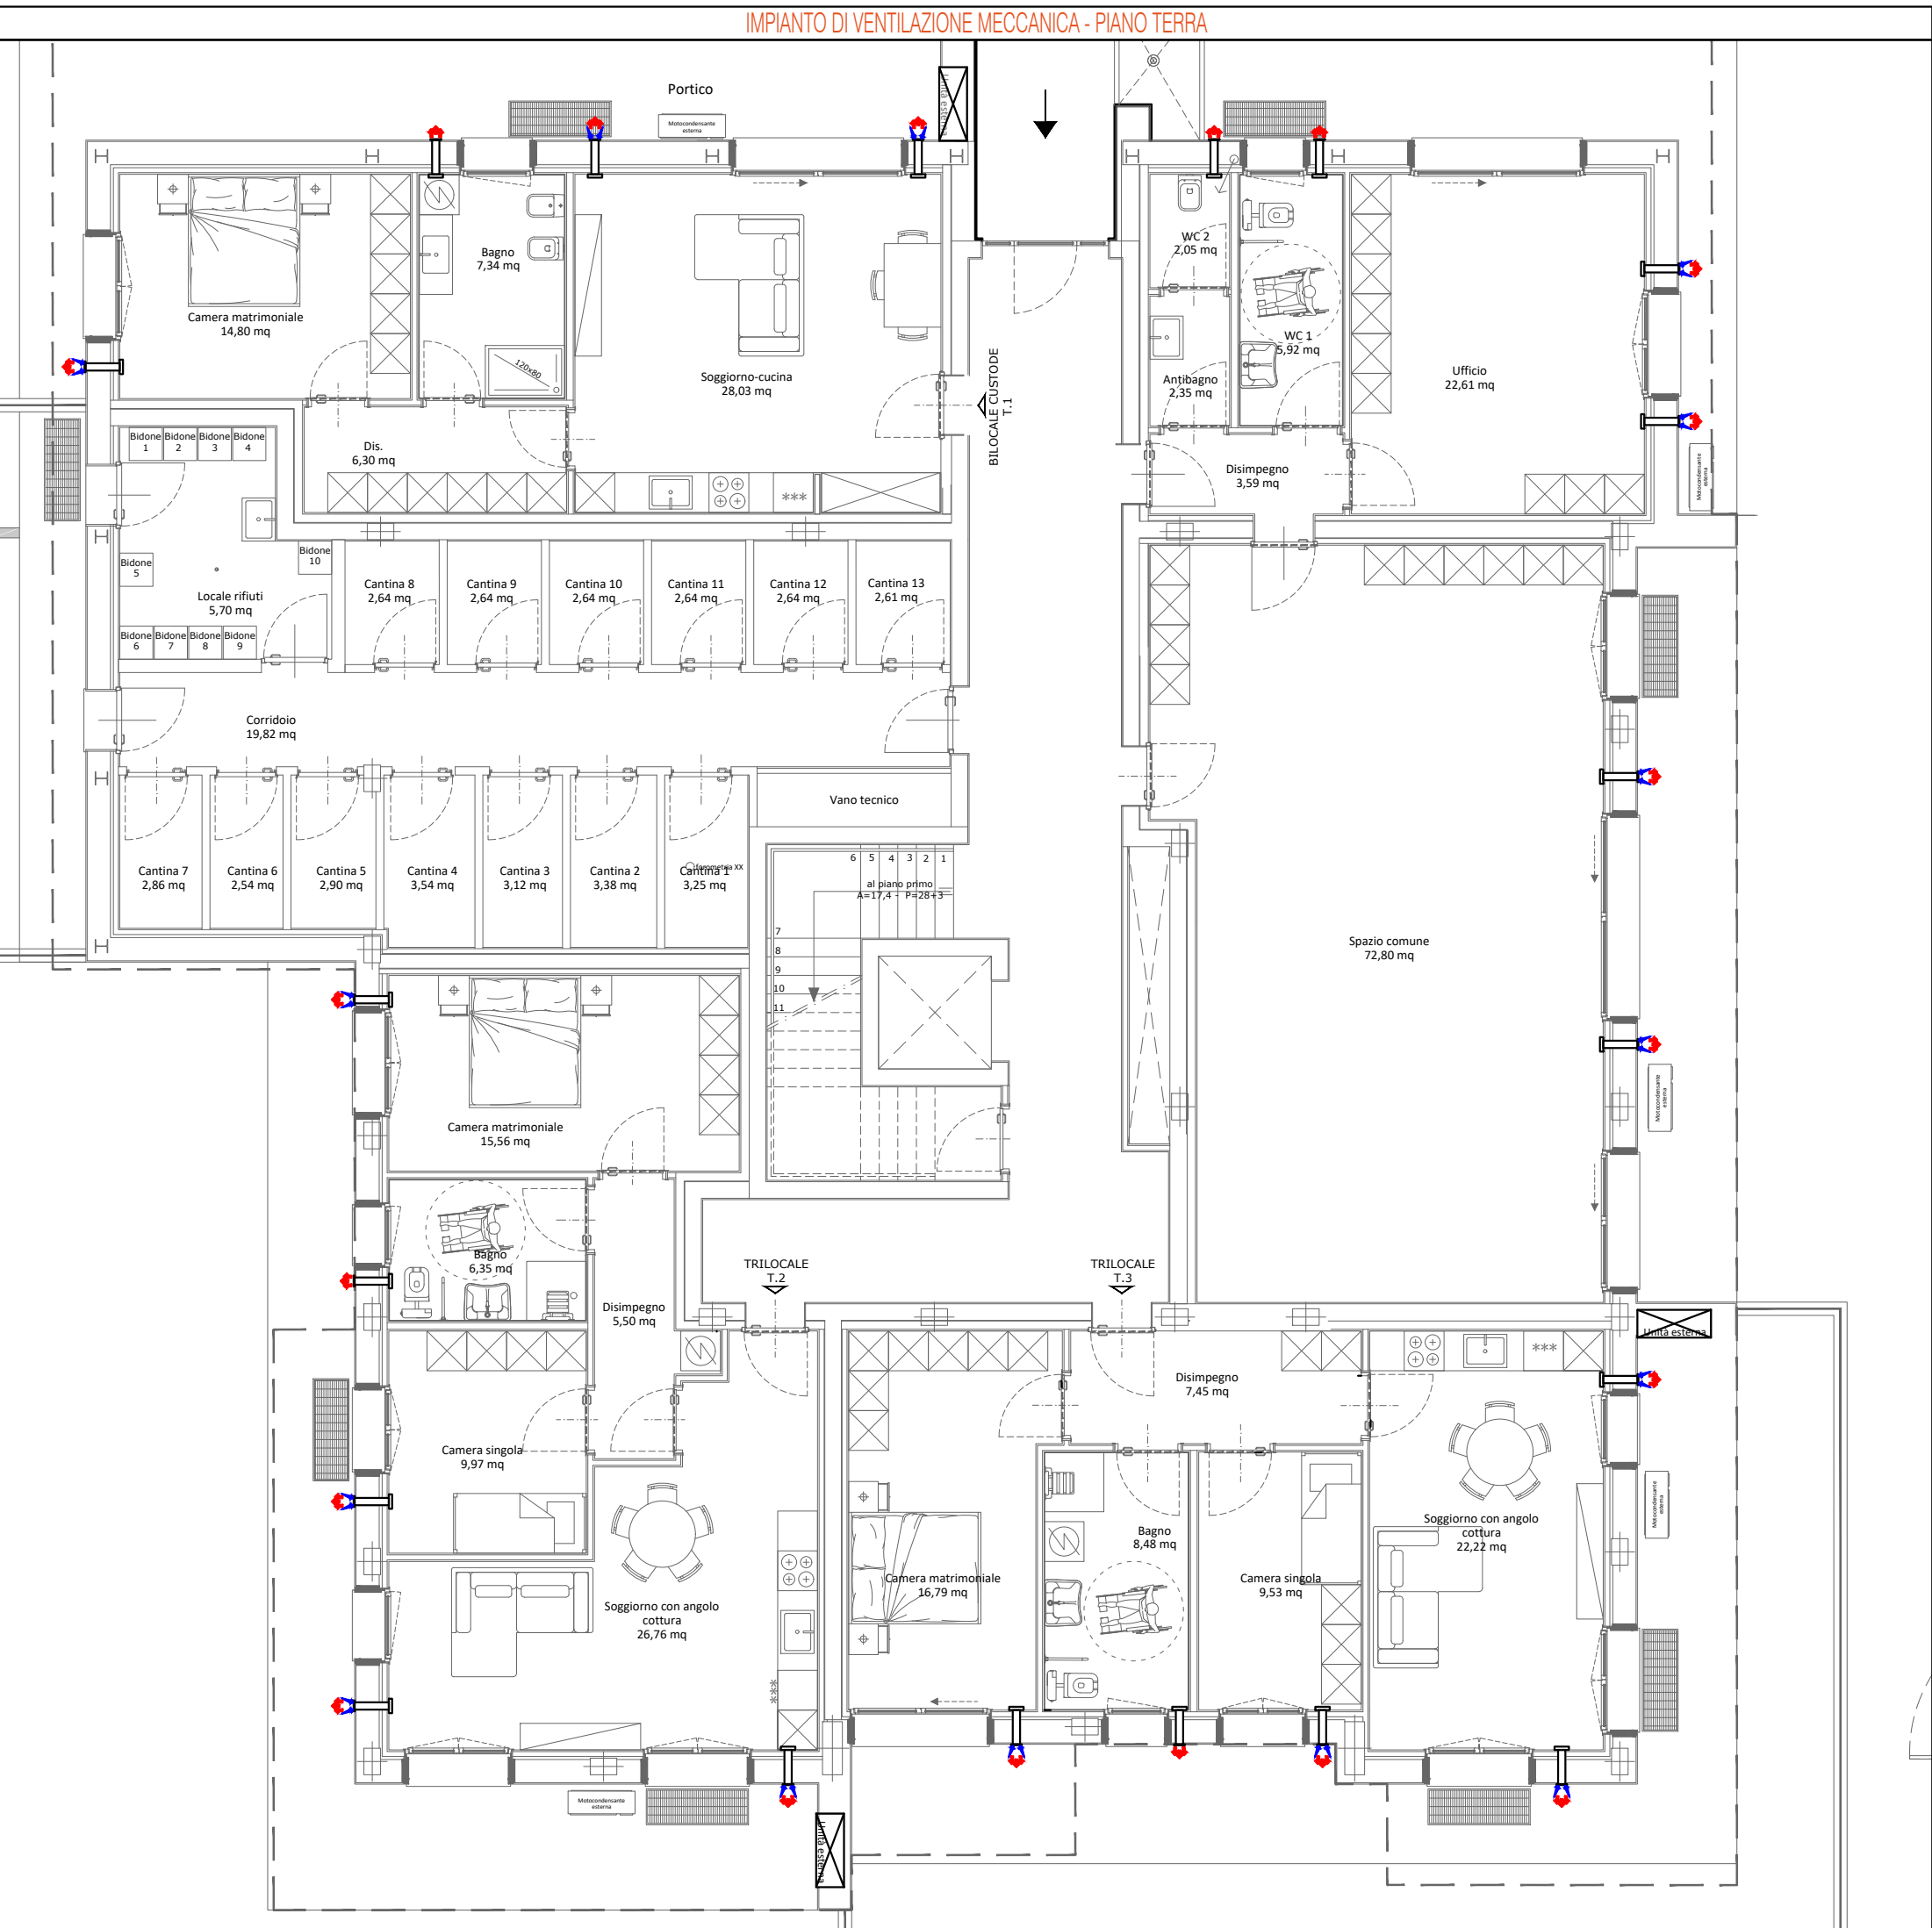

IL PROGETTO IMPIANTISTICO HA VALENZA PER QUANTO RIGUARDA GLI ASPETTI LEGATI AGLI IMPIANTI STESSI. PER TUTTE LE CARATTERISTICHE E LE MISURE ARCHITETTONICHE E CO-STRUTTURALI FANNO FEDE I DISegni DI COMPETENZA.

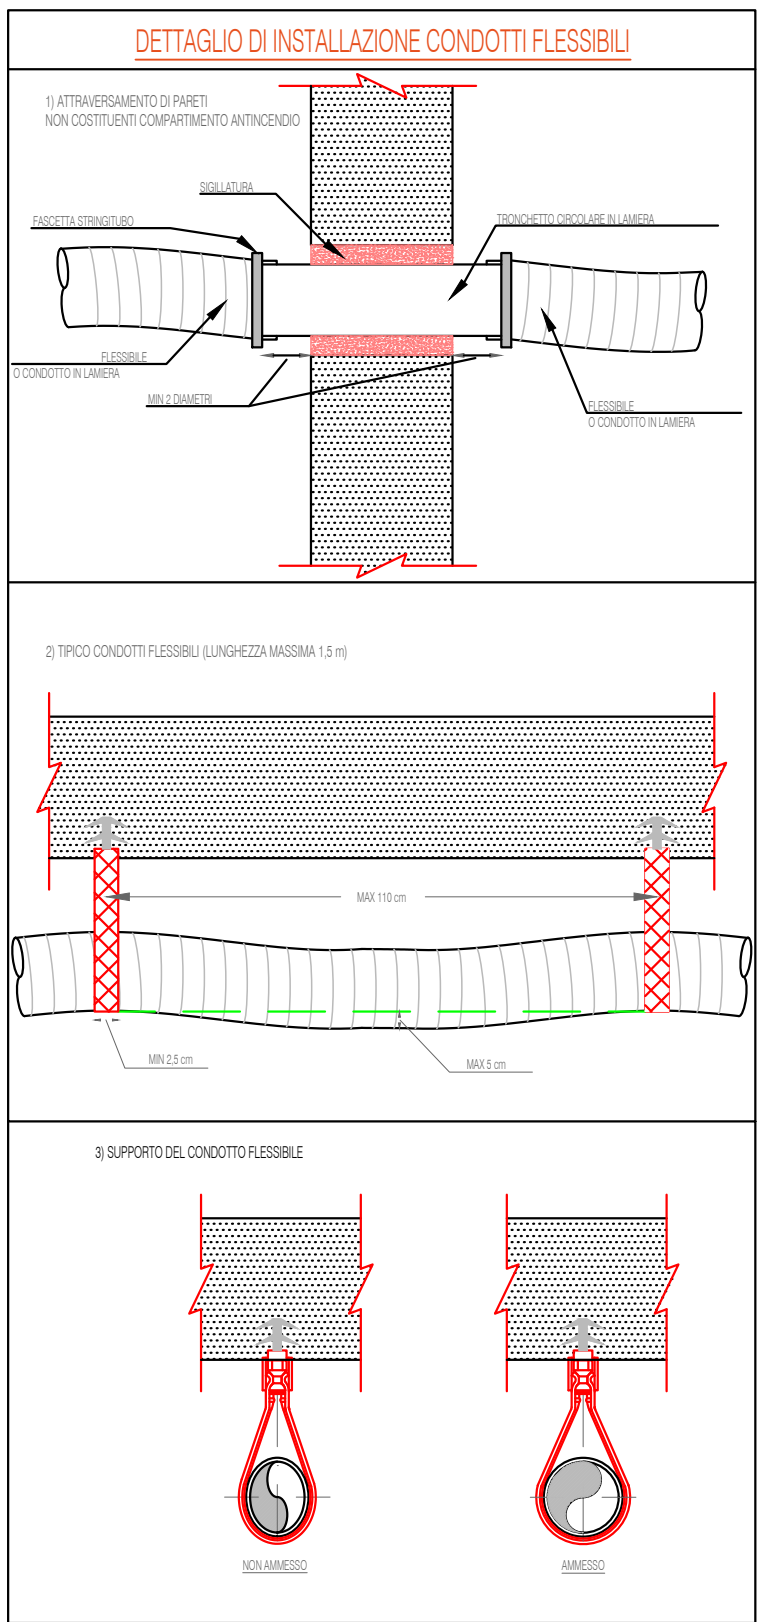
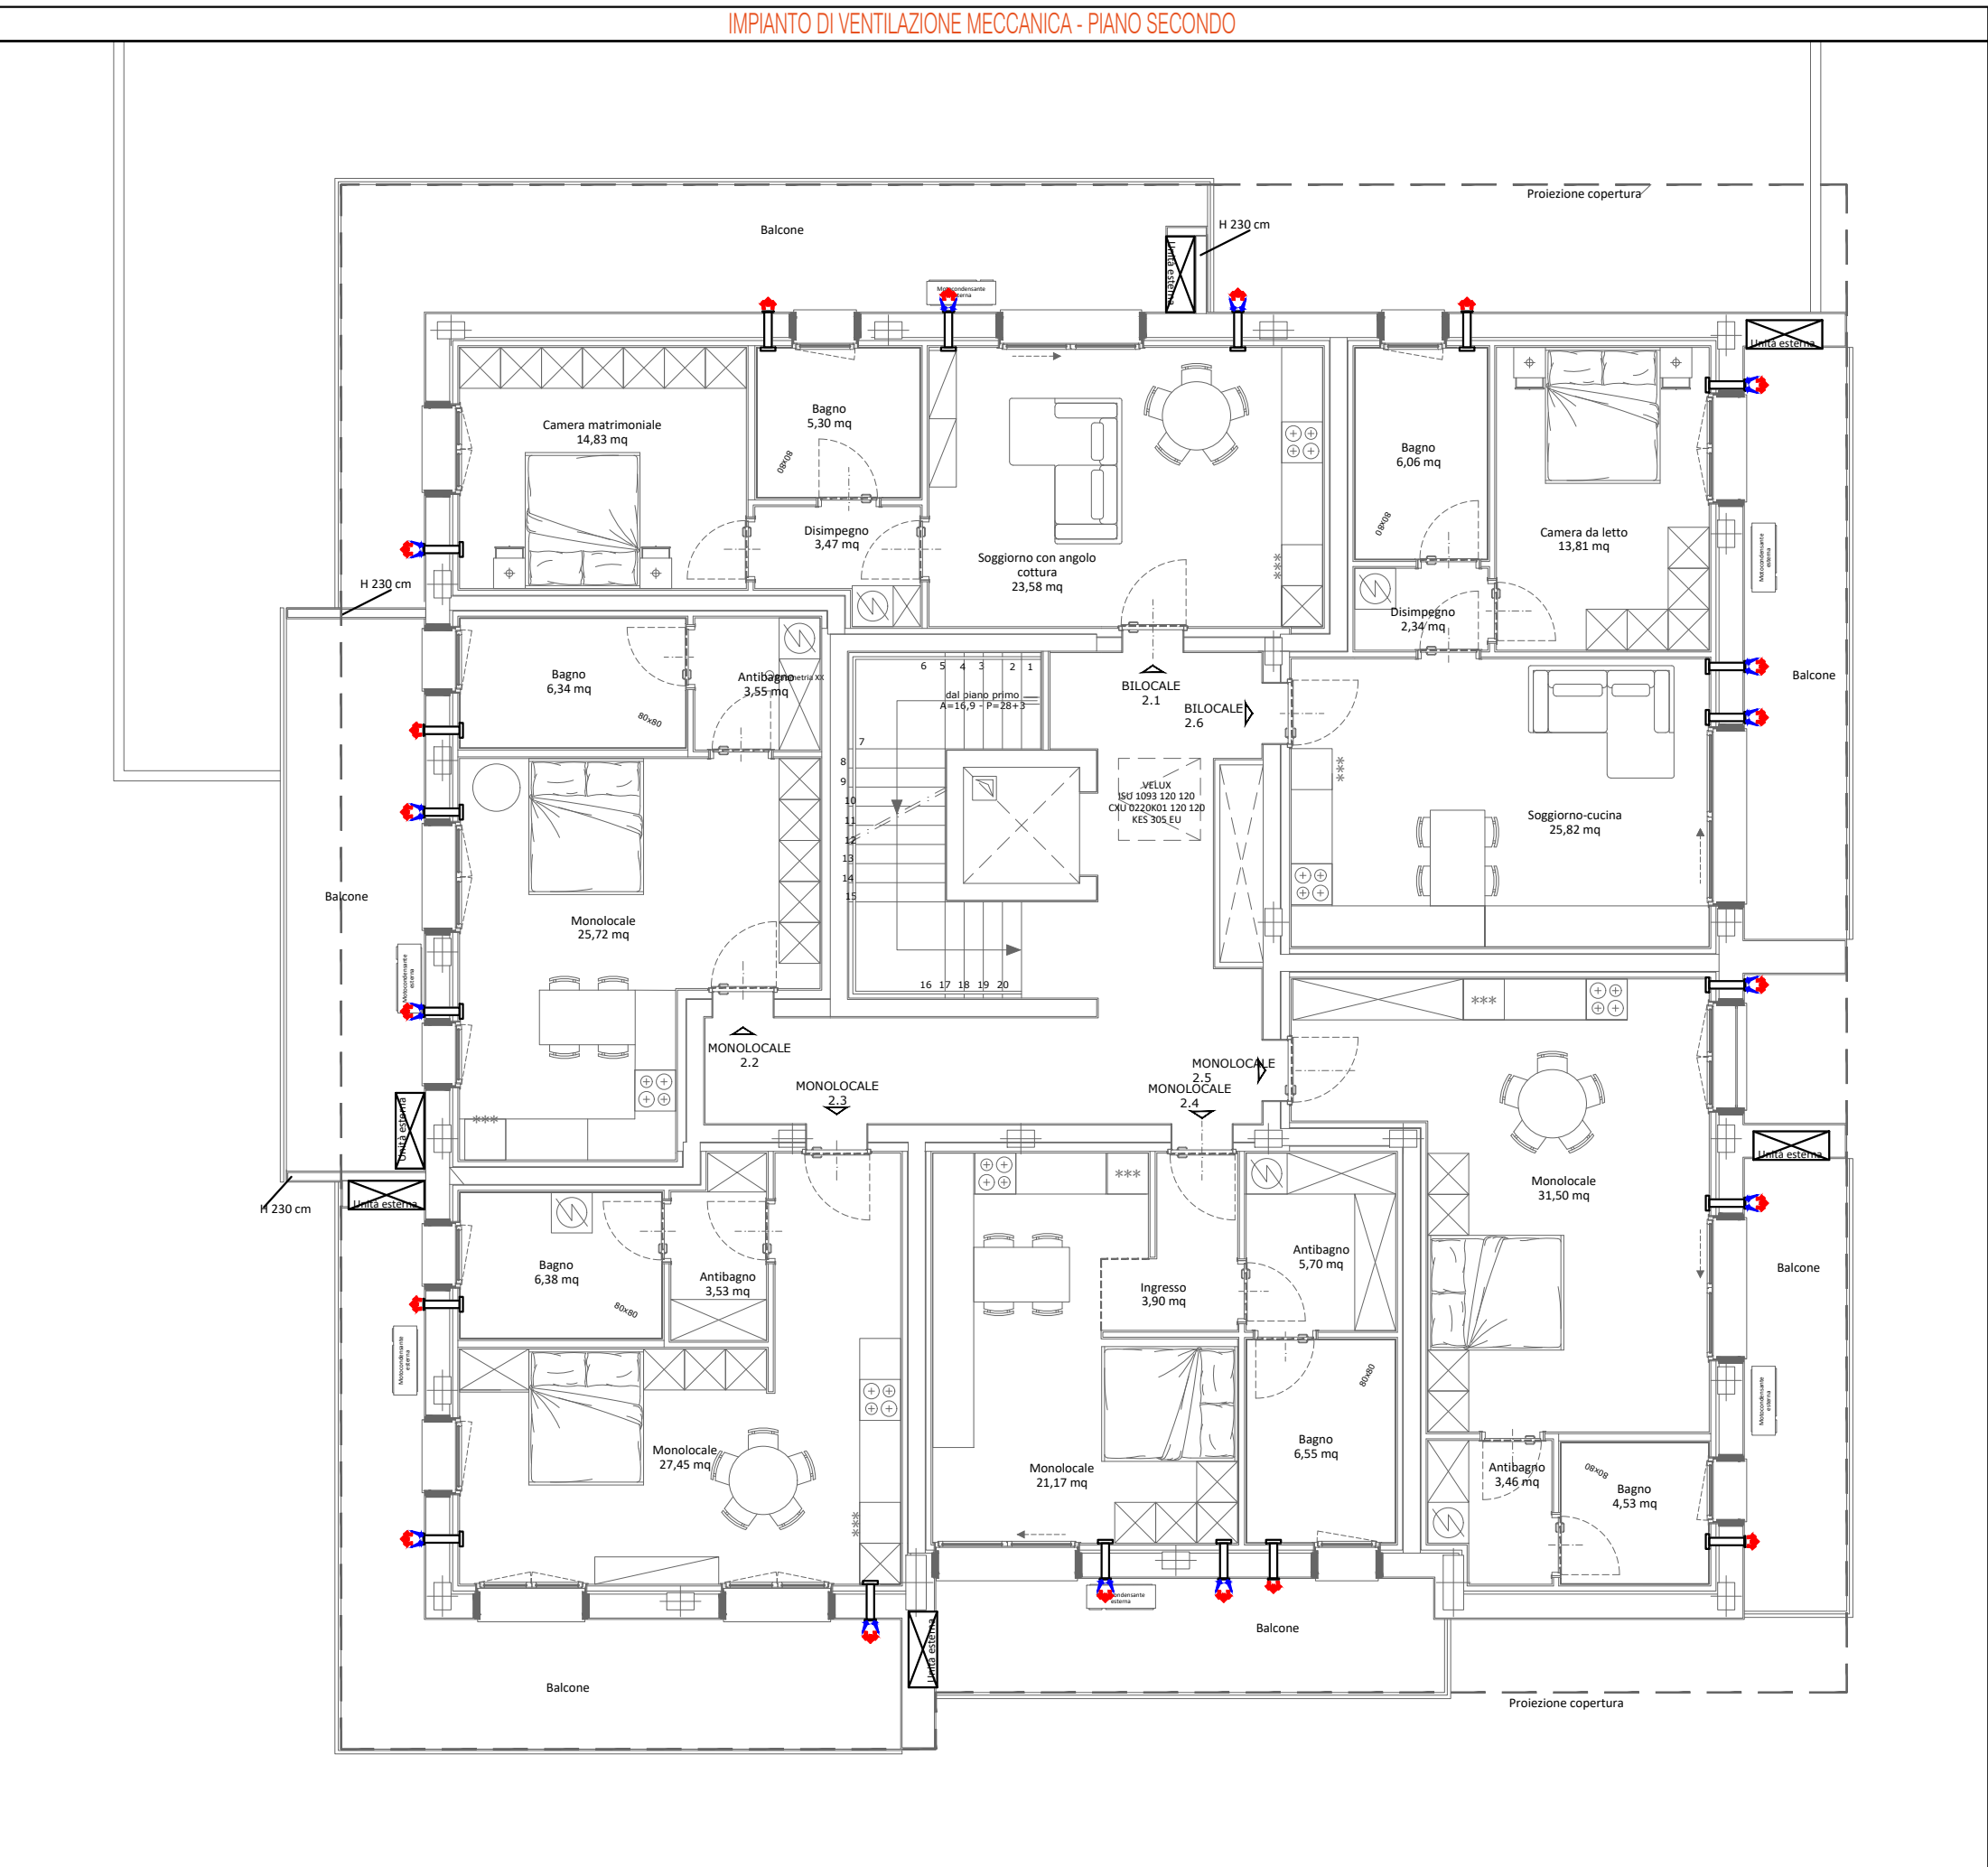


TABELLA INDICATIVA DEGLI ISOLAMENTI TERMICI DELLE CONDOTTE

ISOLAMENTO TERMICO DELLE CANALIZZAZIONI DELL'ARIA REALIZZATO CON LASTRA ISOLANTE IN ELASTOMERO ESPANSO A CELLE CHIUSE INCOLLATA ESTERNAMENTE ALLA CANALIZZAZIONE, COMPRESI RIPRISTINI DI GIUNTI, FLANGE ETC.				
$\lambda = 0.034 \text{ [W/MK]} \text{ A } T=0^{\circ}\text{C}$ $\lambda = 0.038 \text{ [W/MK]} \text{ A } T=40^{\circ}\text{C}$				
CIRCUITO	INSTALLAZIONE DELLE TUBAZIONI	TIPO ISOLANTE	SPESORE ISOLANTE [mm]	FINITURA ESTERNA
CANALI DI MANDATA CANALI DI RIPRESA PRESA ARIA ESTERNA	ALL'ESTERNO	ELASTOMERO	25	LAMIERINO D'ALLUMINIO SP. 6/10 [MM]
	NEI LOCALI TECNICI	ELASTOMERO	19	LAMIERINO D'ALLUMINIO SP. 6/10 [MM]
	NEI CAVEDI	ELASTOMERO	19	
	NEI CONTROSOFFITTI	ELASTOMERO	10	
	A VISTA NEGLI AMBIENTI	ELASTOMERO	10	LAMIERINO D'ALLUMINIO SP. 6/10 [MM]

TUBAZIONE FLESSIBILE ISOLATA

Diametro mm	Portata (V < 3 m/s) mc/h
100	< 80
125	80 - 150
160	150 - 200
200	200 - 300
250	300 - 500
315	500 - 700
450	700 - 1000

NB: velocità dell'aria < 3 m/s

TIPOLOGIA VMC

	Dimensioni unità (L x H x P)	Portata aria m3/h	Dim. flessibile mm
TIPO 1	580x255x580	150	160
TIPO 2		200	160
TIPO 3	795x295x600	295	200
TIPO 4	1150x290x650	450	250

Progetto impianti

COMUNE DI COLOGNO MONZESE (MI)
AREA Ex TORRIANI ARAS 01
PROGETTO ESECUTIVO
Progetto Servizi Abitativi Pubblici di via Pergolesi

N° DATA DESCRIZIONE MOTIVAZIONE DELL'AGGIORNAMENTO STUDIO DIS.

00 16/01/2026 Prima emissione G.B.&P. L.M.

Progetto **PROGETTO ESECUTIVO** Servizi Abitativi Pubblici Comune di Cologno Monzese(MI)

Proponente **Officine Mak S.r.l.** Corso Europa, 10 Milano 20122

Scala **1:100**

Data **23/01/2026**

Tipo tavola **IMPIANTI**

Serie **PROGETTO ESECUTIVO**

Titolo **IMPIANTI MECCANICI - IMPIANTO DI VENTILAZIONE MECCANICA**

Tavola nr. **IMP**

Sigla / Serie **ES**

Numero / Variante **02**

Agg. **00**

Orientamento

Documentazione di proprietà della Società G.B. & Partners S.r.l. E' vietata la riproduzione. Tutti i diritti sono riservati.