




SEZIONE PILASTRO TIPO
scala 1:50

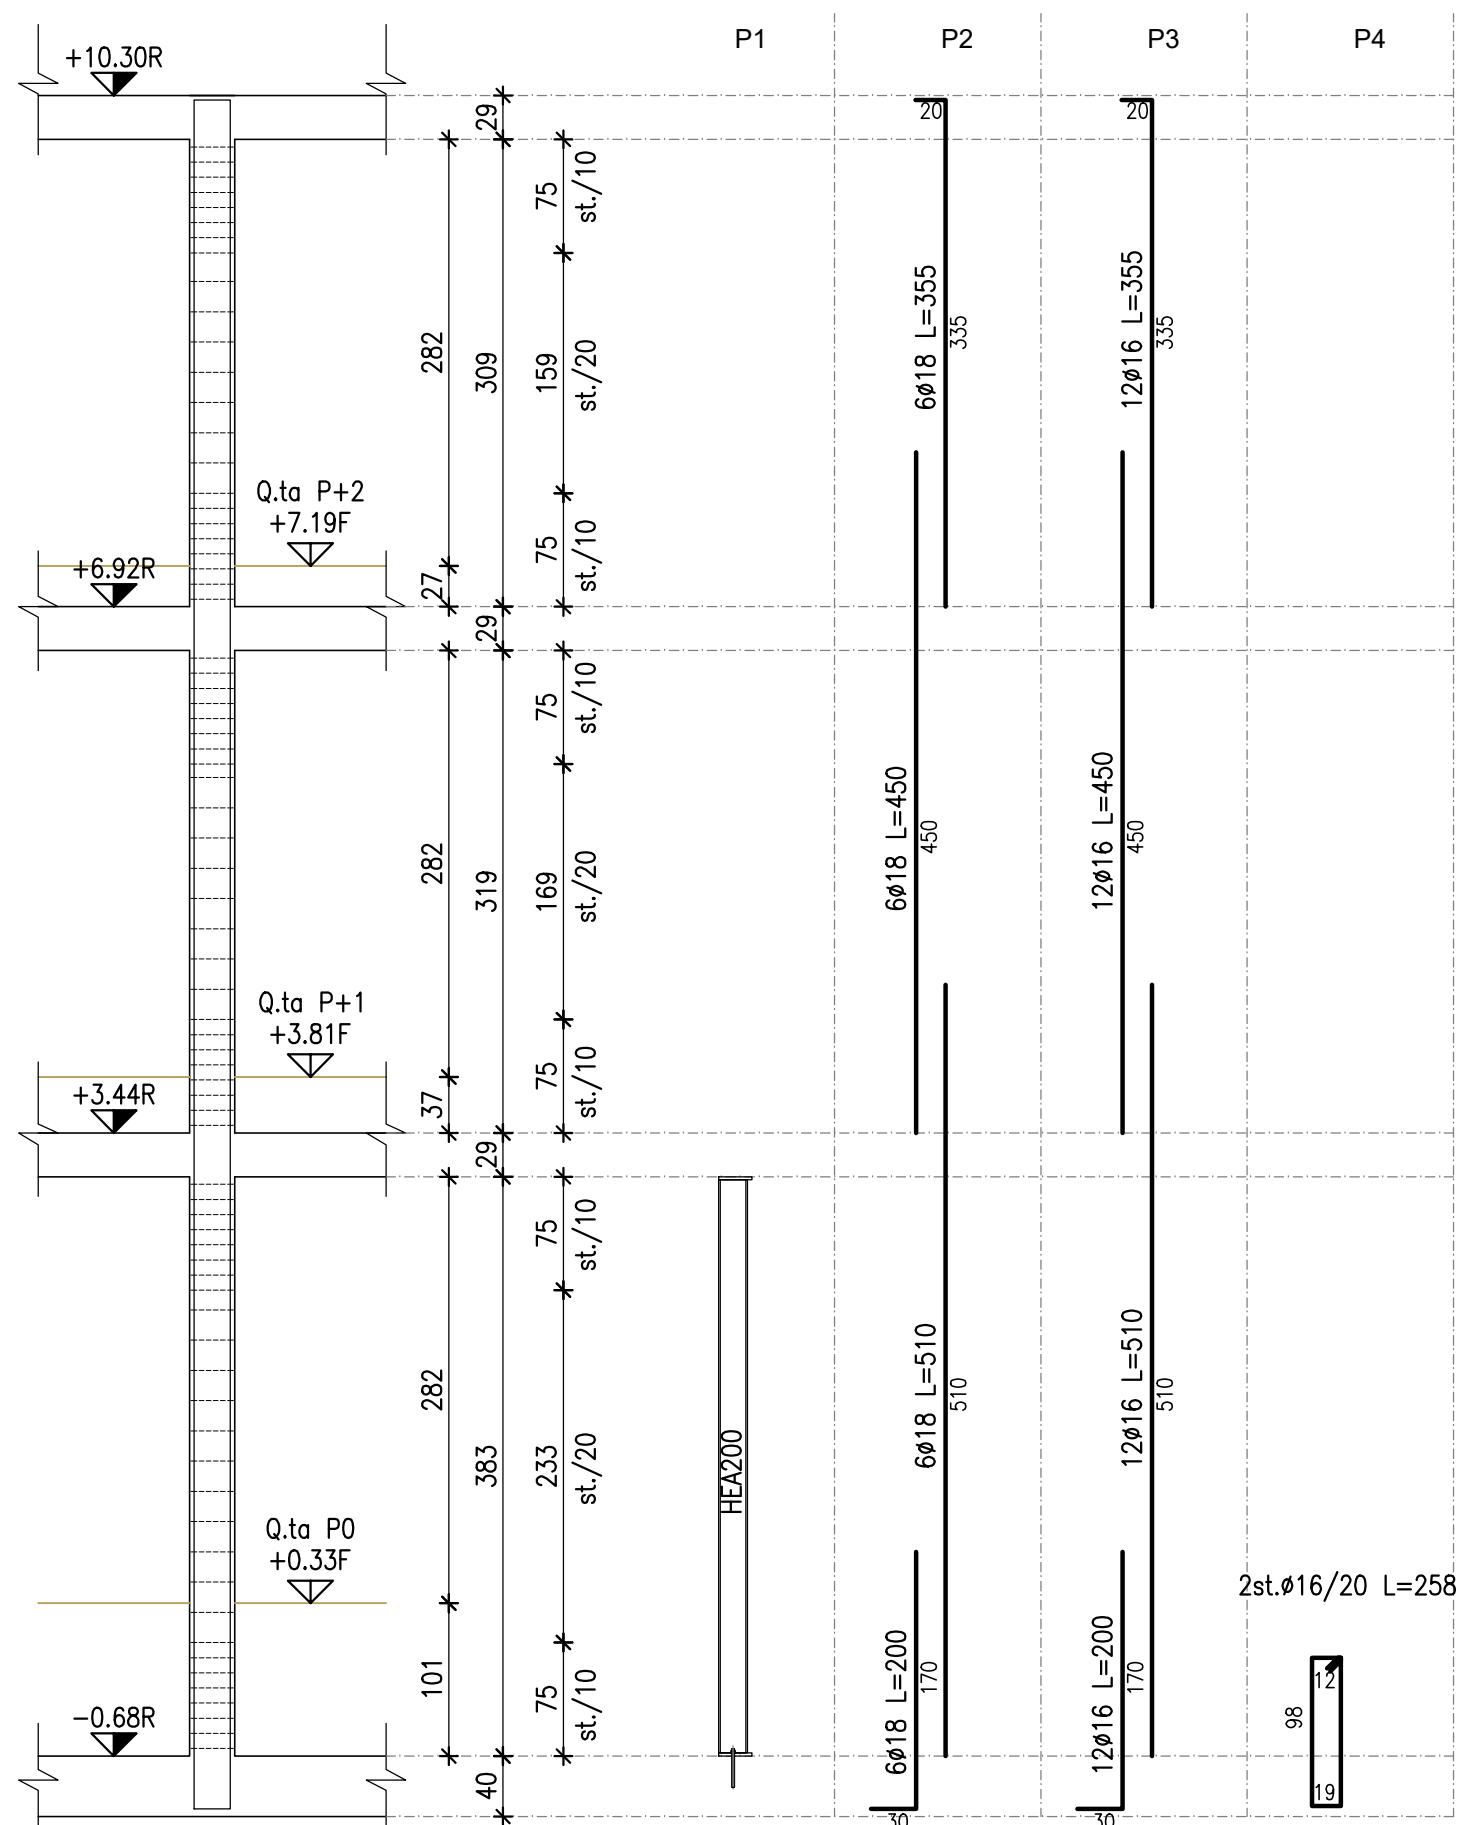


ABACO SEZIONE PILASTRI
scala 1:25

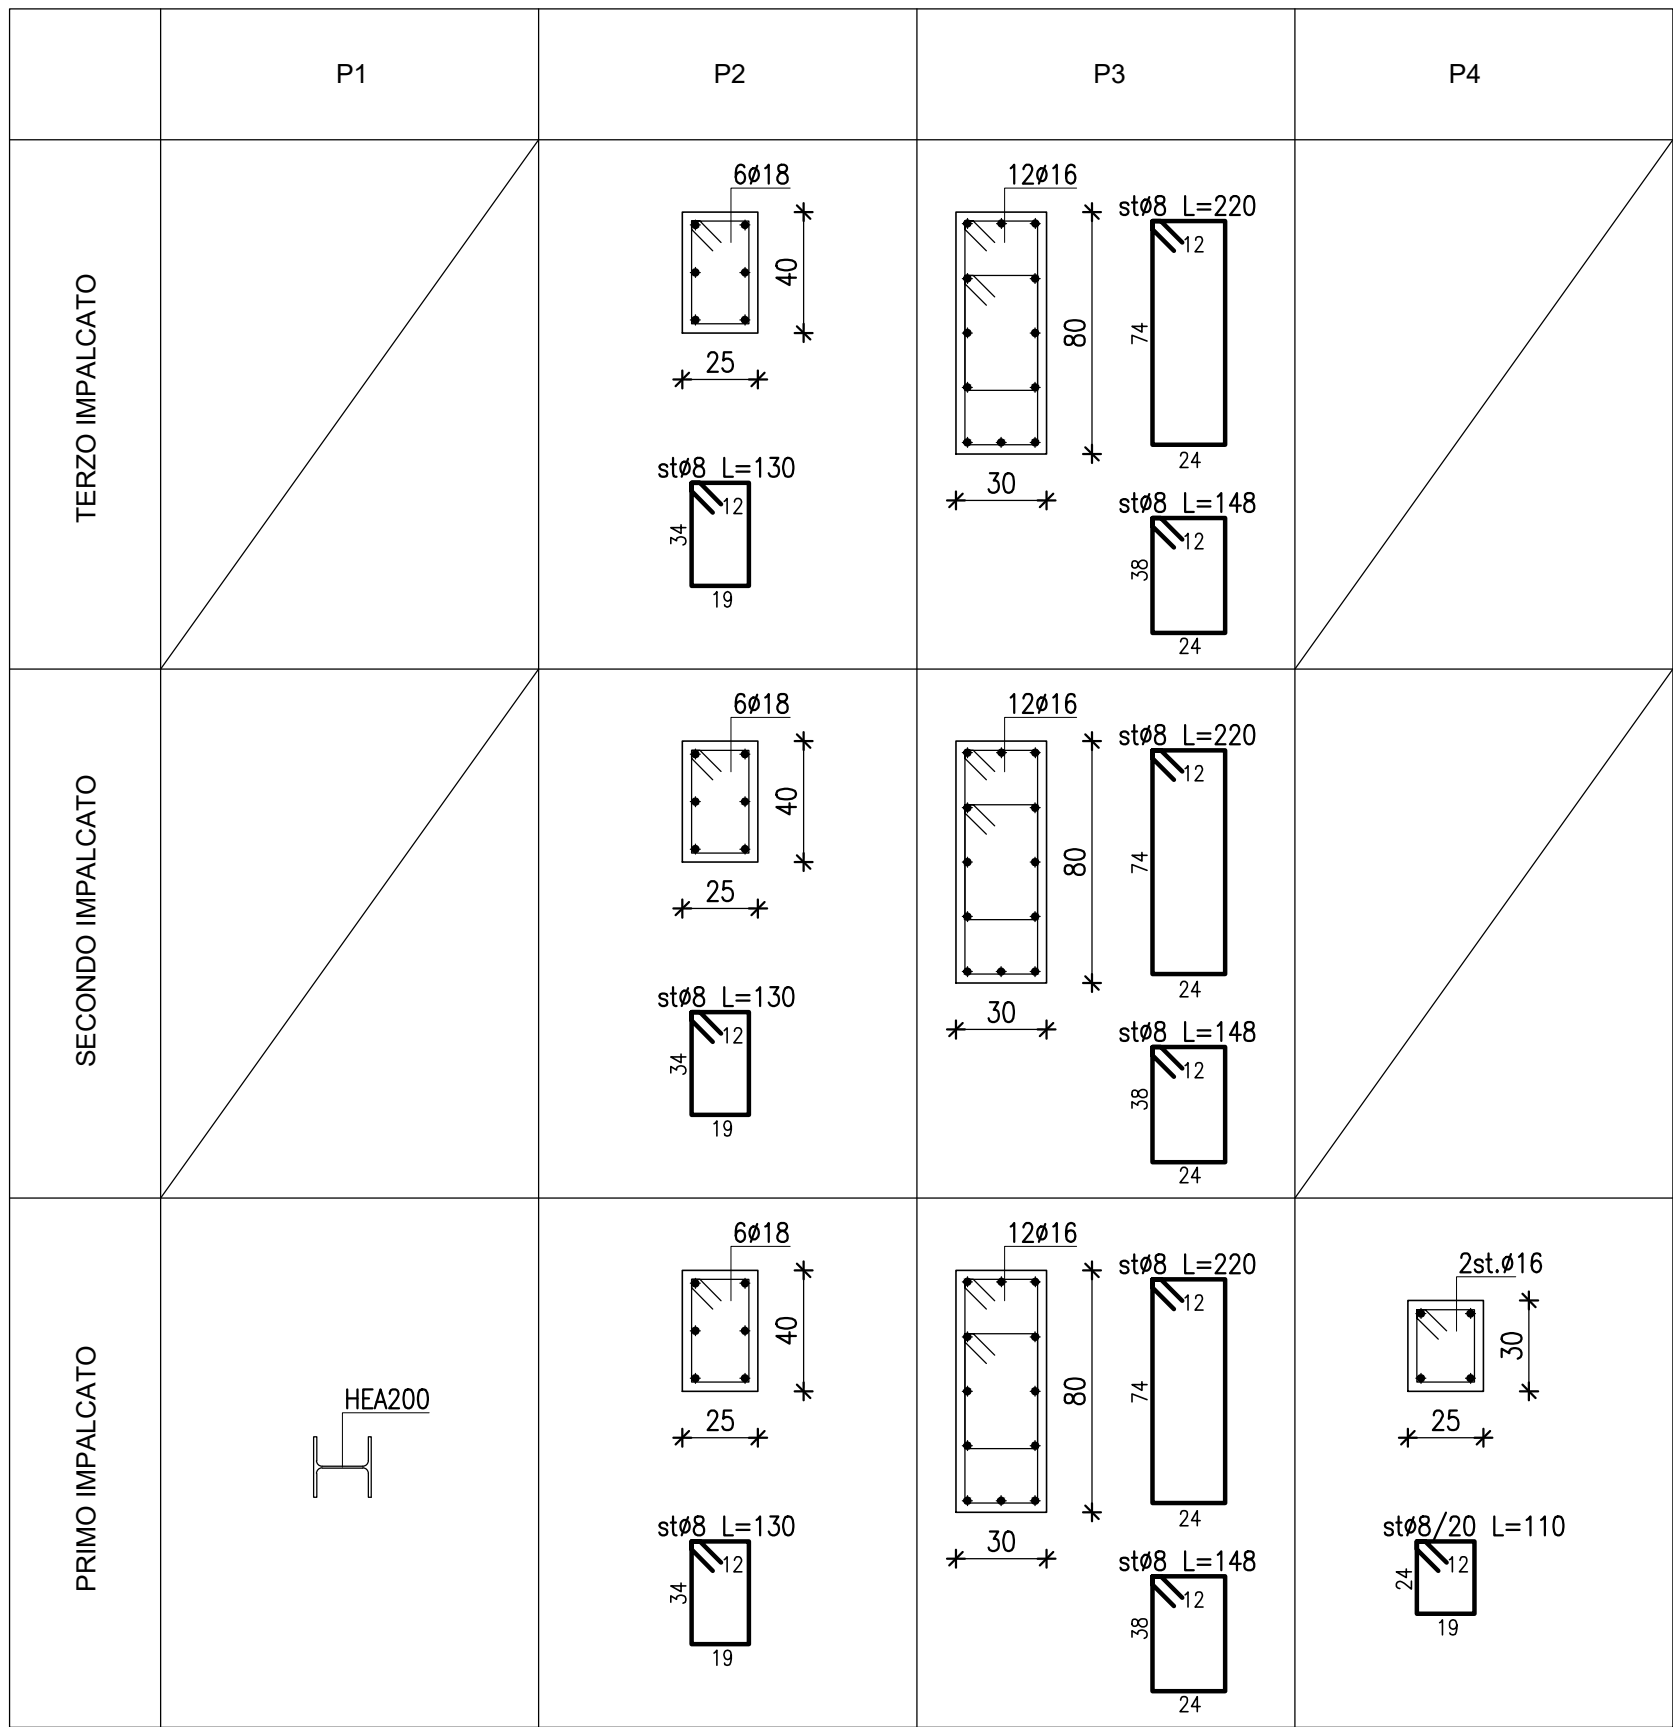

DETTAGLIO ANCORAGGI P1
scala 1:10

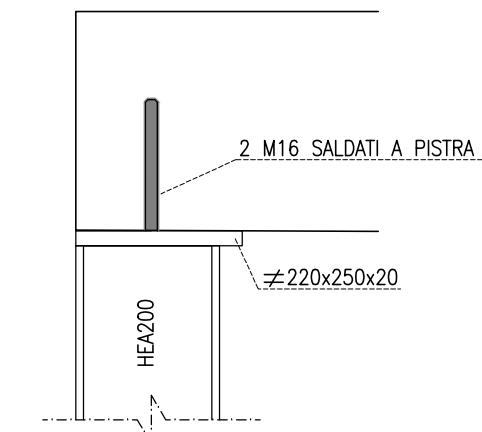

DETTAGLIO PIASTRA DI BASE
scala 1:10

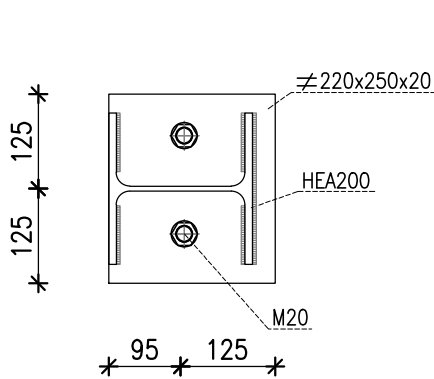

TAVOLE DI RIFERIMENTO

S00			SPECIFICHE TECNICHE
S01			PIANTA TRACCIAMENTO
S02	*		PIANTA FONDAZIONI
S03	*		PIANTA PRIMO IMPALCATO
S04	*		PIANTA SECONDO IMPALCATO
S05	*		PIANTA COPERTURA
S06			ABACO PILASTRI
S07			VANO SCALA E ASCENSORE
*			ATTENZIONE!!!! BLOCCO TAVOLE ELEMENTO STRUTTURALE

PER SPECIFICHE MATERIALI E DETTAGLI COSTRUTTIVI VEDERE TAVOLA ES-00-00_SPECIFICHE TECNICHE

GB&PARTNERS
SERVIZI E PROGETTI IMMOBILIARI
Via Verdi, 20 - 20121 Milano (MI)
Tel. 02/77777777 - Fax 02/77777777
Email: info@gbpartners.it - gbpartners@gbpartners.it
www.gbpartners.it

STEN
ENGINEERING
STRUCTURAL
Via Verdi, 20 - 20121 Milano (MI)
Tel. 02/77777777 - Fax 02/77777777
Email: info@sten.it - sten@sten.it
www.sten.it

Progetto strutturale:
Ing. Alessandro Bertozzi
Piazza Alpini, 2
25039 Travagliato (BS)
Cell. 3890777193
E-mail: alessandro@bertozzinegneria.it

COMUNE DI COLOGNO MONZESE (MI)
AREA Ex TORRIANI ARAS 01
PROGETTO ESECUTIVO
Progetto Servizi Abitativi Pubblici di via Pergolesi

N°	DATA	DESCRIZIONE	MOTIVAZIONE DELL'AGGIORNAMENTO	STUDIO	DIS.
00	22/05/2025	Prima emissione		STEN	LC
01	29/05/2025	Revisione generale		STEN	LC
02	09/06/2025	Pilastro P4		STEN	LC
03	26/01/2026	Modifiche architettoniche	260118	STEN	LC

Progetto
PROGETTO ESECUTIVO
Servizi Abitativi Pubblici
Comune di Cologno Monzese (MI)

Proponente
Officine Mak S.r.l.
Corso Europa, 10
Milano 20122

Scala
1:50
Data
26/01/2026

Tipo tavola
ESECUTIVI
Serie
STRUTTURE
Titolo
ABACO PILASTRI

Tavola nr.
Tipo
Tavola
E
Sigla /
Serie
S
Numero /
Variante
06
Agg.
03

Il Progettista
Collegio Provinciale
Geometri e Geometri Laureati
di Lodi
Inscrizione Albo
N. 267
Geometra
Gianpiero Bianchi

Il Proponente
Officine Mak S.r.l.
Corso Europa, 10
Milano 20122

Orientamento
N

Documento di proprietà della Società G.B. & Partners S.r.l. E' vietata la riproduzione. Tutti i diritti sono riservati.