




SEZIONE S1
scala 1:50

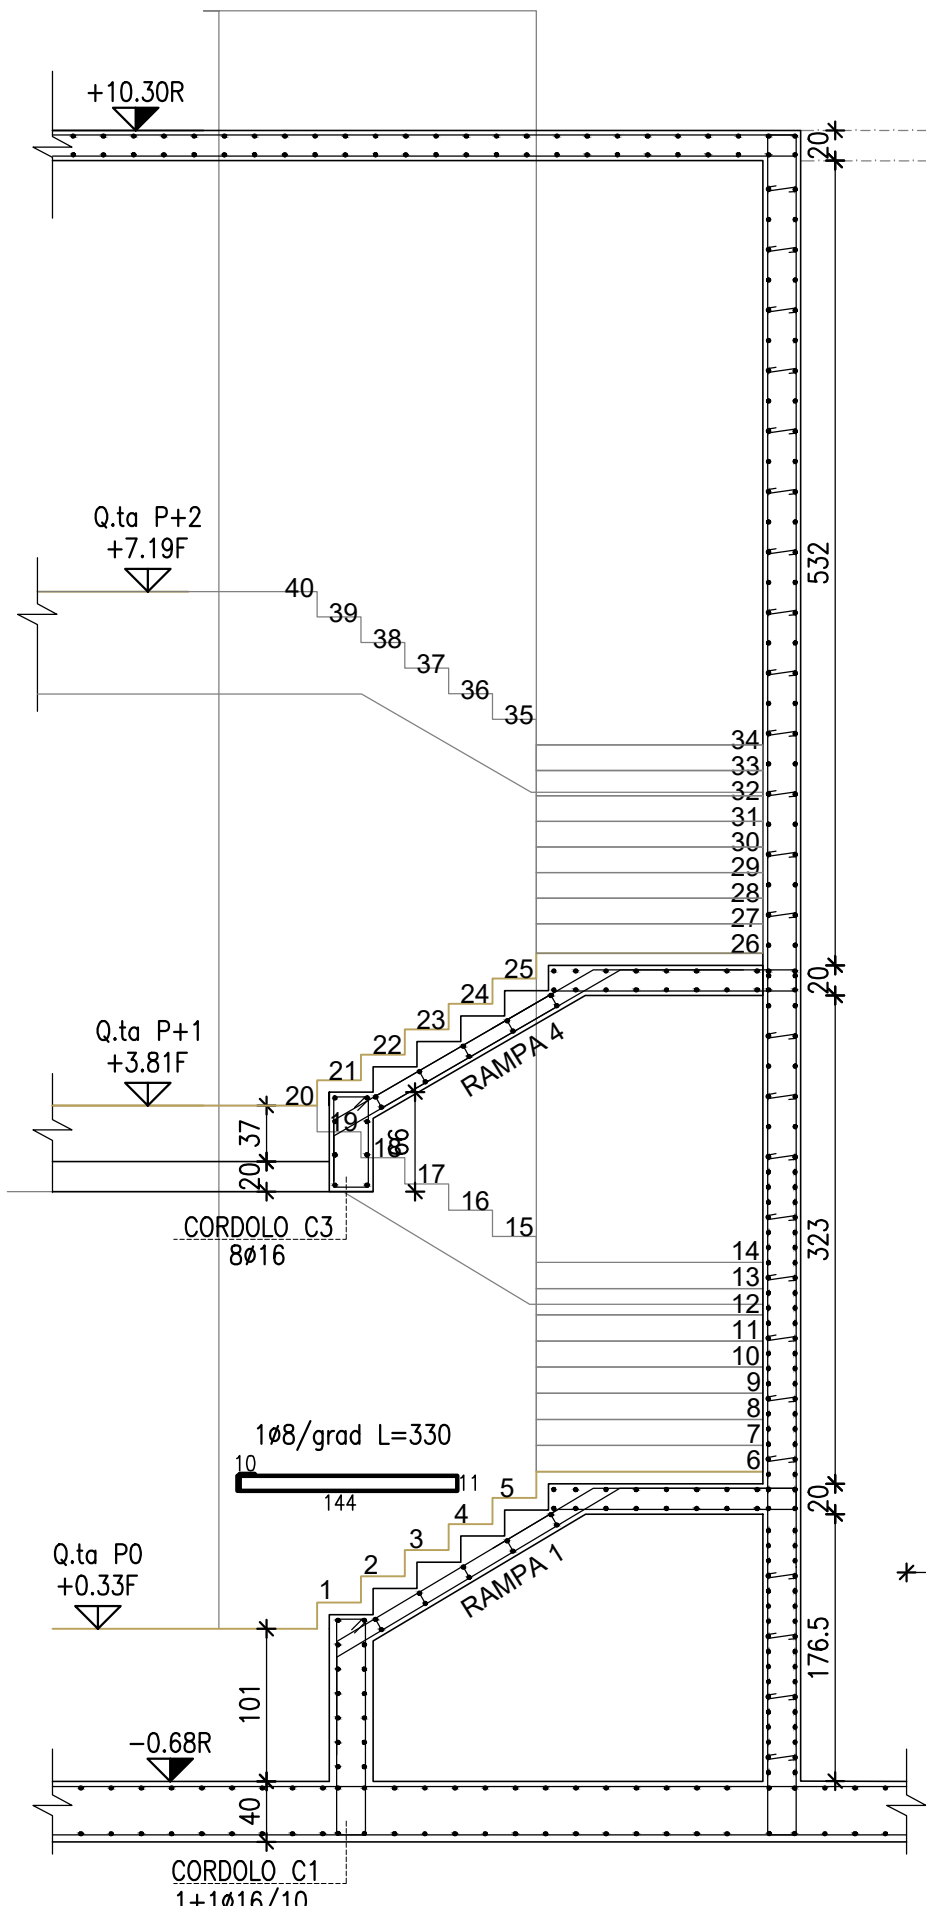


SEZIONE S2
scala 1:50

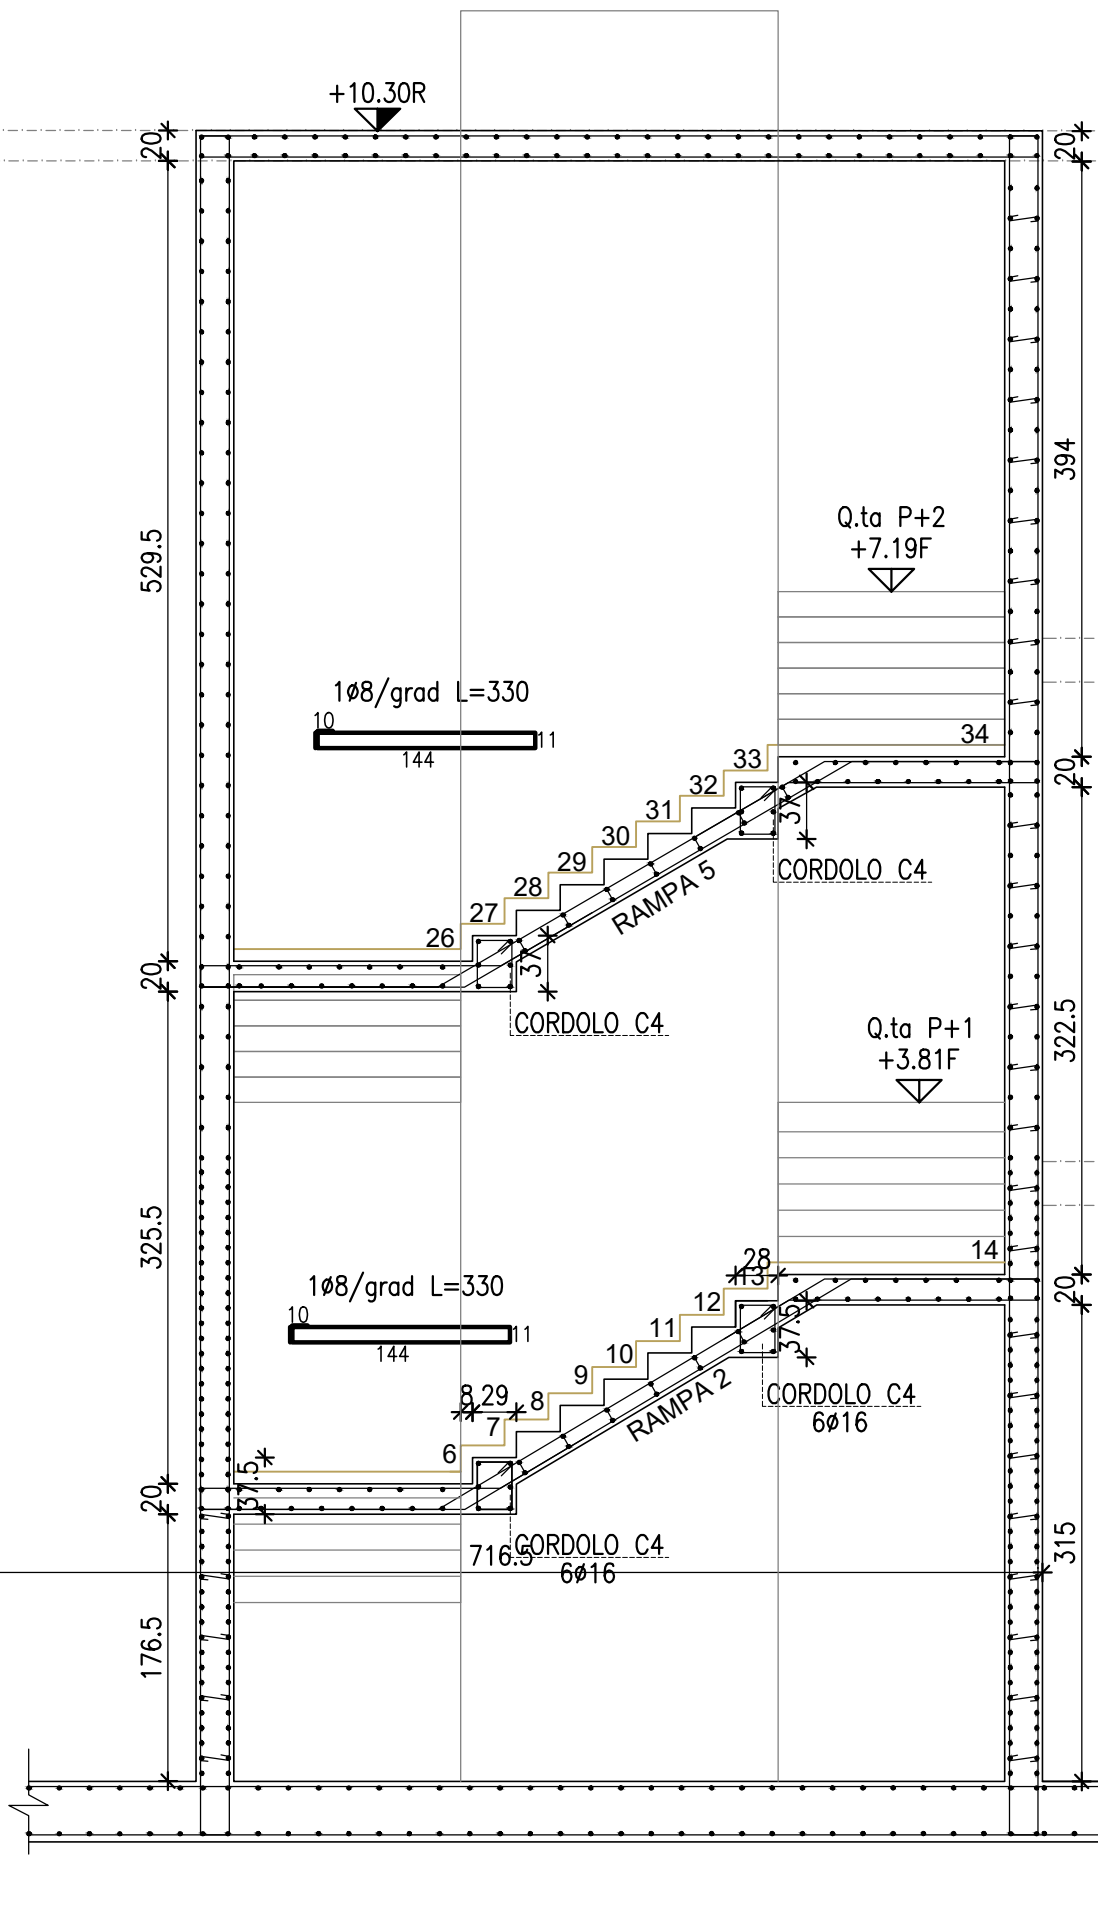


SEZIONE S3
scala 1:50

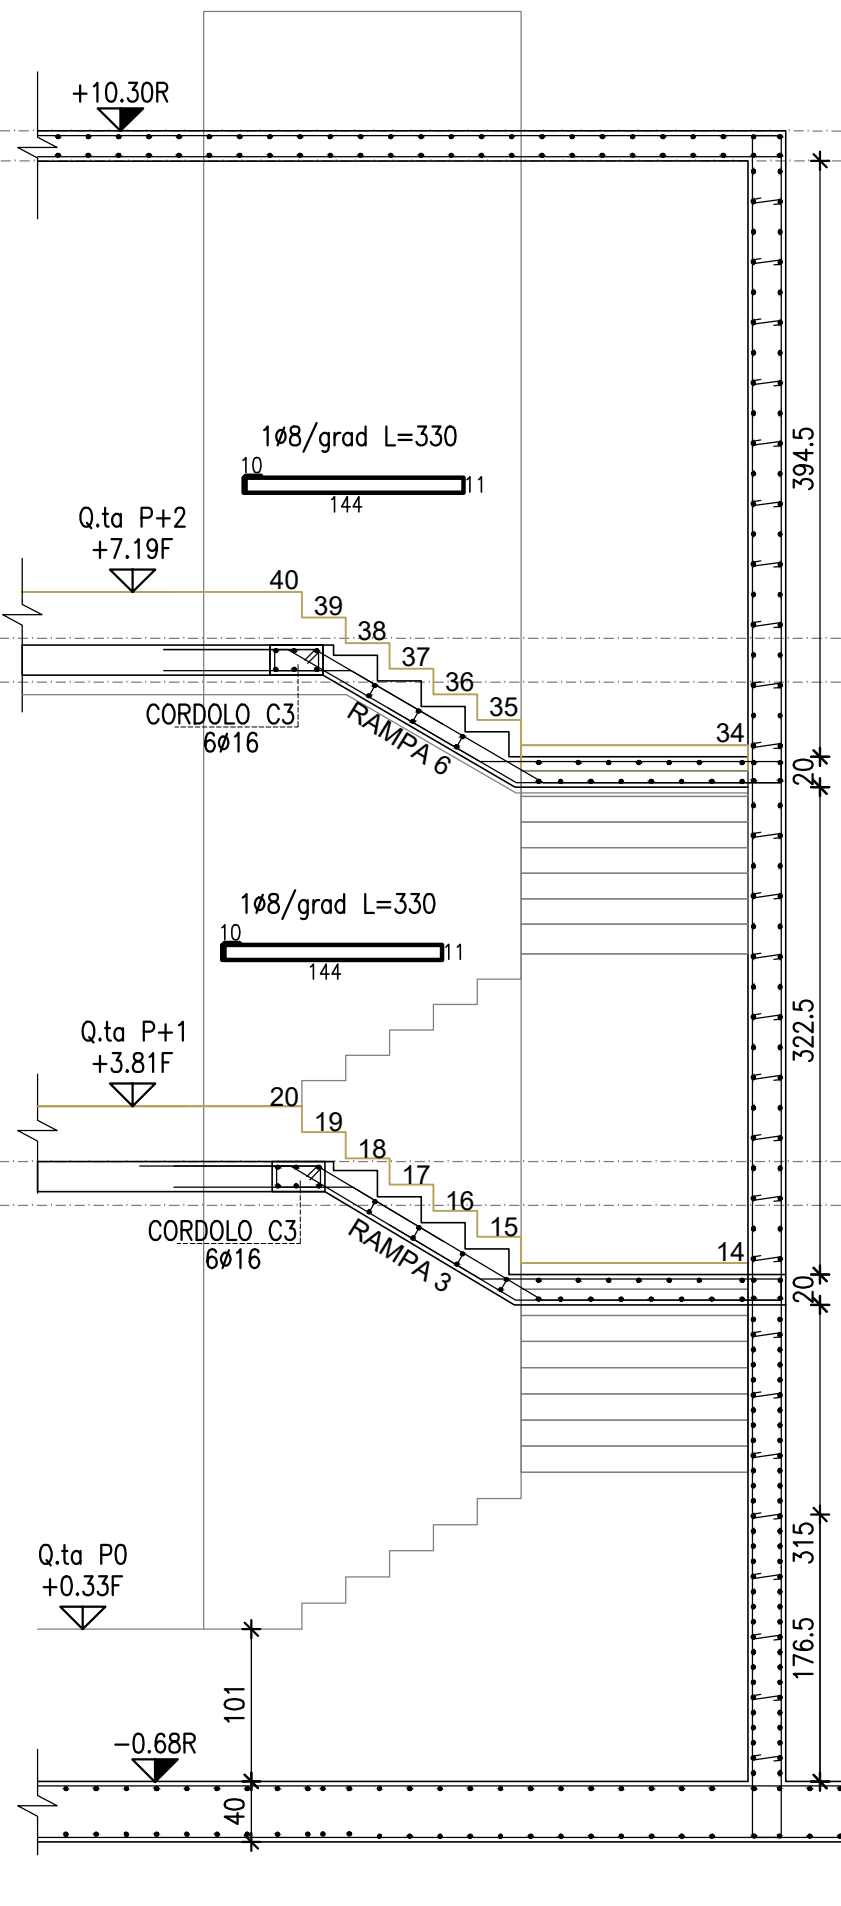

SVILUPPO FERRI VANO SCA
scala 1:50

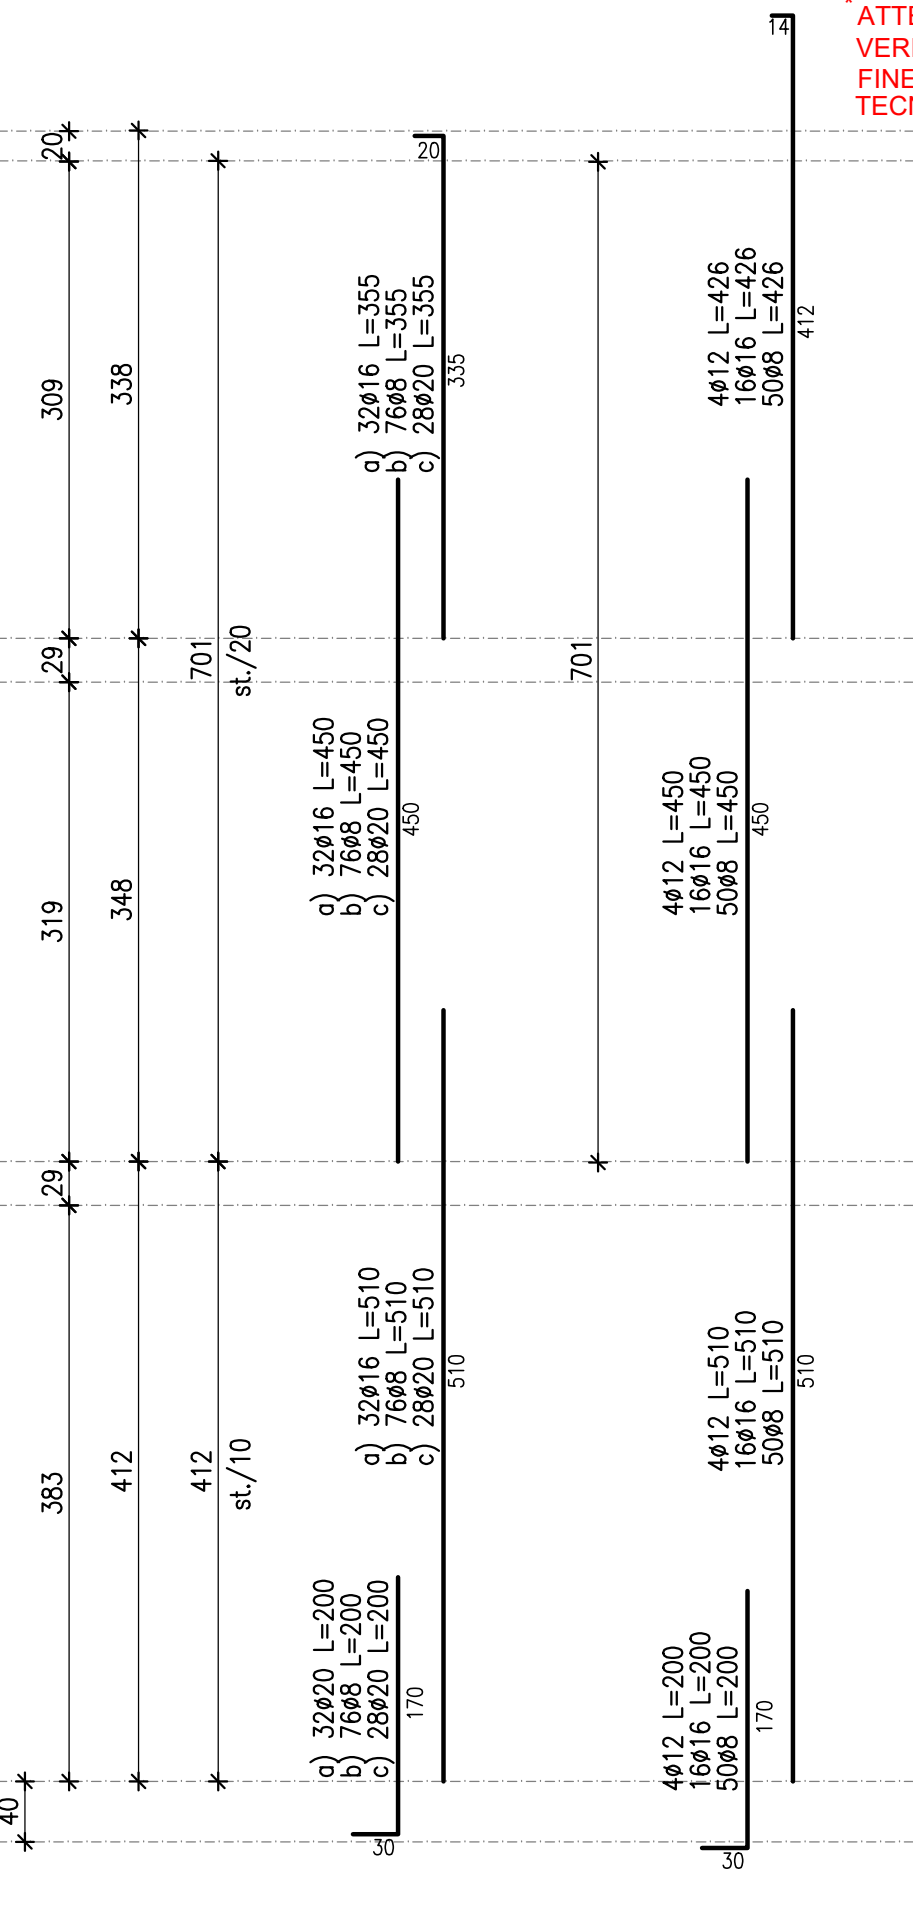

SVILUPPO FERRI VANO ASCENSORE
scala 1:50

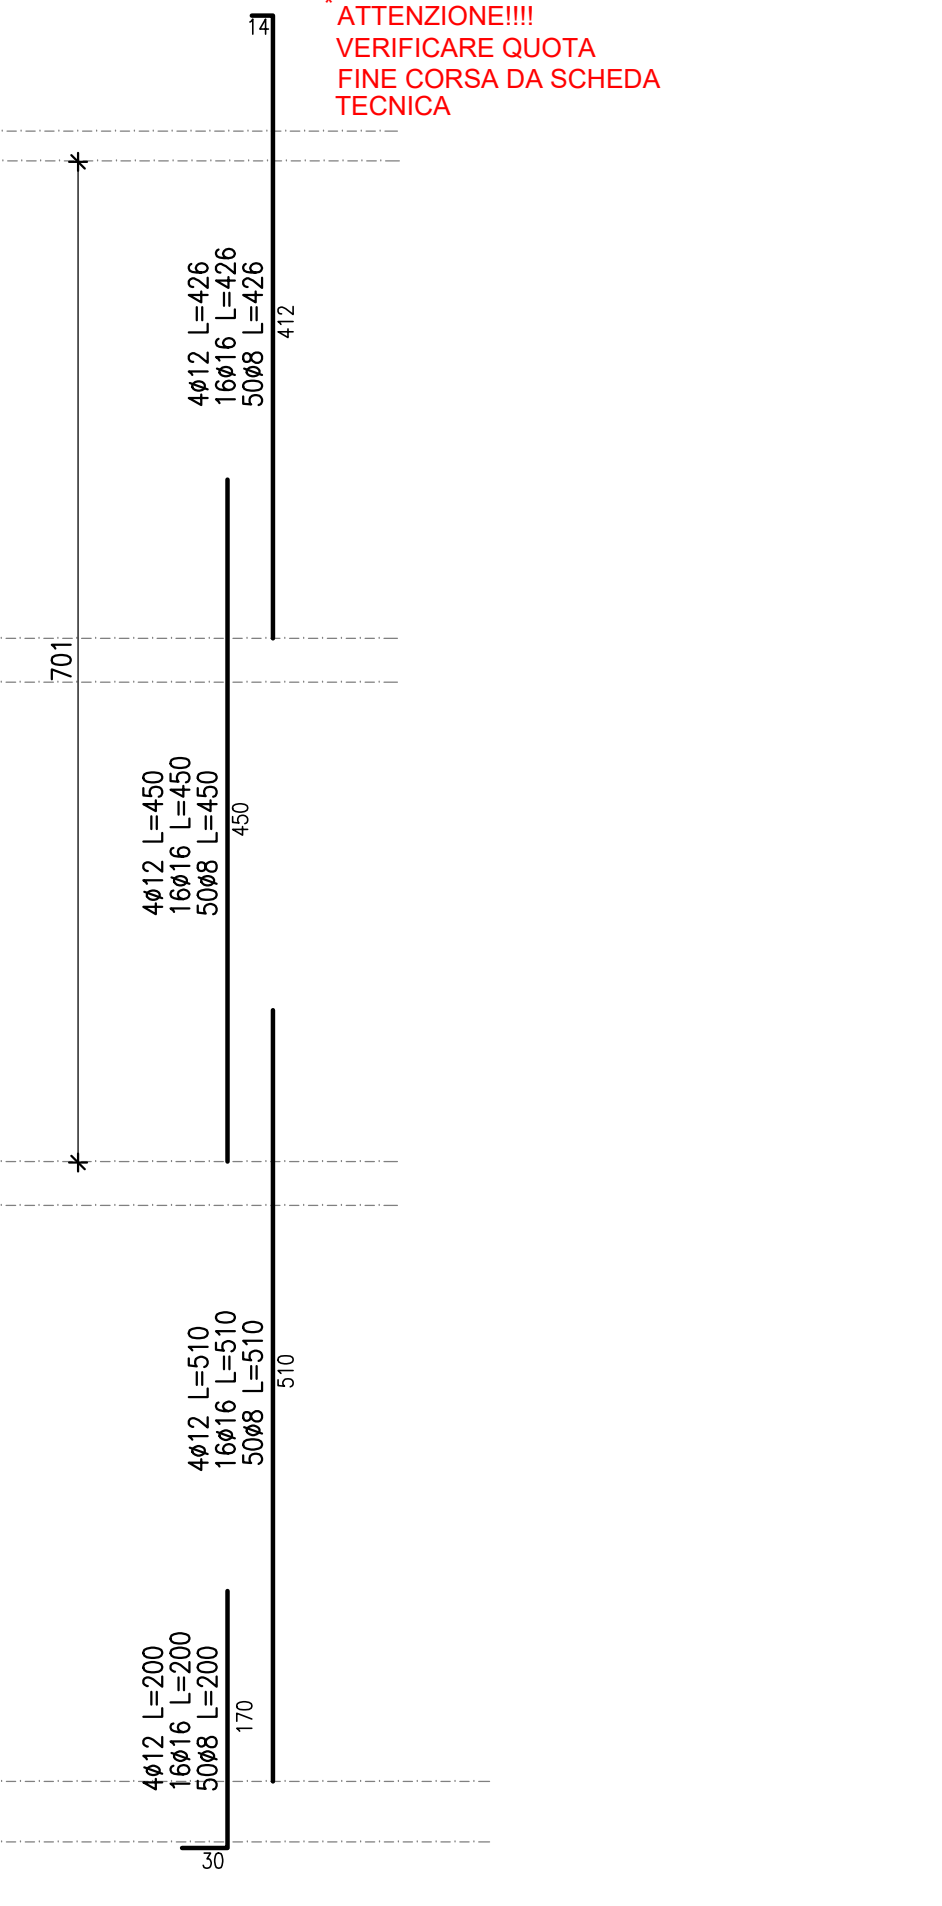


TAVOLE DI RIFERIMENTO

S00		SPECIFICHE TECNICHE
S01		PIANTA TRACCIAMENTO
S02	*	PIANTA FONDAZIONI
S03	*	PIANTA PRIMO IMPALCATO
S04	*	PIANTA SECONDO IMPALCATO
S05	*	PIANTA COPERTURA
S06		ABACO PILASTRI
S07		VANO SCA E ASCENSORE
*		ATTENZIONE!!!! BLOCCO TAVOLE ELEMENTO STRUTTURALE


CARICHI SCA

PESO PROPRIO	500 kg/mq
CARICO PERMANENTE NON STRUTTURALE	300 kg/mq
CARICO VARIABILE	400 kg/mq

DETTAGLIO GRADINO RAMPA 4-5-6
scala 1:20

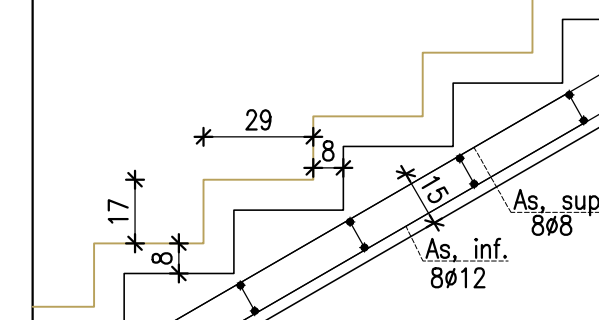

DETTAGLIO GRADINO RAMPA 1-2-3
scala 1:20

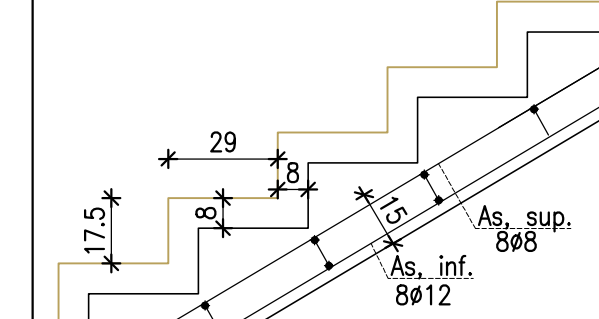

PER SPECIFICHE MATERIALI E DETTAGLI COSTRUTTIVI VEDERE TAVOLA ES-00-00_SPECIFICHE TECNICHE

GB&PARTNERS SERVIZI PROGETTI IMMOBILIARI
STEN STRUCTURAL ENGINEERING
Progetto strutturale:
 Ing. Alessandro Bertozzi
 Piazza Alpi, 2
 25039 Travagliato (BS)
 Cell. 3890777193
 E-mail: alessandra@bertozzingeria.it

Il Progettista



Il Proponente




COMUNE DI COLOGNO MONZESE (MI)
AREA Ex TORRIANI ARAS 01
PROGETTO ESECUTIVO
 Progetto Servizi Abitativi Pubblici di via Pergolesi

N°	DATA	DESCRIZIONE MOTIVAZIONE DELL'AGGIORNAMENTO	STUDIO	DIS.
00	22/05/2025	Prima emissione	STEN	LC
01	29/05/2025	Revisione generale	STEN	LC
02	26/01/2026	Aggiornamento architettonico 260118	STEN	LC
03	05/02/2026		STEN	LC


Progetto PROGETTO ESECUTIVO Servizi Abitativi Pubblici Comune di Cologno Monzese(MI)	Proponente Officine Mak S.r.l. Corso Europa, 10 Milano 20122	Scala 1:50 Data 05/02/2025
--	--	---

Tipo tavola ESECUTIVI Serie STRUTTURE Titolo VANO SCA E ASCENSORE	Tavola nr. Tipo Tavola Sigla / Serie Numero / Variante Agg.	E S 07 03
---	--	--


Orientamento

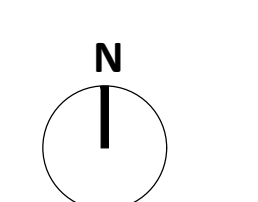


STRALCIO PANTA FONDAZIONI
scala 1:50

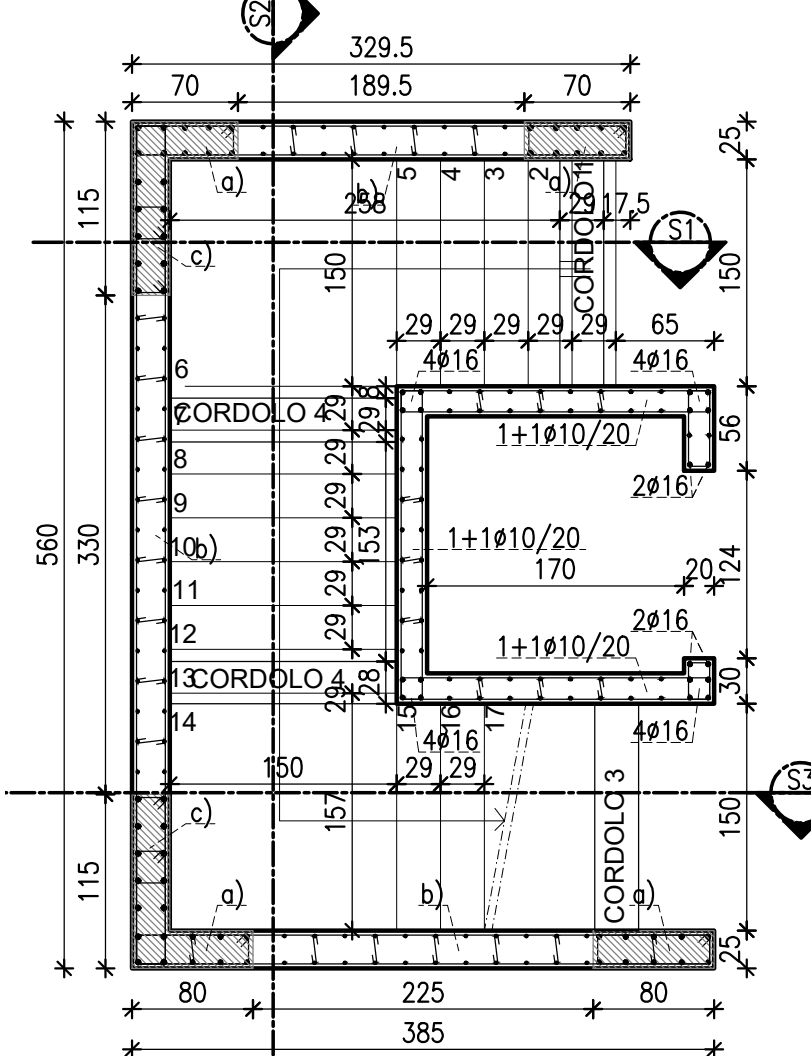


STRALCIO PANTA PRIMO IMPALCATO
scala 1:50

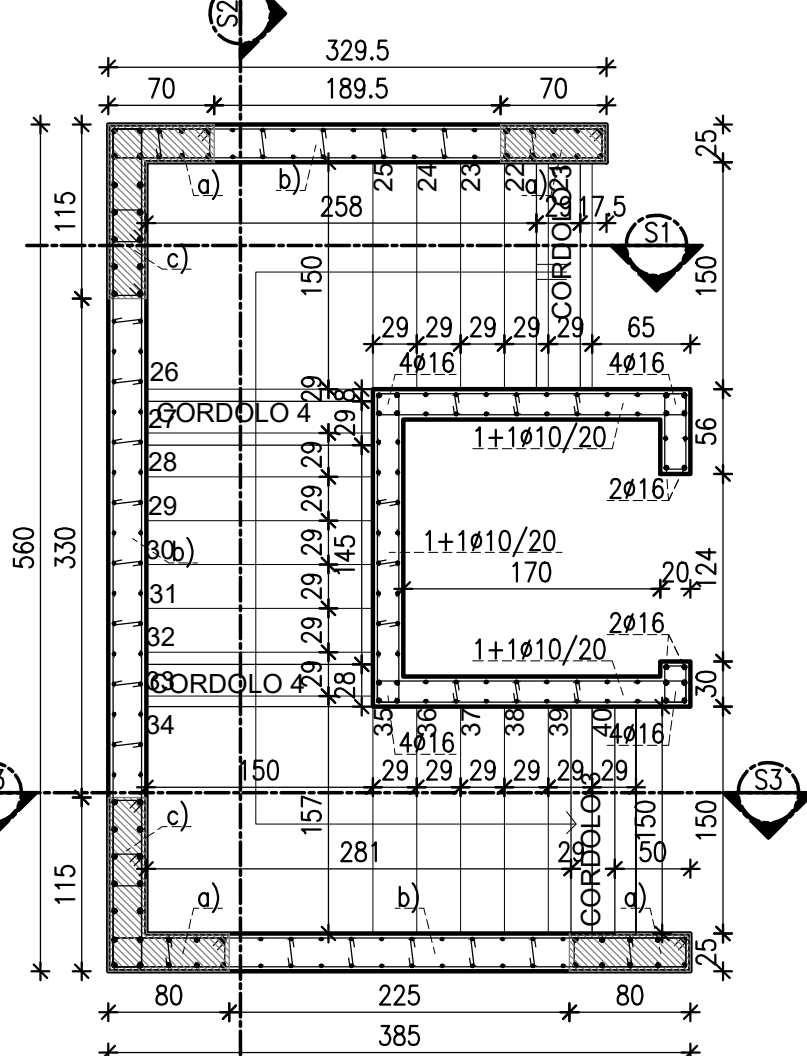

STRALCIO PANTA SECONDO IMPALCATO
scala 1:50

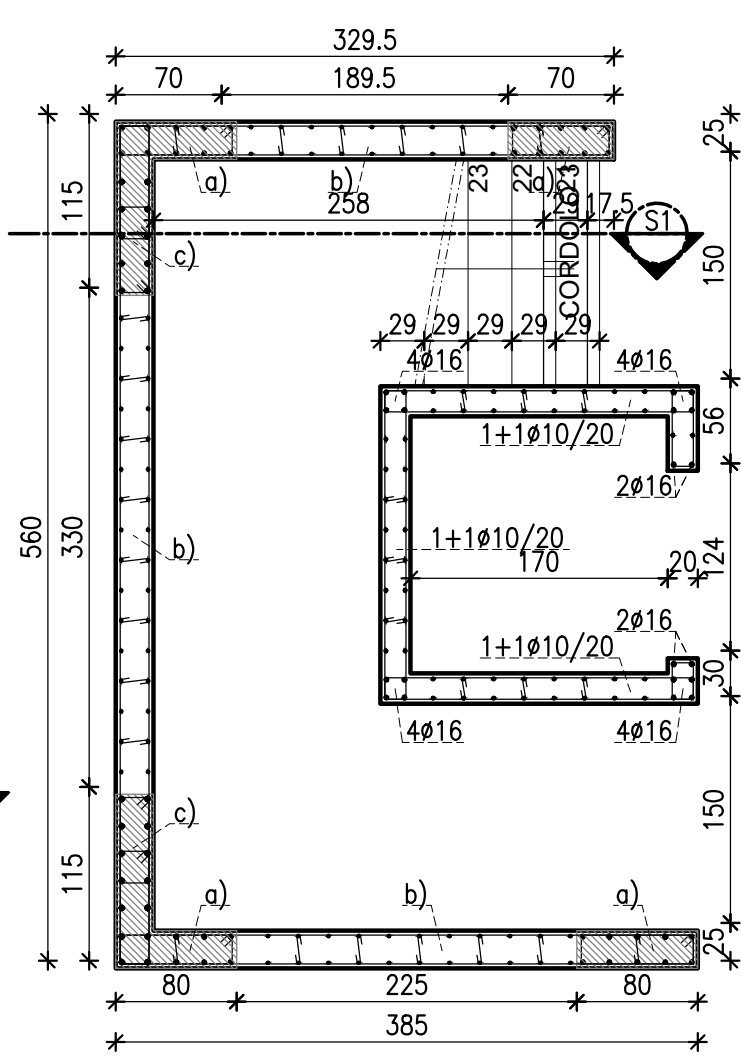

STRALCIO PANTA FUORI CORSA
scala 1:50

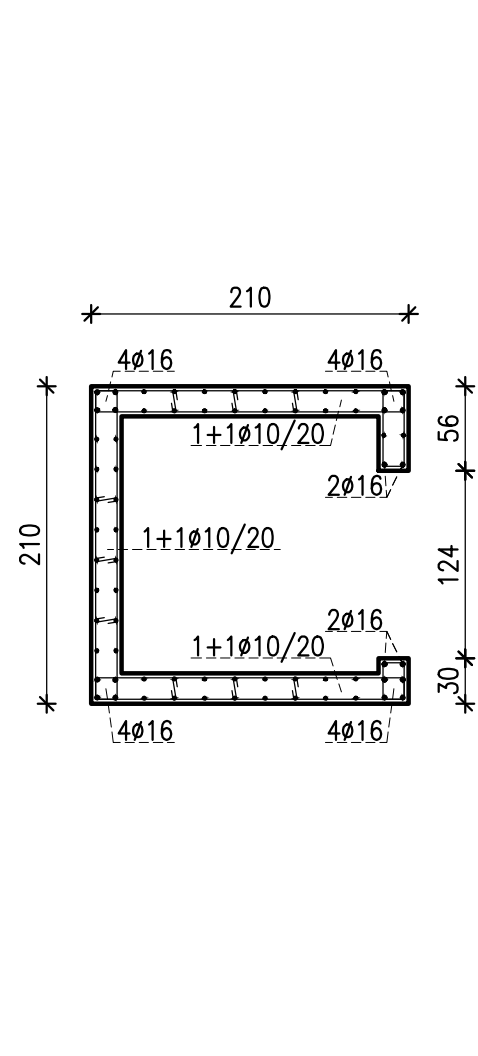

STRALCIO VANO SCA E ASCENSORE -- ARMATURA CORRENTE
scala 1:50

