




scala 1:50

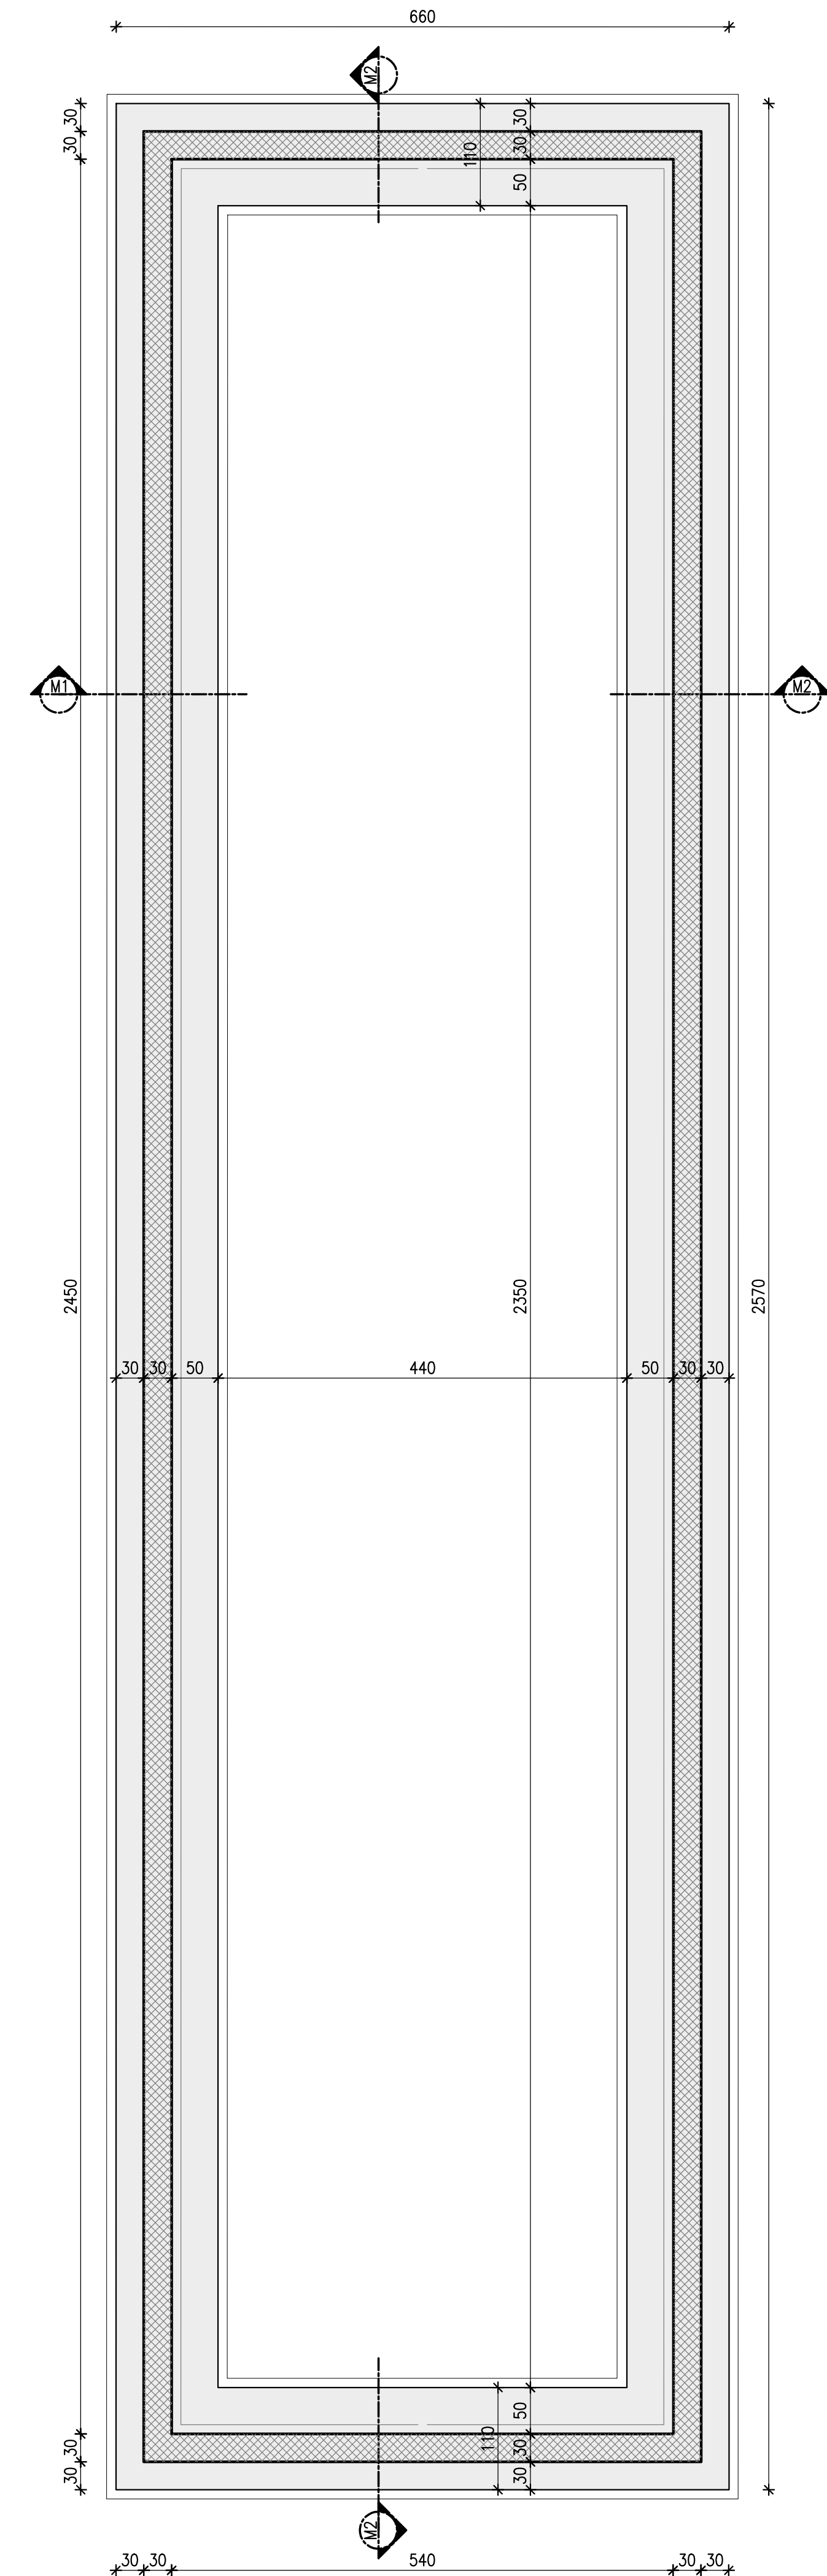


scala 1:50

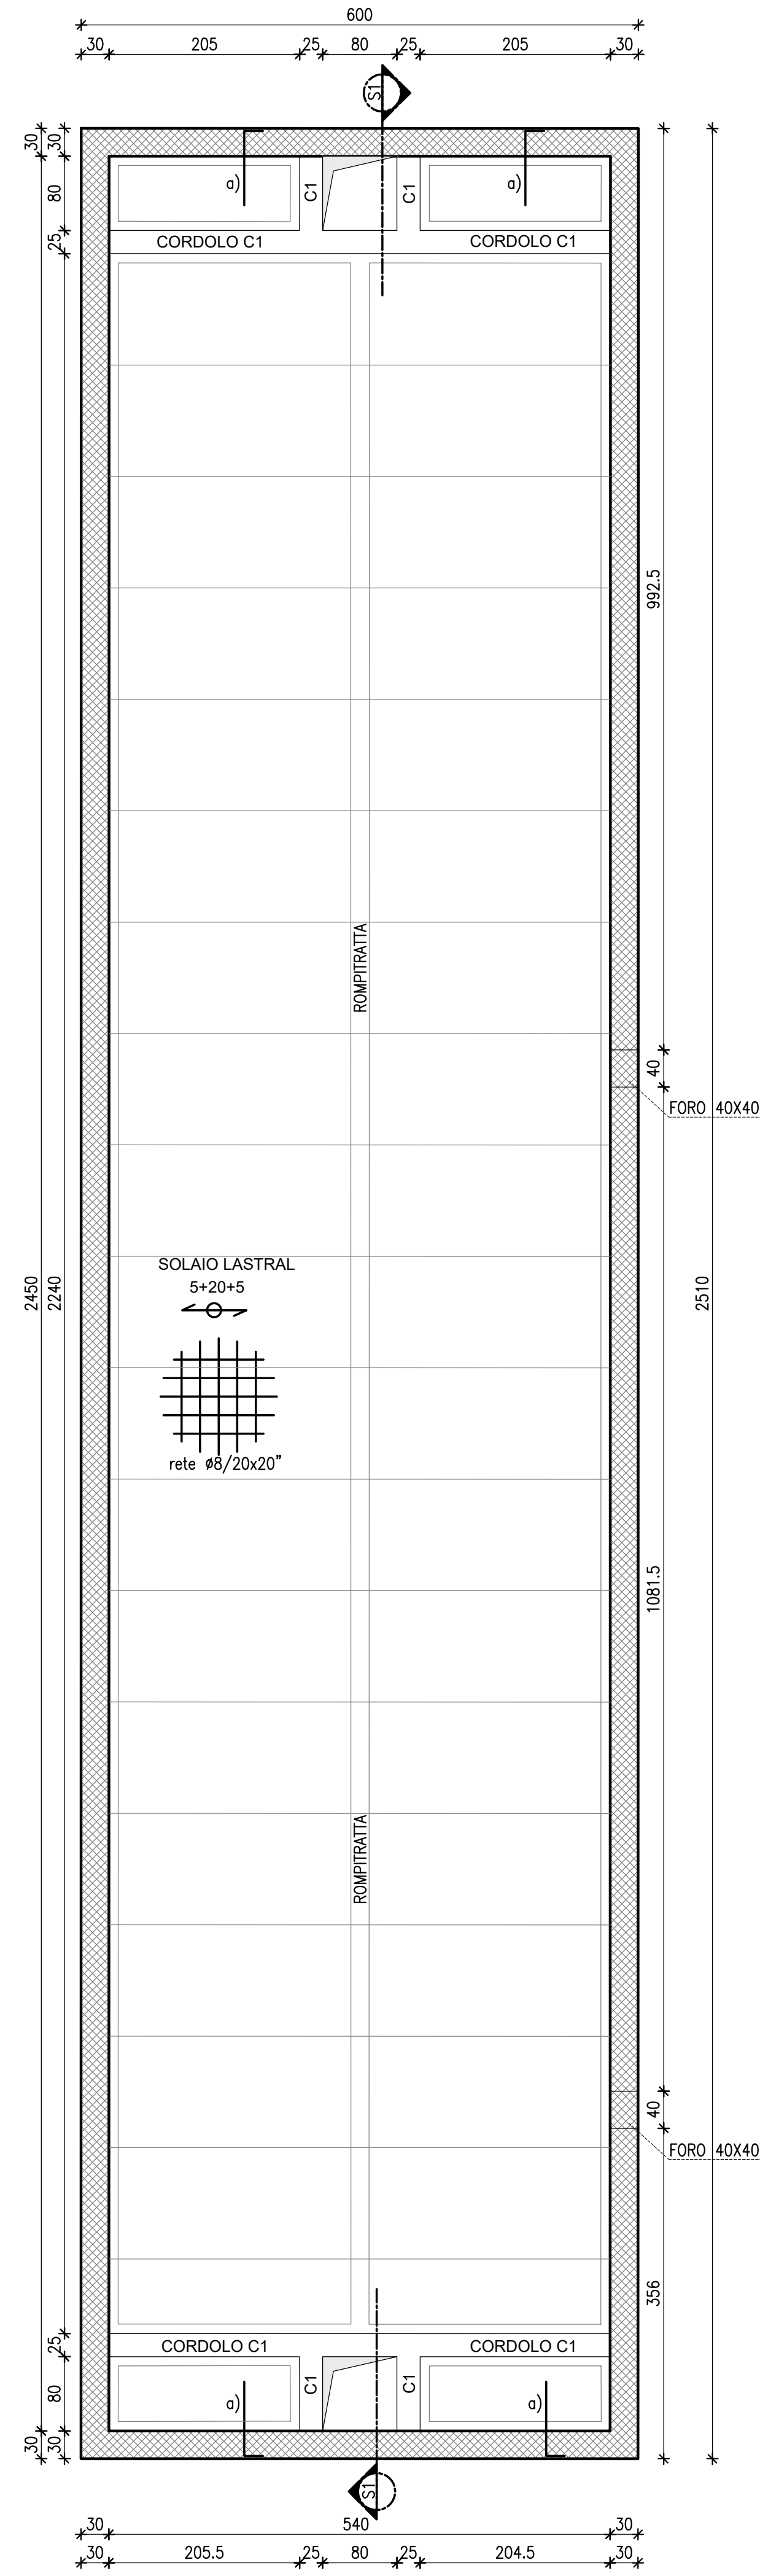


scala 1:25

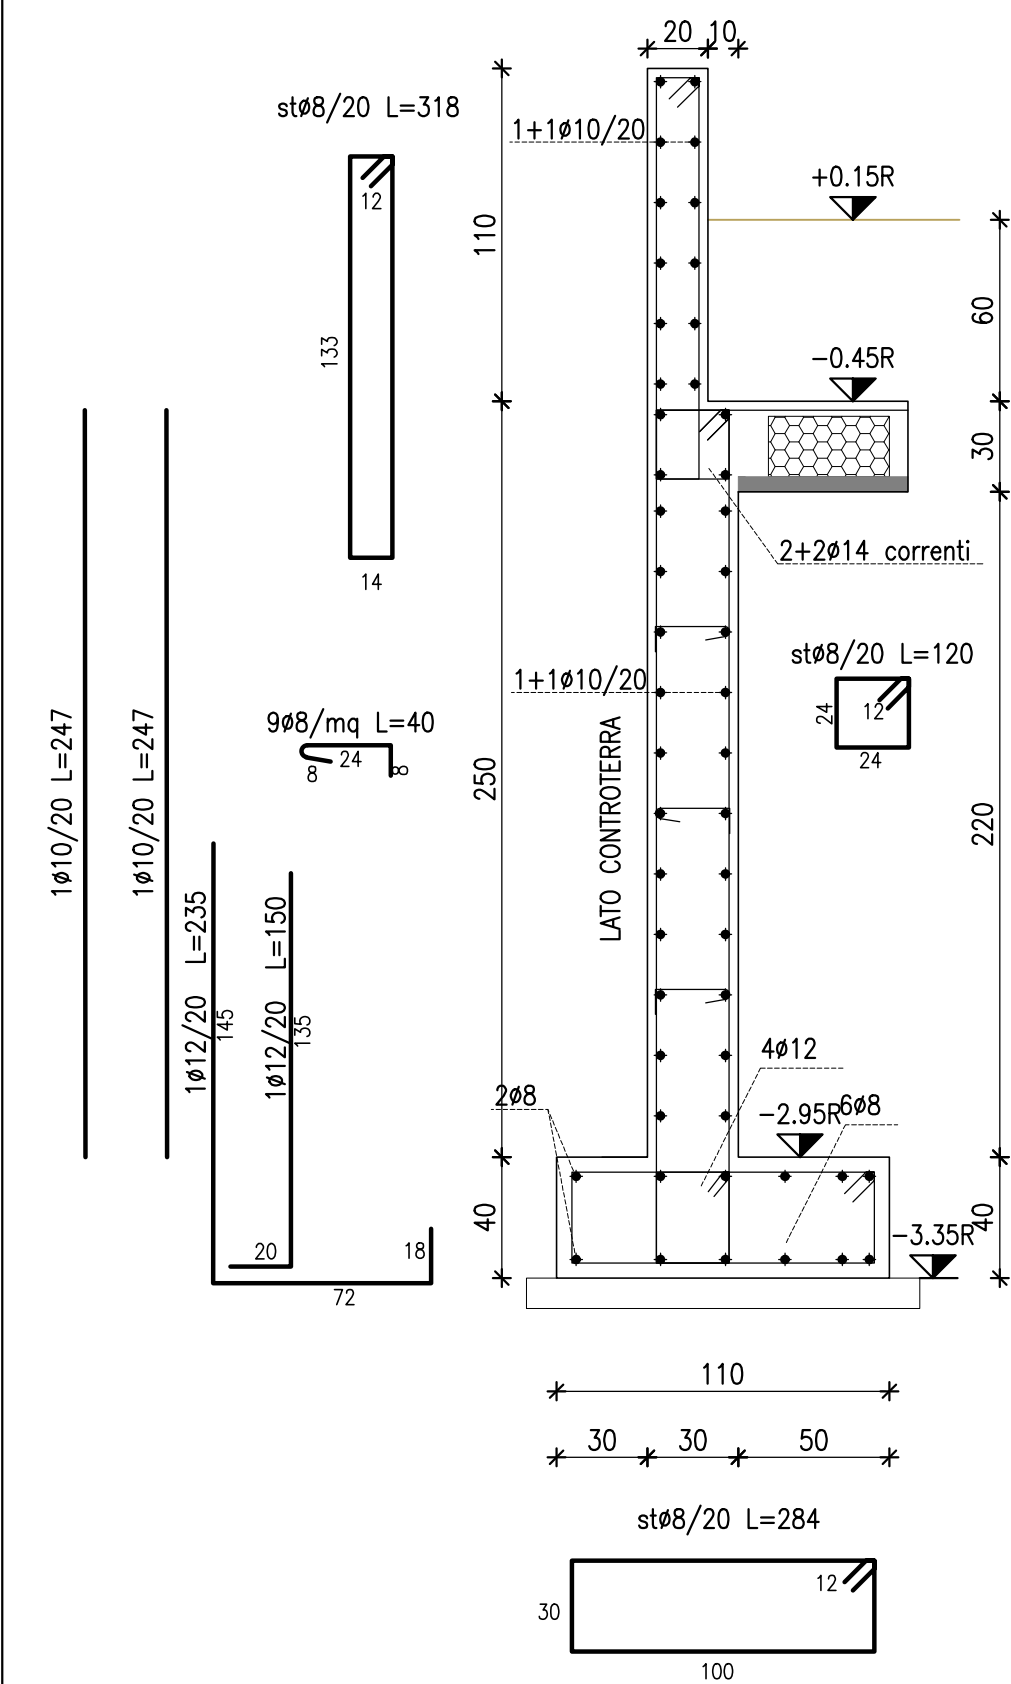

scala 1:25

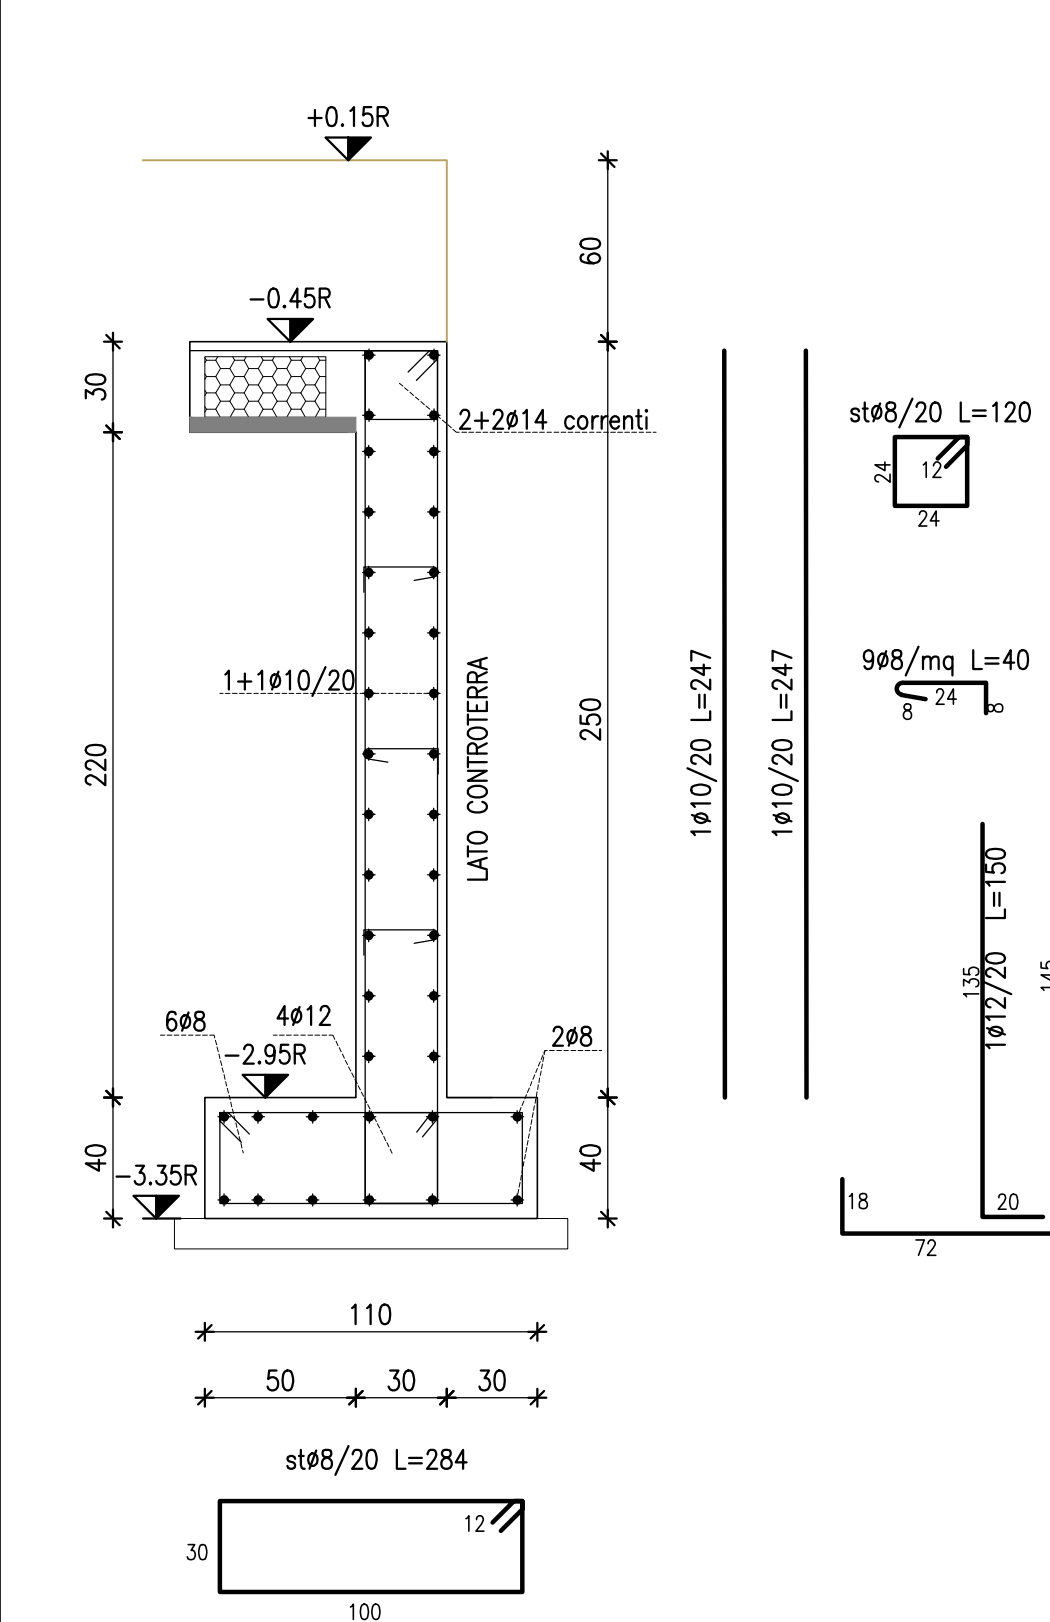


scala 1:50

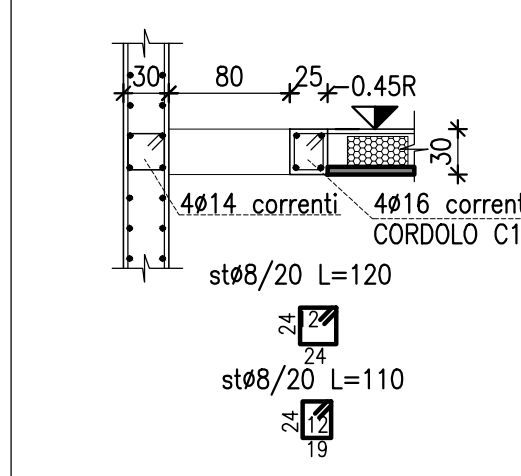


S00			SPECIFICHE TECNICHE
S01			PIANTA TRACCIAMENTO
S02	*		PIANTA FONDAZIONI
S03	*		PIANTA PRIMO IMPALCATO
S04	*		PIANTA SECONDO IMPALCATO
S05	*		PIANTA COPERTURA
S06			ABACO PILASTRI
S07			VANO SCALA E ASCENSORE
S08			VASCA ACQUE METEORICHE
*			ATTENZIONE!!!! BLOCCO TAVOLE ELEMENTO STRUTTURALE

PESO PROPRIO SOLAIO 5+20+5	430 kg/mq
CARICO PERMANENTE NON STRUTTURALE INTERNO	900 kg/mq
CARICO VARIABILE	400 kg/mq


scala 1:50

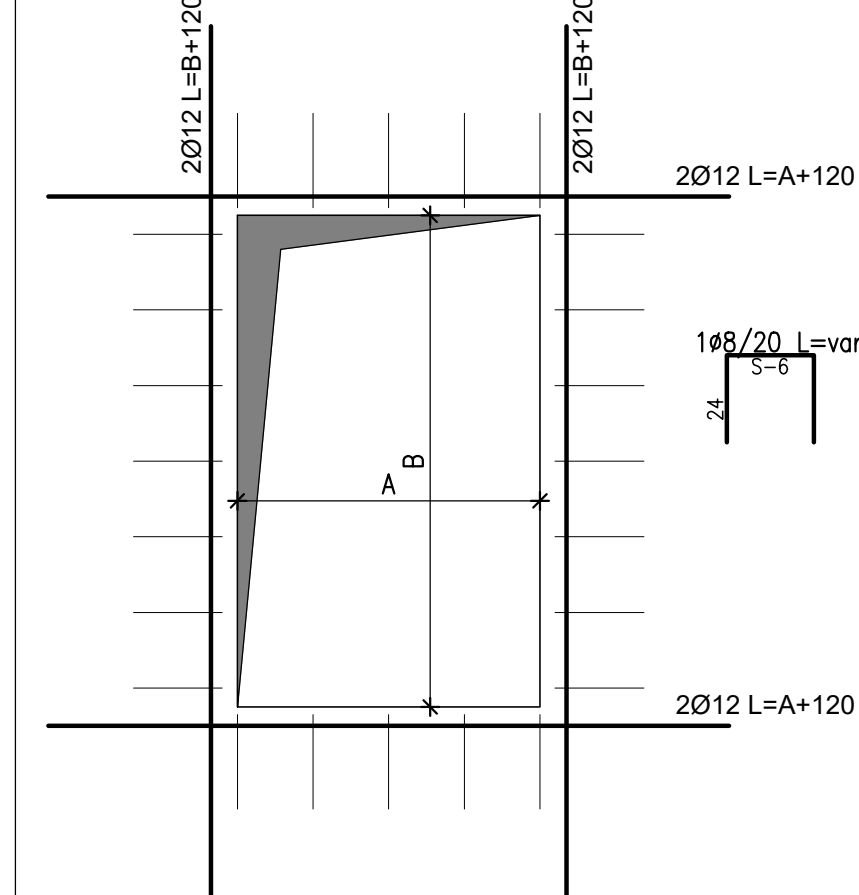

scala 1:20

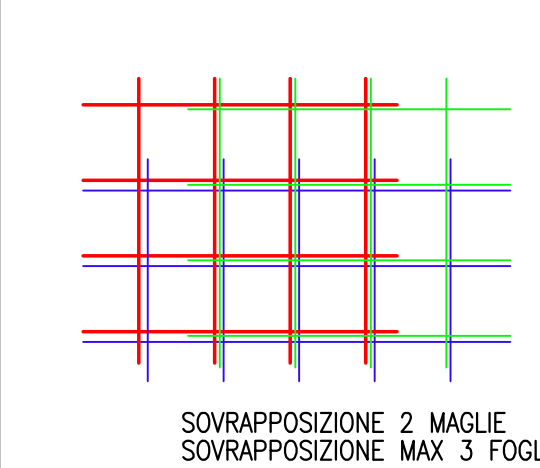

scala 1:20

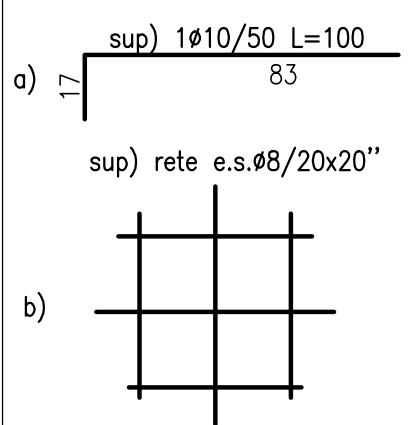

PER SPECIFICHE MATERIALI E DETTAGLI COSTRUTTIVI VEDERE TAVOLA ES-00-00_SPECIFICHE TECNICHE



GB & PARTNERS
SOCIETÀ PER AZIONI
S.r.l. - 20139 Milano (MI)
Sede e Direzione Generale
Via Sallustiana, 10
00100 Roma (RM)
Tel. 02 574941
Fax 02 57494200
E-mail: gb@gbpartners.it




20139 MILANO
20139 MILANO

Progetto strutturale:
Ing. Alessandro Bertozzi
Piazza Alipini, 2
25039 Travagliato (BS)
Cell. 3890777193
E-mail: alessandro@bertozzingegneria.it

COMUNE DI COLOGNO MONZESE (MI)
AREA Ex TORRIANI ARAS 01
PROGETTO ESECUTIVO
Progetto Servizi Abitativi Pubblici di via Pergolesi

N°	DATA	DESCRIZIONE	MOTIVAZIONE DELL'AGGIORNAMENTO	STUDIO	DIS.
00	29/07/2025	Prima emissione		STEN	ST

Il Progettista

Collegio Provinciale
Geometri e Geometri Laureati
di Lodi

 Iscrizione Albo
N. 267

Geometra
Gianpiero Bianchi



Il Proponente

Progetto	Proponente	Scala
<u>PROGETTO ESECUTIVO</u>	Officine Mak S.r.l.	
	Corso Europa, 10	1:50
Servizi Abitativi Pubblici	Milano 20122	
Comune di Cologno		Data
Monzese(MI)		29/07/2025

Tipo tavola		Tavola nr.	
ESECUTIVI		Tipo Tavola	E
Serie		Sigla / Serie	S
STRUTTURE			
Titolo		Numero / Variante	08
VASCA ACQUE METEORICHE		Agg.	00

Orientamento

