
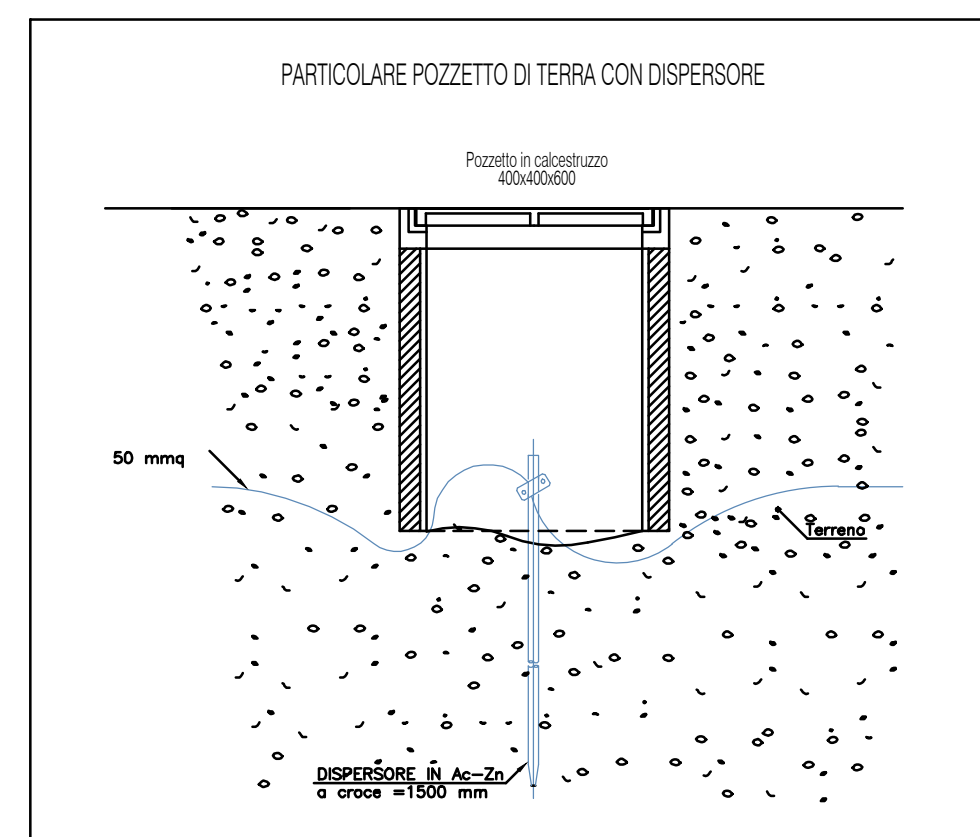
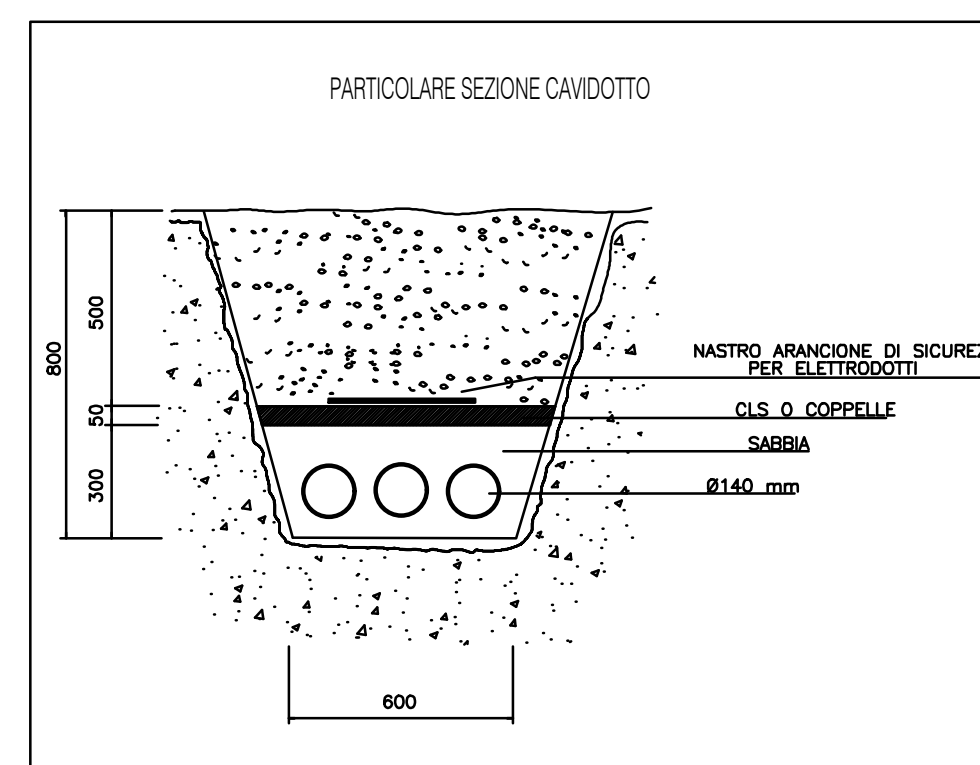
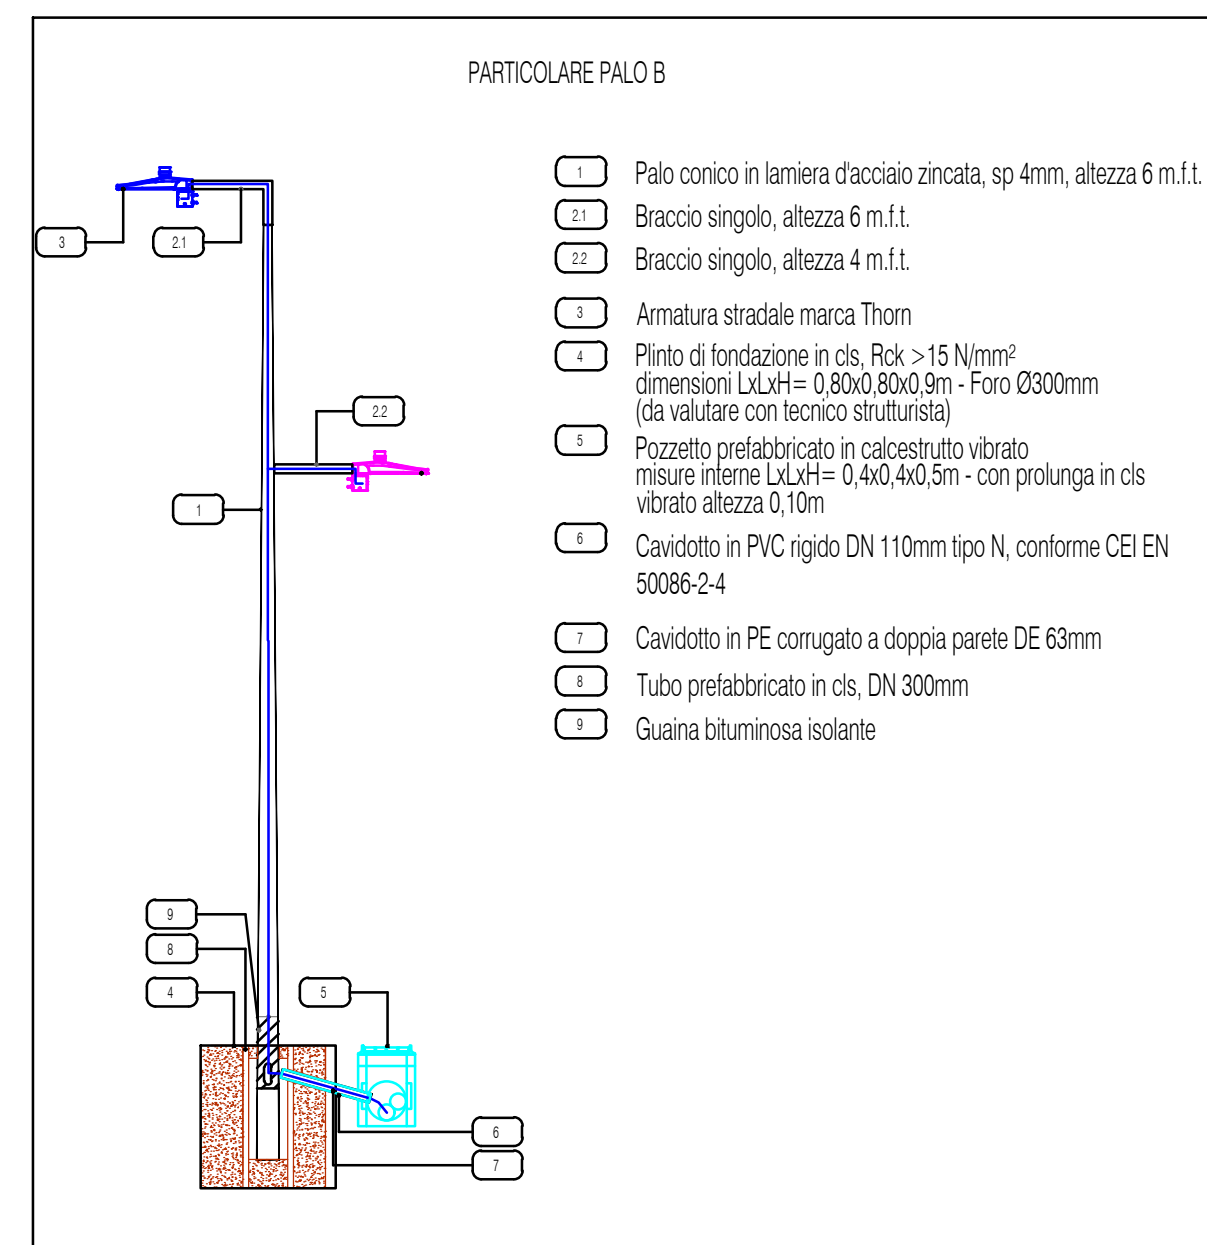
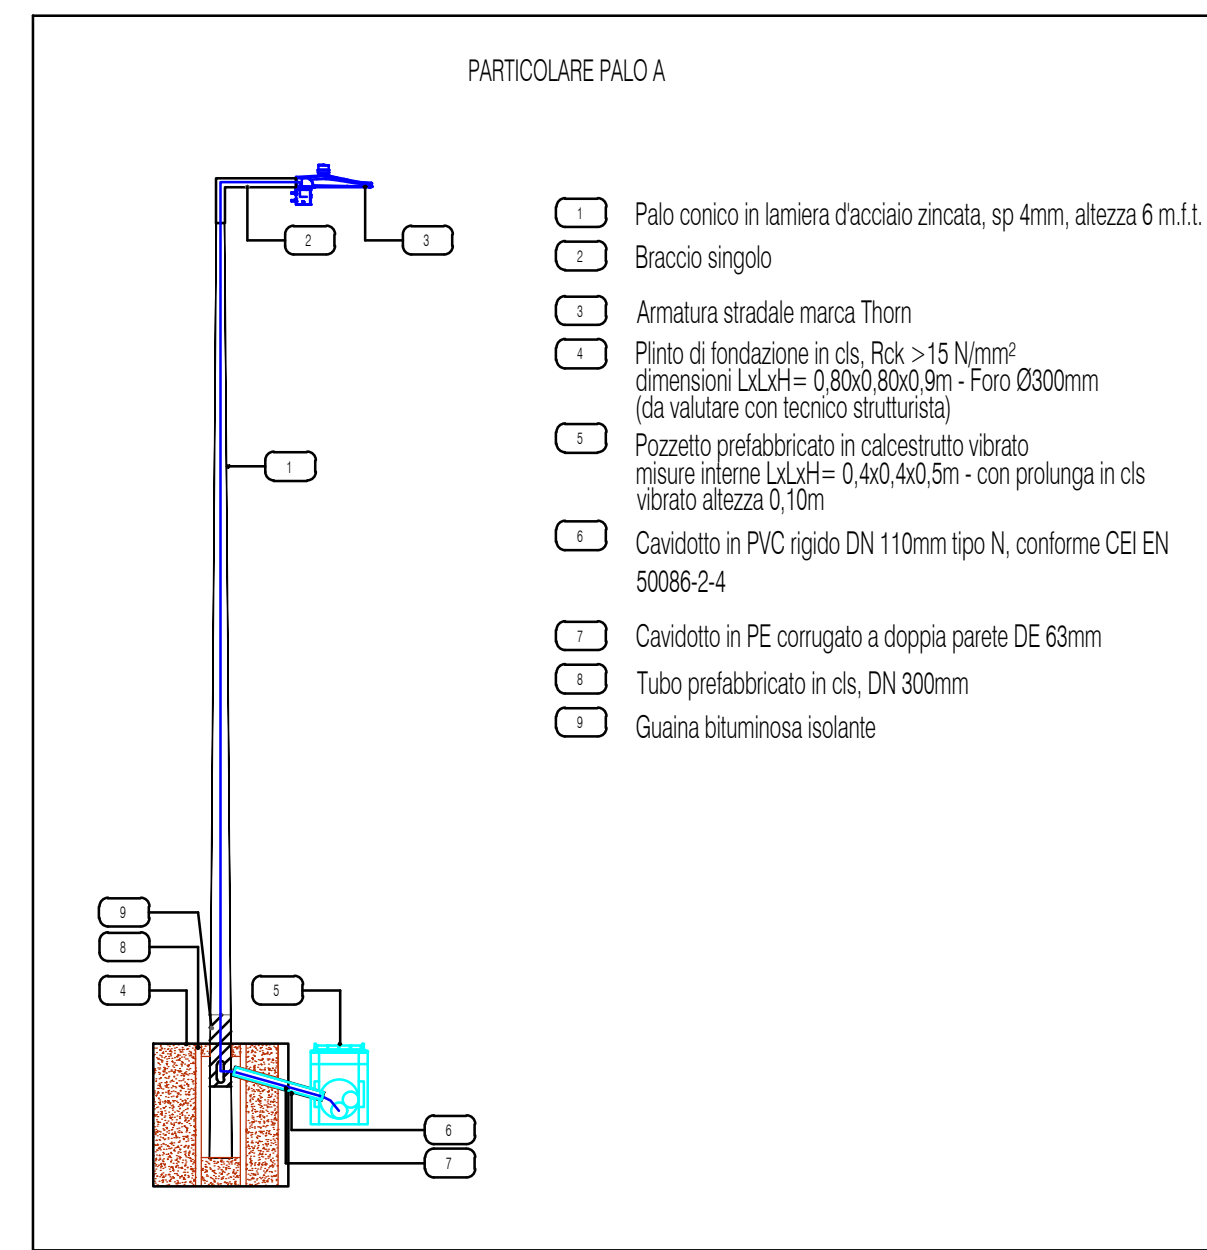


SCALA 1:200

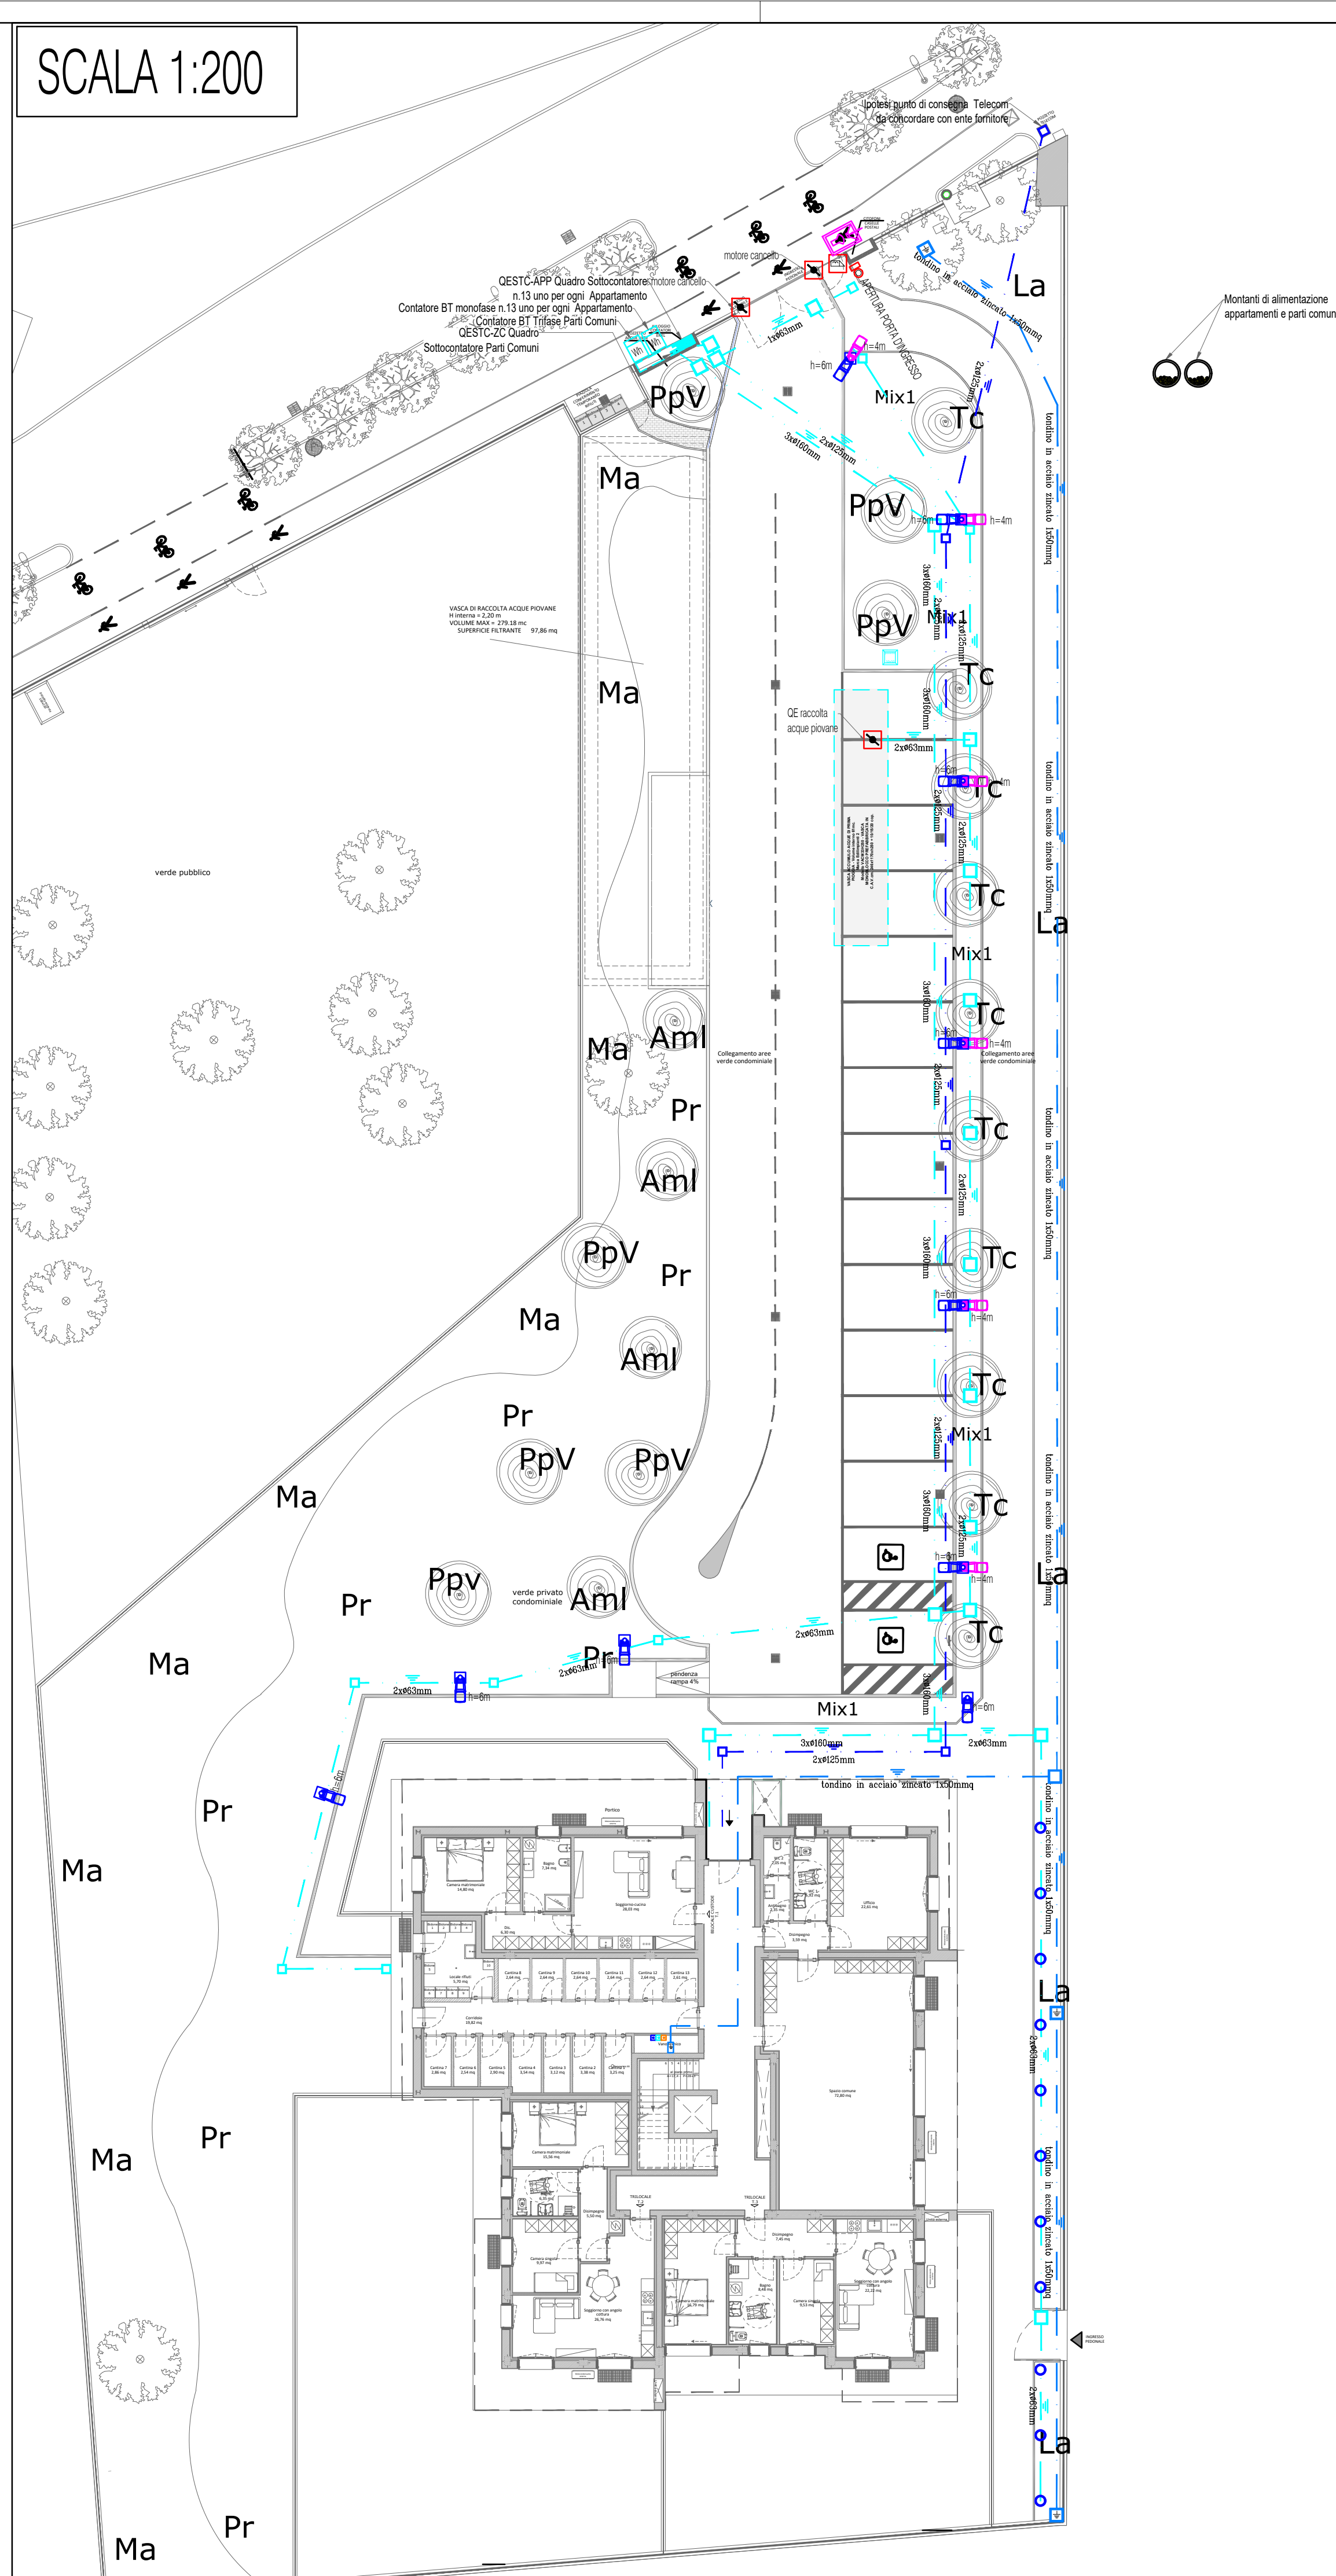

Il presente elaborato ha validità solo per impianti

SIMBOLI VARI					
	CONDIZIONE INTEL DIDOGIA ATIMA		SCAROLA NORMALITÀ PER PARETI NORMALI		TUBAZIONE ESTERNA
	POZZETTO		SCAROLA PORTABRILLO PER PARETI REI		TUBAZIONE INCASSATA
	QUADRO		SCAROLA DI DERIVAZIONE		TUBAZIONE INTERPIA
	SALITA		CALATA		MONDANTE
	CARBOTTETTO ENERGIA CON INDICAZIONE DEL DIAMETRO		CARBOTTETTO SPECIALI CON INDICAZIONE DEL DIAMETRO		

LEGENDE: IMPIANTO DI TERRA			
	POZZETTO CON PUNTAZZA DI TERRA		NODO EQUIPOTENZIALE
	PUNTAZZA DI TERRA		PUNTO EQUIPOTENZIALE
	TENDINO IN ACCORDO ZINCATO 50mmq		CONNETTORE EQUIPOTENZIALE
			COLLEGAMENTO ALLA RETE INALAMBA

LEGENDE: IMPIANTO DI ILLUMINAZIONE			
	ARMATURA SINGOLA TIPO TUBO LINEAR LIGHTING (CRO) PRO 180 283x106 18,7W O EQUIVALENTE		PIANTO E PAILO 14m
	ARMATURA SINGOLA TIPO TUBO LINEAR LIGHTING (CRO) PRO 180 283x106 18,7W O EQUIVALENTE		PIANTO E PAILO 16m
			LAMPIONINO ESTERNO

LEGENDE: IMPIANTO DI FORZA MOTRICE			
	PRESA UNIVERSALE		PRESA 12/18A
	PULSANTE		INTERFACCIA BIFASICA
			ALLACCIAMENTO GENERICO
			ALLACCIAMENTO ELETTRICISTRUZZURA (CONTROLO ACCESS)

LEGENDE: IMPIANTO AUSILIARE					
	PRESA TRASMISSIONE DATI		PRESA TV		ANTENNA SAT
	VIDEOCITOFONO		SUONERIA		PONDERATORE
	PULSANTE PER CAMPANELLO APPARTAMENTO		PULSANTE DI SELEZIONE CHIAMATA VOCE		ANTENNA TV

[illegible]