

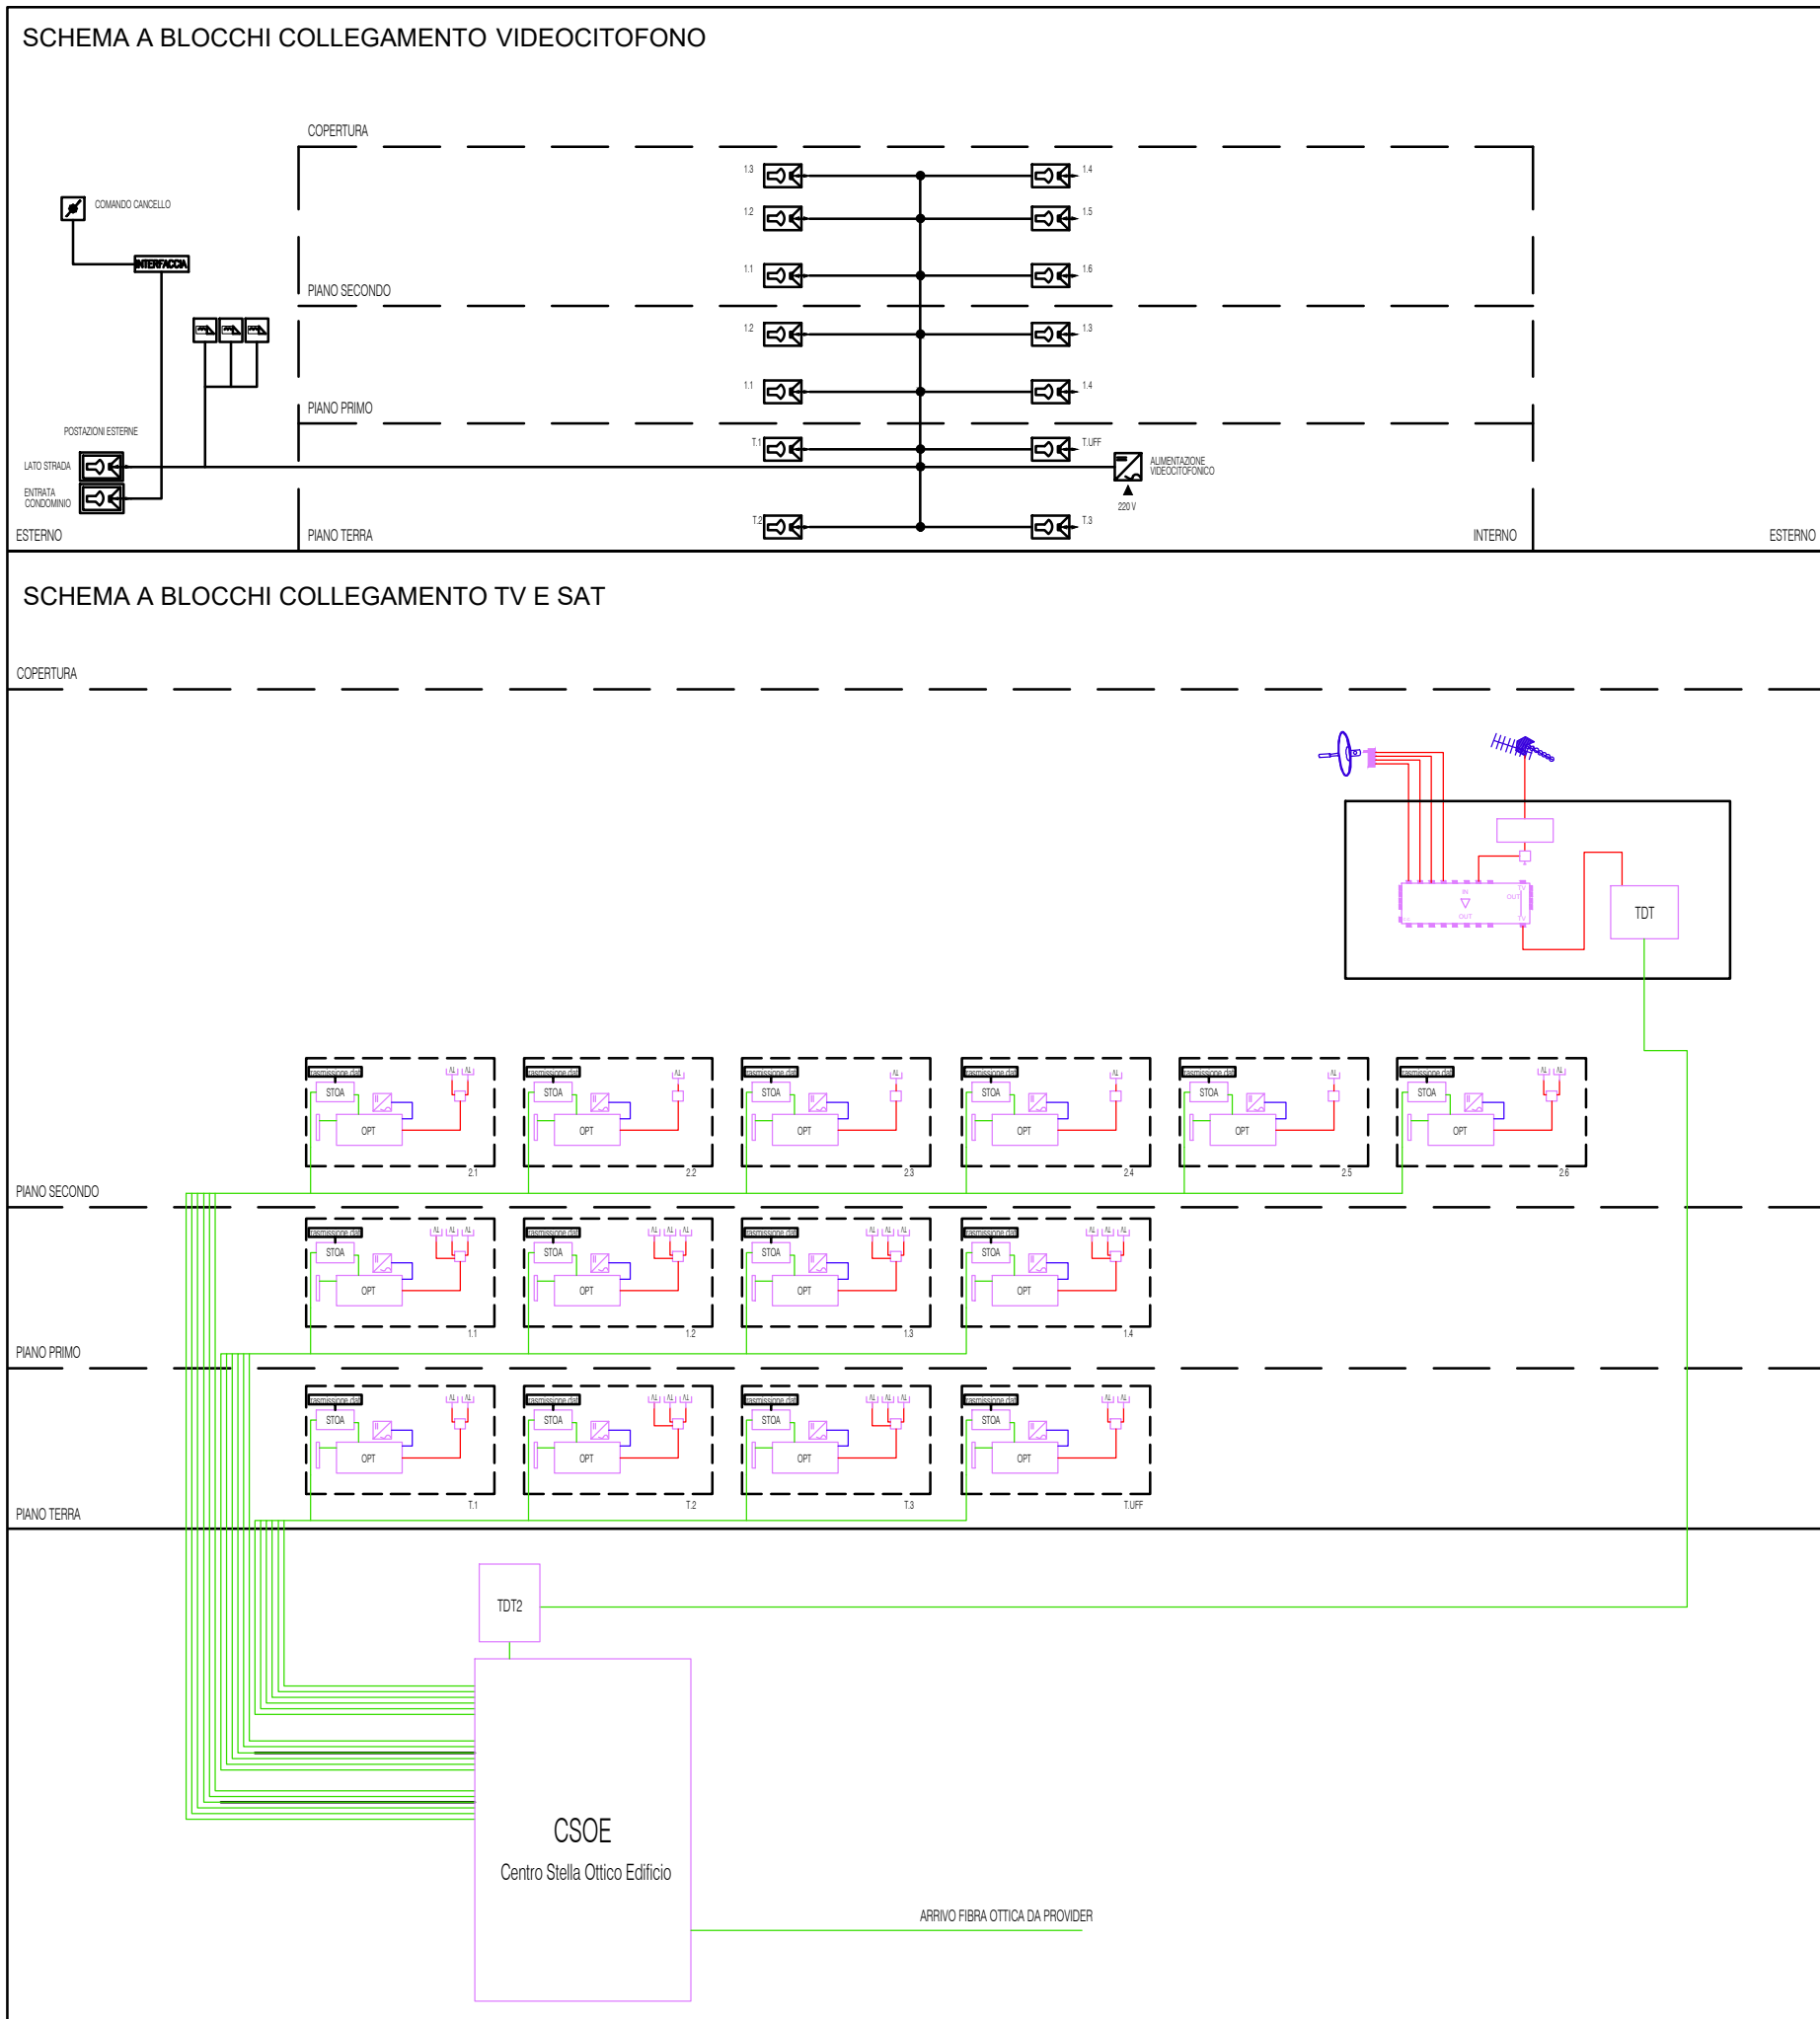
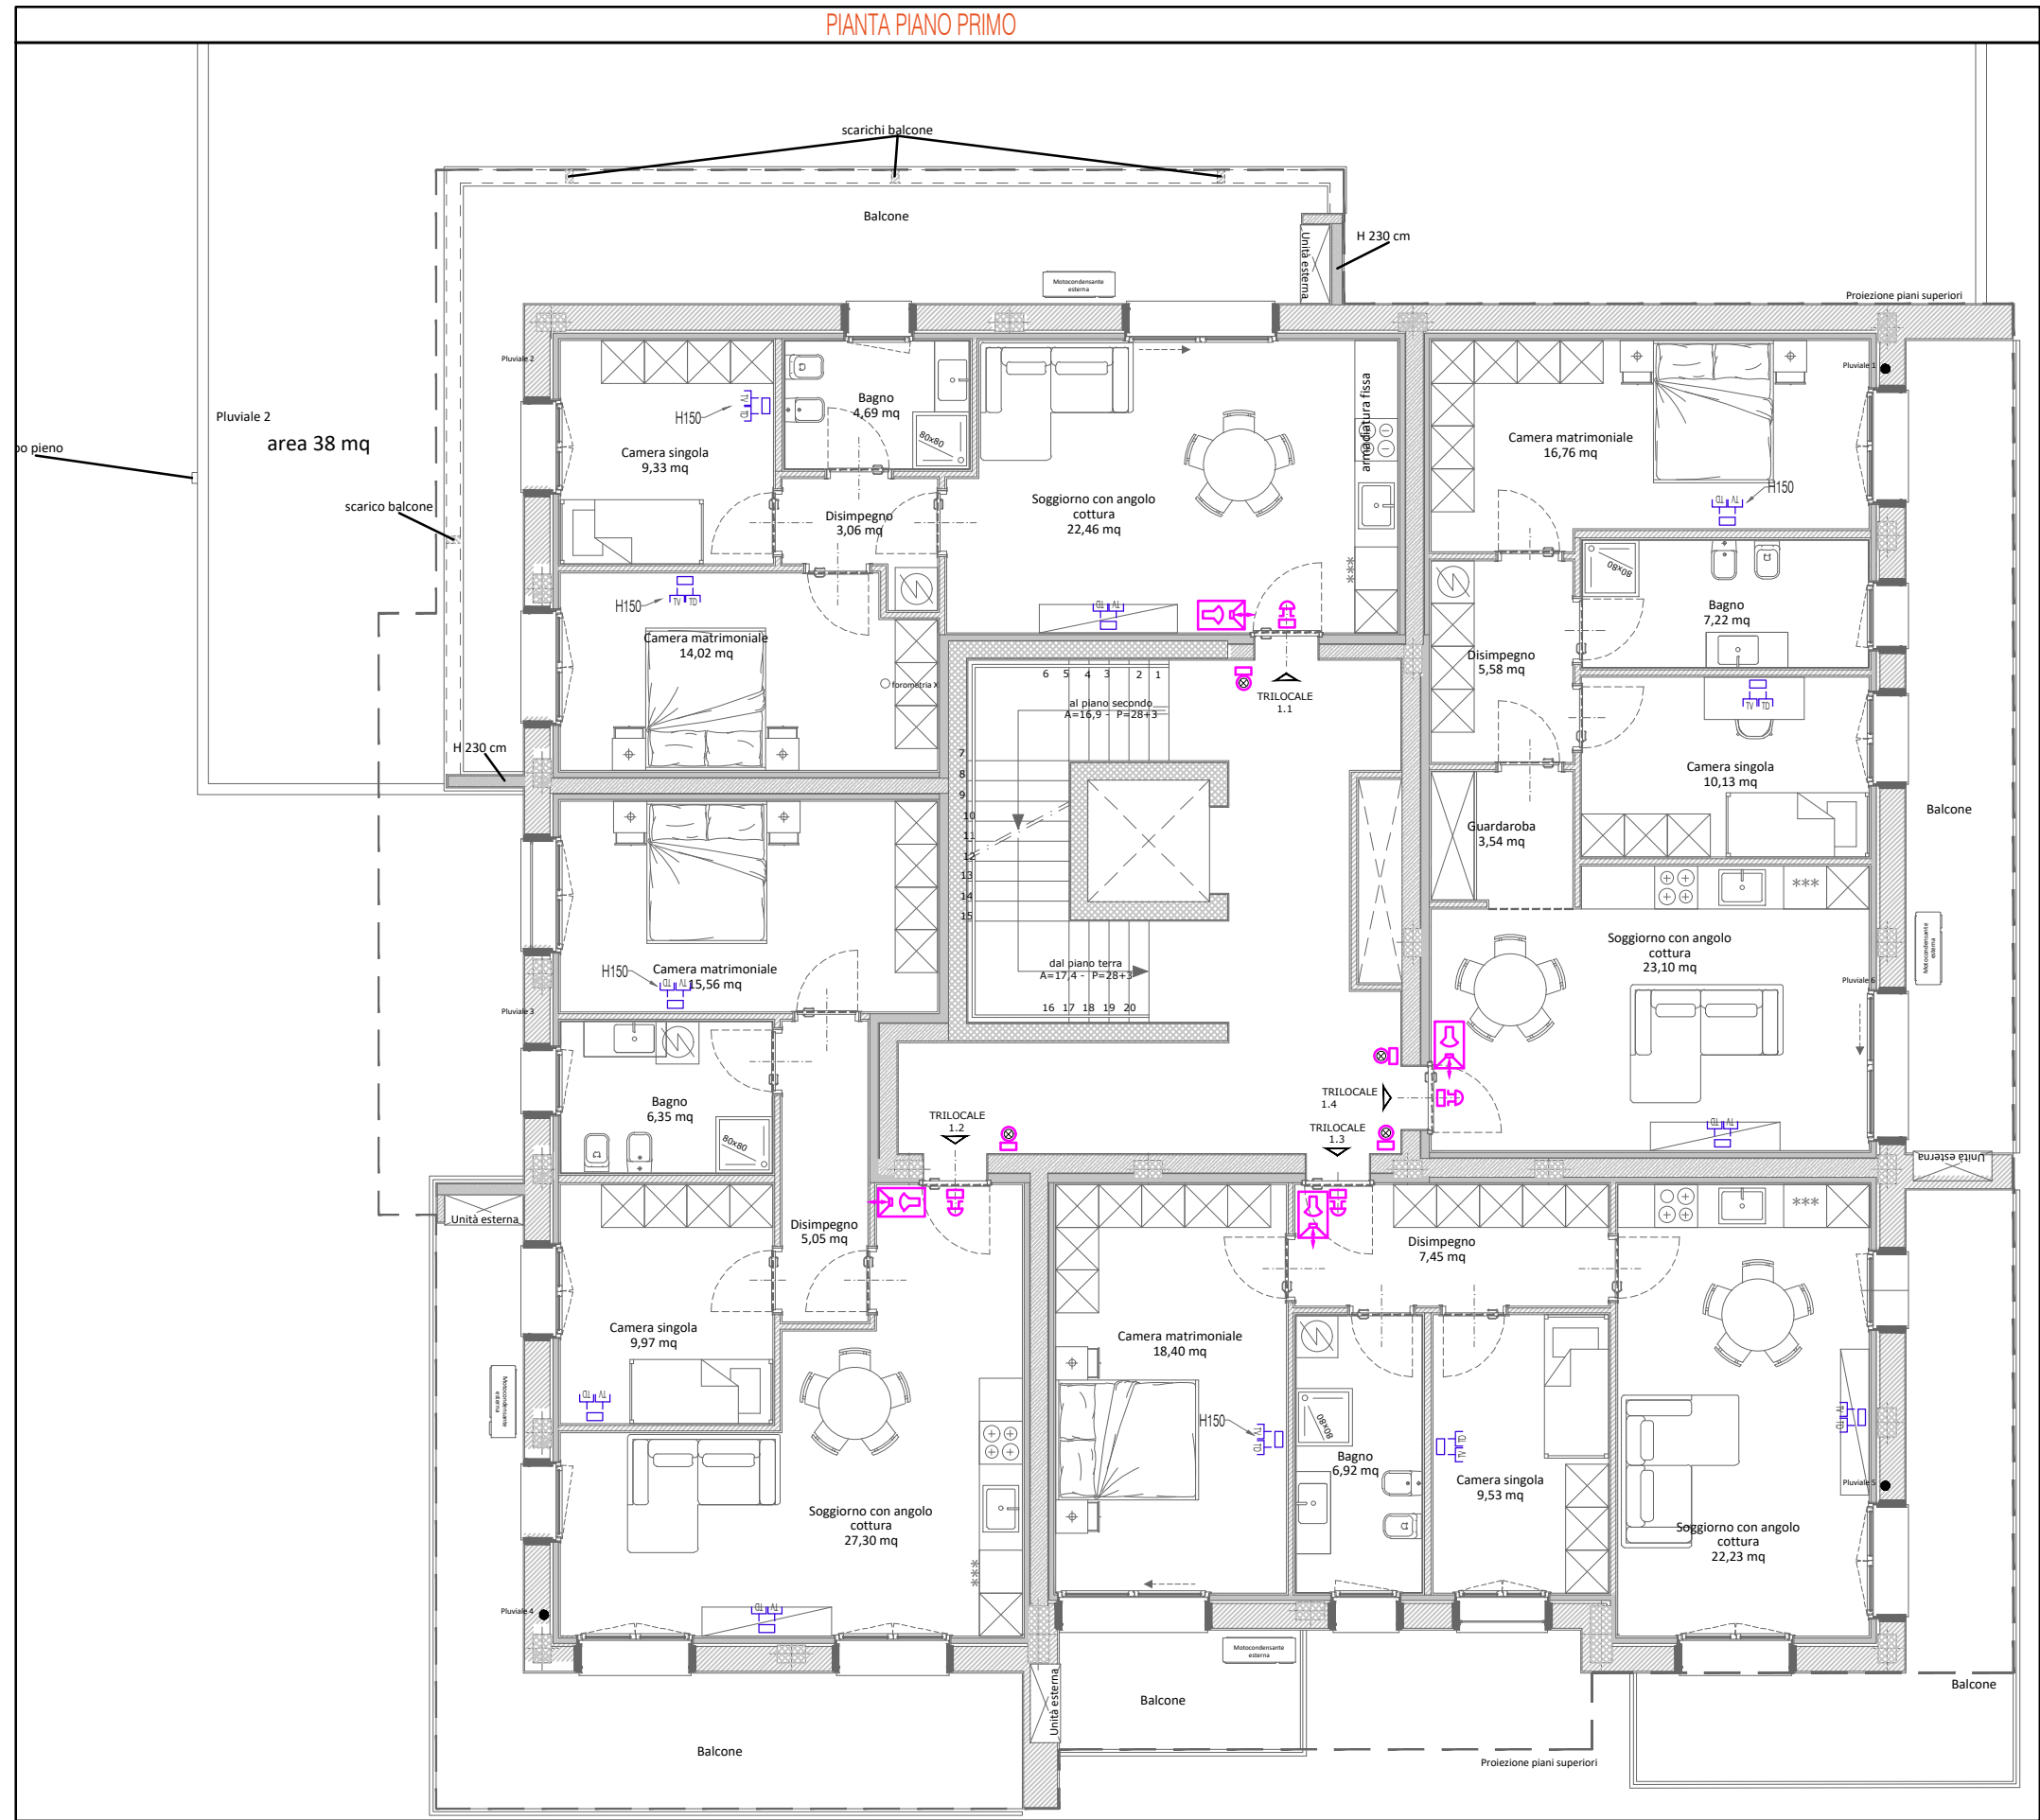
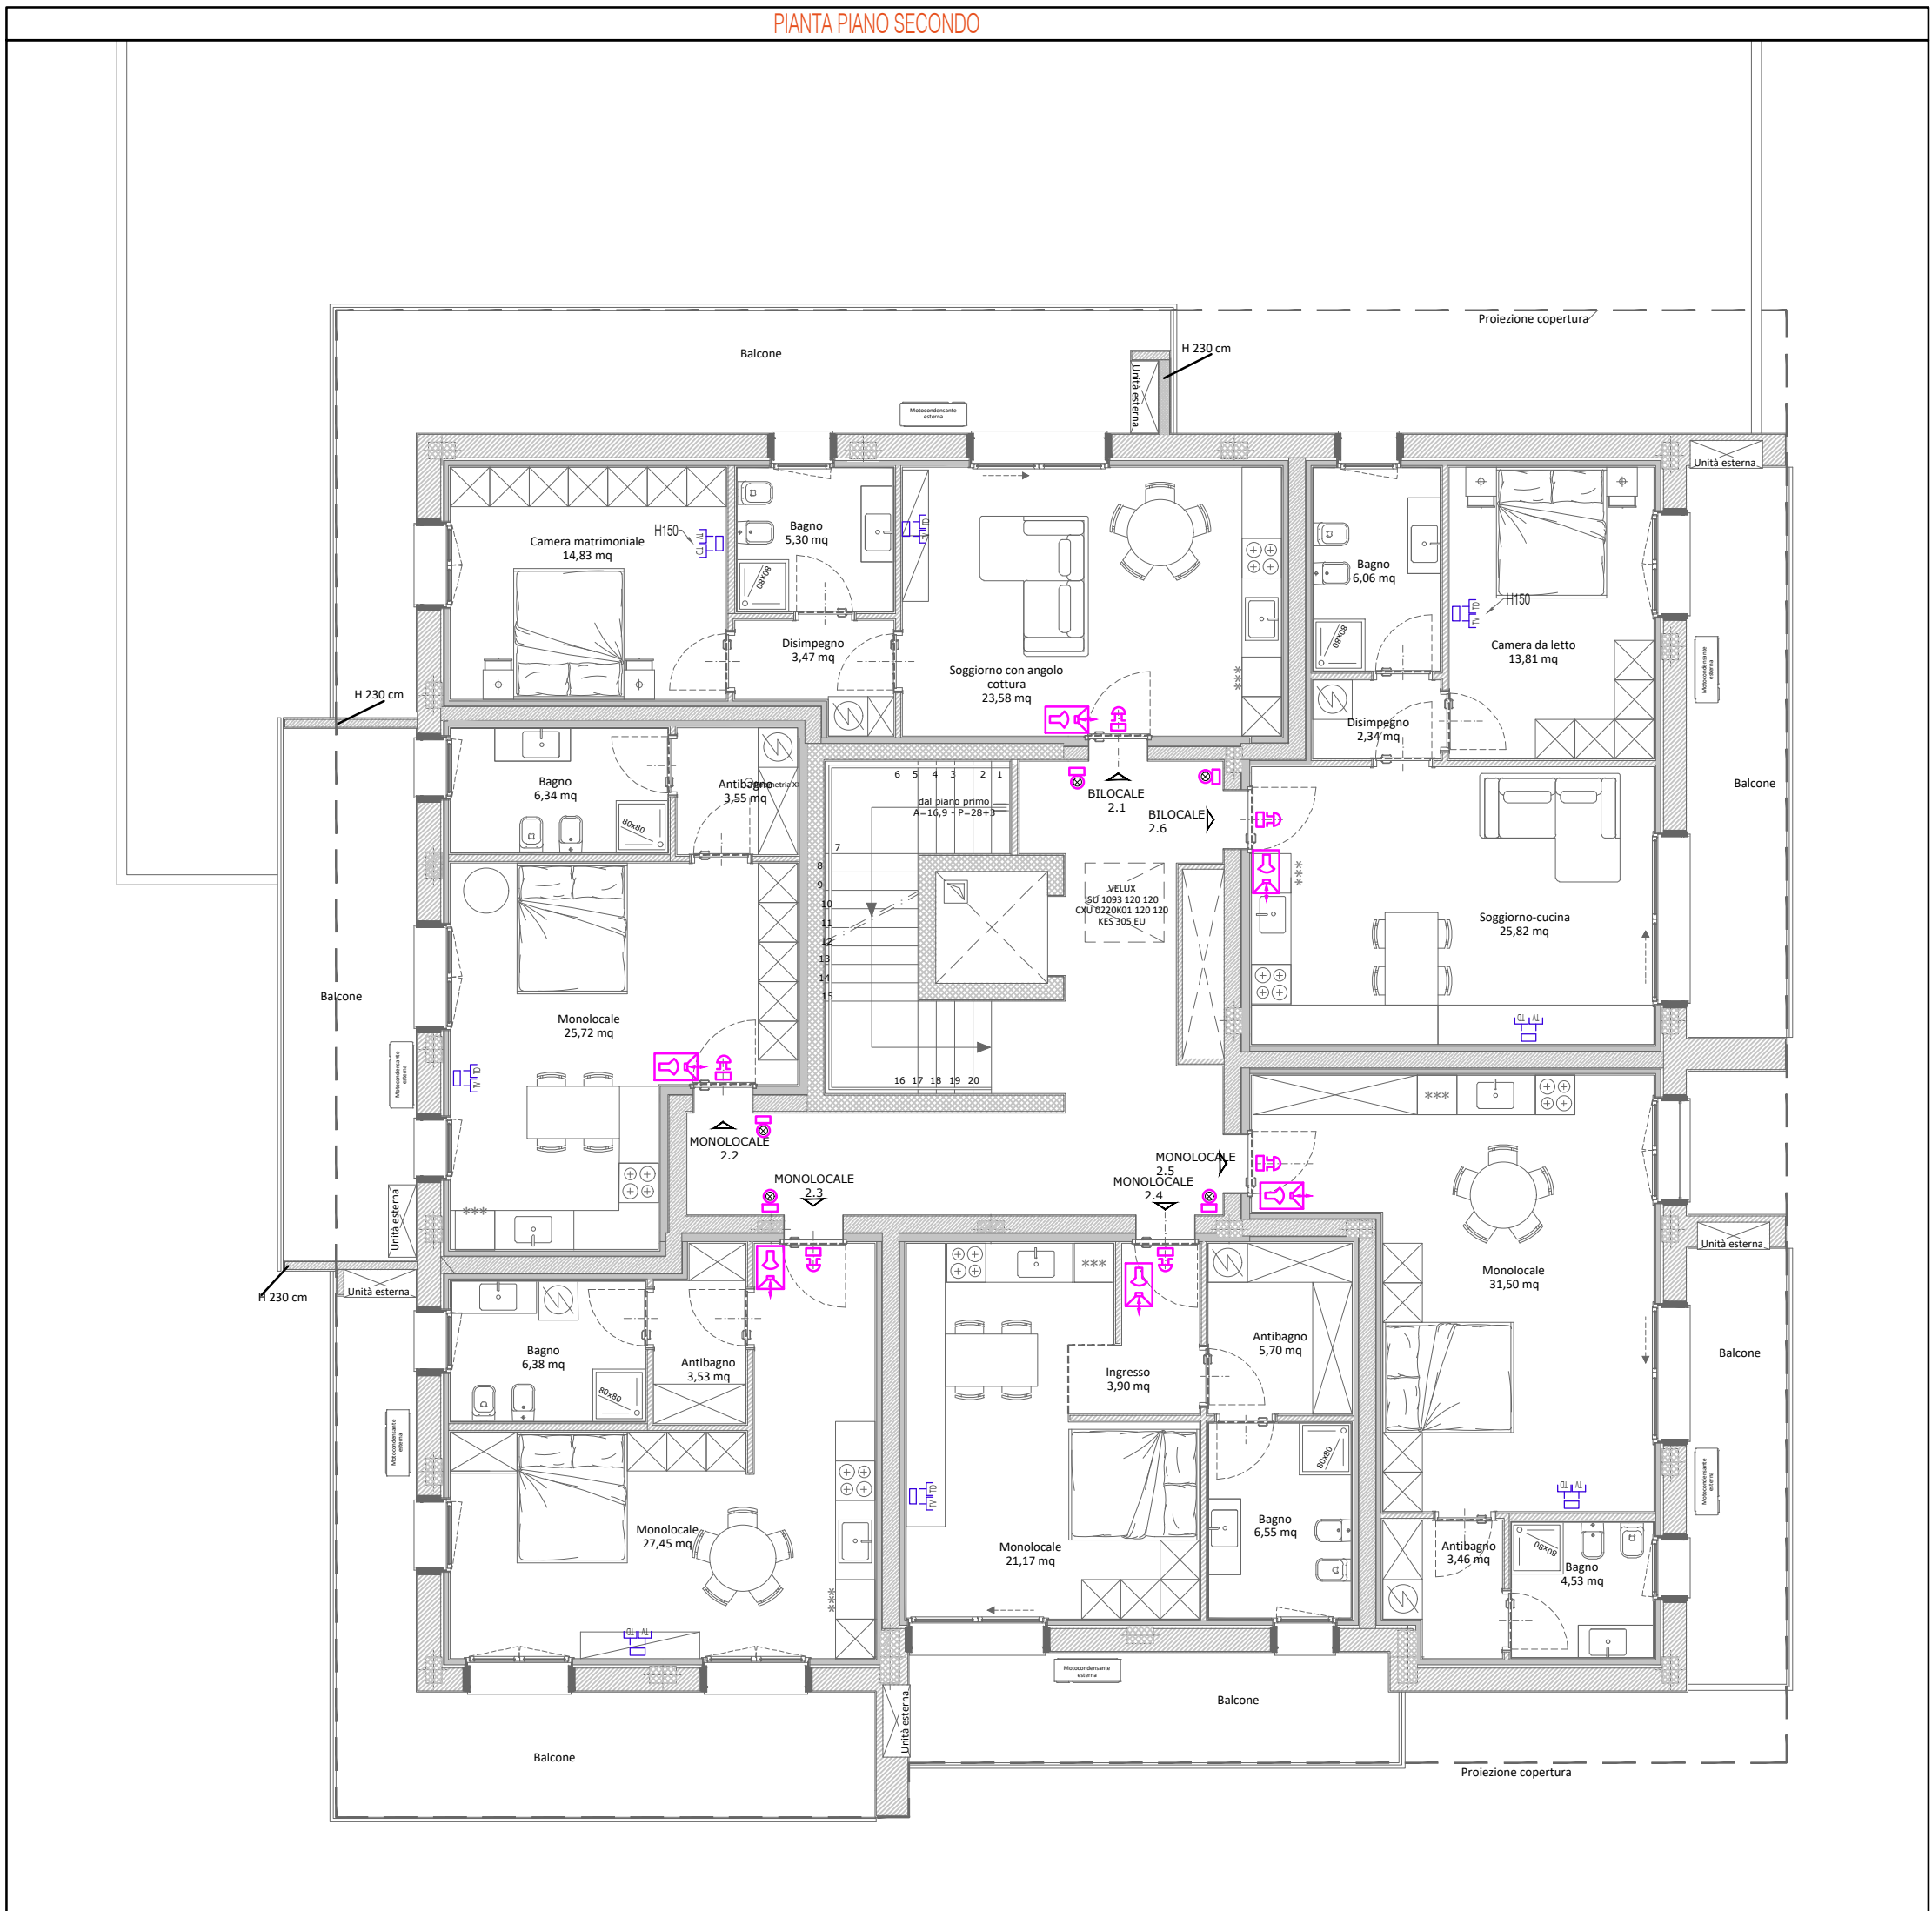


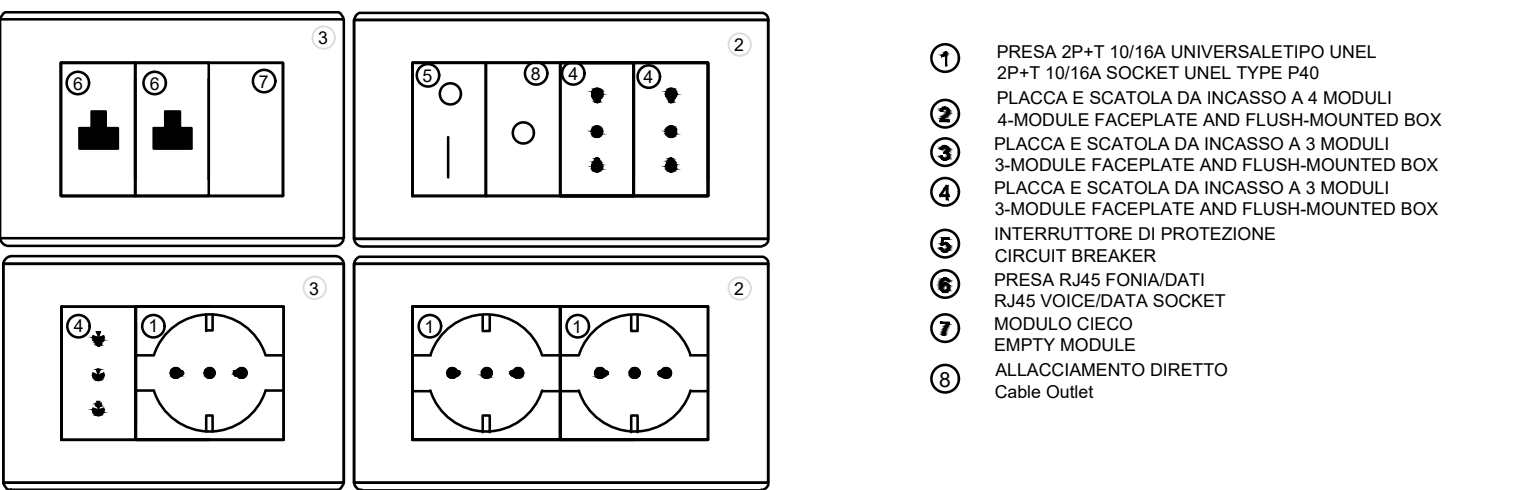

LEGENDE: IMPIANTO AUSILIARE

	PRESA TRASMISSIONE DATI		PRESA TV		ANTENNA SAT
	VIDEOCITOFONO		SUCKERIA		FORNITORE
	PULSANTE PER CAMPANELLO APPARTAMENTO		PULSANTE DI TACITAZIONE CHIAMATA ERM		ANTENNA TV

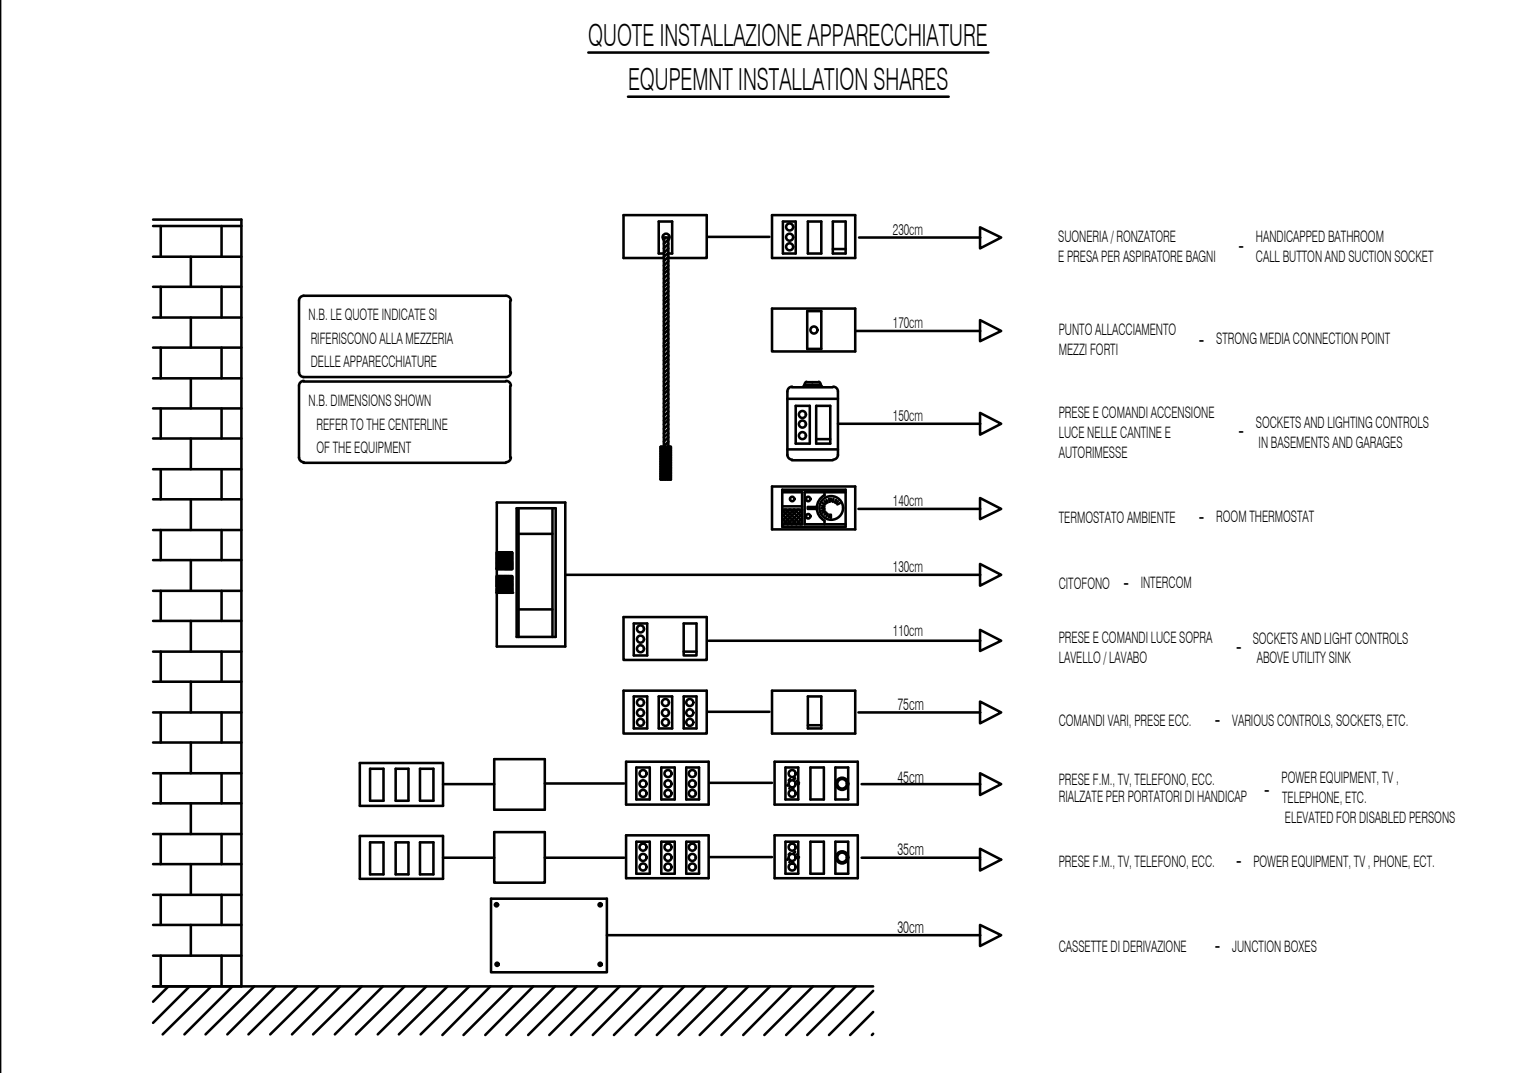

Progetto impianti

COMUNE DI COLOGNO MONZESE (MI)
AREA Ex TORRIANI ARAS 01
PROGETTO ESECUTIVO
Progetto Servizi Abitativi Pubblici di via Pergolesi

N° DATA DESCRIZIONE MOTIVAZIONE DELL'AGGIORNAMENTO STUDIO DIS.

00 16/01/2026 Prima emissione G.B.&P. L.M.

Progetto **PROGETTO ESECUTIVO**

Proponente **Officine Mak S.r.l.**
Corso Europa, 10
Milano 20122

Scala **1:100**

Data **23/01/2026**

Tipo tavola **IMPIANTI**

Serie **PROGETTO ESECUTIVO**

Titolo **IMPIANTI ELETTRICI - IMPIANTI SPECIALI**

Tavola nr. **IMP**
Tipo Tavola **ES**
Sigla / Serie **01**
Numero / Variante **00**

Orientamento

Documento di proprietà della Società G.B. & Partners S.r.l.. E' vietata la riproduzione. Tutti i diritti sono riservati.