
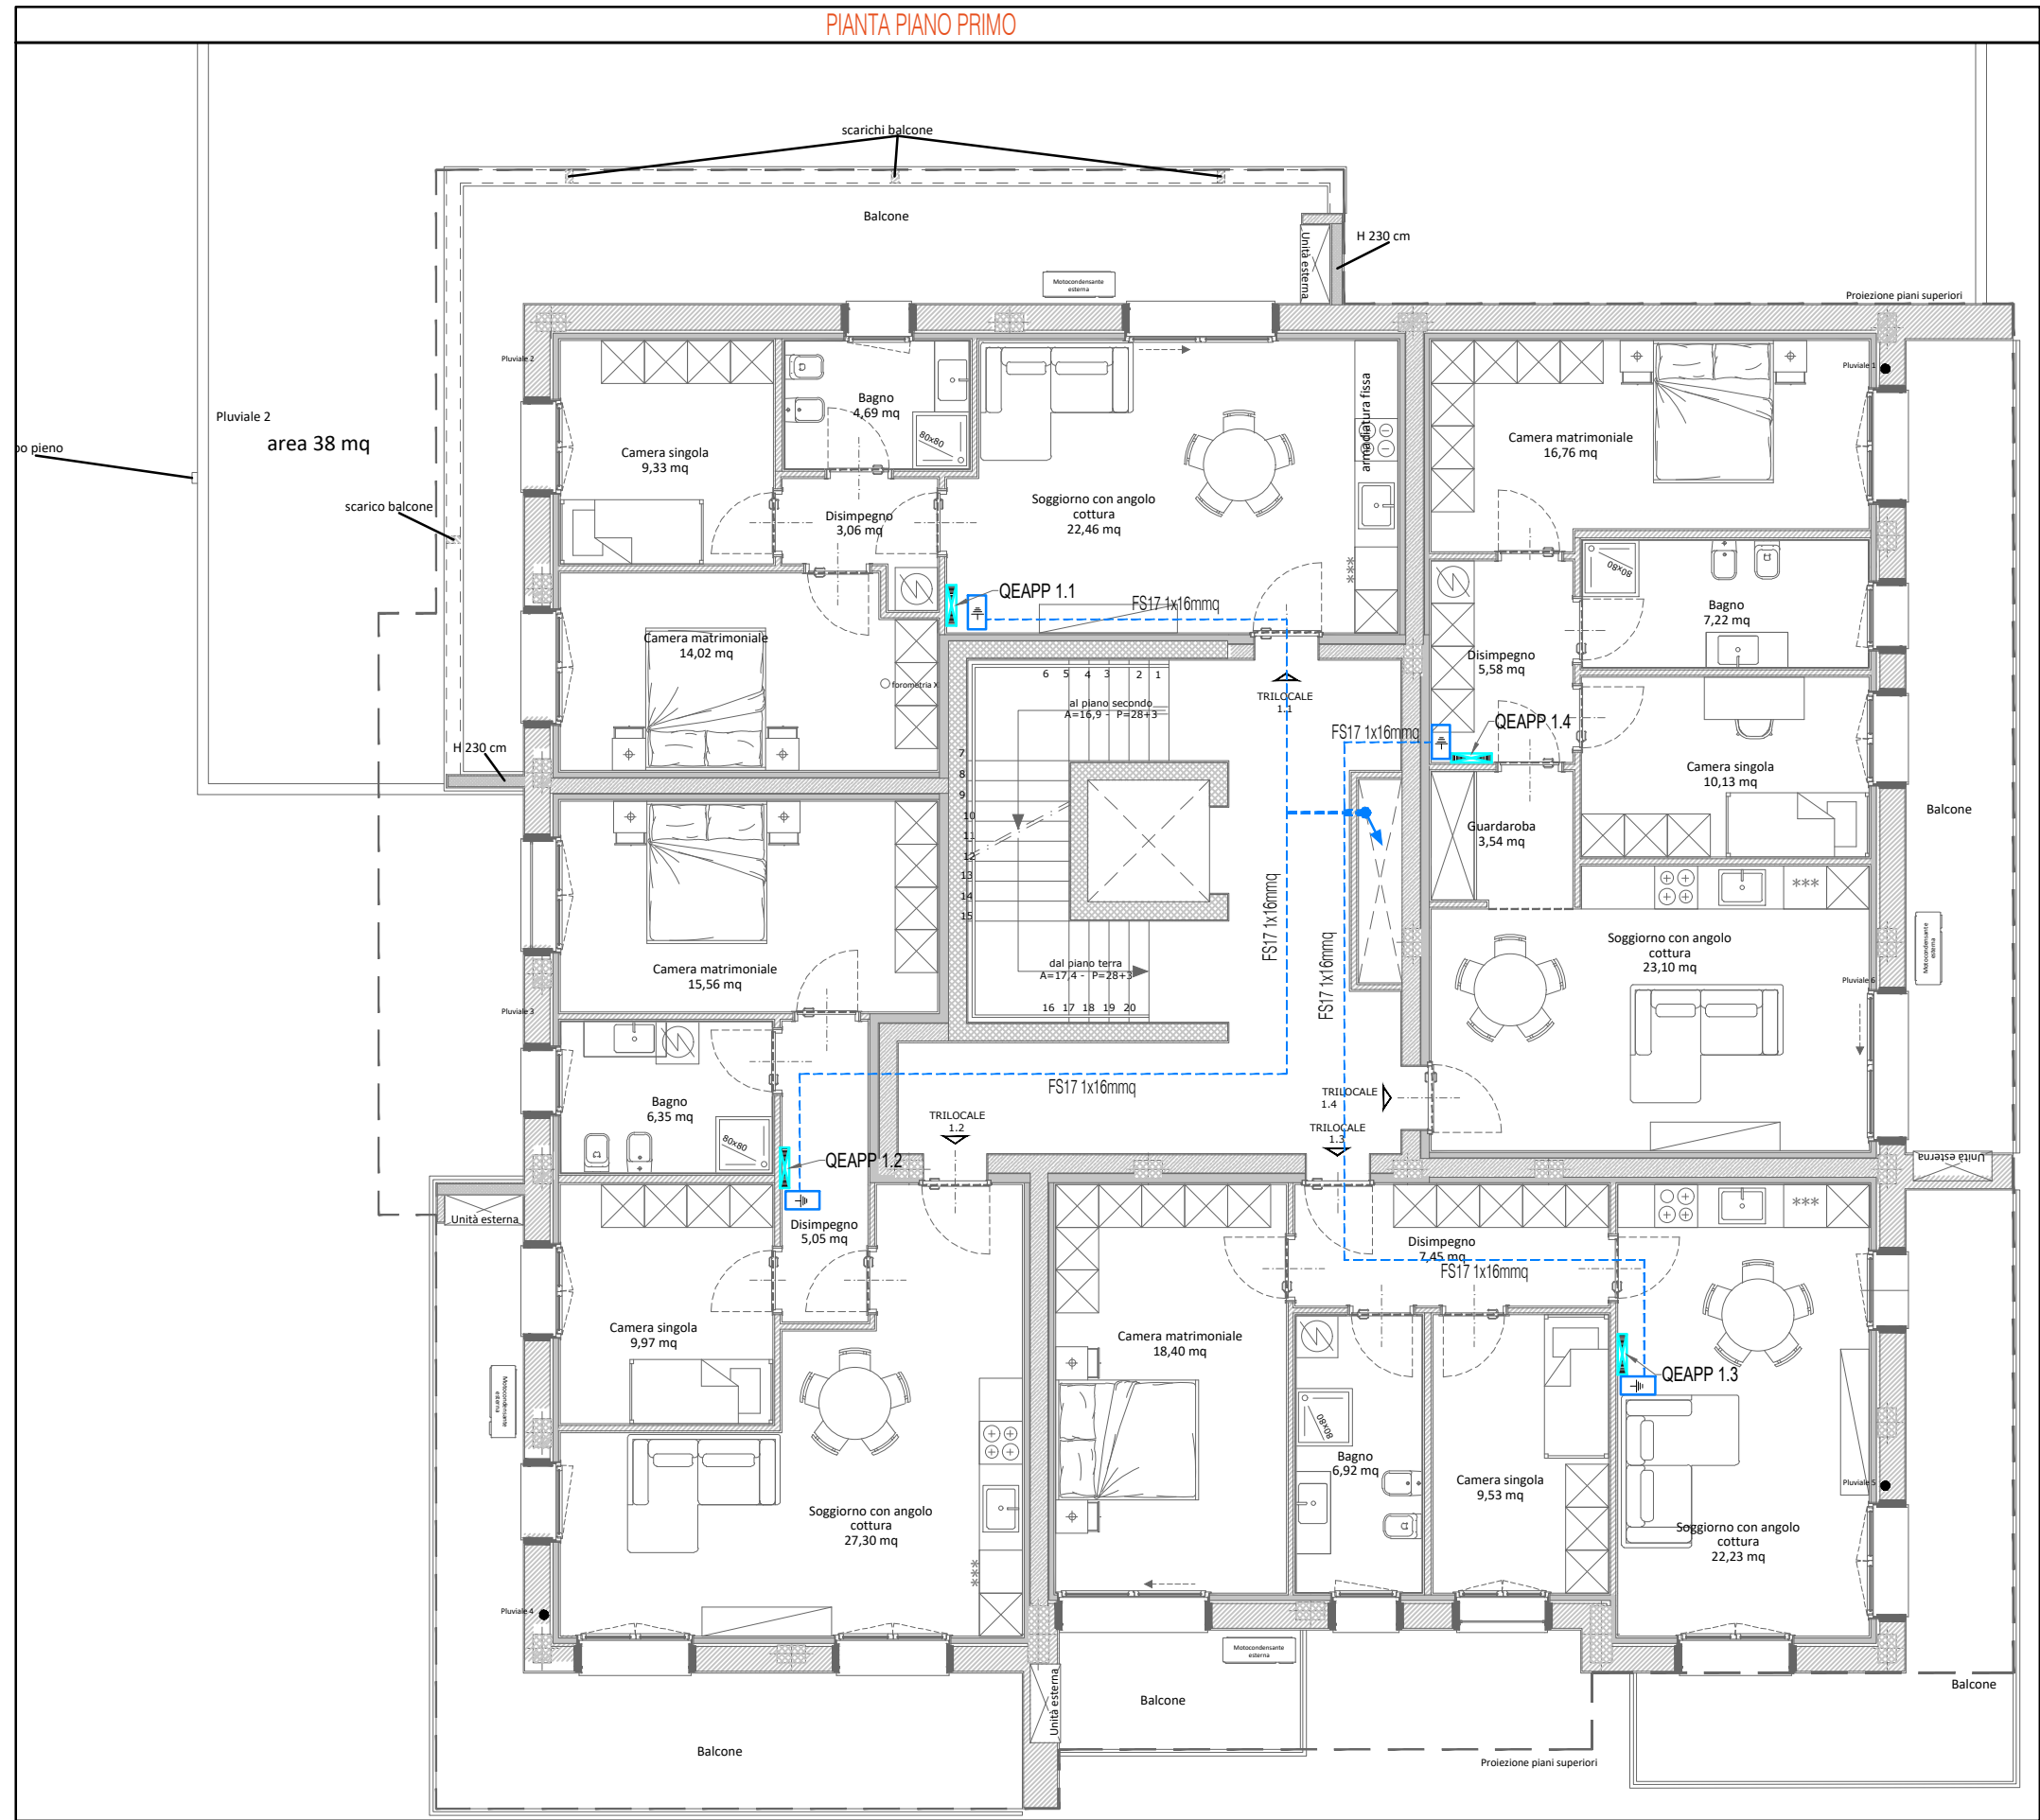
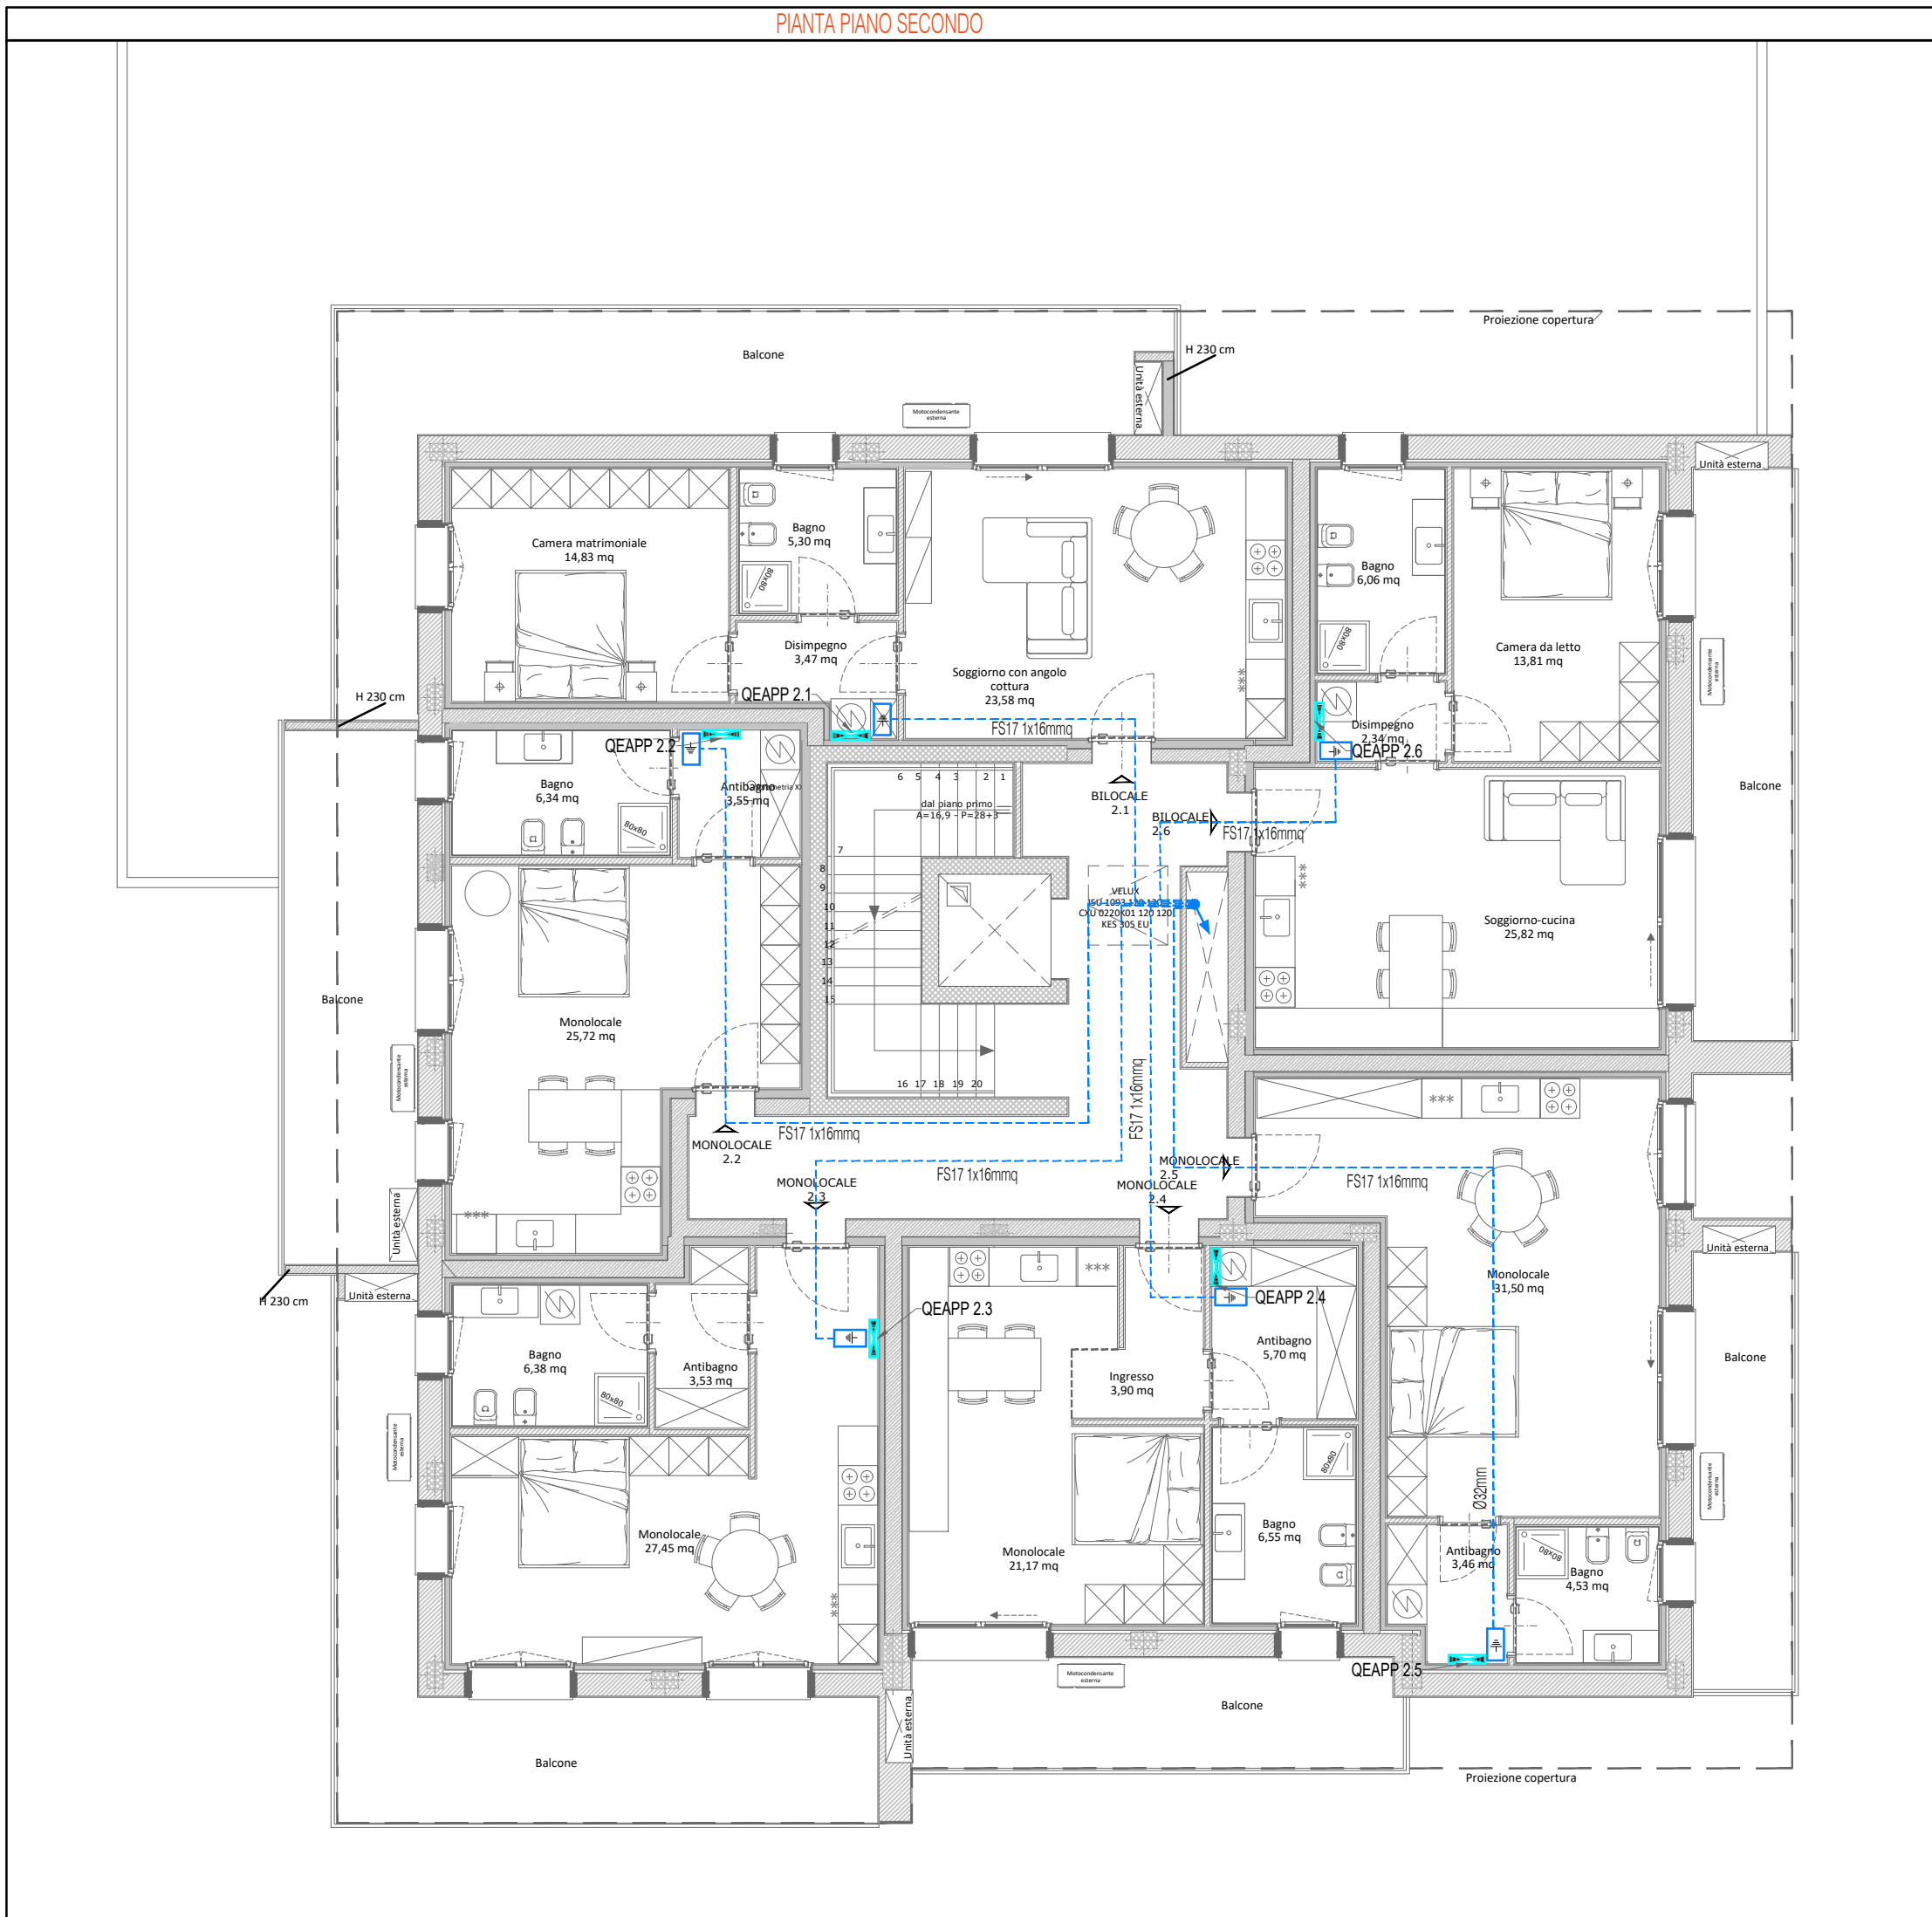


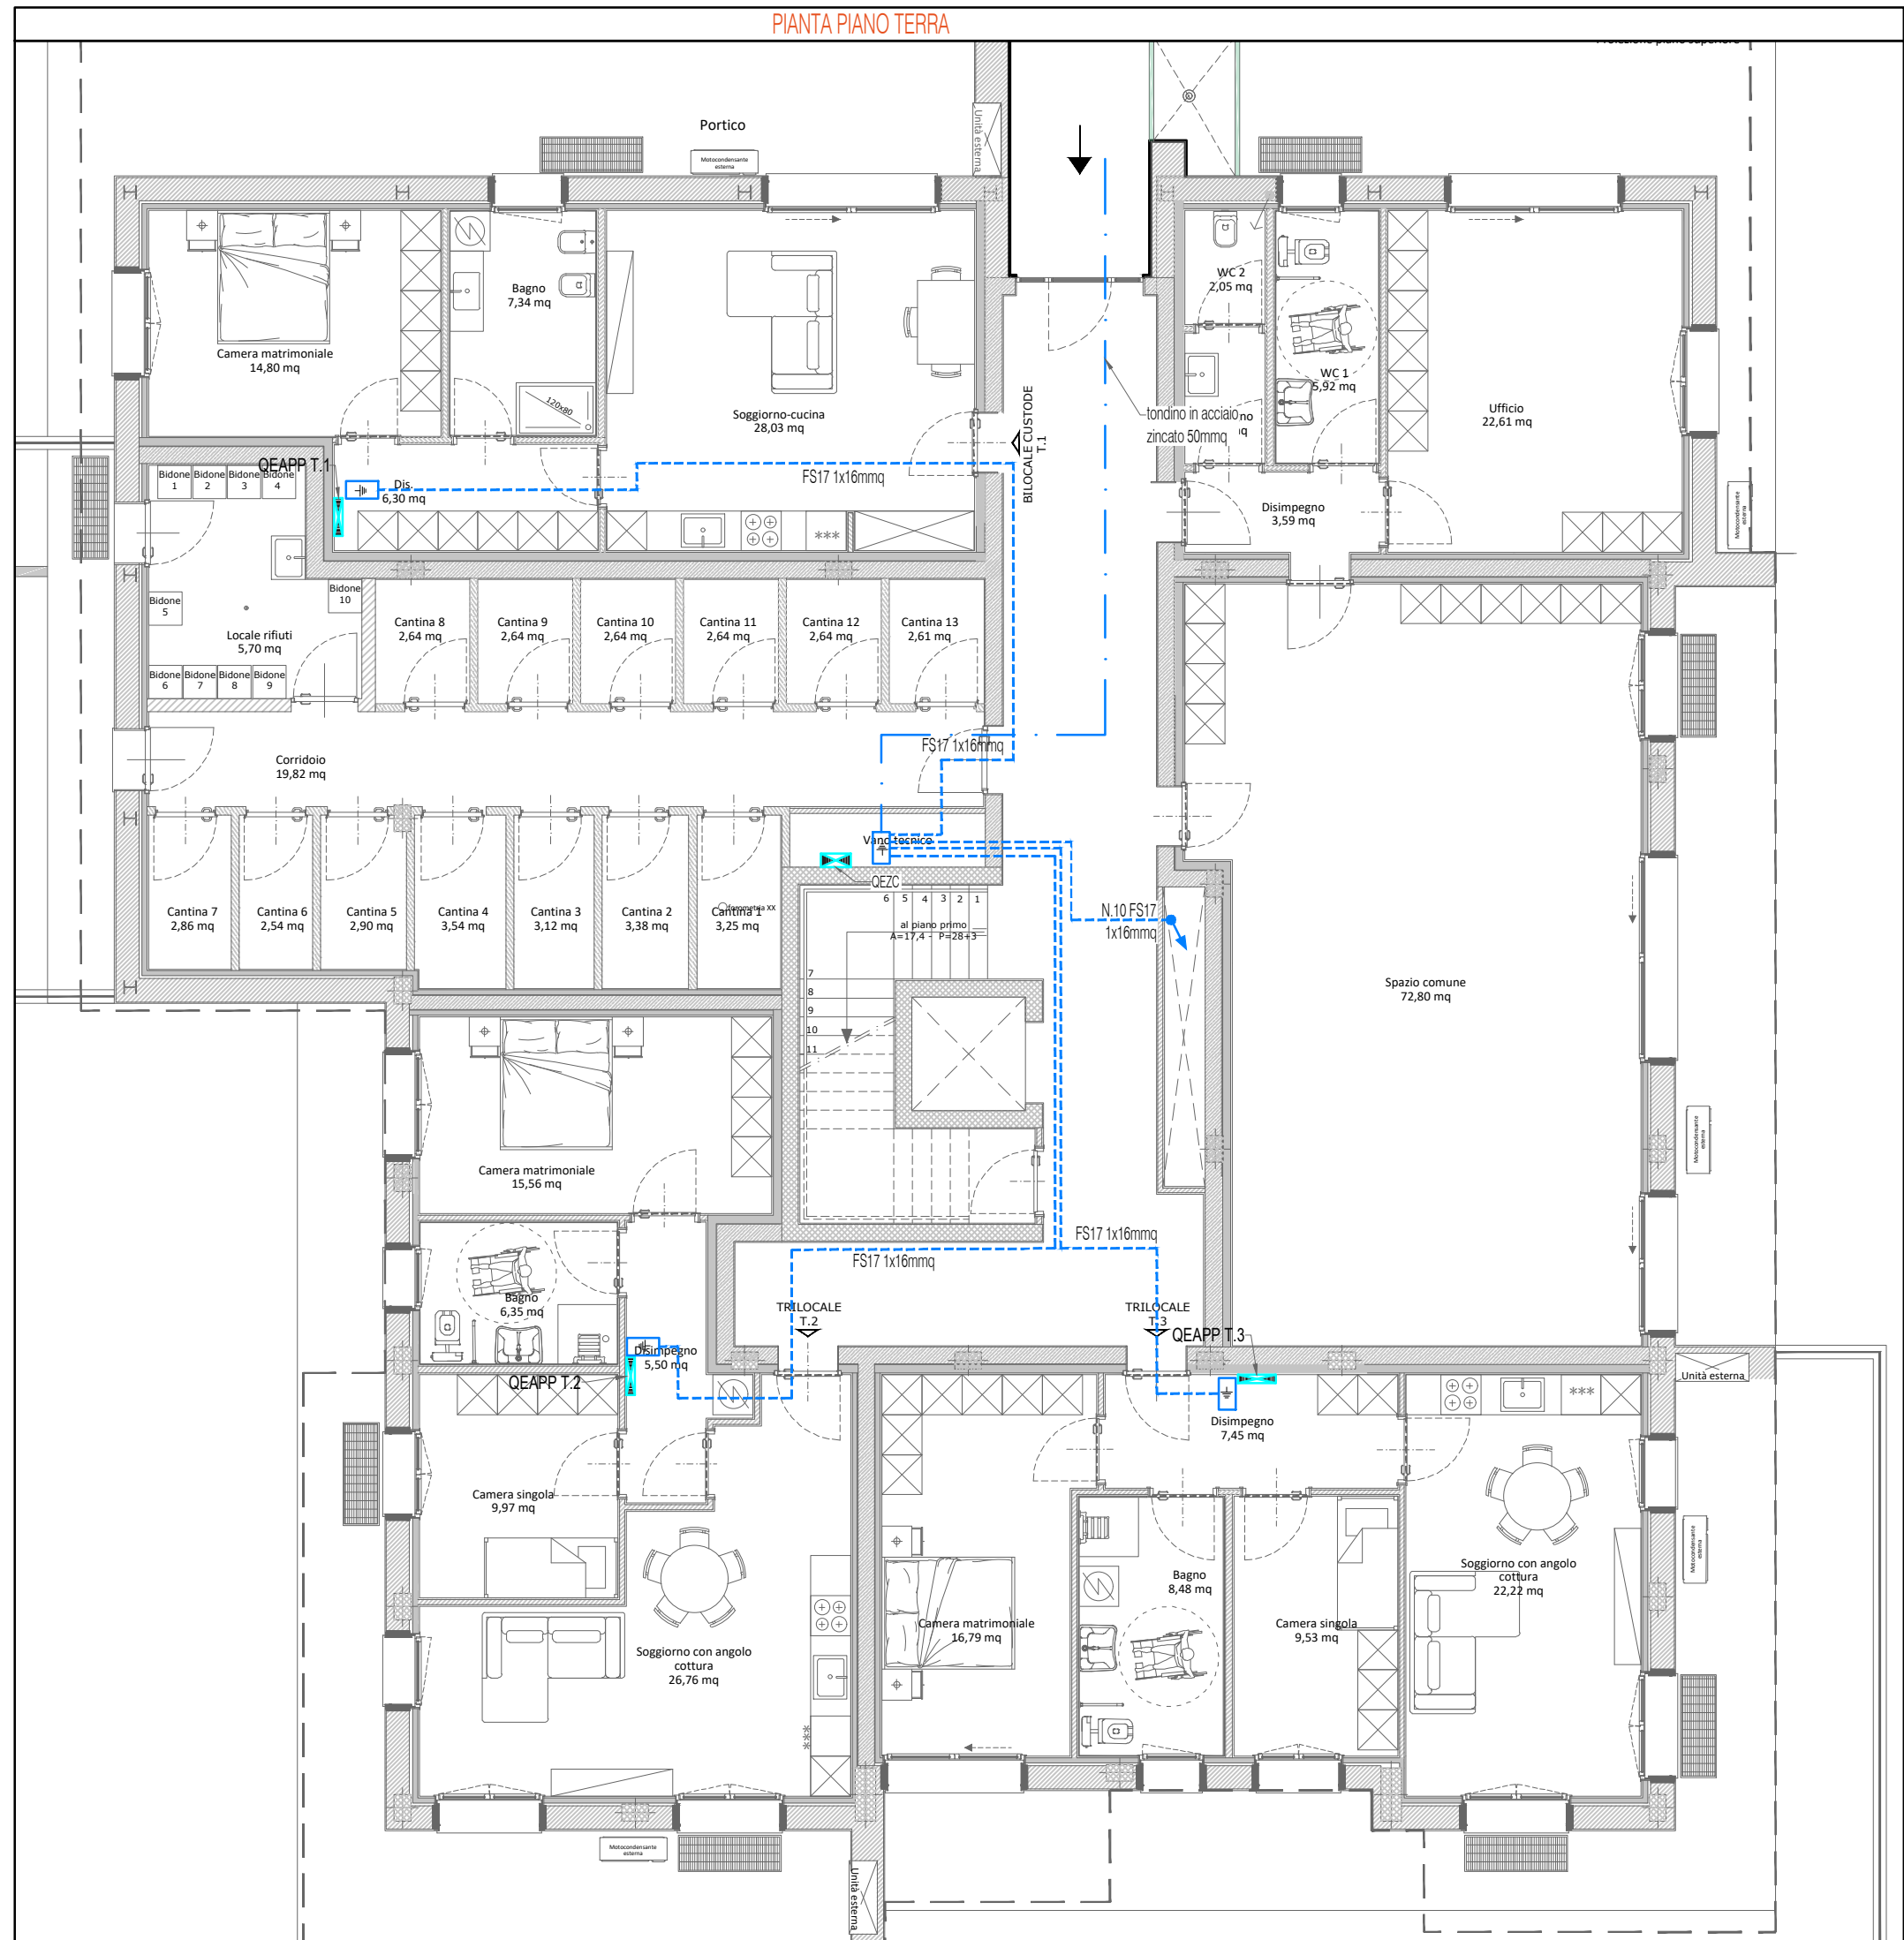


LEGENDE: IMPIANTO DI TERRA

|  |                                                  |  |                                                      |  |                              |
|--|--------------------------------------------------|--|------------------------------------------------------|--|------------------------------|
|  | DISPENSORE DI TERRA GRIZZ<br>IN TONDO Acci 50mmq |  | CONDUTTORE DI PROTEZIONE<br>IN TUBAZIONE CORR. Ø32mm |  | NODO EQUIPOTENZIALE          |
|  | POZZETTO CON<br>PUNTAZZA DI TERRA                |  | PUNTO EQUIPOTENZIALE                                 |  | CONNETTORE<br>EQUIPOTENZIALE |

SIMBOLI VARI

|  |          |  |                                           |  |                     |
|--|----------|--|-------------------------------------------|--|---------------------|
|  | QUADRO   |  | SCATOLA PORTAFRUTTI<br>PER PARETI NORMALI |  | TUBAZIONE ESTERNA   |
|  | MONTANTE |  | SCATOLA DI<br>DERIVAZIONE                 |  | TUBAZIONE INCASSATA |
|  | CALATA   |  | SALITA                                    |  | TUBAZIONE INTERRATA |

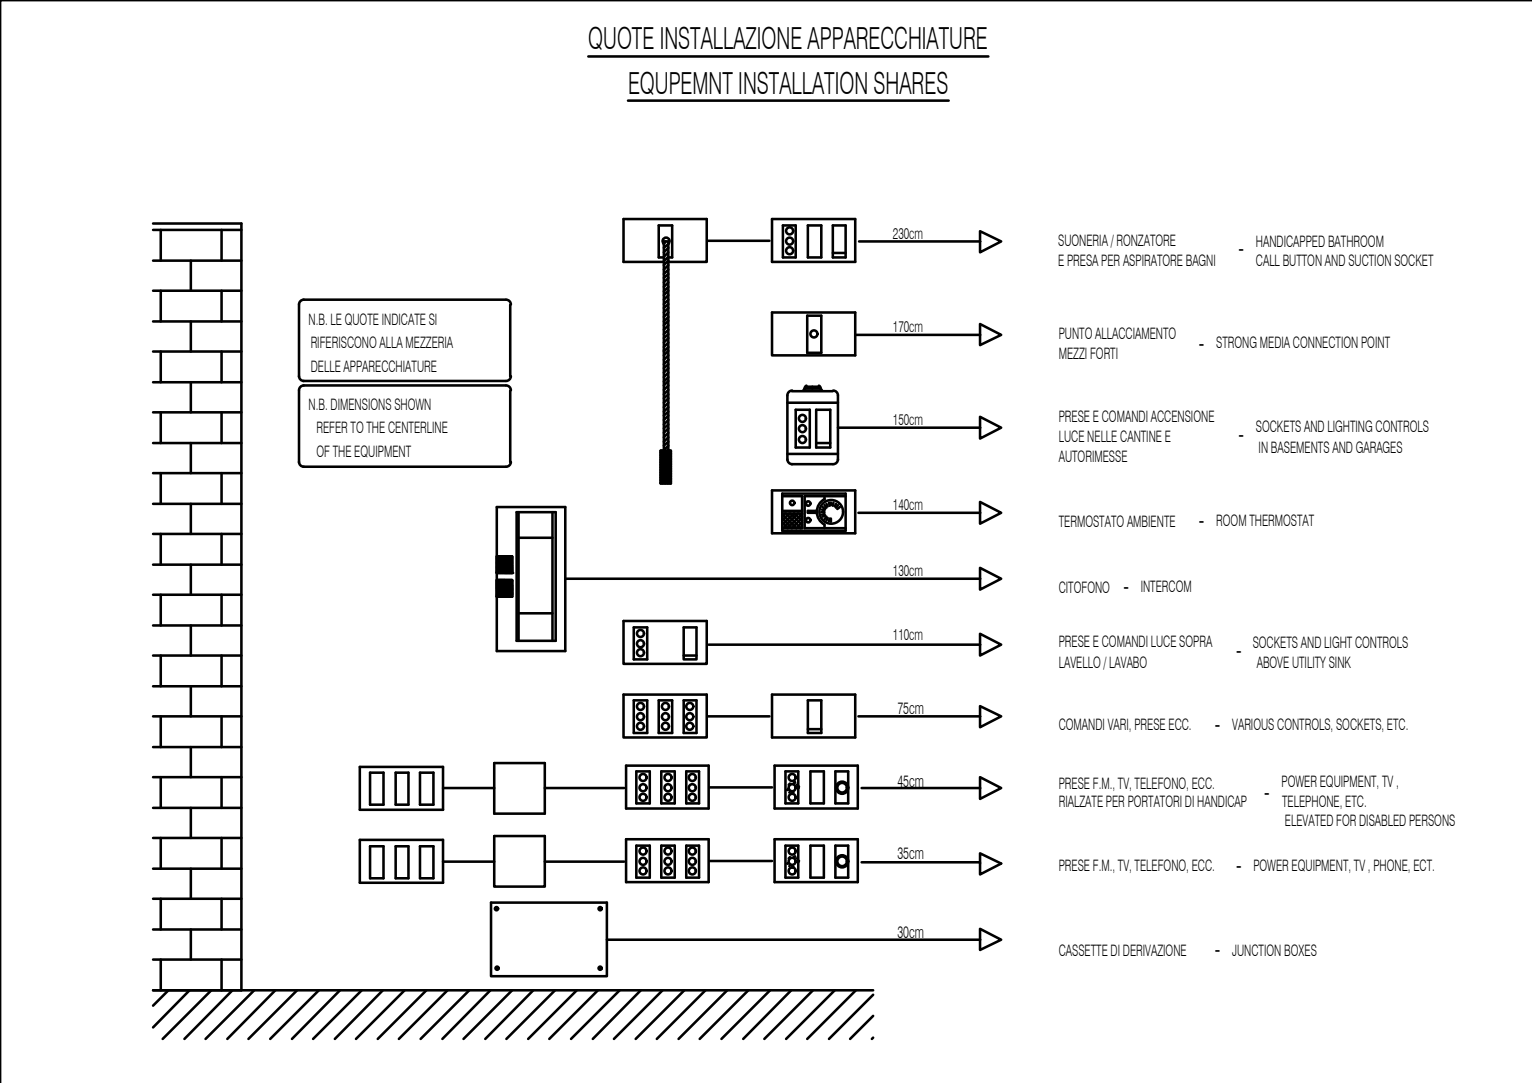

Progetto impianti

**COMUNE DI COLOGNO MONZESE (MI)**  
**AREA Ex TORRIANI ARAS 01**  
**PROGETTO ESECUTIVO**  
**Progetto Servizi Abitativi Pubblici di via Pergolesi**

N° DATA DESCRIZIONE MOTIVAZIONE DELL'AGGIORNAMENTO STUDIO DIS.

00 16/01/2026 Prima emissione G.B.&P. L.M.

Progetto **PROGETTO ESECUTIVO** Servizi Abitativi Pubblici Comune di Cologno Monzese(MI)

Proponente **Officine Mak S.r.l.** Corso Europa, 10 Milano 20122

Scala **1:100**

Data **23/01/2026**

Tipo tavola **IMPIANTI**

Serie **PROGETTO ESECUTIVO**

Titolo **IMPIANTI ELETTRICI - IMPIANTO DI TERRA ED EQUIPOTENZIALE**

Tavola nr. **IMP**

Tipo Tavola **ES**

Sigla / Serie **01**

Numero / Variante **00**

Agg. **00**

Orientamento

Documentazione di proprietà della Società G.B. & Partners S.r.l. E' vietata la riproduzione. Tutti i diritti sono riservati.