
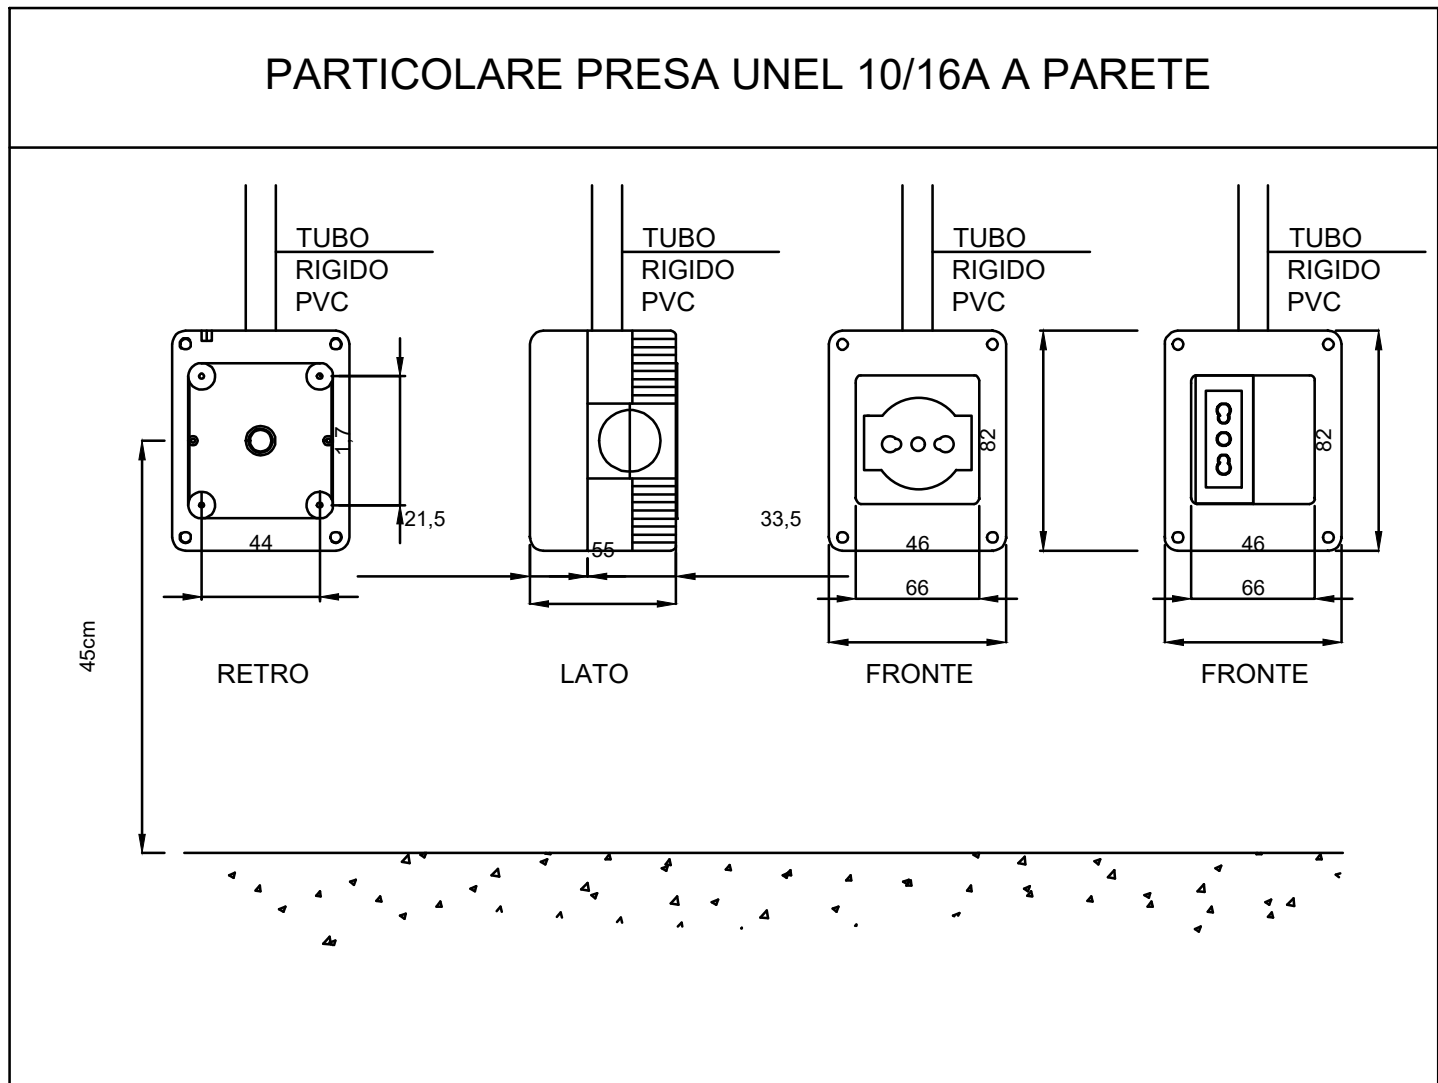
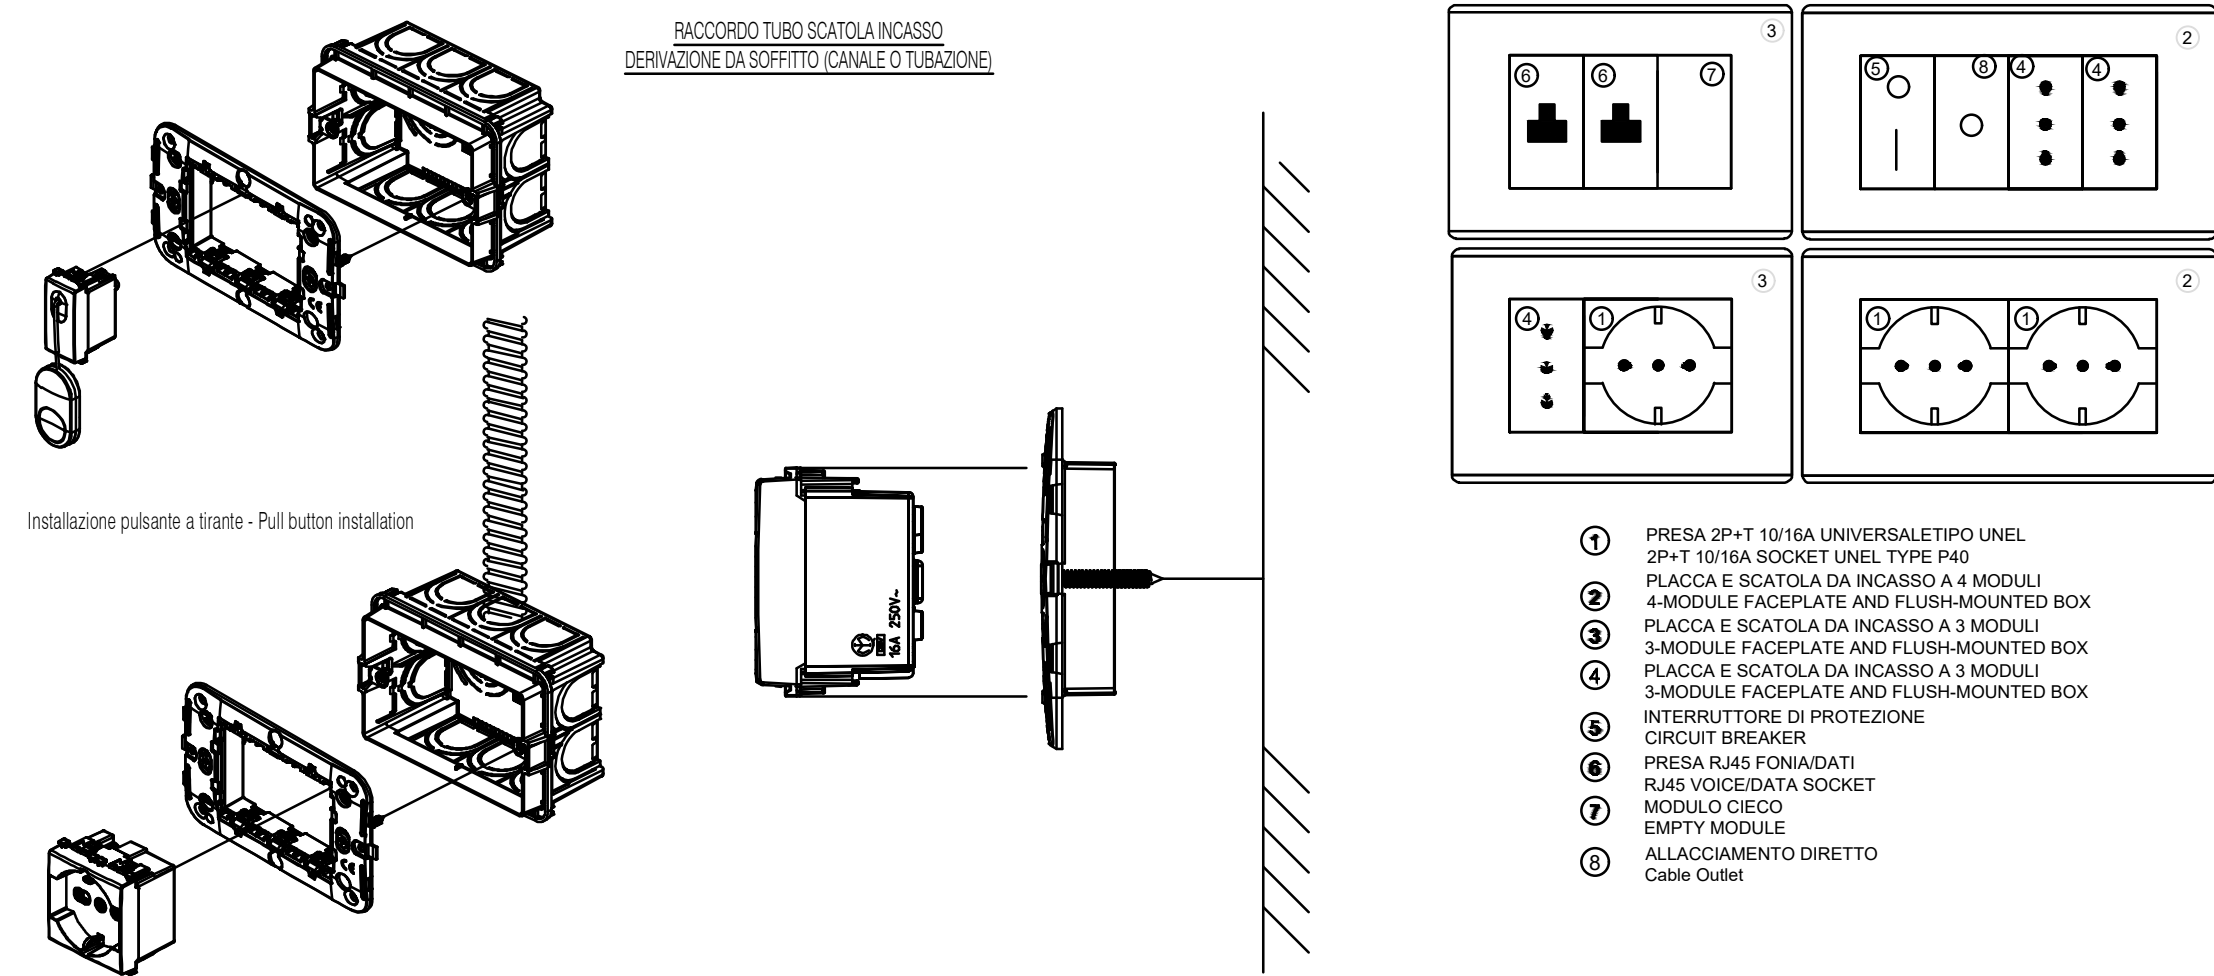
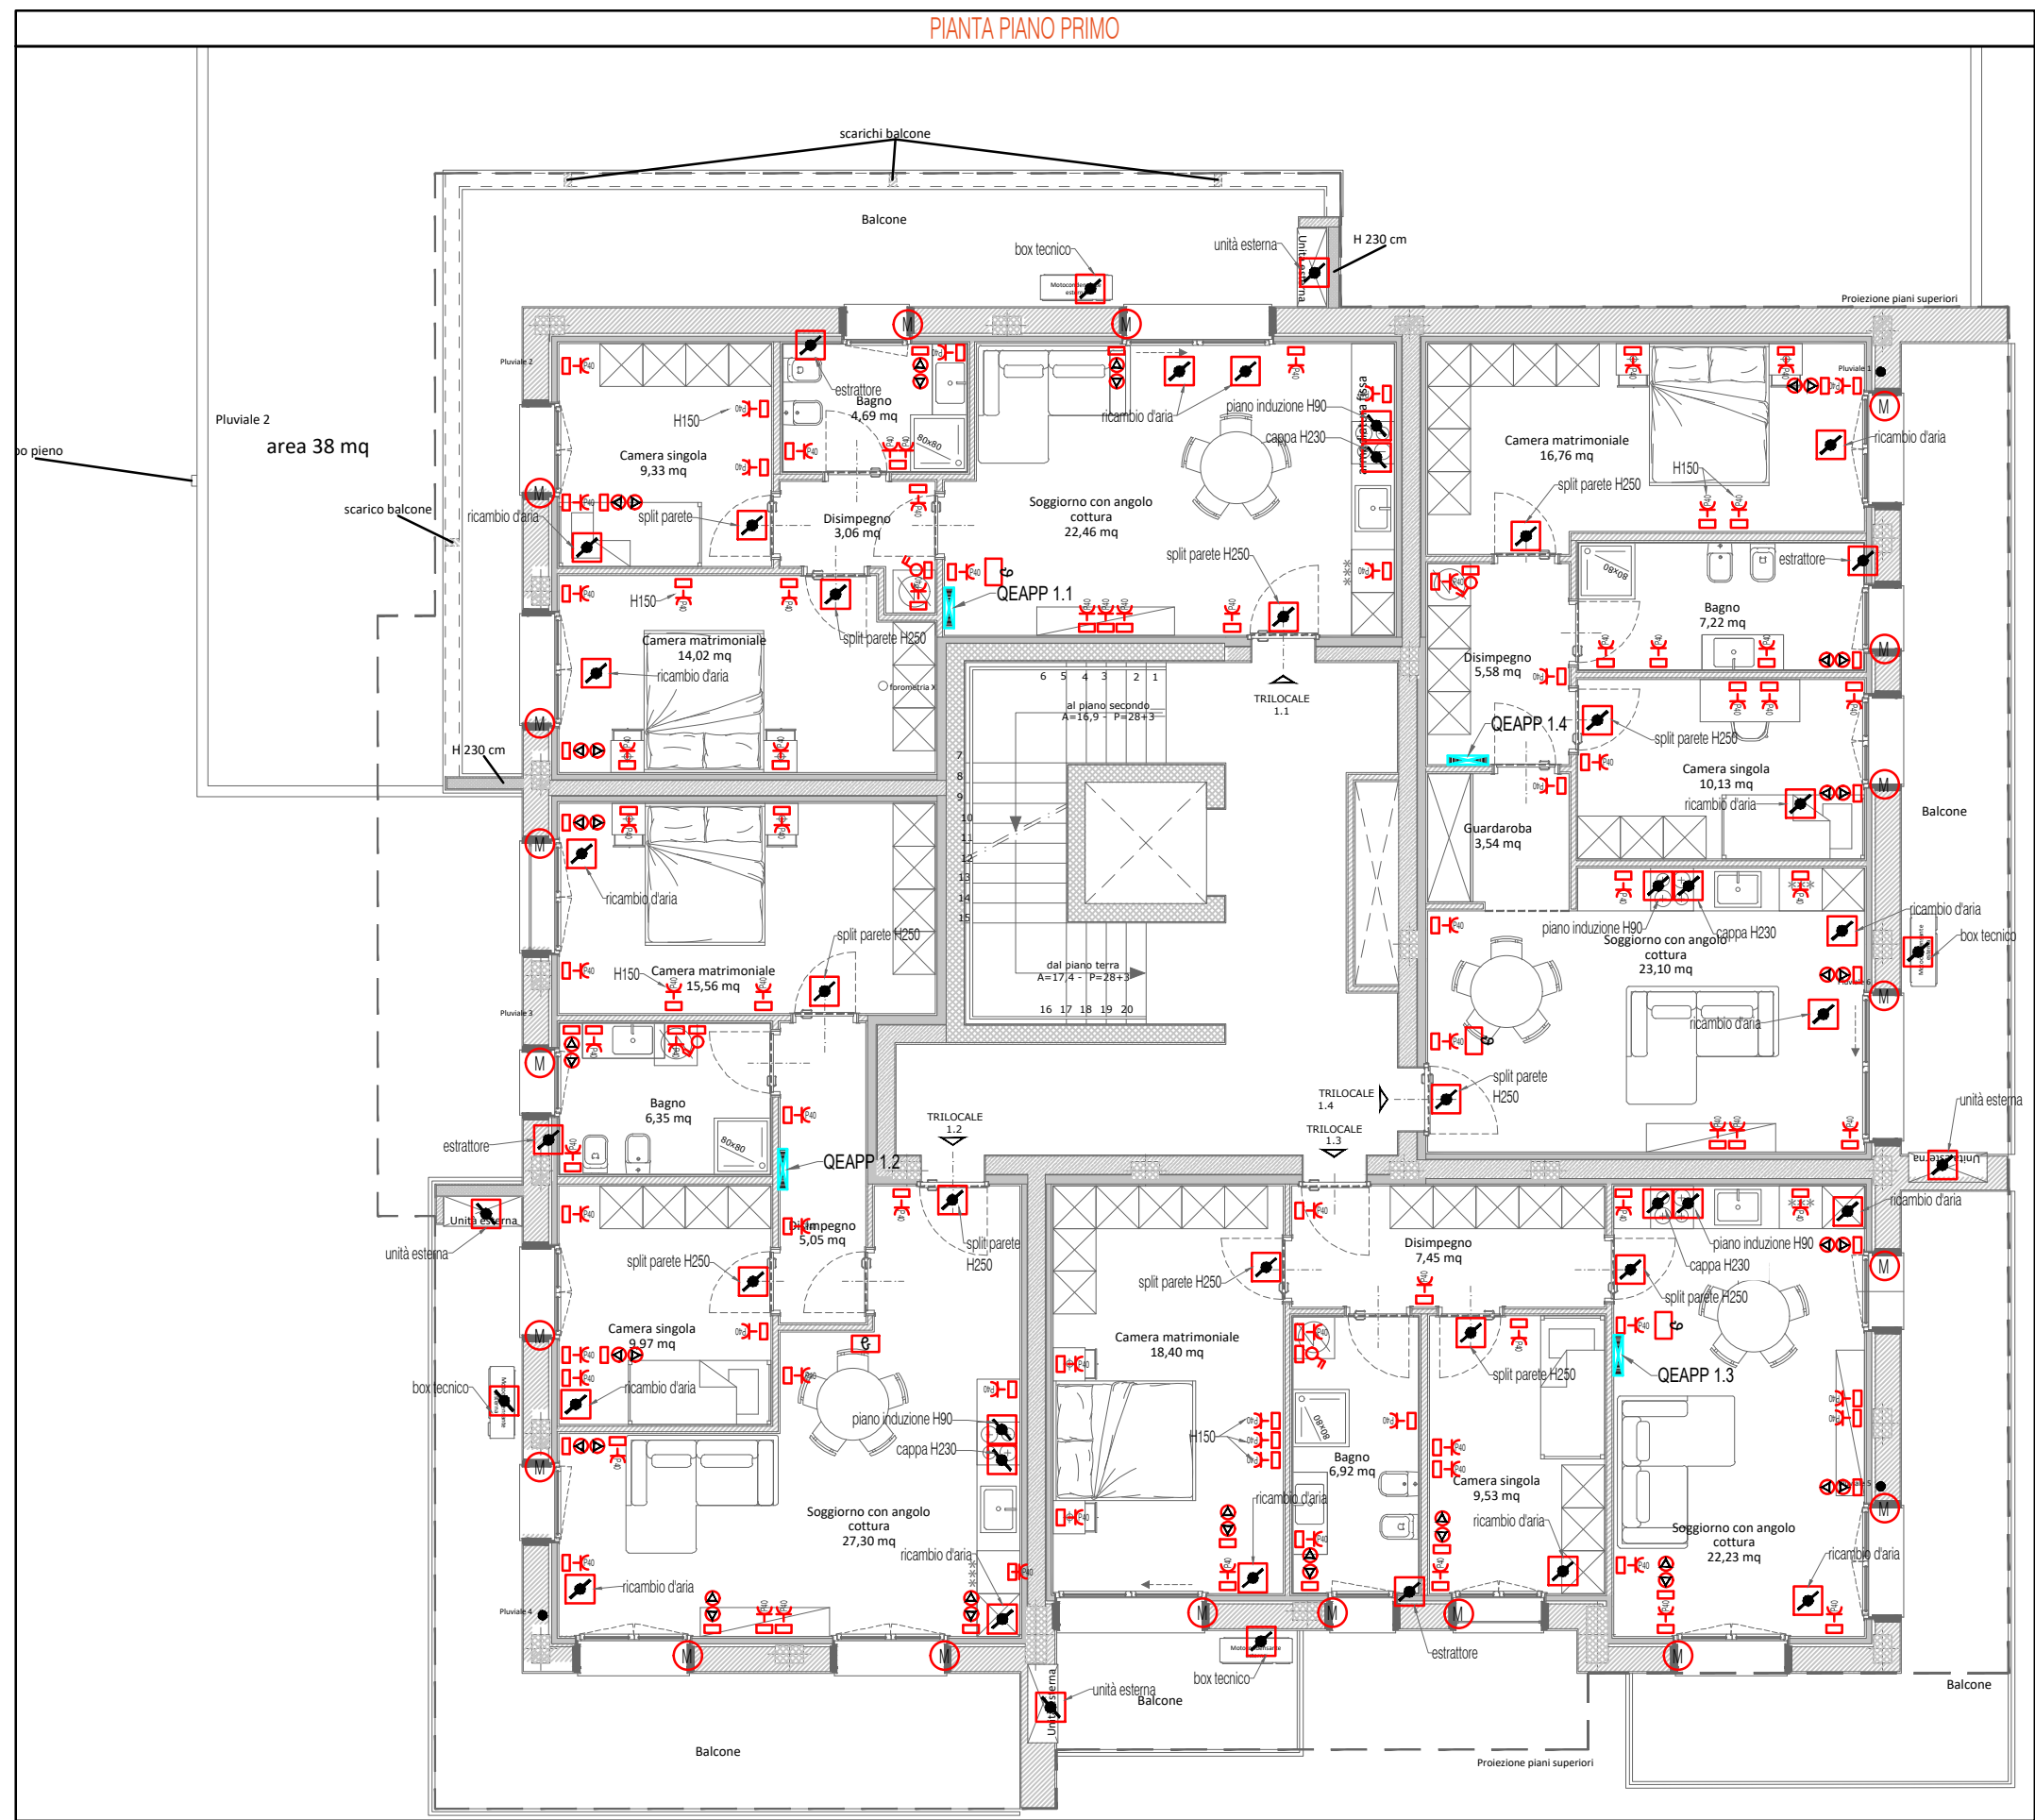


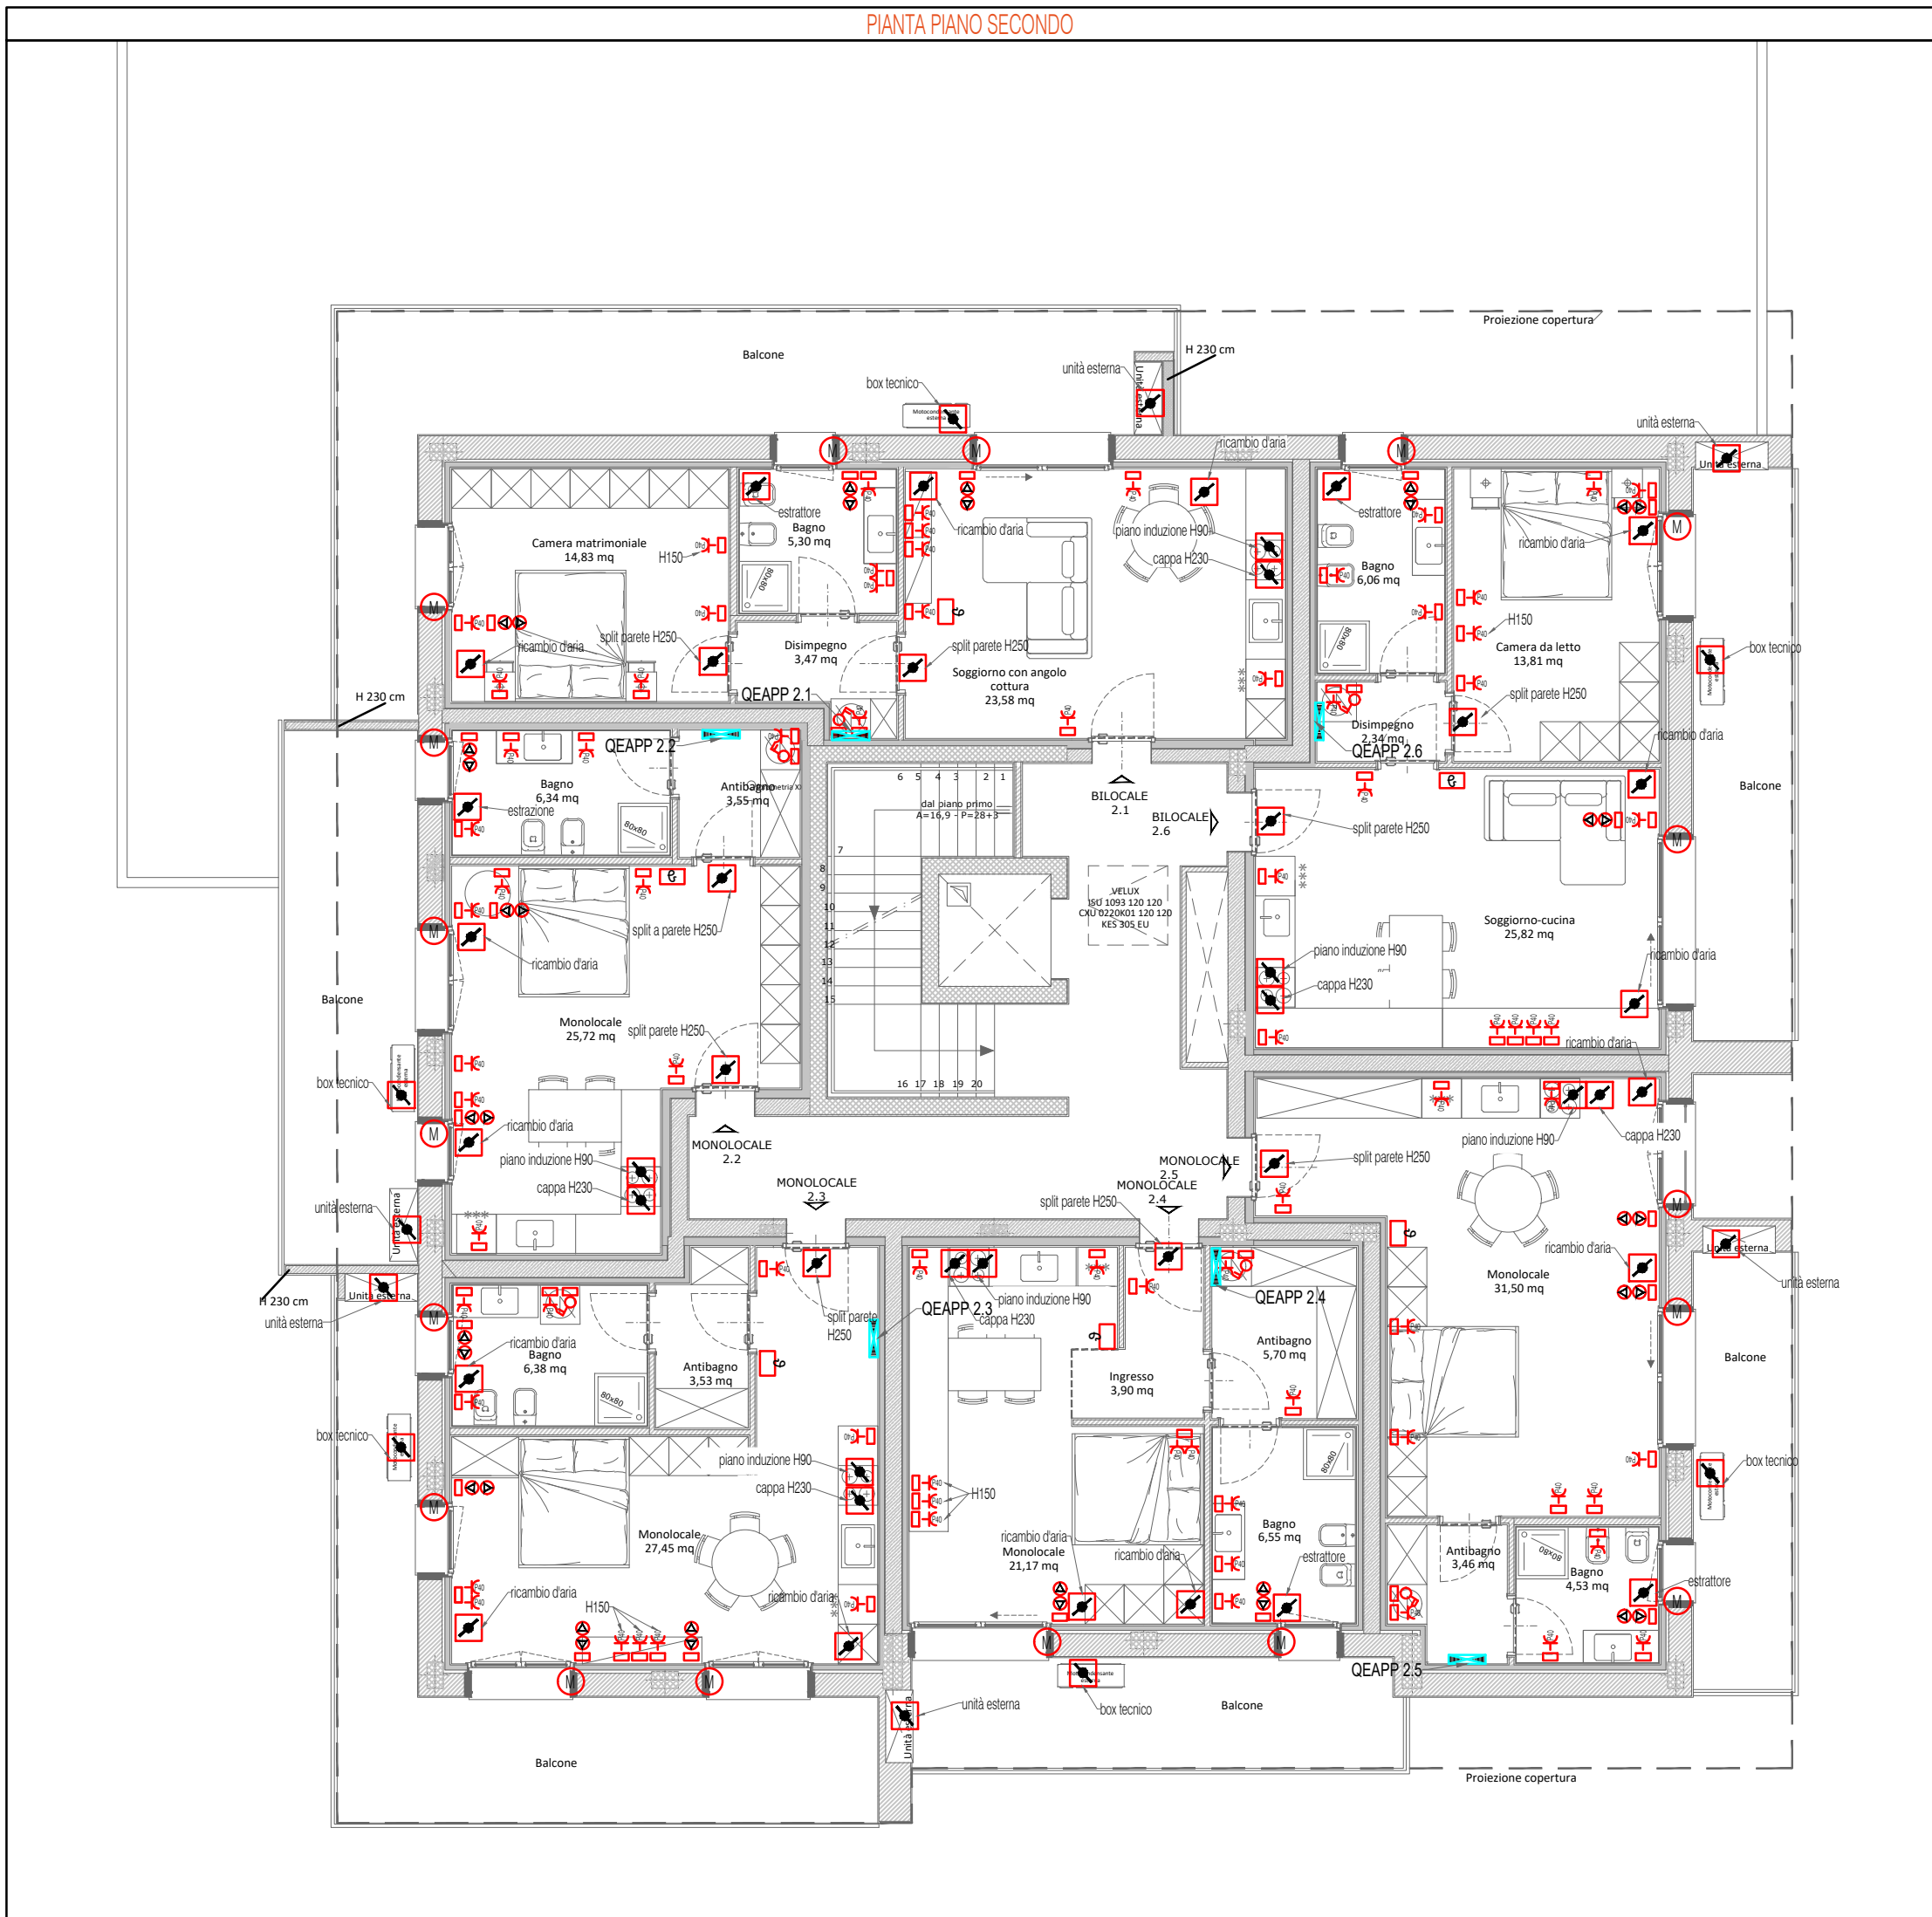


LEGENDE: IMPIANTO DI FORZA MOTRICE

	PRESA UNIVERSALE		PRESA 10/16A		ALLACCIAMENTO GENERICO
	PULSANTE		INTERRUTTORE BIPOLARE		ALLACCIAMENTO ELETTROSBARRA CONTROLLO ACCESS
	PULSANTE SALUSCENDI		ALLACCIAMENTO TAPPARELLE		

SIMBOLI VARI

	QUADRO		SCATOLA PORTAFRUTTI PER PARETI NORMALI		TUBAZIONE ESTERNA
	MONTANTE		SCATOLA DI DERIVAZIONE		TUBAZIONE INCASSATA
	CALATA		SALITA		TUBAZIONE INTERRATA

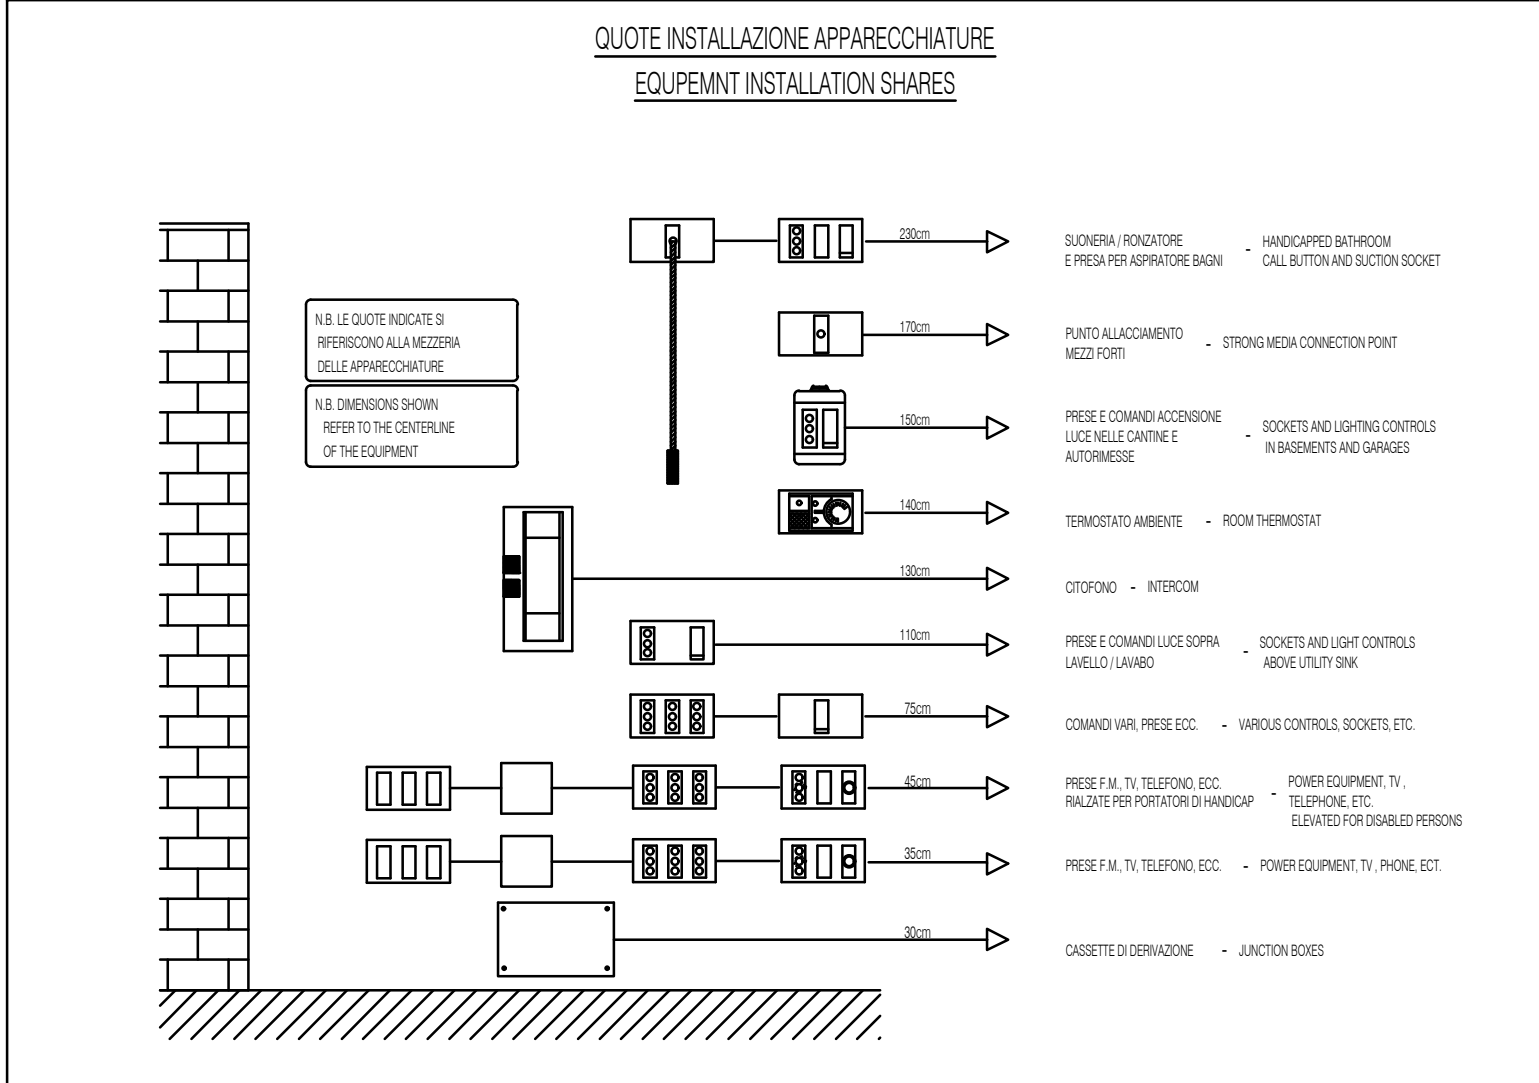

Progetto impianti

COMUNE DI COLOGNO MONZESE (MI)
AREA Ex TORRIANI ARAS 01
PROGETTO ESECUTIVO
Progetto Servizi Abitativi Pubblici di via Pergolesi

N°	DATA	DESCRIZIONE MOTIVAZIONE DELL'AGGIORNAMENTO	STUDIO	DIS.
00	16/01/2026	Prima emissione	G.B.&P.	L.M.

Progetto
PROGETTO ESECUTIVO
Servizi Abitativi Pubblici
Comune di Cologno
Monzese(MI)

Proponente
Officine Mak S.r.l.
Corso Europa, 10
Milano 20122

Scala
1:100
Data
23/01/2026

Tipo tavola
IMPIANTI
Serie
PROGETTO ESECUTIVO
Titolo
**IMPIANTI ELETTRICI -
IMPIANTO DI FORZA MOTRICE**

Tavola nr.
Tipo
Tavola
Sigla /
Serie
Numero /
Variante
Agg.

IMP
ES
01
00

Orientamento
N

Documento di proprietà della Società G.B. & Partners S.r.l.. E' vietata la riproduzione. Tutti i diritti sono riservati.