


	INVERTER		QUADRO ELETTRICO CORRENTE CONTINUA		CONTATORE
	MODULO FOTOVOLTAICO		QUADRO ELETTRICO CORRENTE ALTERNATA		CALATA

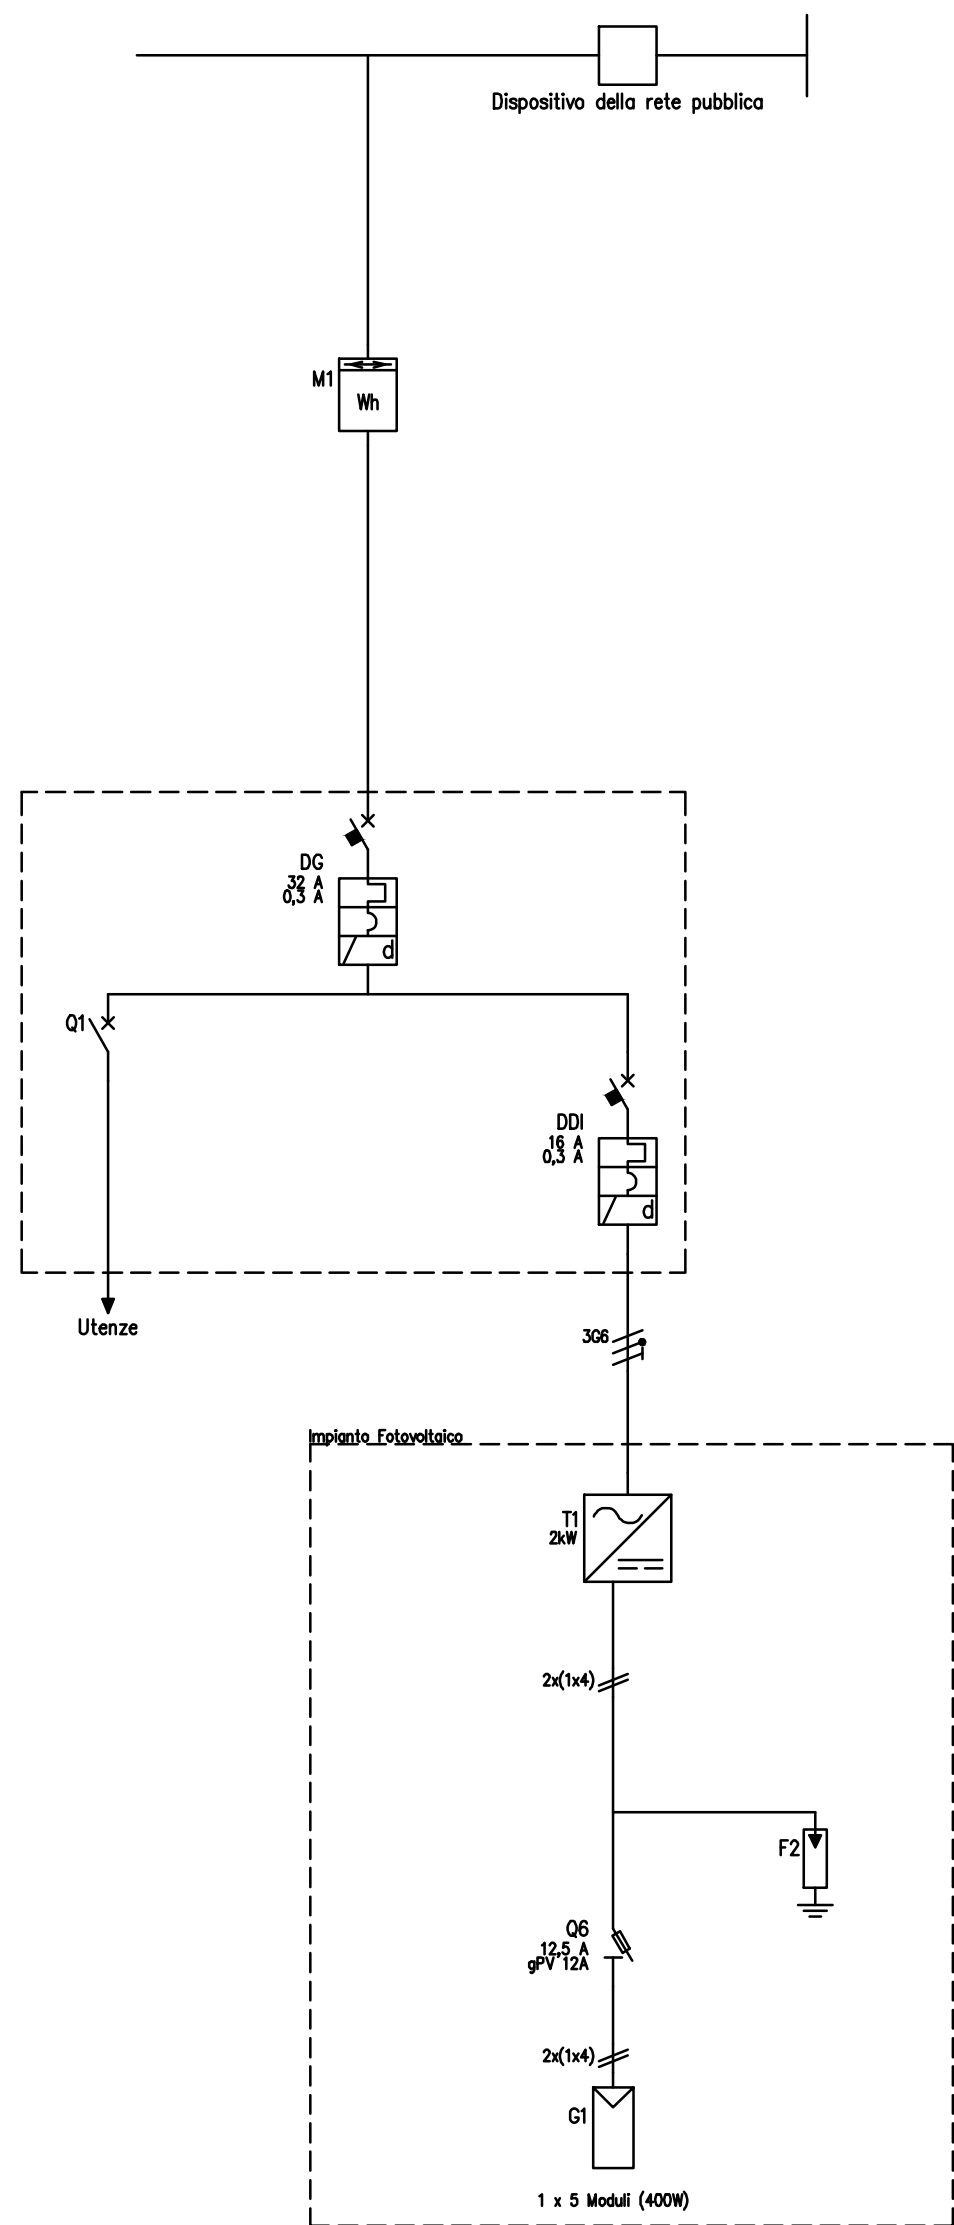

Legenda simboli	
	Contatore bidirezionale
	Inverter
	Campo fotovoltaico
	Magnetotermico
	Fusibile
	Magnetotermico-Differenziale
	Int. manovra sezionatore
	Interruttore
	Scaricatore

DG: Dispositivo Generale
DD: Dispositivo di Interfaccia

Assetti di esercizio

Assetto 1 - Dispositivo generale e di interfaccia chiusi.
carichi dell'impianto sono alimentati dalla rete e dal generatore fotovoltaico

Assetto 2 - Dispositivo generale chiuso e dispositivo di interfaccia aperto.
carichi sono alimentati solamente dalla rete (evento anomalo sul generatore o mancata produzione)

Assetto 3 - Dispositivo generale e di interfaccia aperti.
carichi dell'impianto non sono alimentati (mancanza di alimentazione sulla rete)

Legenda simboli	
	Contatore bidirezionale
	Inverter
	Campo fotovoltaico
	Magnetotermico
	Fusibile
	Magnetotermico-Differenziale
	Int. manovra sezionatore
	Interruttore
	Scaricatore

DG: Dispositivo Generale DDI: Dispositivo di interfaccia	
Assetti di esercizio	
Assetto 1 – Dispositivo generale e di interfaccia chiusi. I carichi dell'impianto sono alimentati dalla rete o dal generatore fotovoltaico	
Assetto 2 – Dispositivo generale chiuso e dispositivo di interfaccia aperto. I carichi dell'impianto sono alimentati solamente dalla rete (evento anomalo sul generatore o mancato produzione)	
Assetto 3 – Dispositivo generale e di interfaccia aperti. I carichi dell'impianto non sono alimentati (mancanza di alimentazione sulla rete)	

area 67 mq

area 84 mq

area 82 mq

area 83 mq

area 81 mq

area 89 mq

IMPIANTO FOTOVOLTAICO
N. 10 MODULI DA 800W CADA
POTENZA COMPLESSIVA: 8.000 Wp

area 67 mq

area 84 mq

area 82 mq


area 83 mq

area 81 mq

area 89 mq

IMPIANTO FOTOVOLTAICO
N. 10 MODULI DA 800W CADA
POTENZA COMPLESSIVA: 8.000 Wp

	PRESA TRASMISSIONE DATI		PRESA TV		ANTENNA SAT
	VIDEOCITOFONO		SUONERIA		RICEVITORE
	PULSANTE PER CAMPANELLO APPARTAMENTO		PULSANTE DI TACITAZIONE CHIAMATA BAGNI		ANTENNA TV

 
GB&PARTNERS
 SERVIZI A PROGETTI IMMOBILIARI
 Via S. Maria Maddalena 10 - 00187 Roma (RM) - Tel. 06/47811111
 E-mail: info@gbpartners.it - www.gbpartners.it
 P.IVA 04451890230 - Partita IVA 04451890230
 Registro Imprese Roma 1355055 - C.A.B. 0268/2013
 2014-2015






Progetto impianti


Dabster srl
 Via Sommacampagna 63/H - 37137 Verona
 P.IVA 04451890230
 E-mail: mail@dabster.it

N°	DATA	DESCRIZIONE MOTIVAZIONE DELL'AGGIORNAMENTO	STUDIO	DIS.
00	16/01/2026	Prima emissione	G.B.&P.	L.M.

Collegio Provinciale
Geometri e Geometri Laureati
di Lodi

 Iscrizione Albo
N. 257

Geometra
Gianpiero Bianchi

Scala
1:100
Data
23/01/2026

Tavola nr.	
Tipo Tavola	IMP
Sigla / Serie	ES
Numero / Variante	01
Agg.	00