
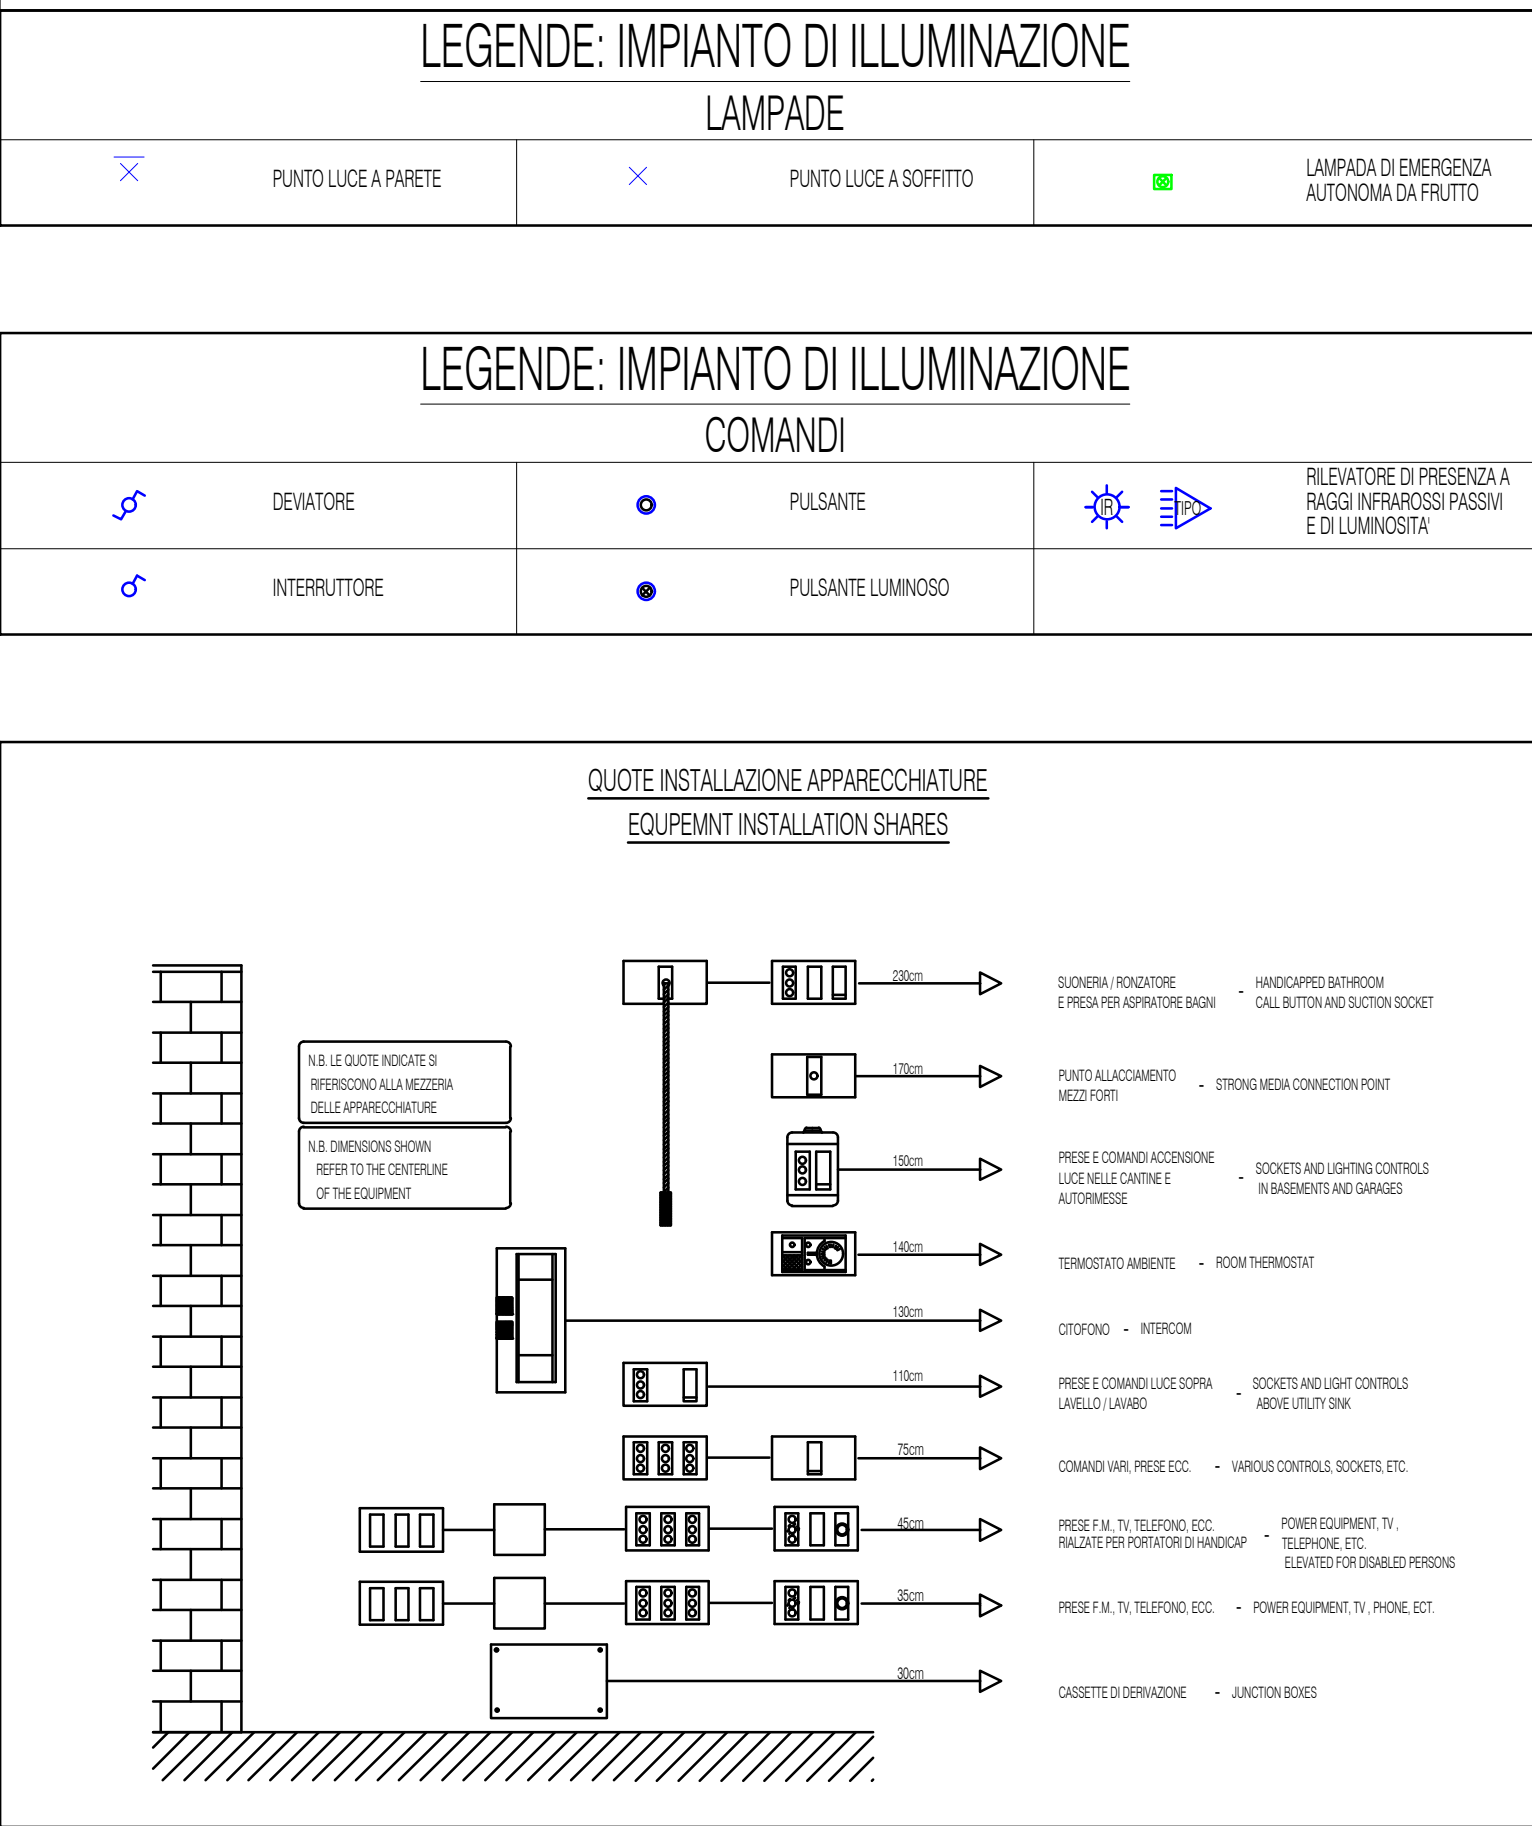
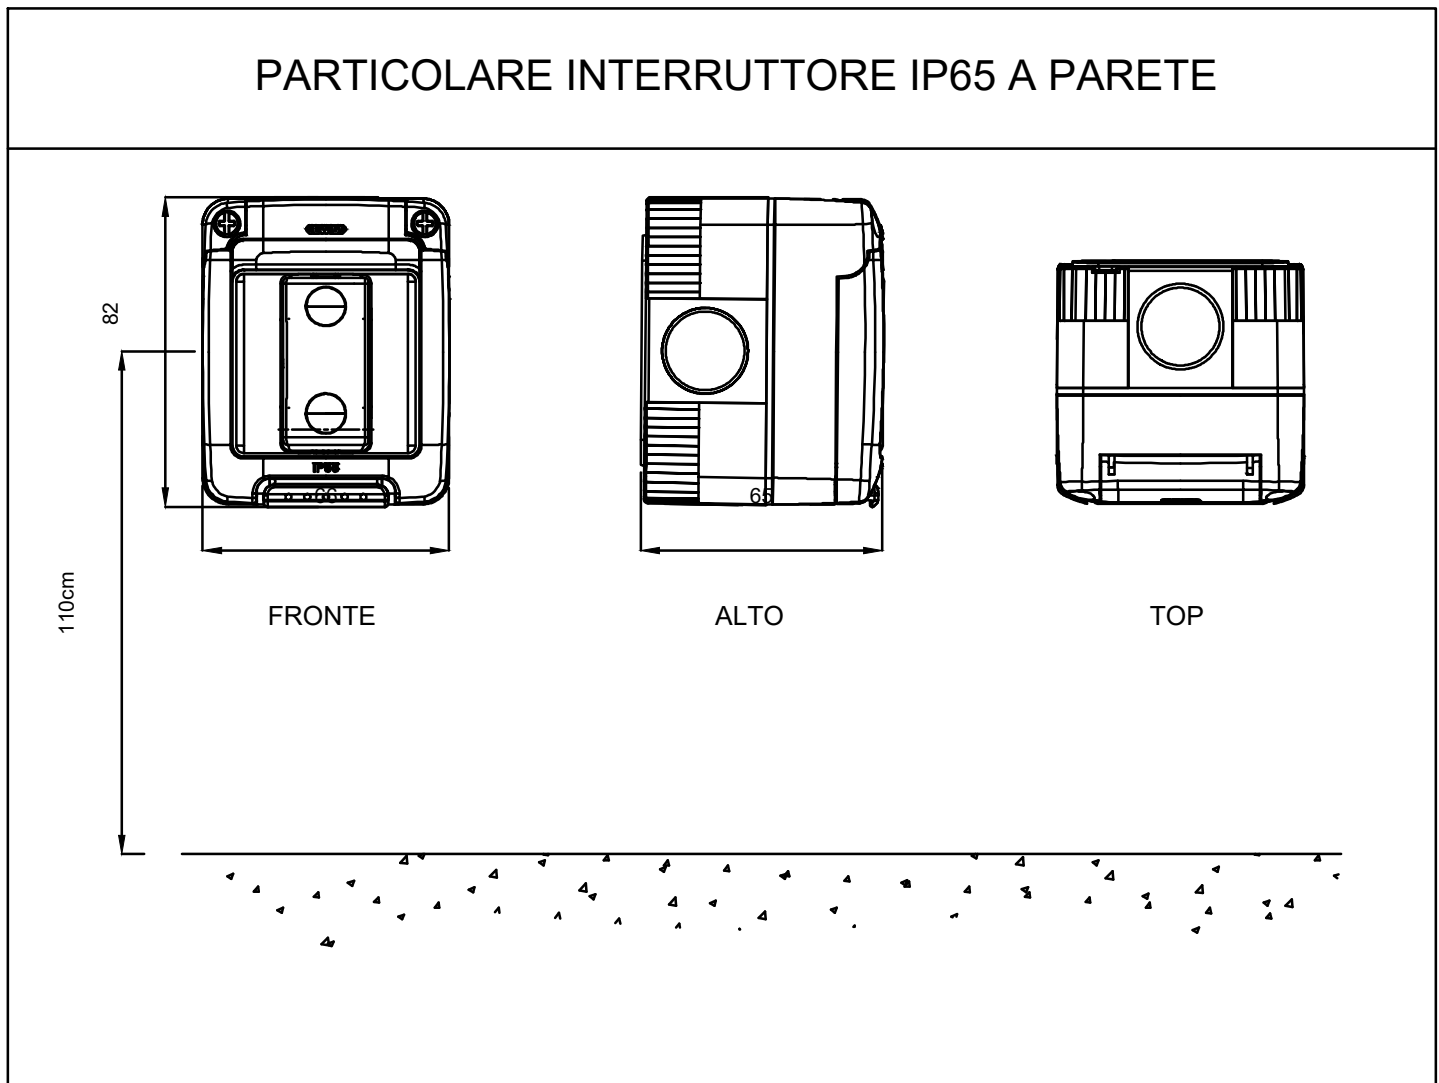
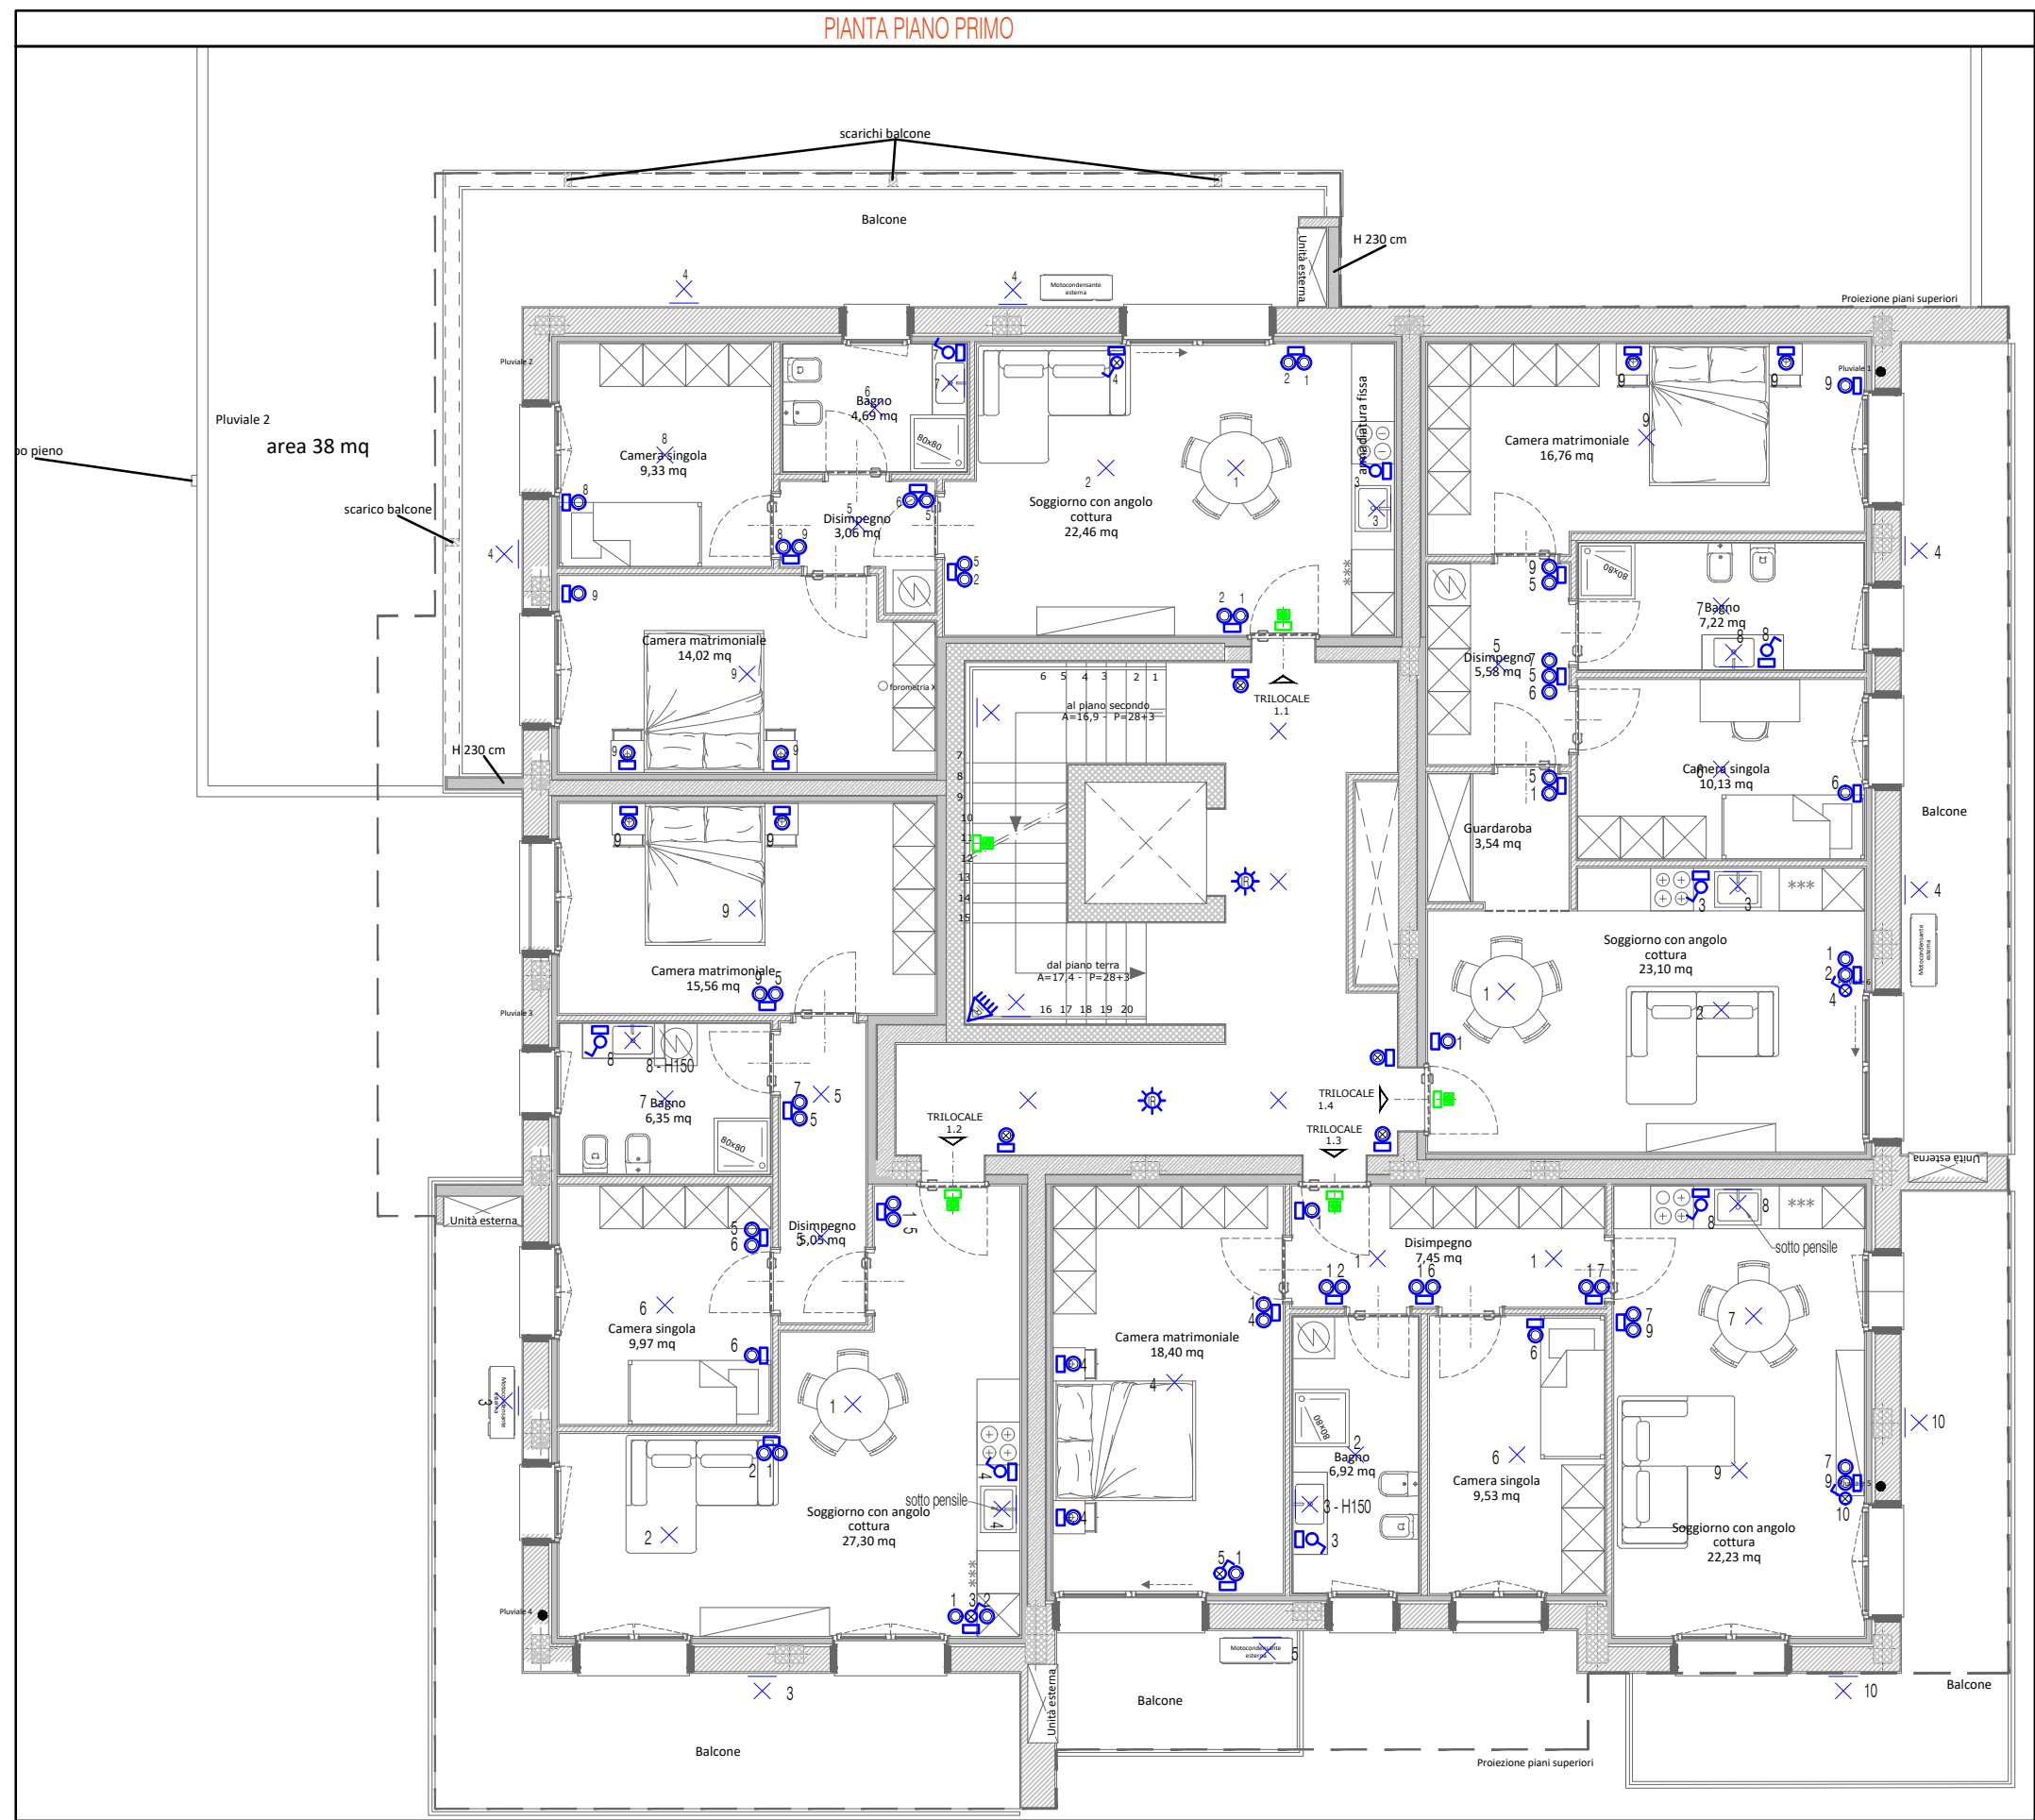


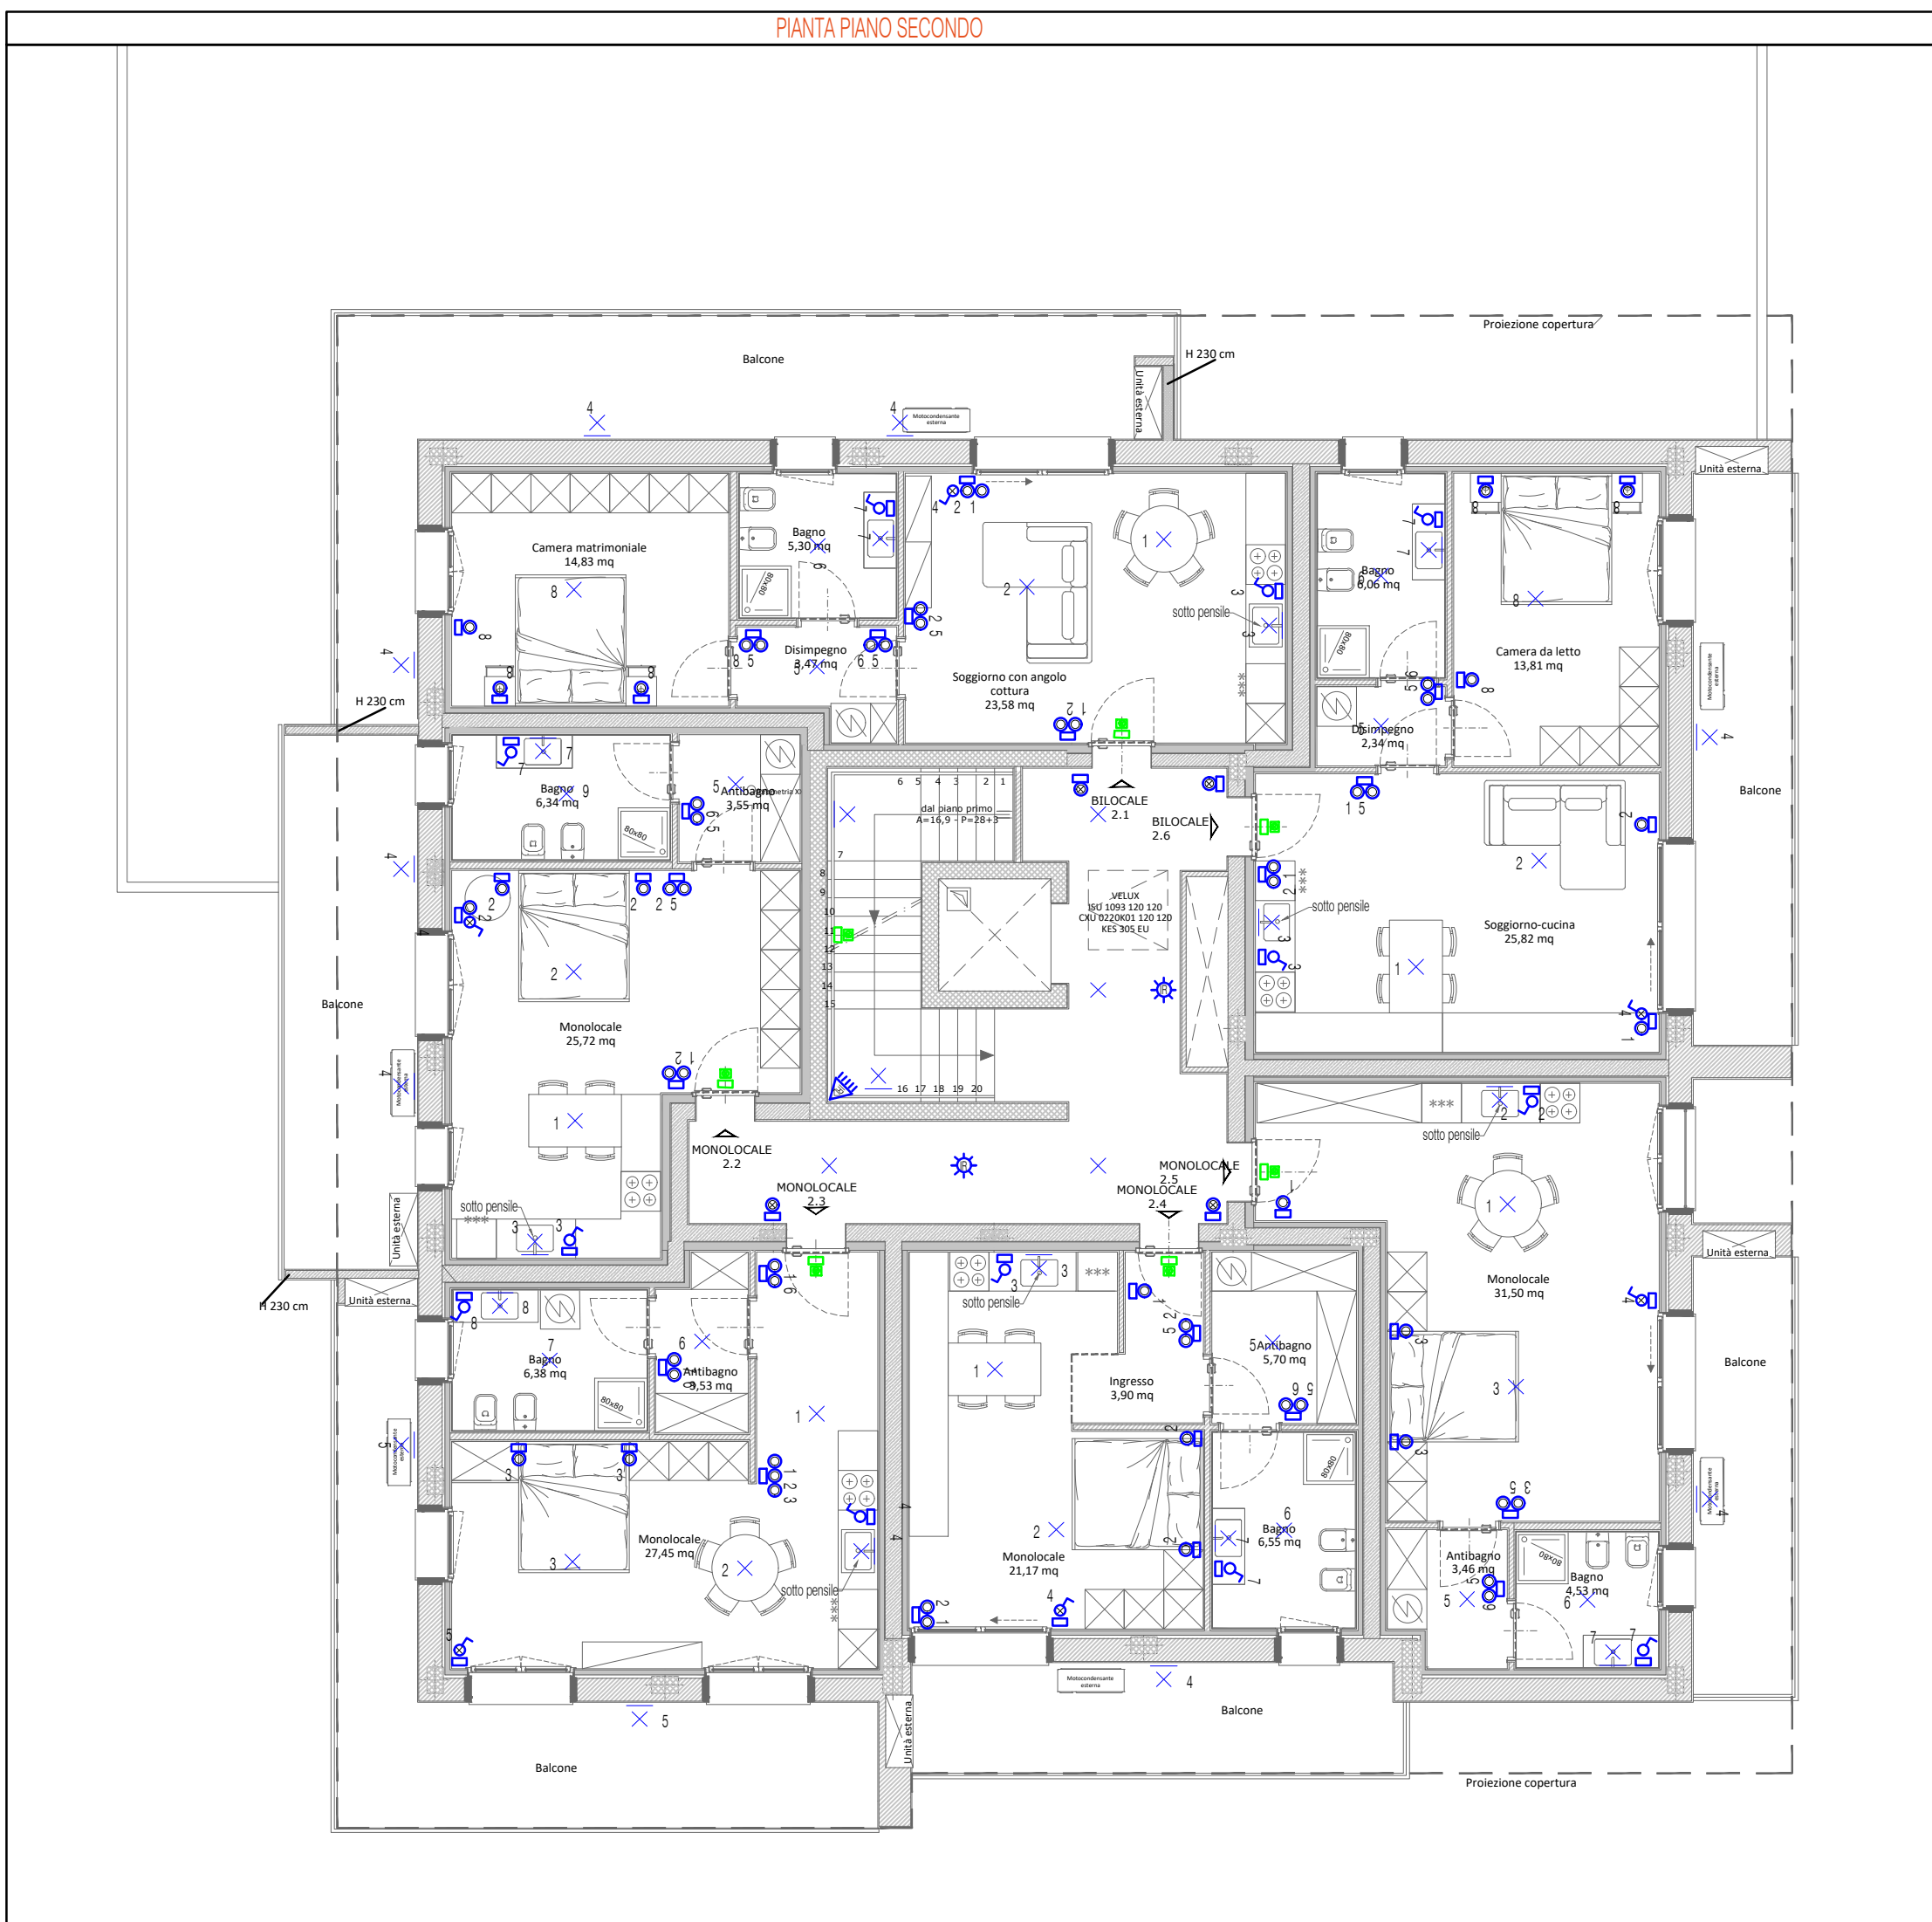

GB&PARTNERS SERVIZI E PROGETTI IMMOBILIARI

Progetto impianti

dabster ENGINEERING

Dabster srl
Via Sommacampagna 63/H - 37137 Verona
P. IVA 04464890230
mail: mail@dabster.it

COMUNE DI COLOGNO MONZESE (MI)
AREA Ex TORRIANI ARAS 01
PROGETTO ESECUTIVO
Progetto Servizi Abitativi Pubblici di via Pergolesi

N°	DATA	DESCRIZIONE	MOTIVAZIONE DELL'AGGIORNAMENTO	STUDIO	DIS.
00	16/01/2026	Prima emissione		G.B.&P.	L.M.

Il Progettista

Collegio Provinciale Geometri e Geometri Laureati di Lodi

Ing. Gianpiero Bianchi

Geometra Gianpiero Bianchi

Progetto

PROGETTO ESECUTIVO

Servizi Abitativi Pubblici
Comune di Cologno Monzese(MI)

Proponente

Officine Mak S.r.l.
Corso Europa, 10
Milano 20122

Scala

1:100

Data

23/01/2026

Tipo tavola

IMPIANTI

Serie

PROGETTO ESECUTIVO

Titolo

IMPIANTI ELETTRICI - IMPIANTO DI ILLUMINAZIONE

Tavola nr.

Tipo Tavola

IMP

Sigla / Serie

ES

Numero / Variante

01

Agg.

00

Orientamento

N

Documento di proprietà della Società G.B. & Partners S.r.l. E' vietata la riproduzione. Tutti i diritti sono riservati.