## PIANTA PIANO TERRA

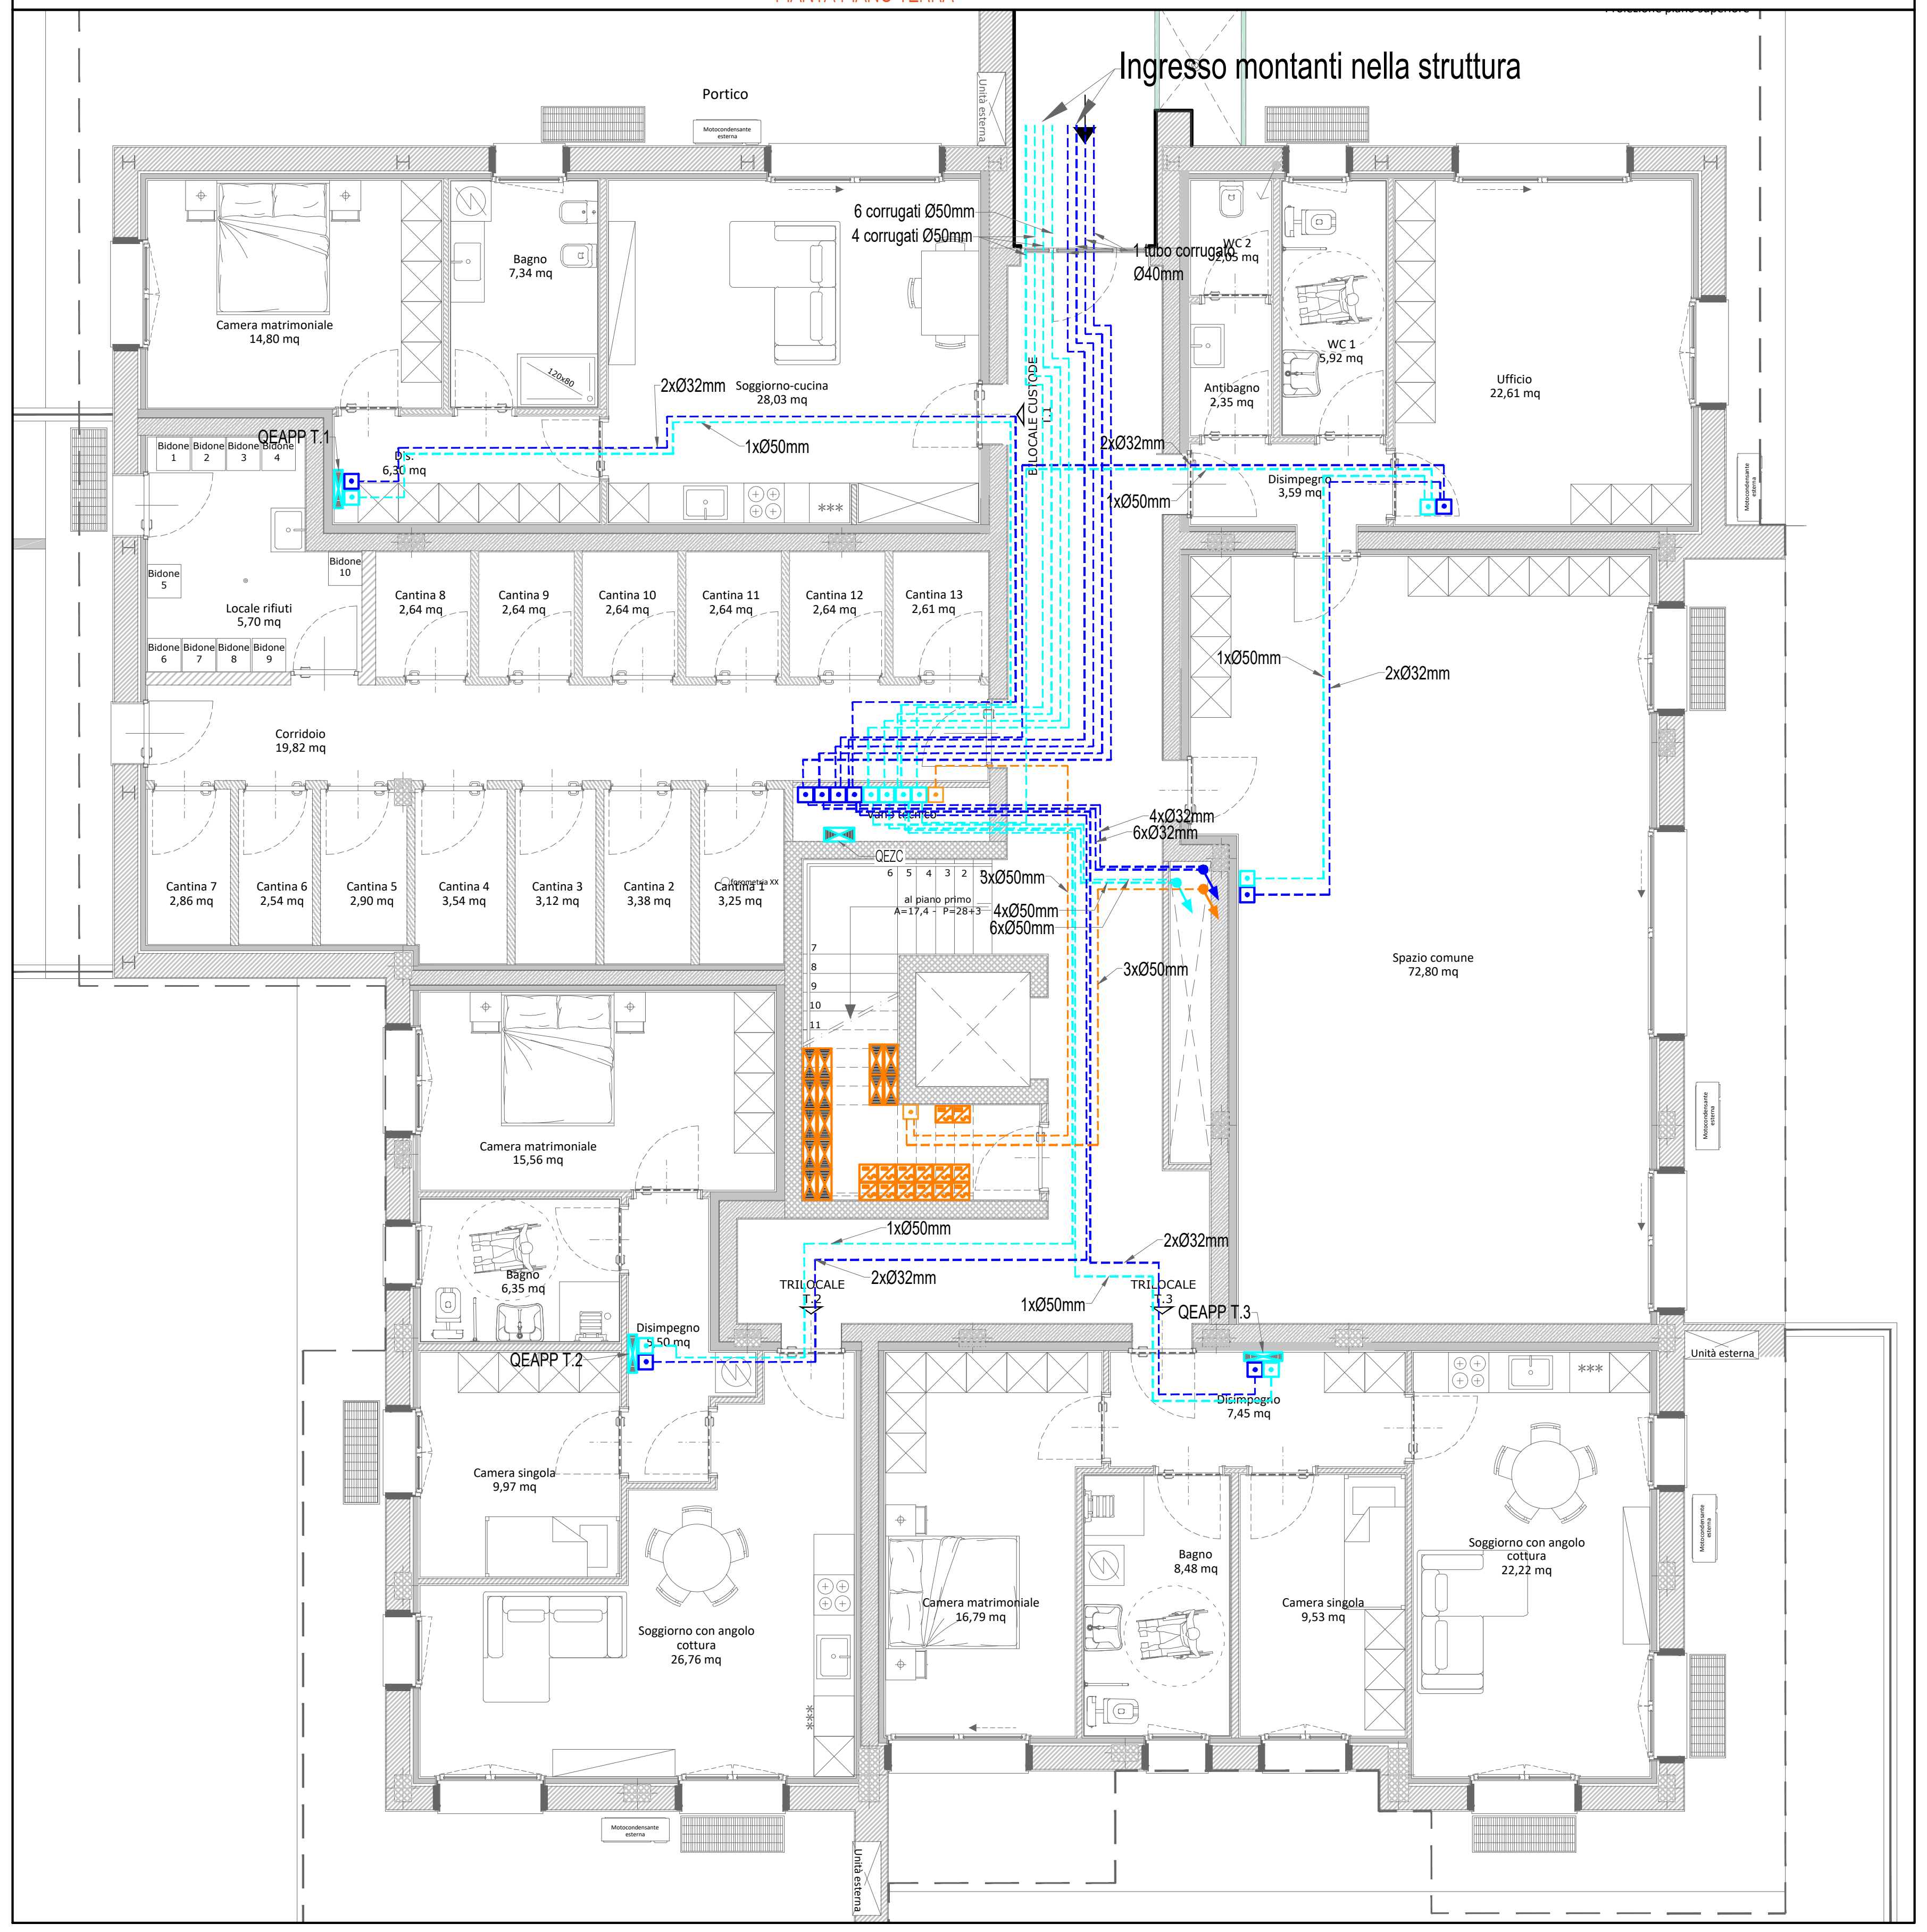

## PIANTA PIANO SECONDO

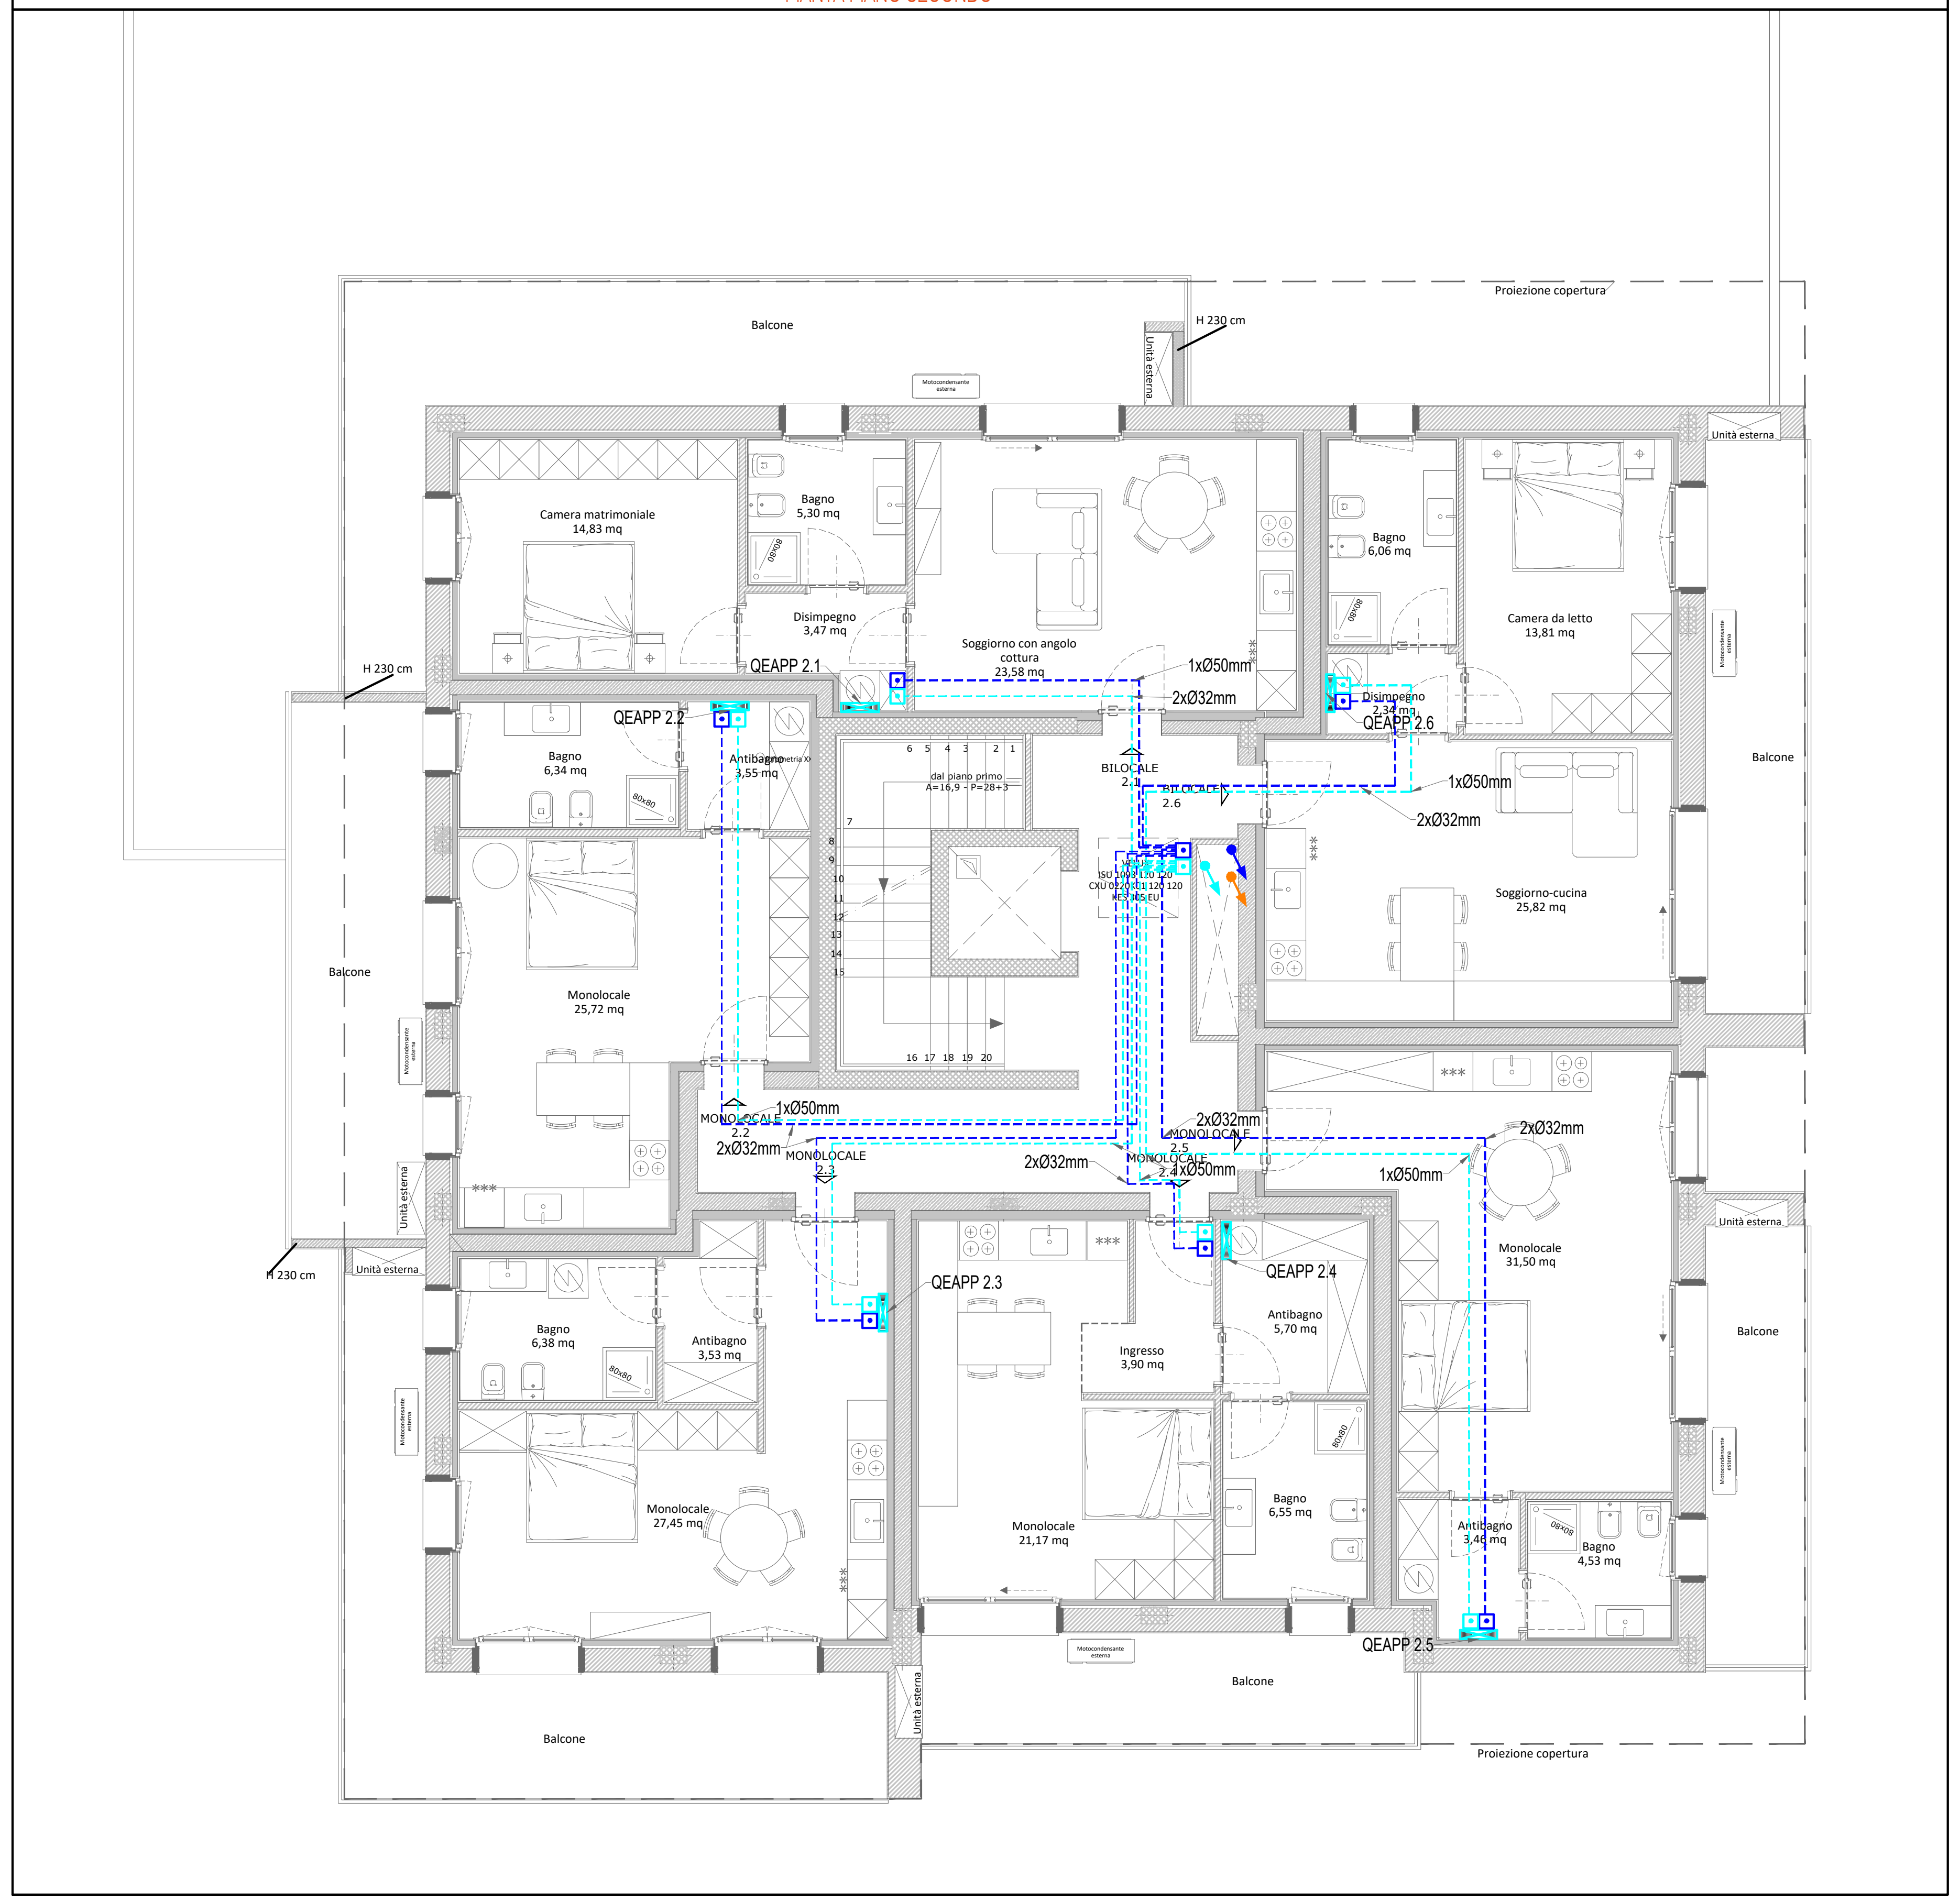

## PIANTA PIANO PRIMO

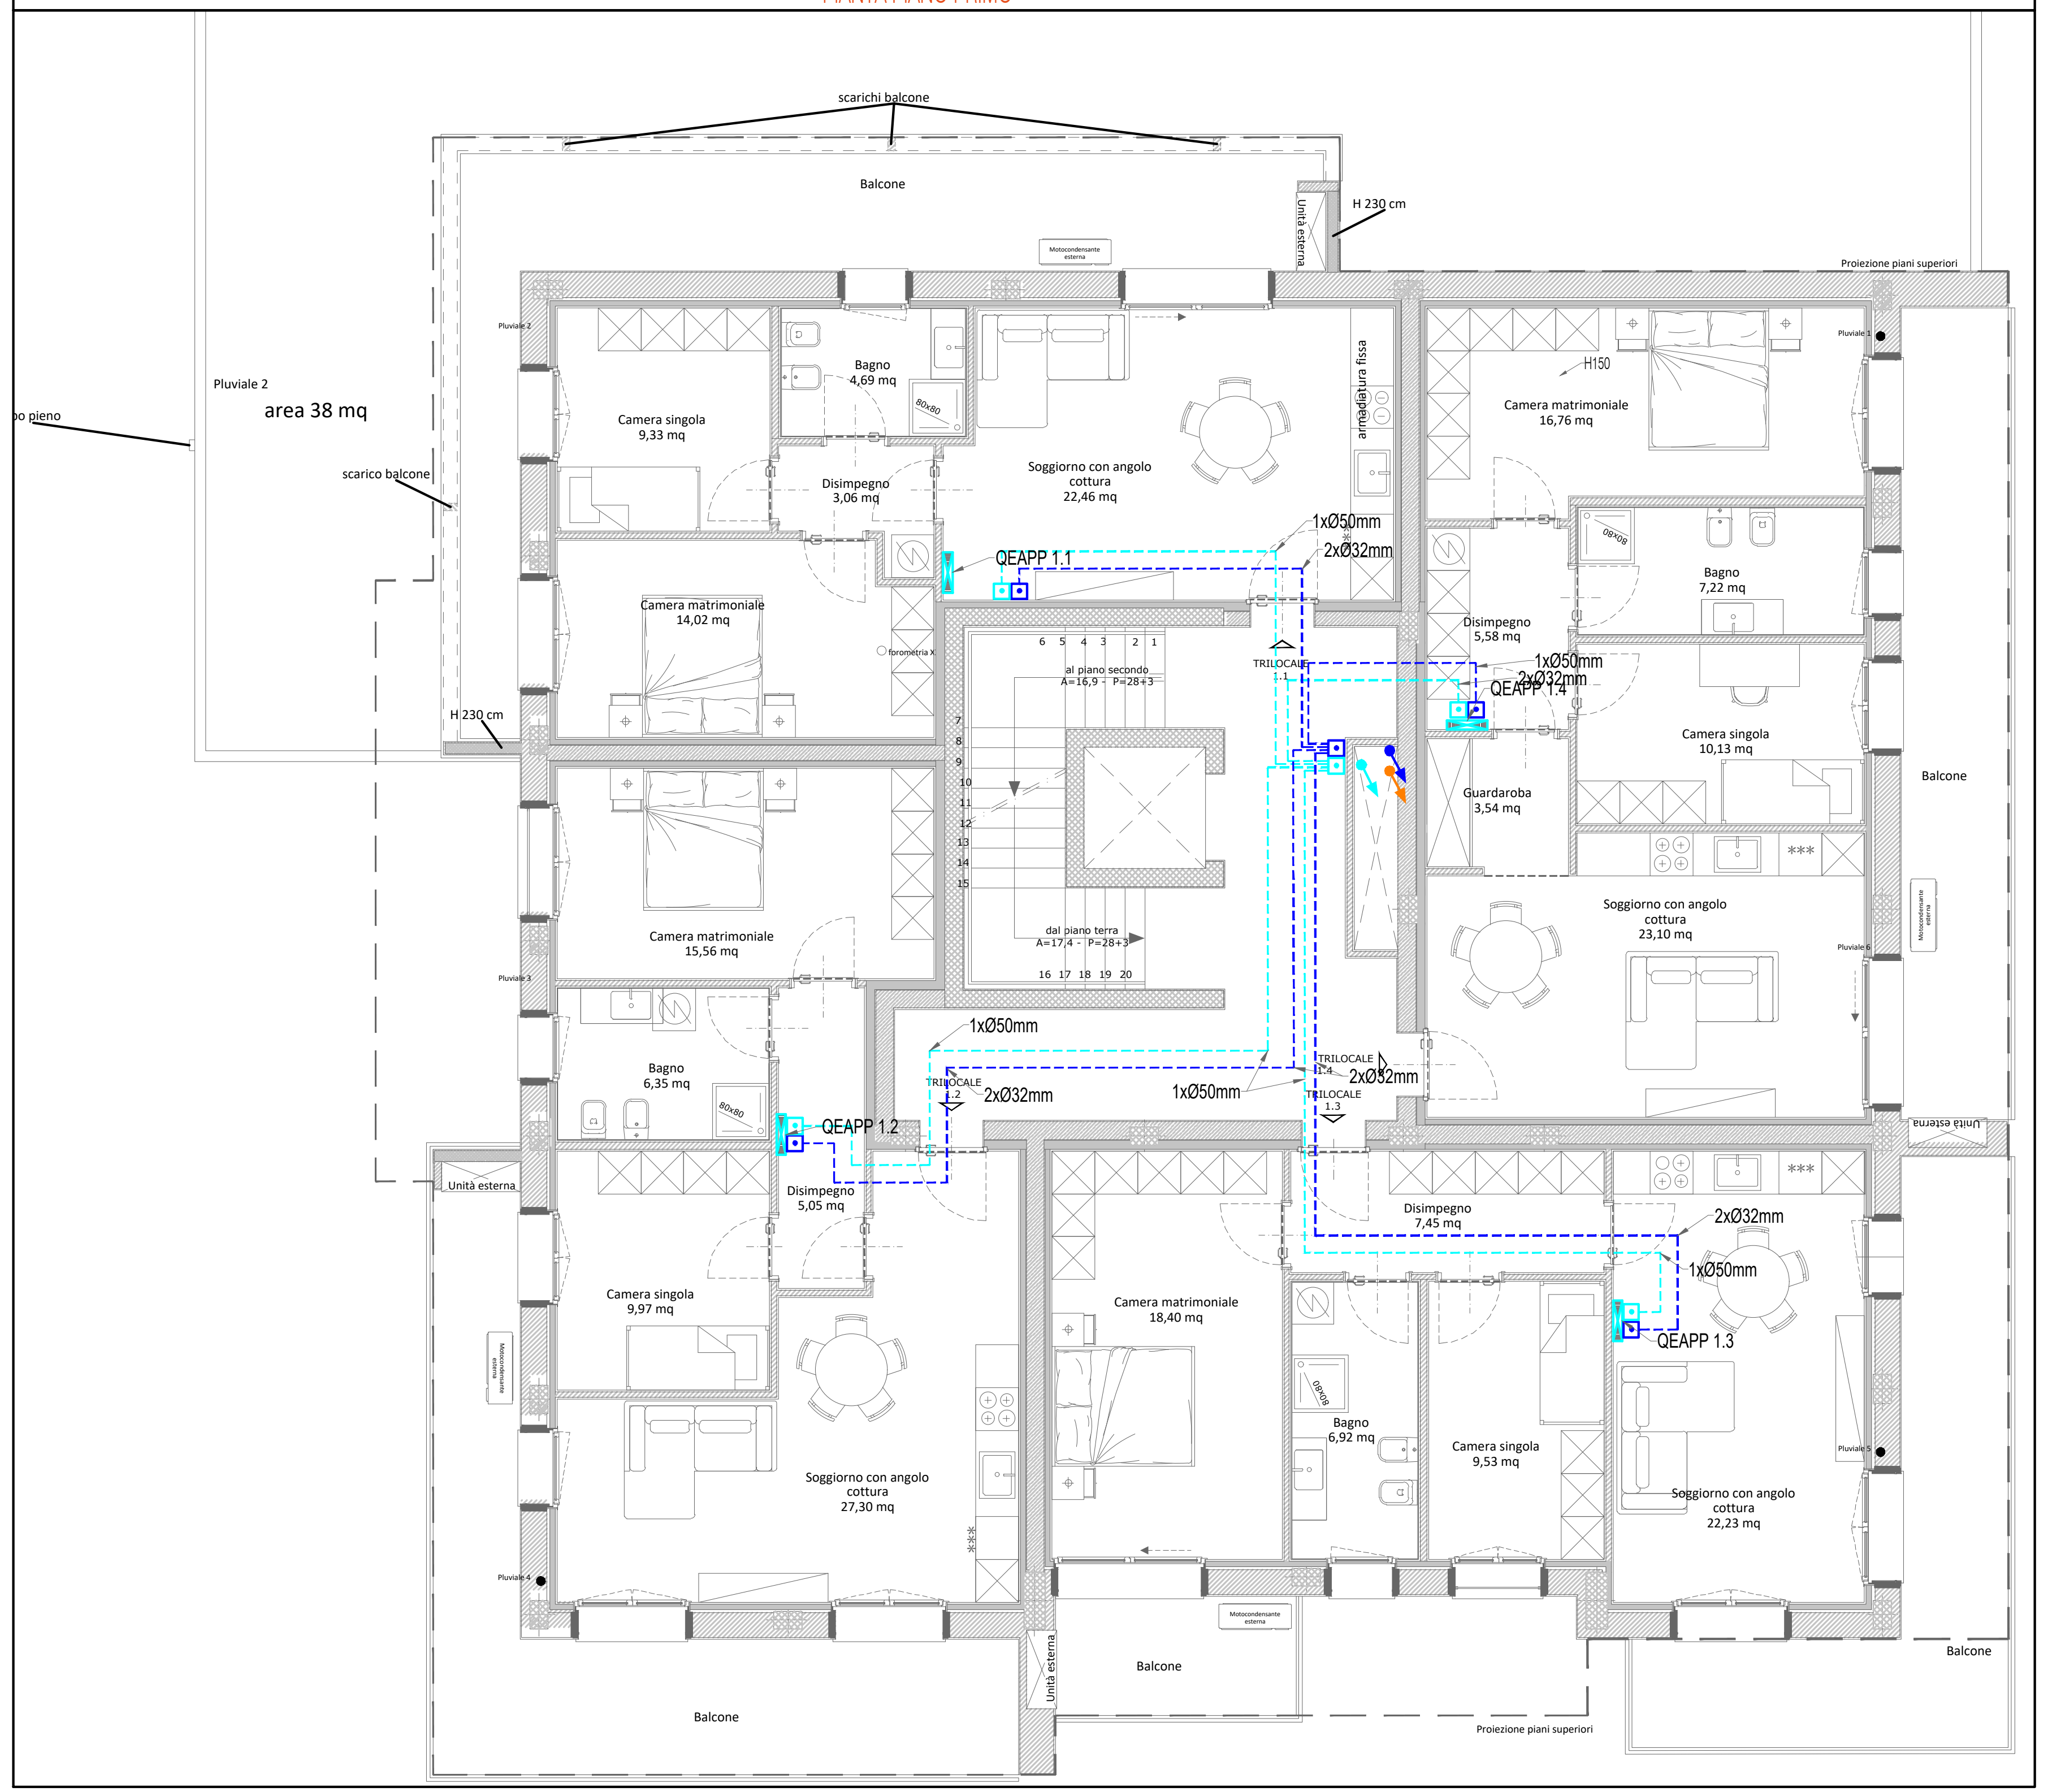

## SIMBOLI FOTOVOLTAICO

| | | | | | |
|---|---|---|---|---|---|
| ▨ | INVERTER | ⊠ | QUADRO ELETTRICO CORRENTE CONTINUA | Wh | CONTATORE |
| ▦ | MODULO FOTOVOLTACO | ⊠ | QUADRO ELETTRICO CORRENTE ALTERNATA | ↙ | CALATA |

## SIMBOLI VARI

| | | | | | |
|---|---|---|---|---|---|
| ⊠ | QUADRO | ▭ | SCATOLA PORTAFRUTTI PER PARETI NORMALI | ш ш | TUBAZIONE ESTERNA |
| ↗↙ | MONTANTE | ⊡ | SCATOLA DI DERIVAZIONE | ⌇∘⌇ | TUBAZIONE INCASSATA |
| ↙ | CALATA | ↗ | SALITA | ≡ | TUBAZIONE INTERRATA |

## QUOTE INSTALLAZIONE APPARECCHIATURE
## EQUPEMNT INSTALLATION SHARES

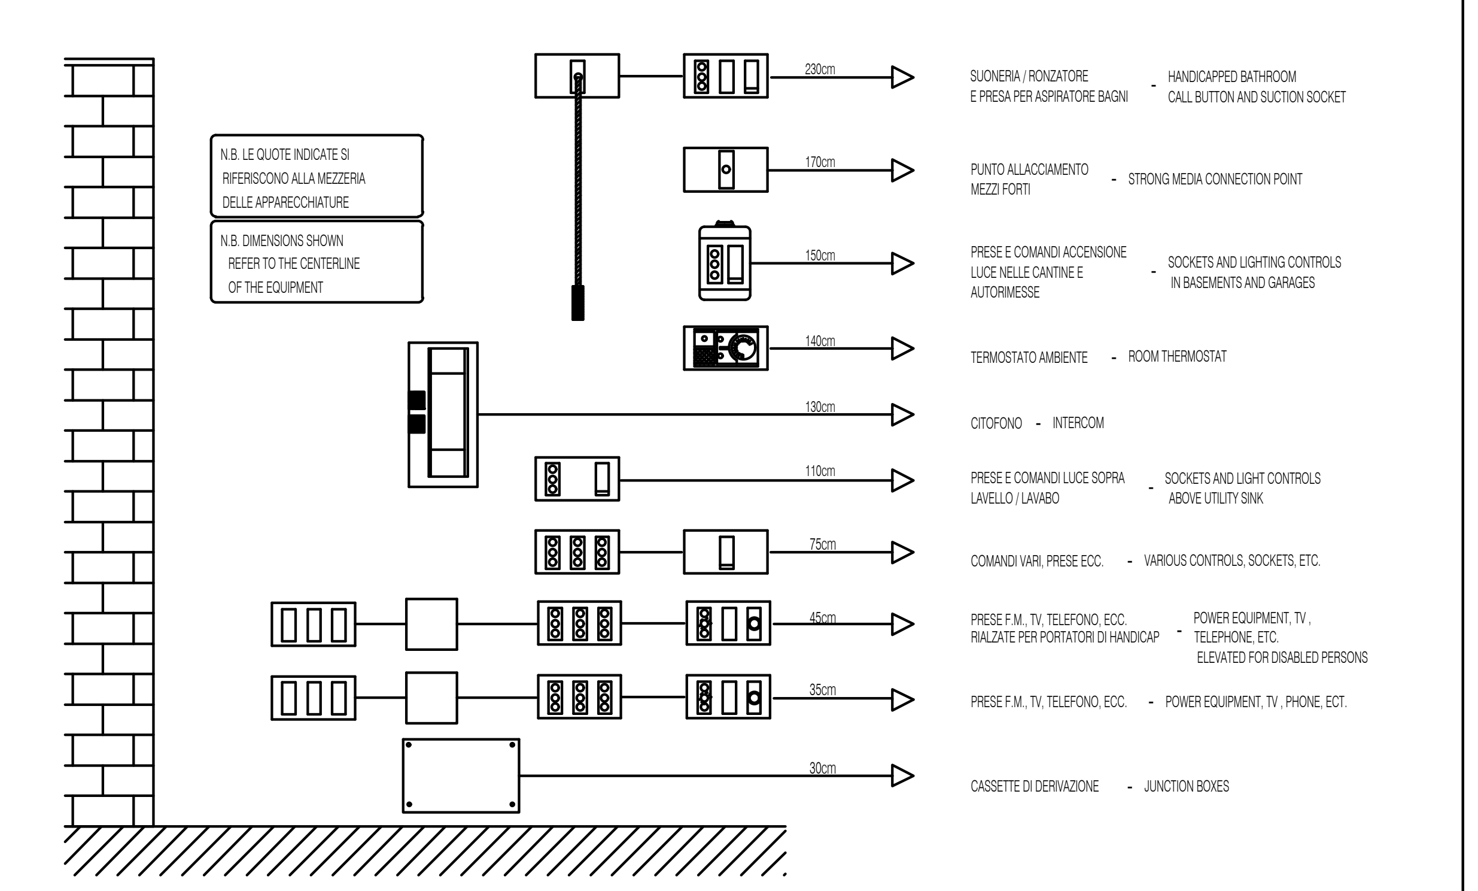
N.B. LE QUOTE INDICATE SI RIFERISCONO ALLA MEZZERIA DELLE APPARECCHIATURE
N.B. DIMENSIONS SHOWN REFER TO THE CENTERLINE OF THE EQUIPMENT
230cm
170cm
150cm
140cm
130cm
110cm
75cm
45cm
35cm
30cm

230cm — SUONERIA / RONZATORE E PRESA PER ASPIRATORE BAGNI - HANDICAPPED BATHROOM CALL BUTTON AND SUCTION SOCKET
170cm — PUNTO ALLACCIAMENTO MEZZI FORTI - STRONG MEDIA CONNECTION POINT
150cm — PRESE E COMANDI ACCENSIONE LUCE NELLE CANTINE E AUTORIMESSE - SOCKETS AND LIGHTING CONTROLS IN BASEMENTS AND GARAGES
140cm — TERMOSTATO AMBIENTE - ROOM THERMOSTAT
130cm — CITOFONO - INTERCOM
110cm — PRESE E COMANDI LUCE SOPRA LAVELLO / LAVABO - SOCKETS AND LIGHT CONTROLS ABOVE UTILITY SINK
75cm — COMANDI VARI, PRESE ECC. - VARIOUS CONTROLS, SOCKETS, ETC.
45cm — PRESE F.M., TV, TELEFONO, ECC. RIALZATE PER PORTATORI DI HANDICAP - POWER EQUIPMENT, TV , TELEPHONE, ETC. ELEVATED FOR DISABLED PERSONS
35cm — PRESE F.M., TV, TELEFONO, ECC. - POWER EQUIPMENT, TV , PHONE, ECT.
30cm — CASSETTE DI DERIVAZIONE - JUNCTION BOXES

**GB&PARTNERS**
SERVIZI E PROGETTI IMMOBILIARI
Via Varalli 37, 26845 Codogno (LO)
Telefono 0377 436099 - 0377 34691 - Fax 0377 436654
E-mail amministrazione@gbepartners.it - tecnico@gbepartners.it
www.gbepartners.it
REGISTRO IMPRESE DI LODI n°05966150962
PARTITA I.V.A / C.F. 05966150962
C.S. € 11.111,10 iv
UNI EN ISO 9001:2015
UNI EN ISO 14001:2015

Progetto impianti

Dabster srl
Via Sommacampagna 63/H - 37137 Verona
P.IVA 04461890230
mail: mail@dabster.it

# COMUNE DI COLOGNO MONZESE (MI)
# AREA Ex TORRIANI ARAS 01
## PROGETTO ESECUTIVO
## Progetto Servizi Abitativi Pubblici di via Pergolesi

Il Progettista

Collegio Provinciale Geometri e Geometri Laureati di Lodi
Iscrizione Albo N. 267
Geometra
Gianpiero Bianchi

CRISTIANO SCHIAVI
421

| N° | DATA | DESCRIZIONE MOTIVAZIONE DELL'AGGIORNAMENTO | STUDIO | DIS. |
|---|---|---|---|---|
| 00 | 16/01/2026 | Prima emissione | G.B.&P. | L.M. |

Progetto
**PROGETTO ESECUTIVO**
***Servizi Abitativi Pubblici***
*Comune di Cologno Monzese(MI)*

Proponente
***Officine Mak S.r.l.***
*Corso Europa, 10*
*Milano 20122*

**Scala**
**1:100**

**Data**
23/01/2026

Tipo tavola
**IMPIANTI**

Serie
**PROGETTO ESECUTIVO**

Titolo
**IMPIANTI ELETTRICI -**
**IMPIANTO DI DISTRIBUZIONE**

Tavola nr.

| | |
|---|---|
| Tipo Tavola | **IMP** |
| Sigla / Serie | **ES** |
| Numero / Variante | **01** |
| Agg. | **00** |

Orientamento
N

Documento di proprietà della Società G.B. & Partners S.r.l.. E' Vietata la riproduzione. Tutti i diritti sono riservati.