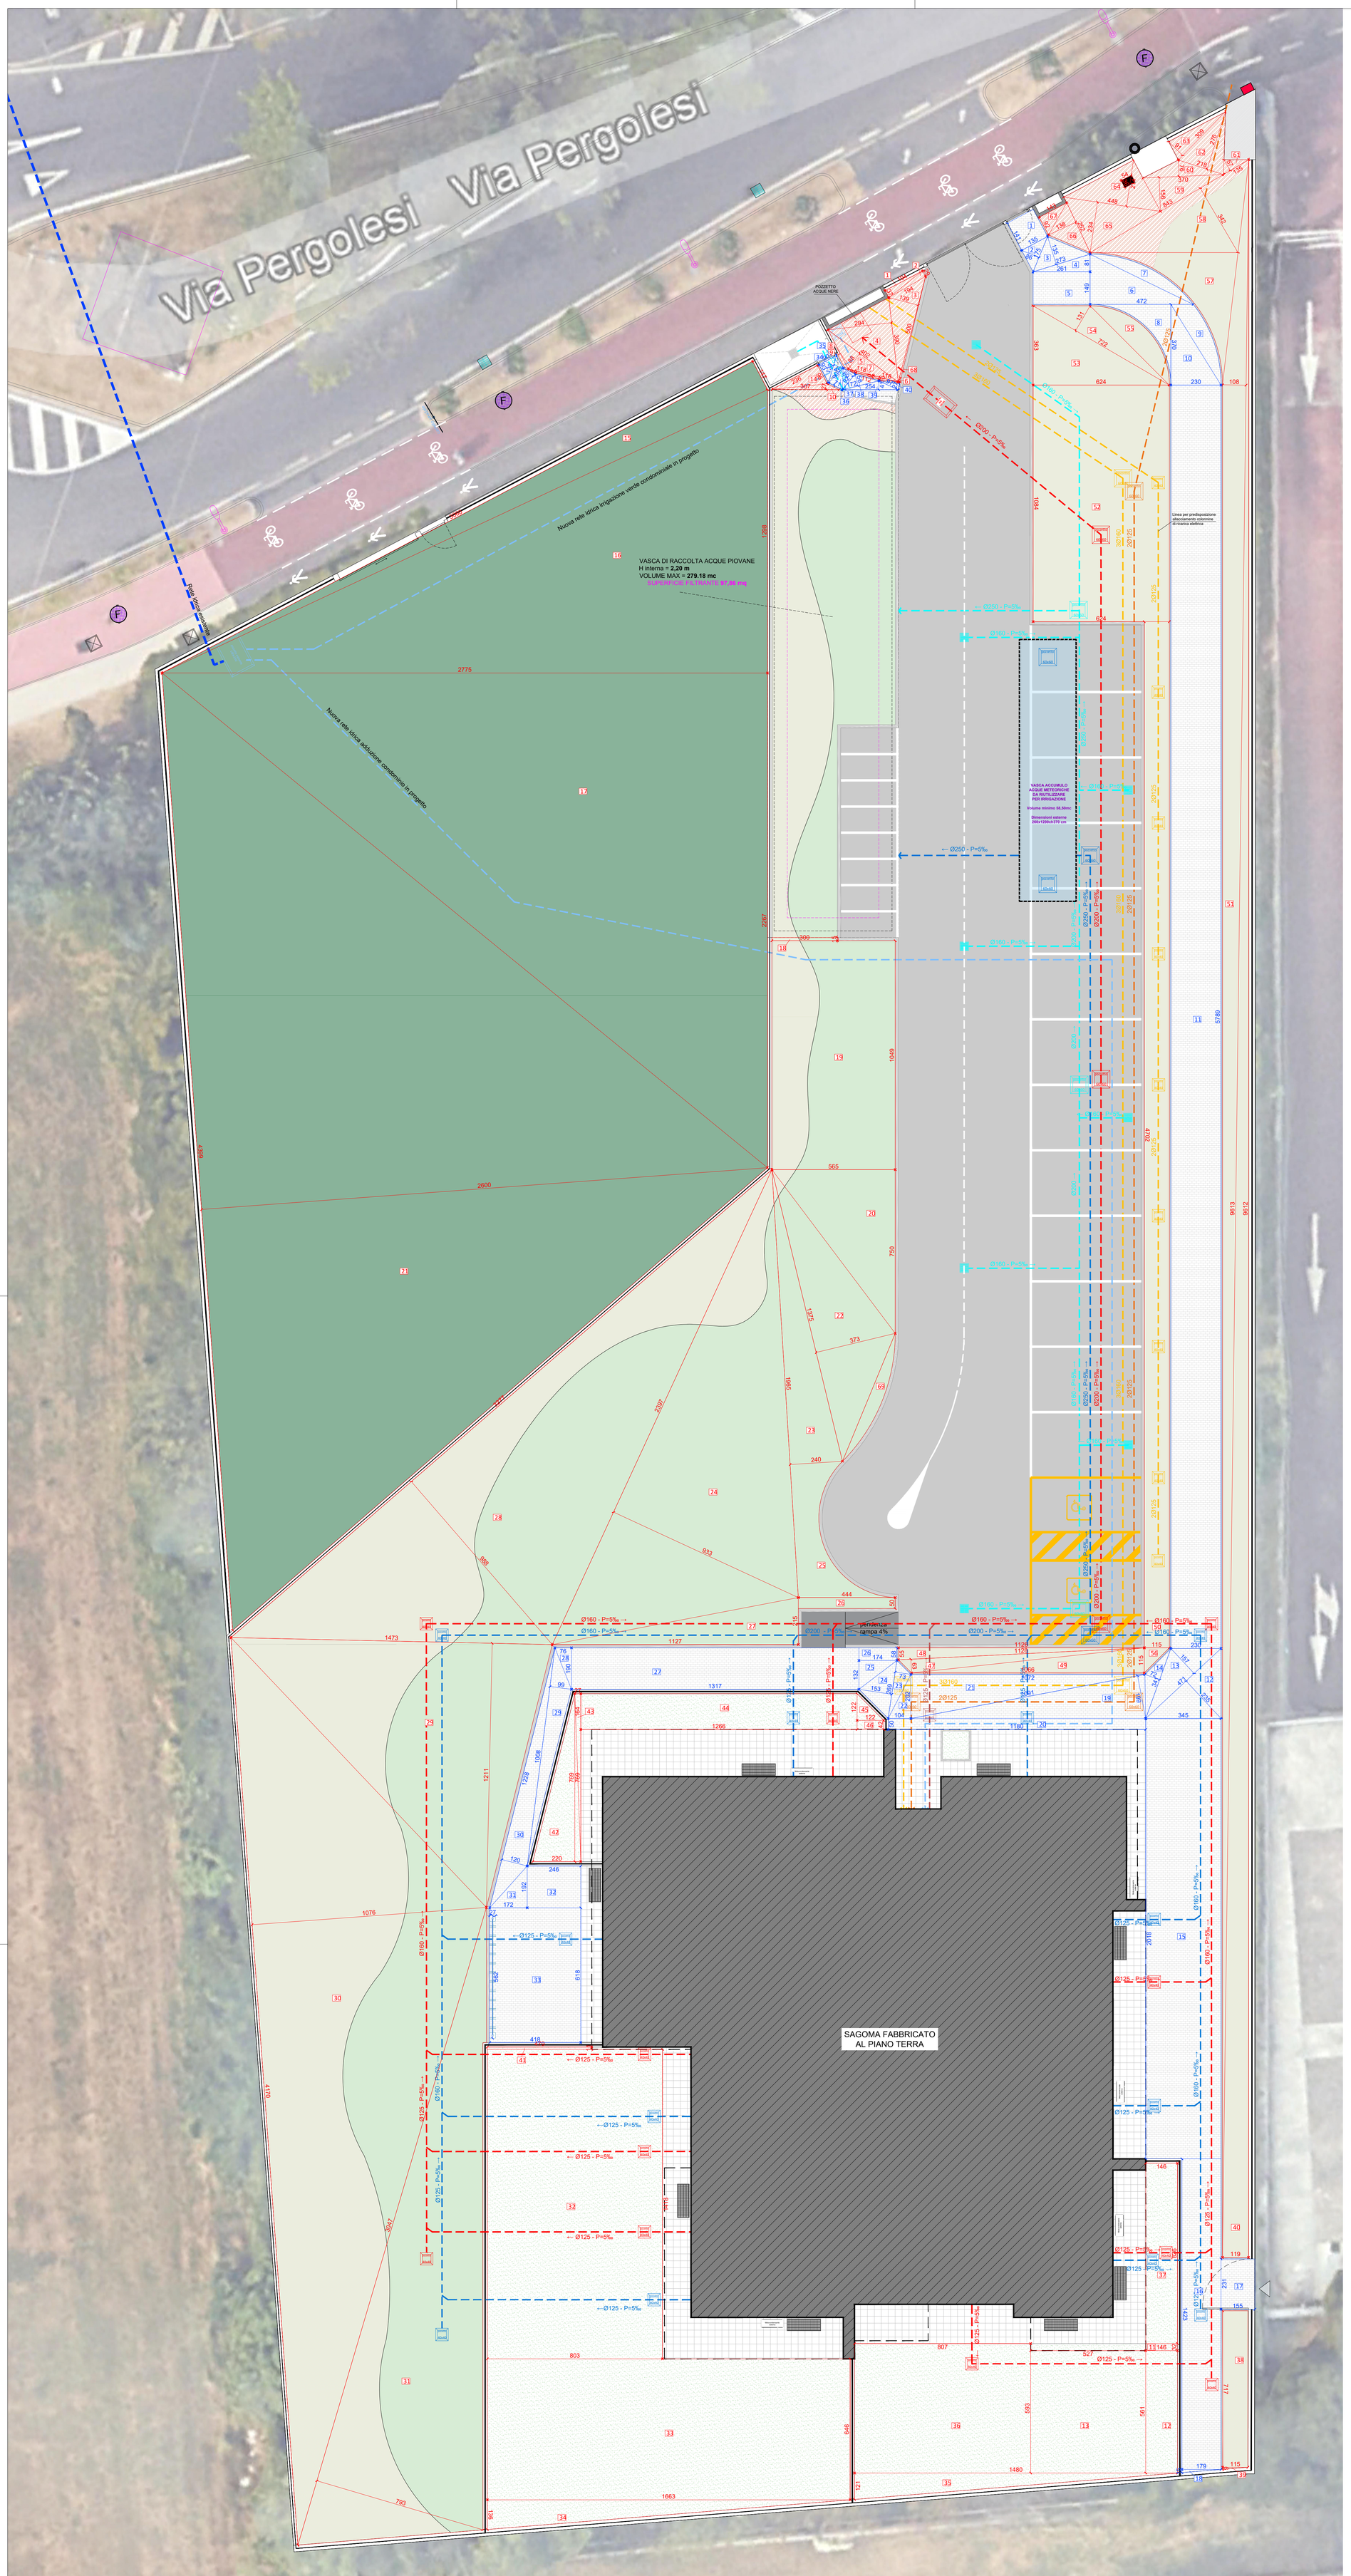


CALCOLO SUPERFICIE DRENANTE				
SUPERFICI DRENANTI A VERDE				
AREA	LUNGHEZZA (m)	LARGHEZZA (m)	ALTEZZA (m)	**TOTALE (mq)**
1	1,94		0,37	**0,36**
2	1,94		0,29	**0,28**
3	5,00		1,39	**3,48**
4	3,90		2,94	**5,73**
5	4,02		0,88	**1,77**
6	1,18		0,10	**0,06**
7	1,12		0,09	**0,05**
8	1,18		0,08	**0,05**
9	dedotto da autocad			**0,09**
10	3,07		0,27	**0,41**
11	1,46	0,32		**0,47**
12	1,46	5,61		**8,19**
13	5,27	5,61		**29,56**
14	2,36		0,96	**1,13**
15	30,60		1,47	**22,49**
16	27,75		12,98	**180,10**
17	27,75		22,67	**314,55**
18	3,00	0,15		**0,45**
19	5,65	10,49		**59,27**
20	5,65		7,50	**21,19**
21	43,99		26,00	**571,87**
22	13,75		3,73	**25,64**
23	13,54		2,40	**16,25**
24	23,97		9,33	**111,82**
25	dedotto da autocad			**10,60**
26	4,44	0,50		**2,22**
27	11,27		2,15	**12,12**
28	32,77		9,88	**161,88**
29	14,73		12,11	**89,19**
30	41,70		10,76	**224,35**
31	30,47		7,93	**120,81**
32	8,03	14,18		**113,87**
33	16,63	6,46		**107,43**
34	16,63		1,36	**11,31**
35	14,80		1,21	**8,95**
36	8,07	5,93		**47,86**
37	1,46	8,26		**12,06**
38	1,15	7,17		**8,25**
39	1,15		0,09	**0,05**
40	1,19		96,12	**57,19**
41	4,79	0,11		**0,53**
42	2,20		7,69	**8,46**
43	0,27		7,69	**1,04**
44	12,66	1,64		**20,76**
45	1,22		1,22	**0,74**
46	1,22	0,42		**0,51**
47	11,28		0,63	**3,55**
48	11,26		0,55	**3,10**
49	10,66		1,15	**6,13**
50	1,15	47,02		**54,07**
51	96,13		1,08	**51,91**
52	6,24	10,84		**67,64**
53	6,24		3,63	**11,33**
54	7,22		1,31	**4,73**
55	dedotto da autocad			**3,76**
56	1,15		1,15	**0,66**
57	dedotto da autocad			**10,05**
58	8,43		3,42	**14,42**
59	3,70		1,56	**2,89**
60	3,70		0,76	**1,41**
61	1,35		0,57	**0,38**
62	2,18		2,76	**3,01**
63	3,09		0,91	**1,41**
64	4,48		2,14	**4,79**
65	4,48		2,34	**5,24**
66	2,52		1,38	**1,74**
67	1,43		0,92	**0,66**
68	5,00		0,07	**0,18**
69	dedotto da autocad			**2,68**
			TOTALE	**2.651,15**

SUPERFICI DRENANTI PAVIMENTATE				
AREA	LUNGHEZZA (m)	LARGHEZZA (m)	ALTEZZA (m)	**TOTALE (mq)**
1	1,41	1,35		**1,90**
2	1,75		0,86	**0,75**
3	2,73		1,35	**1,84**
4	2,61		0,81	**1,06**
5	2,61	1,49		**3,89**
6	4,72		2,30	**5,43**
7	dedotto da autocad			**2,14**
8	dedotto da autocad			**2,95**
9	dedotto da autocad			**2,76**
10	2,30		3,70	**4,26**
11	2,30	57,89		**133,15**
12	4,71		2,35	**5,53**
13	4,71		1,57	**3,70**
14	3,41		0,72	**1,23**
15	3,45	20,18		**69,62**
16	1,79	14,23		**25,47**
17	1,55	2,31		**3,58**
18	1,79		0,15	**0,13**
19	10,91		1,99	**10,86**
20	11,80	0,50		**5,90**
21	10,72	2,02		**21,65**
22	1,04		2,02	**1,05**
23	2,69		0,73	**0,98**
24	2,69		1,53	**2,06**
25	1,74		1,32	**1,15**
26	1,74	0,58		**1,01**
27	13,17	1,90		**25,02**
28	0,76		1,90	**0,72**
29	10,08		0,99	**4,99**
30	12,28		1,20	**7,37**
31	1,72		1,92	**1,65**
32	2,46	1,92		**4,72**
33	4,18	6,18		**25,83**
34	0,90		0,93	**0,42**
35	1,30		0,45	**0,29**
36	0,71		0,90	**0,32**
37	0,92		0,60	**0,28**
38	1,72		0,56	**0,48**
39	2,54		0,41	**0,52**
40	0,97		0,27	**0,13**
			TOTALE	**386,80**

AREE DA DEDURRE				
AREA	LUNGHEZZA (m)	LARGHEZZA (m)	QUANTITA'	**TOTALE (mq)**
Colonnina Siptel	0,54	0,36	1	**0,19**
Pozzetti 40x40	0,57	0,57	33	**10,72**
Pozzetti 60x60	0,81	0,81	8	**5,25**
Pozzetto 100x100	1,17	1,17	1	**1,37**
Pozzetto esistente 100x150	1,17	1,67	1	**1,95**
Rastelliera deposito bici	0,27	5,62	1	**1,52**
			TOTALE	**21,01**

TOTALI	
TOTALE SUPERFICI DRENANTI A VERDE	**2.651,15**
TOTALE SUPERFICI DRENANTI PAVIMENTATE	**386,80**
TOTALE SUPERFICI DA DEDURRE	**21,01**
TOTALE SUPERFICI DRENANTI	**3.016,94**

N.B.
La superficie drenante totale, così come calcolata, tiene in considerazione esclusivamente le superfici di verde profondo e le superfici di pavimentazione drenante in autobloccanti, comunque non coperte da aggetti o coperture di alcun tipo.
Nel conteggio non è stata considerata la porzione di area a verde posta al di sopra della vasca di dispersione, in quanto non identificabile come superficie a verde profondo.
Nella tabella delle deduzioni sono invece indicate le diverse riduzioni relative ai manufatti che insistono al di sopra delle superfici drenanti sopra elencate.

Superficie territoriale catastale = 4.649 mq
Superficie drenante totale= 3.016,94 mq

4.649 mq x 0,6 = 2.789,40 mq
3.016,94 mq > 2.789,40 mq

Superficie drenante totale > 60% Superficie territoriale catastale
VERIFICATO

GB&PARTNERS
SERVIZI E PROGETTI IMMOBILIARI
Via Vittorio Veneto 37, 26845 Codogno (LO)
Telefono 0377 430691 0377 34491 Fax 0377 436654
E-mail amministrazione@gbepartners.it tecnico@gbepartners.it
www.gbepartners.it
REGIONE IMPRESE DI LODI Iscrizione n. 109423
PARTITA IVA / C.F. 10944120962
R.E.A. MI-1787004

Il Progettista

Collegio Provinciale Geometri e Geometri Laureati di Lodi
Iscrizione Albo n. 421
Geometra Gianpiero Bianchi

Il Direttore Lavori

Il Committente

COMUNE DI COLOGNO MONZESE (MI)
AREA Ex TORRIANI ARAS 01
PROGETTO ESECUTIVO
Progetto Servizi Abitativi Pubblici di via Pergolesi

N°	DATA	DESCRIZIONE MOTIVAZIONE DELL'AGGIORNAMENTO	STUDIO	DIS.
00	30/01/2026	Prima emissione	G.B.&P.	L.M.

Progetto
PROGETTO ESECUTIVO
Servizi Abitativi Pubblici
Comune di Cologno Monzese(MI)

Proponente
Officine Mak S.r.l.
Corso Europa, 10
Milano 20122

Scala
1:100

Data
30/01/2026

Tipo tavola
ARCHITETTONICI

Serie
PROGETTO ESECUTIVO

Titolo
VERIFICA SUPERFICIE DRENANTE

Tavola nr.

Tipo Tavola	**ARCH**
Sigla / Serie	**ES**
Numero / Variante	**22**
Agg.	**00**

Orientamento
N

Documento di proprietà della Società G.B. & Partners S.r.l.. E' Vietata la riproduzione. Tutti i diritti sono riservati.