


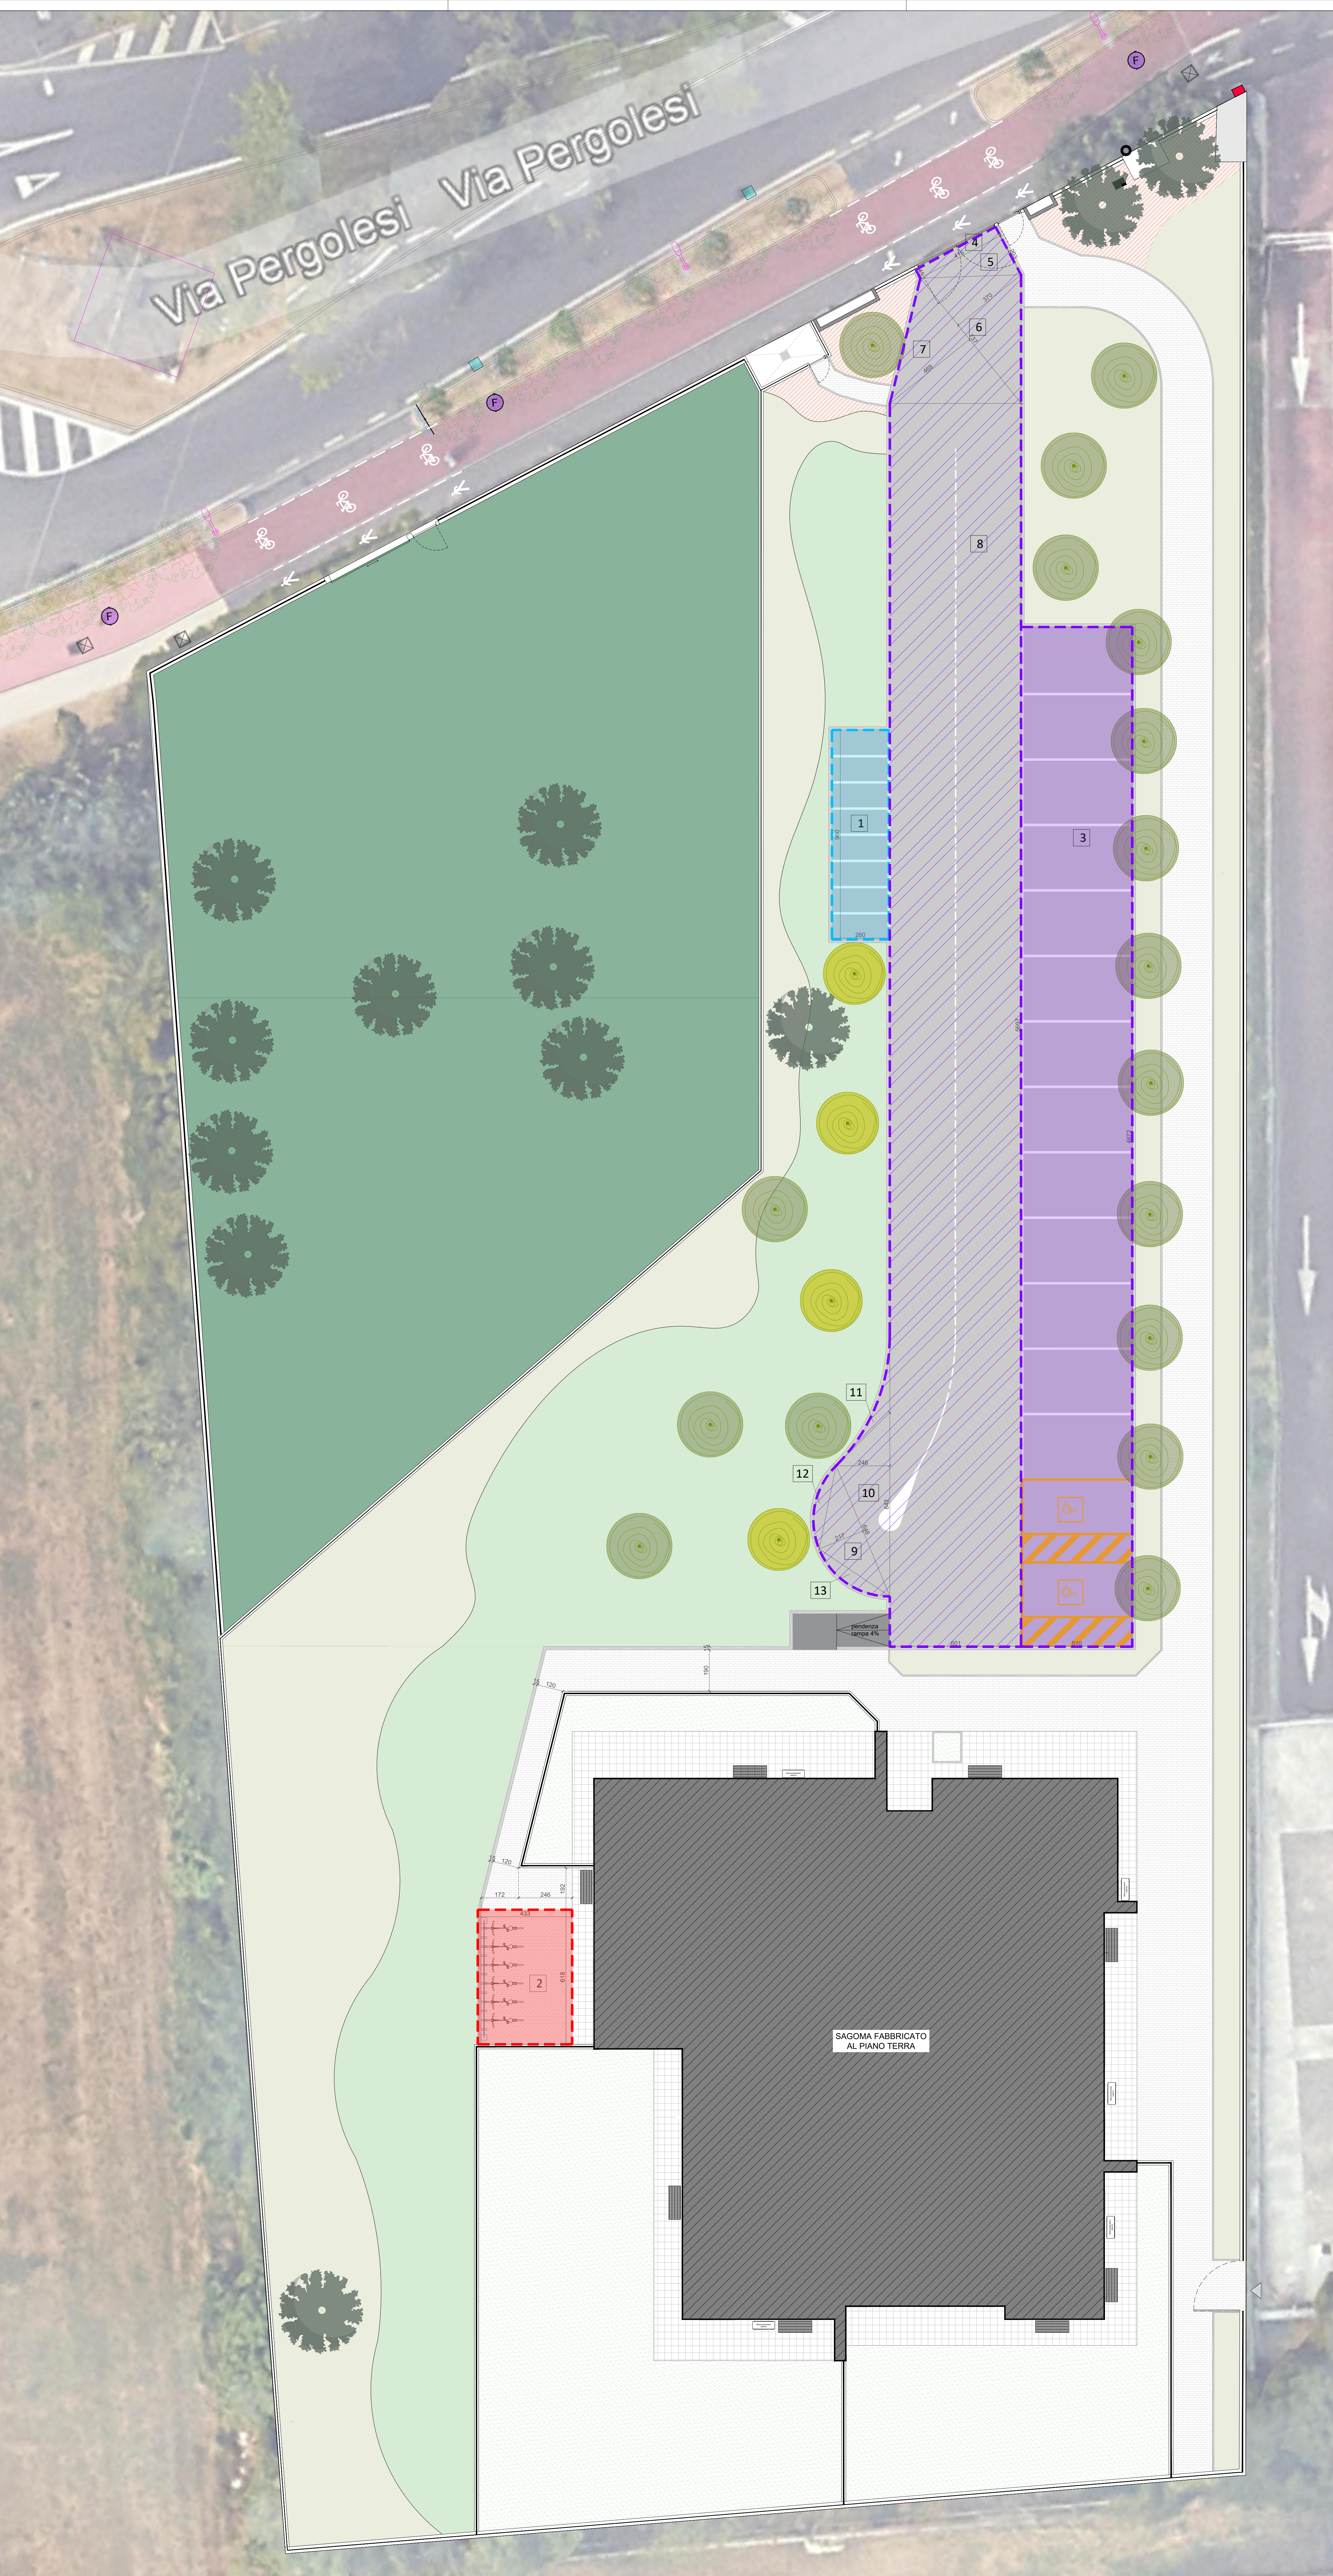

CALCOLO PARCHEGGI PRIVATI MOTO				
PARCHEGGI				
POLIGONO	b (m)	h (m)	mq	totale
1	2,6	9,6	24,96	24,96

CALCOLO PARCHEGGI PRIVATI PERTINENZIALI				
PARCHEGGI PRIVATI PERTINENZIALI				
POLIGONO	b (m)	h (m)	mq	totale
3	5,10	46,72	238,27	238,27
AREA DI MANOVRA				
4	4,15	0,45	1,87	401,49
5	4,15	2,03	4,21	
6	7,37	3,70	13,63	
7	7,37	4,69	17,28	
8	6,01	56,97	342,39	
9	6,48	2,17	7,03	
10	8,42	2,46	10,36	
11	dedotto da autocad		1,58	
12	dedotto da autocad		1,57	
13	dedotto da autocad		1,57	
				639,77

CALCOLO SPAZIO PARCHEGGIO BICI				
POLIGONO	b (m)	h (m)	mq	totale
2	4,33	6,18	26,76	26,76

VERIFICA PARCHEGGI PRIVATI PERTINENZIALI					
		Parcheggi pertinenziali privati minimi da garantire (mq)	parcheggi pertinenziali privati da progettare (mq)		
Superfici e Lorda (mq)	Volume Urbanistico (mq)	PdR_NTA_Art. 26 comma 2, comma 3			
797,87	2.632,97	PdR_NTA_Art. 26 comma 2 - Parcheggi privati uso residenziale 1,00 mq ogni 10 mc e comunque non inferiori ad un posto auto per alloggio	263,30	Parcheggi privati da progetto	444,73
			263,30	<	444,73
				VERIFICATO	
		PdR_NTA_Art. 26 comma 2 - un posto auto per ogni alloggio. Posti auto minimi	13,00	n. posti auto da progetto	15,00
			13,00	<	15,00
				VERIFICATO	
		PdR_NTA_Art. 26 comma 3 - Spazi sosta per il parcheggio di biciclette 10 % degli spazi di sosta minimi	26,33	spazio sosta biciclette da progetto	26,76
			26,33	<	26,76
				VERIFICATO	

LEGENDA	
	SPAZI DI SOSTA PER IL PARCHEGGIO DI BICICLETTE
	CORSIA DI MANOVRA (inclusa nel calcolo dei parcheggi pertinenziali ai sensi delle NTA_PdR_Art. 26 comma4)
	PARCHEGGI PERTINENZIALI
	PARCHEGGI MOTO

GB&PARTNERS
SERVIZI E PROGETTI IMMOBILIARI
10121 Milano - Via Montenapoleone, 12
Tel. +39 02 7600 1111 - Fax +39 02 7600 1112
E-mail: gb@gbpartners.it
Pec: gbpartners@pec.it
Sede Legale: Via Montenapoleone, 12 - 20121 Milano
Sede Operativa: Via Montenapoleone, 12 - 20121 Milano

COMUNE DI COLOGNO MONZESE (MI)
AREA Ex TORRIANI ARAS 01
PROGETTO ESECUTIVO
Progetto Servizi Abitativi Pubblici di via Pergolesi

N°	DATA	DESCRIZIONE MOTIVAZIONE DELL'AGGIORNAMENTO	STUDIO	DIS.
00	30/01/2026	Prima emissione	G.B.&P.	L.M.

Progetto	Proponente	Scala
PROGETTO ESECUTIVO	Officine Mak S.r.l. Corso Europa, 10 Milano 20122	1:100
Servizi Abitativi Pubblici Comune di Cologno Monze (MI)		Data 30/01/2026

Tipo tavola	Tavola nr.
ARCHITETTONICI	ARCH
Serie	Sigla / Serie
PROGETTO ESECUTIVO	ES
Titolo	Numero / Variante
VERIFICHE PLANIVOLUMETRICHE	24
Verifica parcheggi privati pertinenziali e spazi di sosta per il parcheggio di biciclette	Pg: 00

Il Progettista

Il Direttore Lavori

Il Committente

Orientamento