
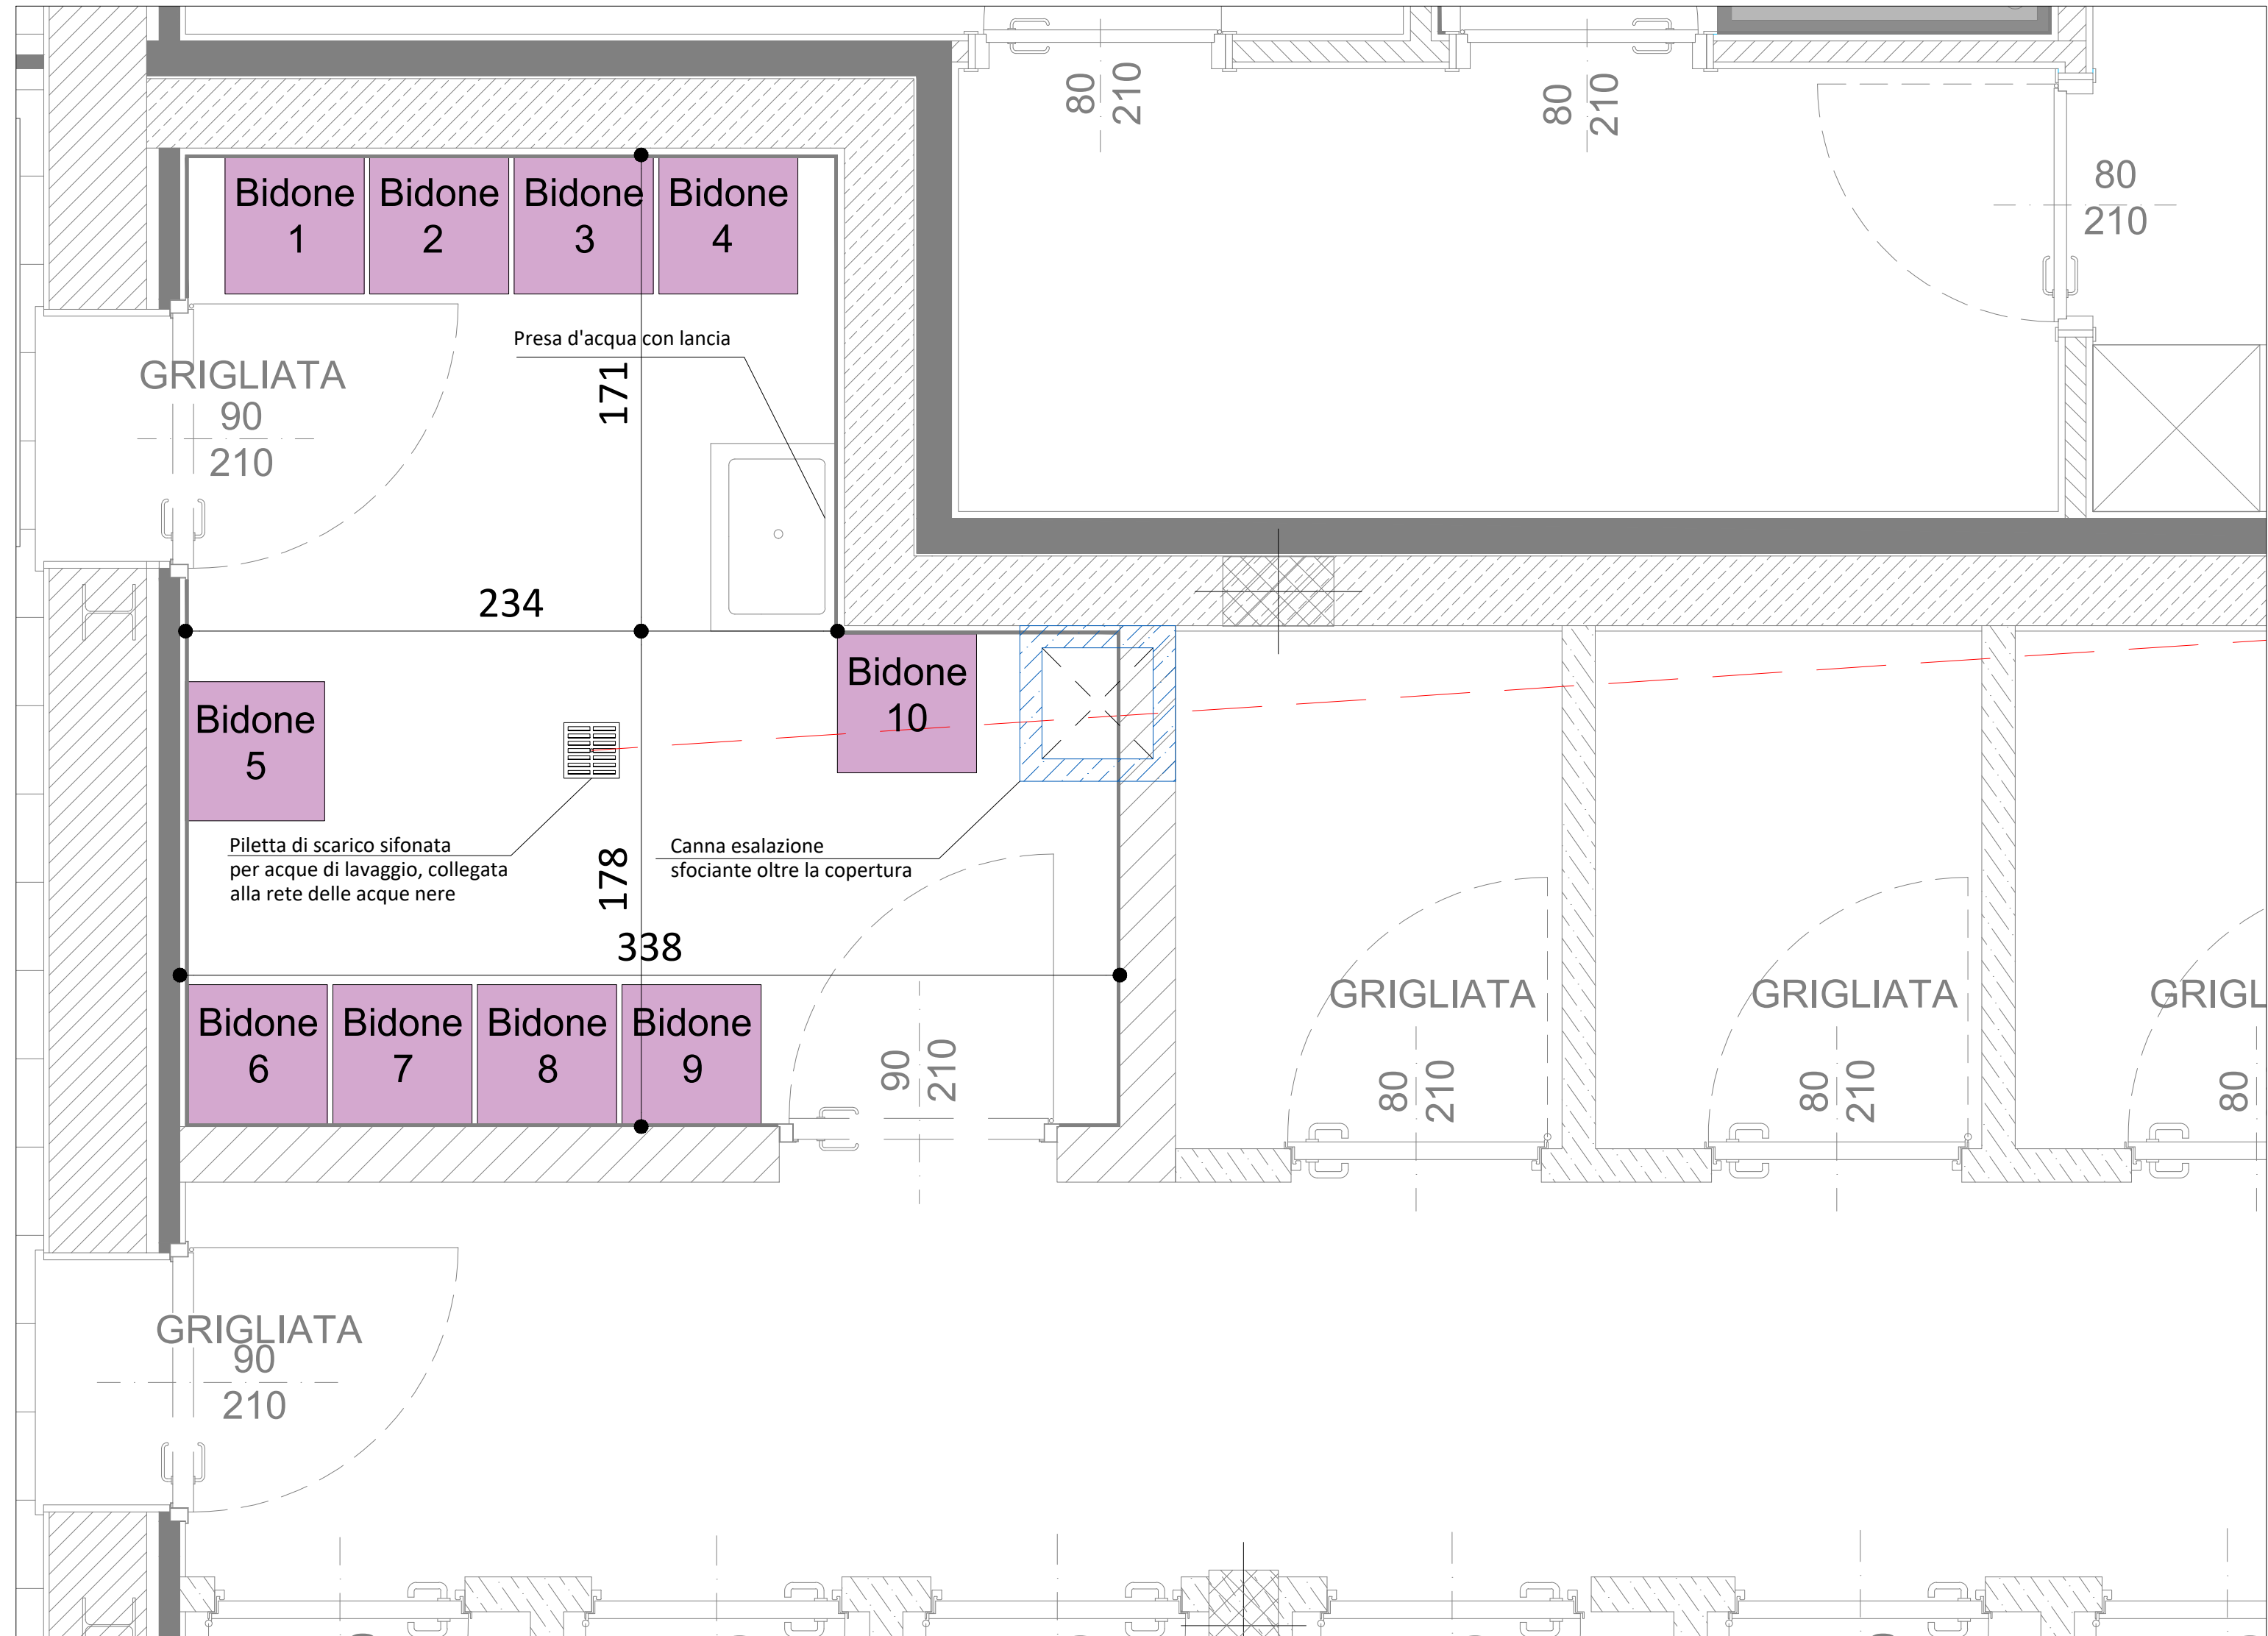


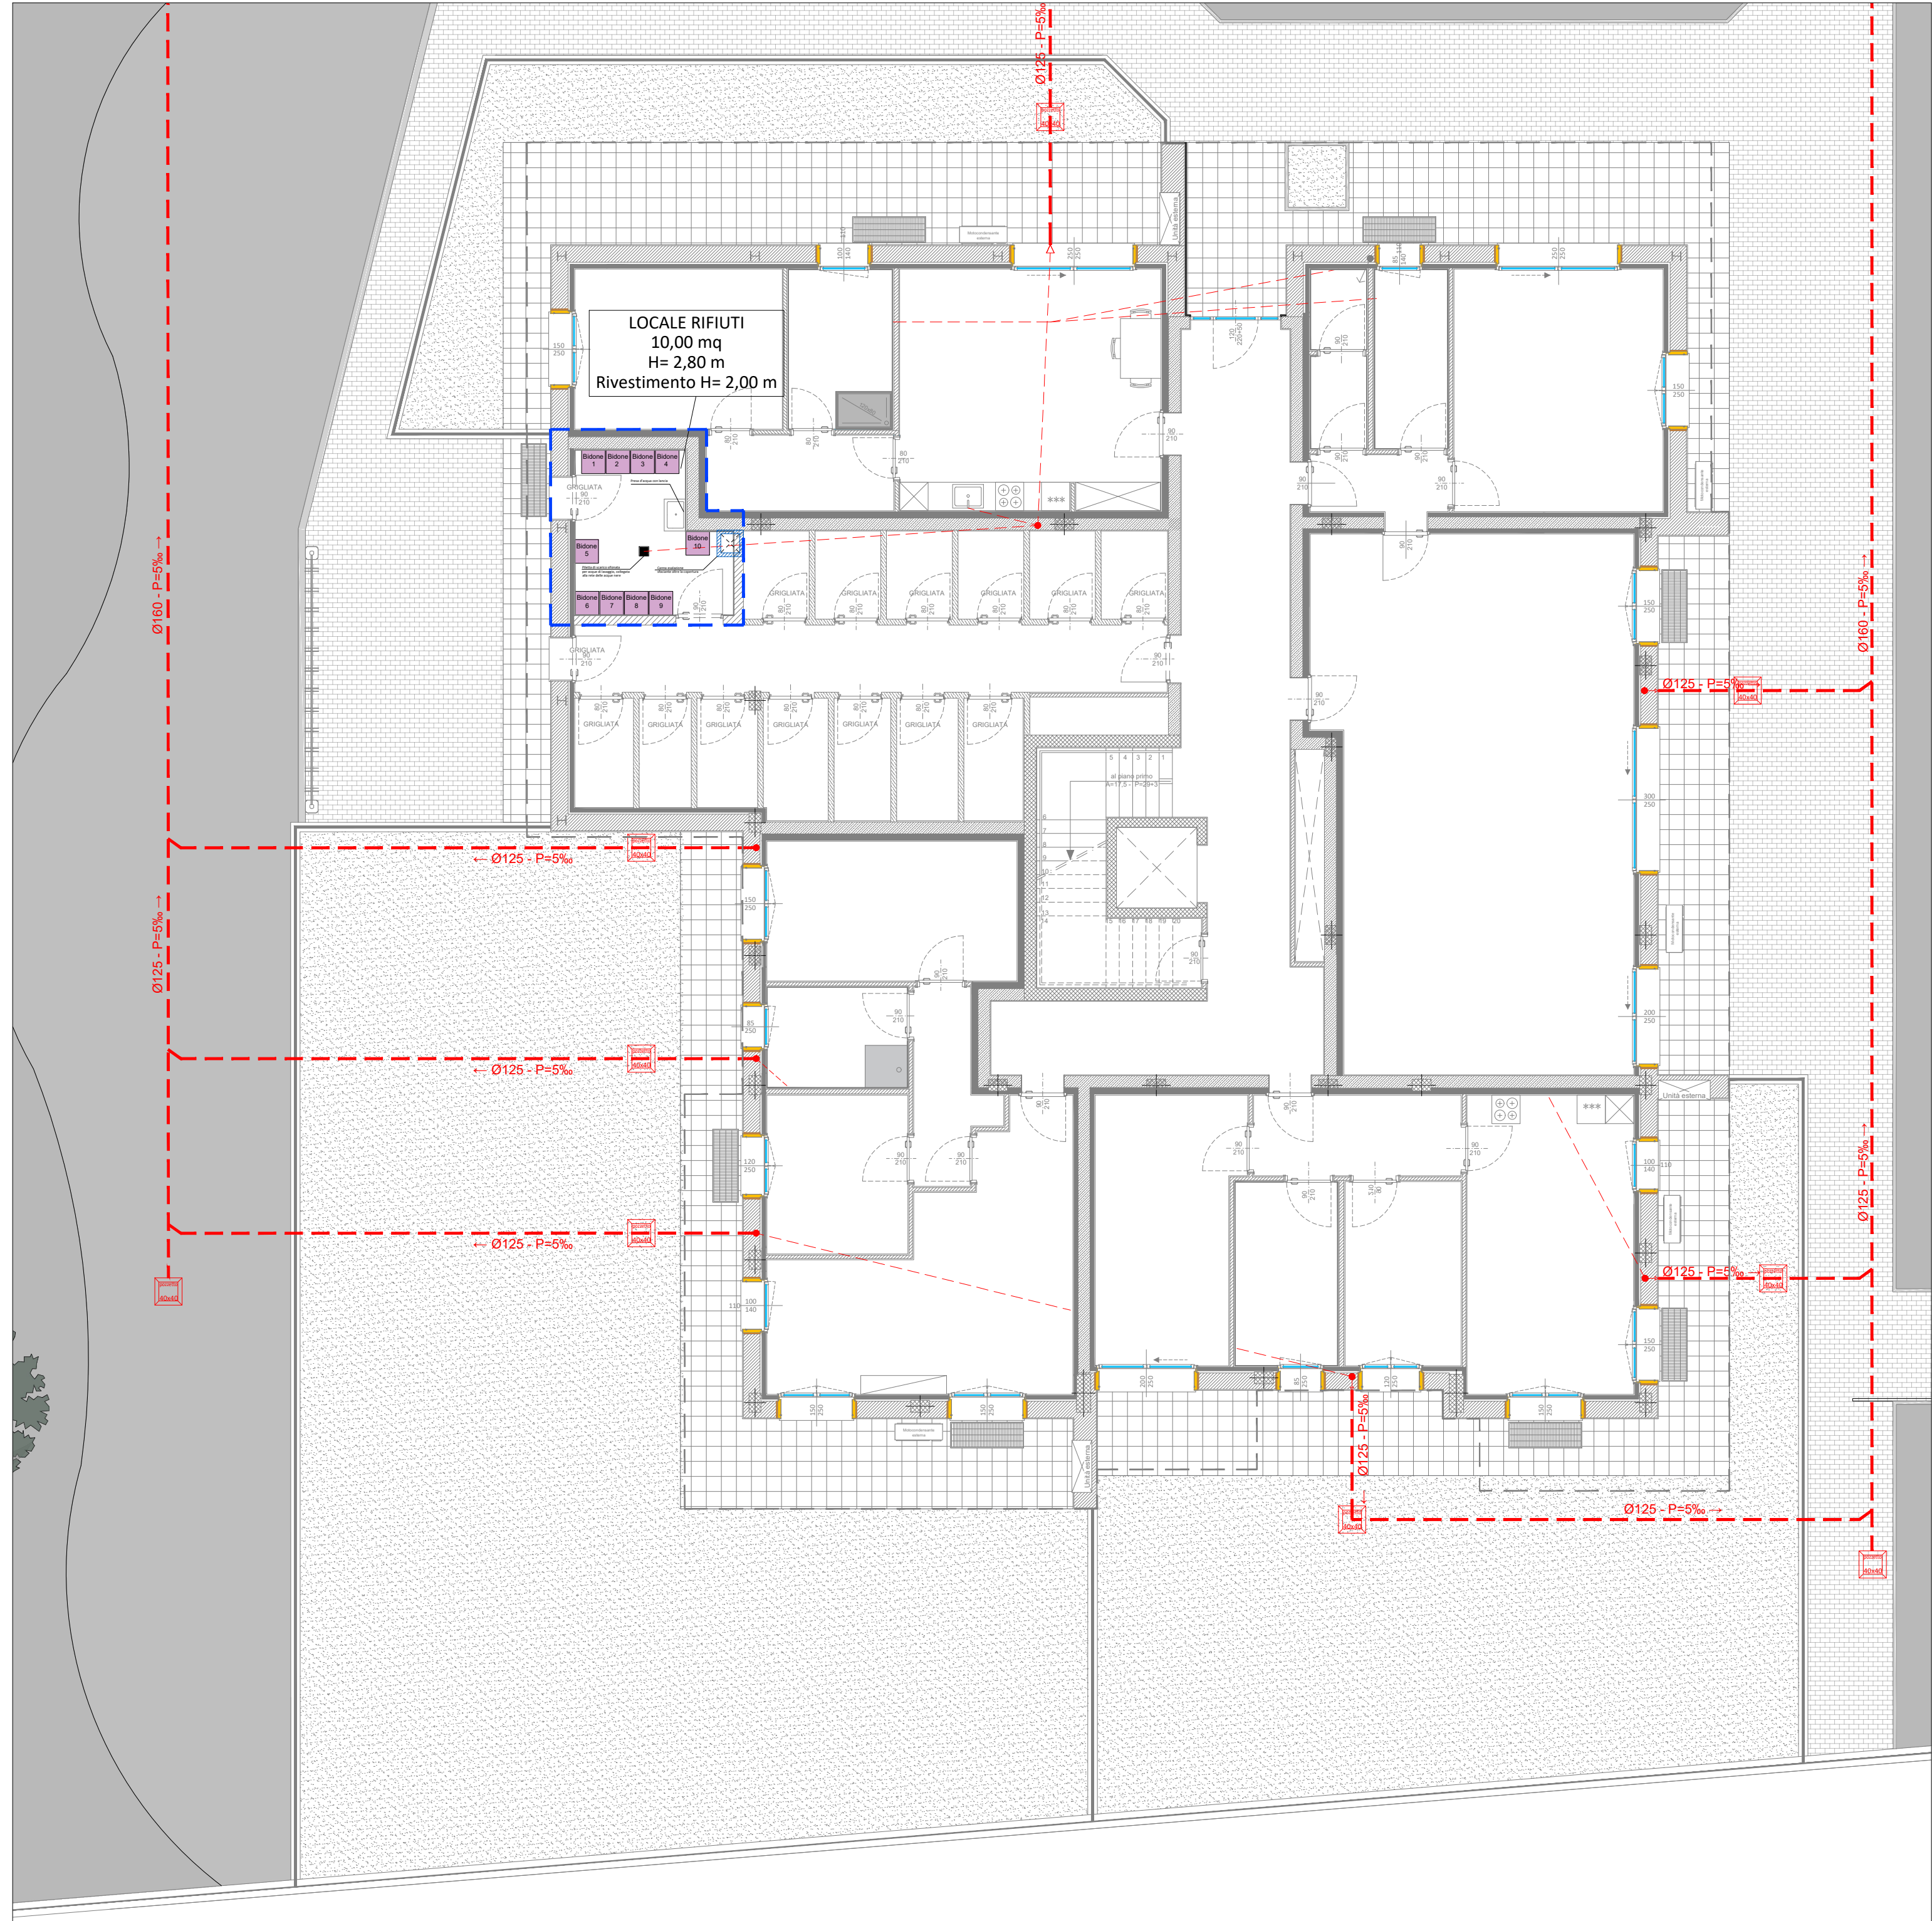

[]

Locale rifiuti

Rete acque nere

VERIFICA REQUISITI LOCALE IMMONDEZZAIO (rif. R.E./art.68)

a) Prevedere almeno un contenitore da 240 lt, di dimensioni indicative di m 0,50 x 0,50, per ogni tipologia di rifiuto ogni 20 abitanti insediabili/residenti con una superficie indicativa di 0,20 mq per abitante teorico

Ab. teorici = 28

01. VERIFICA SUPERFICIE MINIMA

28 a.t. x 0,20 mq. = 5,60 mq
DA PROGETTO = 10,00 mq
10,00 mq > 5,60 mq

VERIFICATO

02. VERIFICA BIDONNI

1 bidone per umido da 240 lt
1 bidone per plastica da 240 lt
1 bidone per carta da 240 lt
1 bidone per secco da 240 lt
1 bidone per vetro e lattine da 240 lt

ogni 20 abitanti teorici

5 bidoni 0,50x0,50 da 240 lt ogni 20 ab. teorici

Quindi: $28 \text{ a.t.} : 20 = 1,4$

Bidoni necessari = $1,4 \times 5 = 7$ bidoni minimo

Bidoni in progetto = 10
VERIFICATO

b) altezza minima interna di m. 2,40.

VERIFICATO

c) Porta metallica a tenuta dimensioni minime di m 0,90 x 2,10

VERIFICATO

d) pavimento e pareti con raccordi arrotondati e costituiti da materiale liscio, facilmente lavabile e impermeabile (piastrelle di ceramica gres) per un'altezza minima di m. 2,00.
VERIFICATO

VERIFICATO

e) essere dotati di apposita canna di esalazione sfociante oltre la copertura

VERIFICATO

f) essere dotati di una presa d'acqua con relativa lancia per il lavaggio con presenza di scarichi regolarmente sifonati per l'acqua di lavaggio collegata alla rete delle acque nere
VERIFICATO

VERIFICATO

g) garantire idonee misure di prevenzione e di difesa antimurine e antinsetti

VERIFICATO

h) se esterni , a cielo libero, essere ubicati ad una corretta distanza dai più vicini locali di abitazione e comunque non inferiori a m. 10,00 dalle pareti finestrate.

[illegible]