



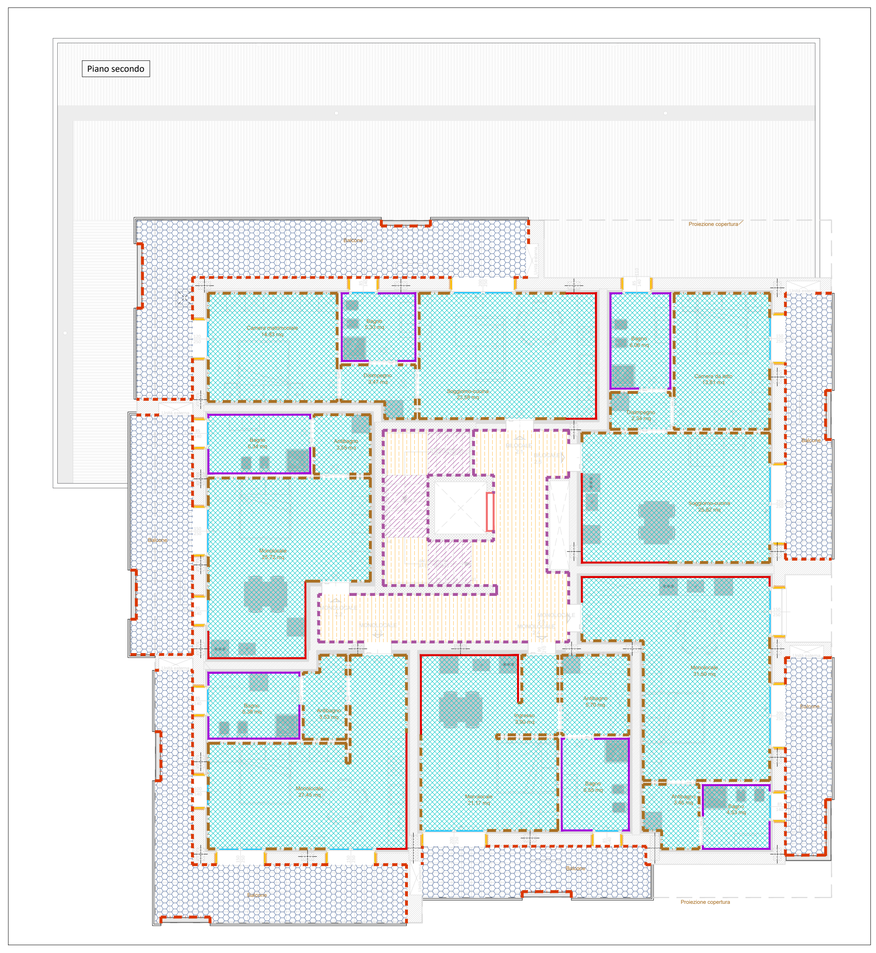

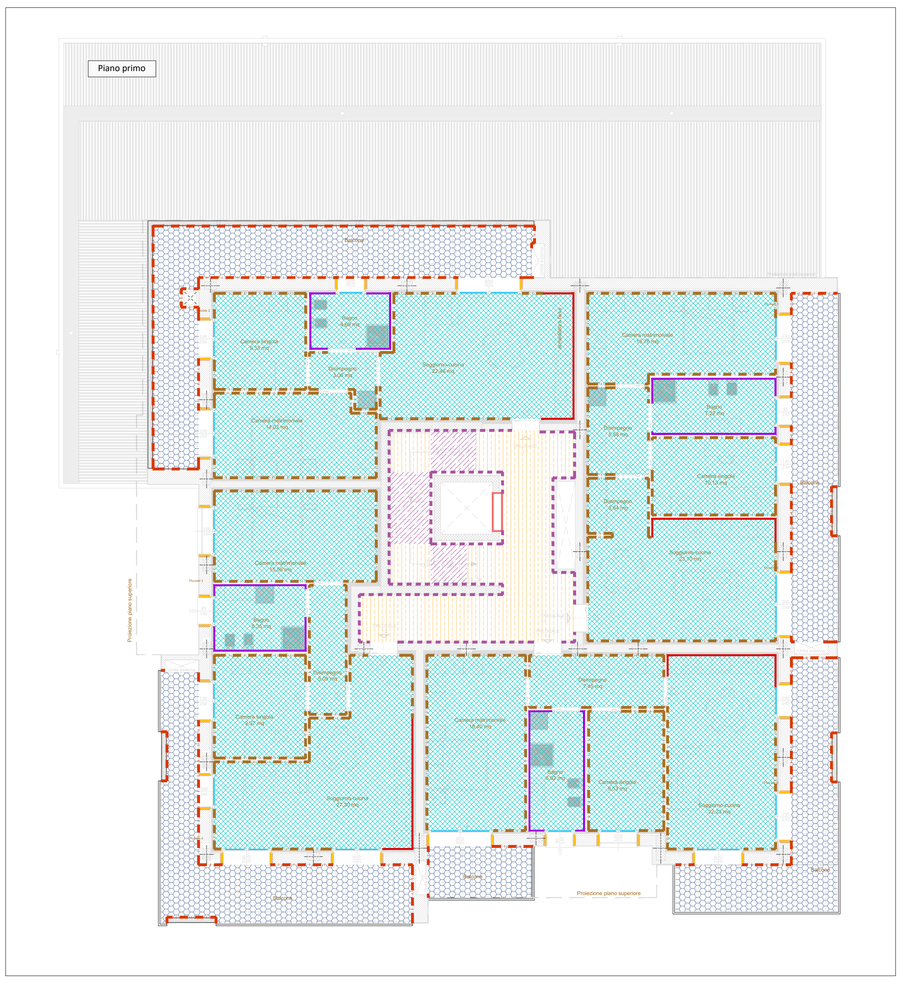

LEGENDA

	Pavimento in autobloccanti filtranti (permeabilità 100%)
	Pavimentazione in asfalto sp. 3cm
	Pedata e alzata in serizzo antigorio con finitura levigata posato a malta. Alzata sp. 2cm, pedata sp. 3 cm
	Pavimento in serizzo antigorio finitura levigata sp. 2 cm incollato su sottofondo in sabbia e cemento
	Pavimento in piastrelle di gres porcellanato, formato 30x30cm, sp. 8-10 cm, incollato su sottofondo, posato con fuga 2mm
	Pavimento in piastrelle di gres fine porcellanato, formato 30x60cm, sp. 8-10 cm, incollato su sottofondo, posato con fuga 2mm
	Pavimento in gres fine porcellanato da esterno (R11), formato 30x60cm, sp. 8-10mm, incollato su sottofondo, posato con fuga 3mm
	Battiscopa in serizzo antigorio finitura levigata, incollato, h. 8 cm sp. 1 cm
	Battiscopa in gres fine porcellanato da esterno (R11), incollato, h. 15 cm, completo di profili in alluminio
	Battiscopa in gres fine porcellanato da esterno (R11), incollato, h. 60 cm, completo di profili in alluminio
	Battiscopa in legno, inchiodato, 80x10 mm, colore in abbinamento alle porte interne
	Rivestimento h 2,00 m con materiale liscio, impermeabile, con superficie facilmente lavabile, con raccordo arrotondato con il pavimento e le pareti
	Rivestimento cucina in gres porcellanato, formato 30x60cm, sp. 8-10 mm, incollato, possato con fuga 2mm h=1.60mt
	Rivestimento bagni in gres porcellanato, formato 30x60cm, sp. 8-10 mm, incollato, possato con fuga 2mm, h= 2,40mt
	Rivestimento porta ascensore in serizzo antigorio con finitura levigata
	Rivestimento in pietra ricostruita a tutta altezza area ingresso

GB&PARTNERS
SERVIZI E PROGETTI IMMOBILIARI
Via Volontà 37, 26845 Codogno (LO)
Telefono 0377 436099 - 0377 34491 **Fax** 0377 436654
E-mail ordine.ingegneri@gbepartners.it tecnico@gbepartners.it
www.gbepartners.it
REGISTRO IMPRESE DI LODI
PARTITA IVA / C.F.
R.E.A.

Il Progettista

Collegio Provinciale Geometri e Geometri Laureati di Lodi — Iscrizione Albo n. 421 — Geometra Gianpiero Bianchi

Il Direttore Lavori

Il Committente

COMUNE DI COLOGNO MONZESE (MI)
AREA Ex TORRIANI ARAS 01
PROGETTO ESECUTIVO
Progetto Servizi Abitativi Pubblici di via Pergolesi

N°	DATA	DESCRIZIONE MOTIVAZIONE DELL'AGGIORNAMENTO	STUDIO	DIS.
00	30/01/2026	Prima emissione	G.B.&P.	L.M.

Progetto
PROGETTO ESECUTIVO
Servizi Abitativi Pubblici
Comune di Cologno Monzese(MI)

Proponente
Officine Mak S.r.l.
Corso Europa, 10
Milano 20122

Scala
1:100

Data
30/01/2026

Tipo tavola
ARCHITETTONICI

Serie
PROGETTO ESECUTIVO

Titolo
ABACO PAVIMENTI E RIVESTIMENTI

Tavola nr.

Tipo Tavola	**ARCH**
Sigla / Serie	**ES**
Numero / Variante	**13**
Agg.	**00**

Orientamento

Documento di proprietà della Società G.B. & Partners S.r.l.. E' Vietata la riproduzione. Tutti i diritti sono riservati.