
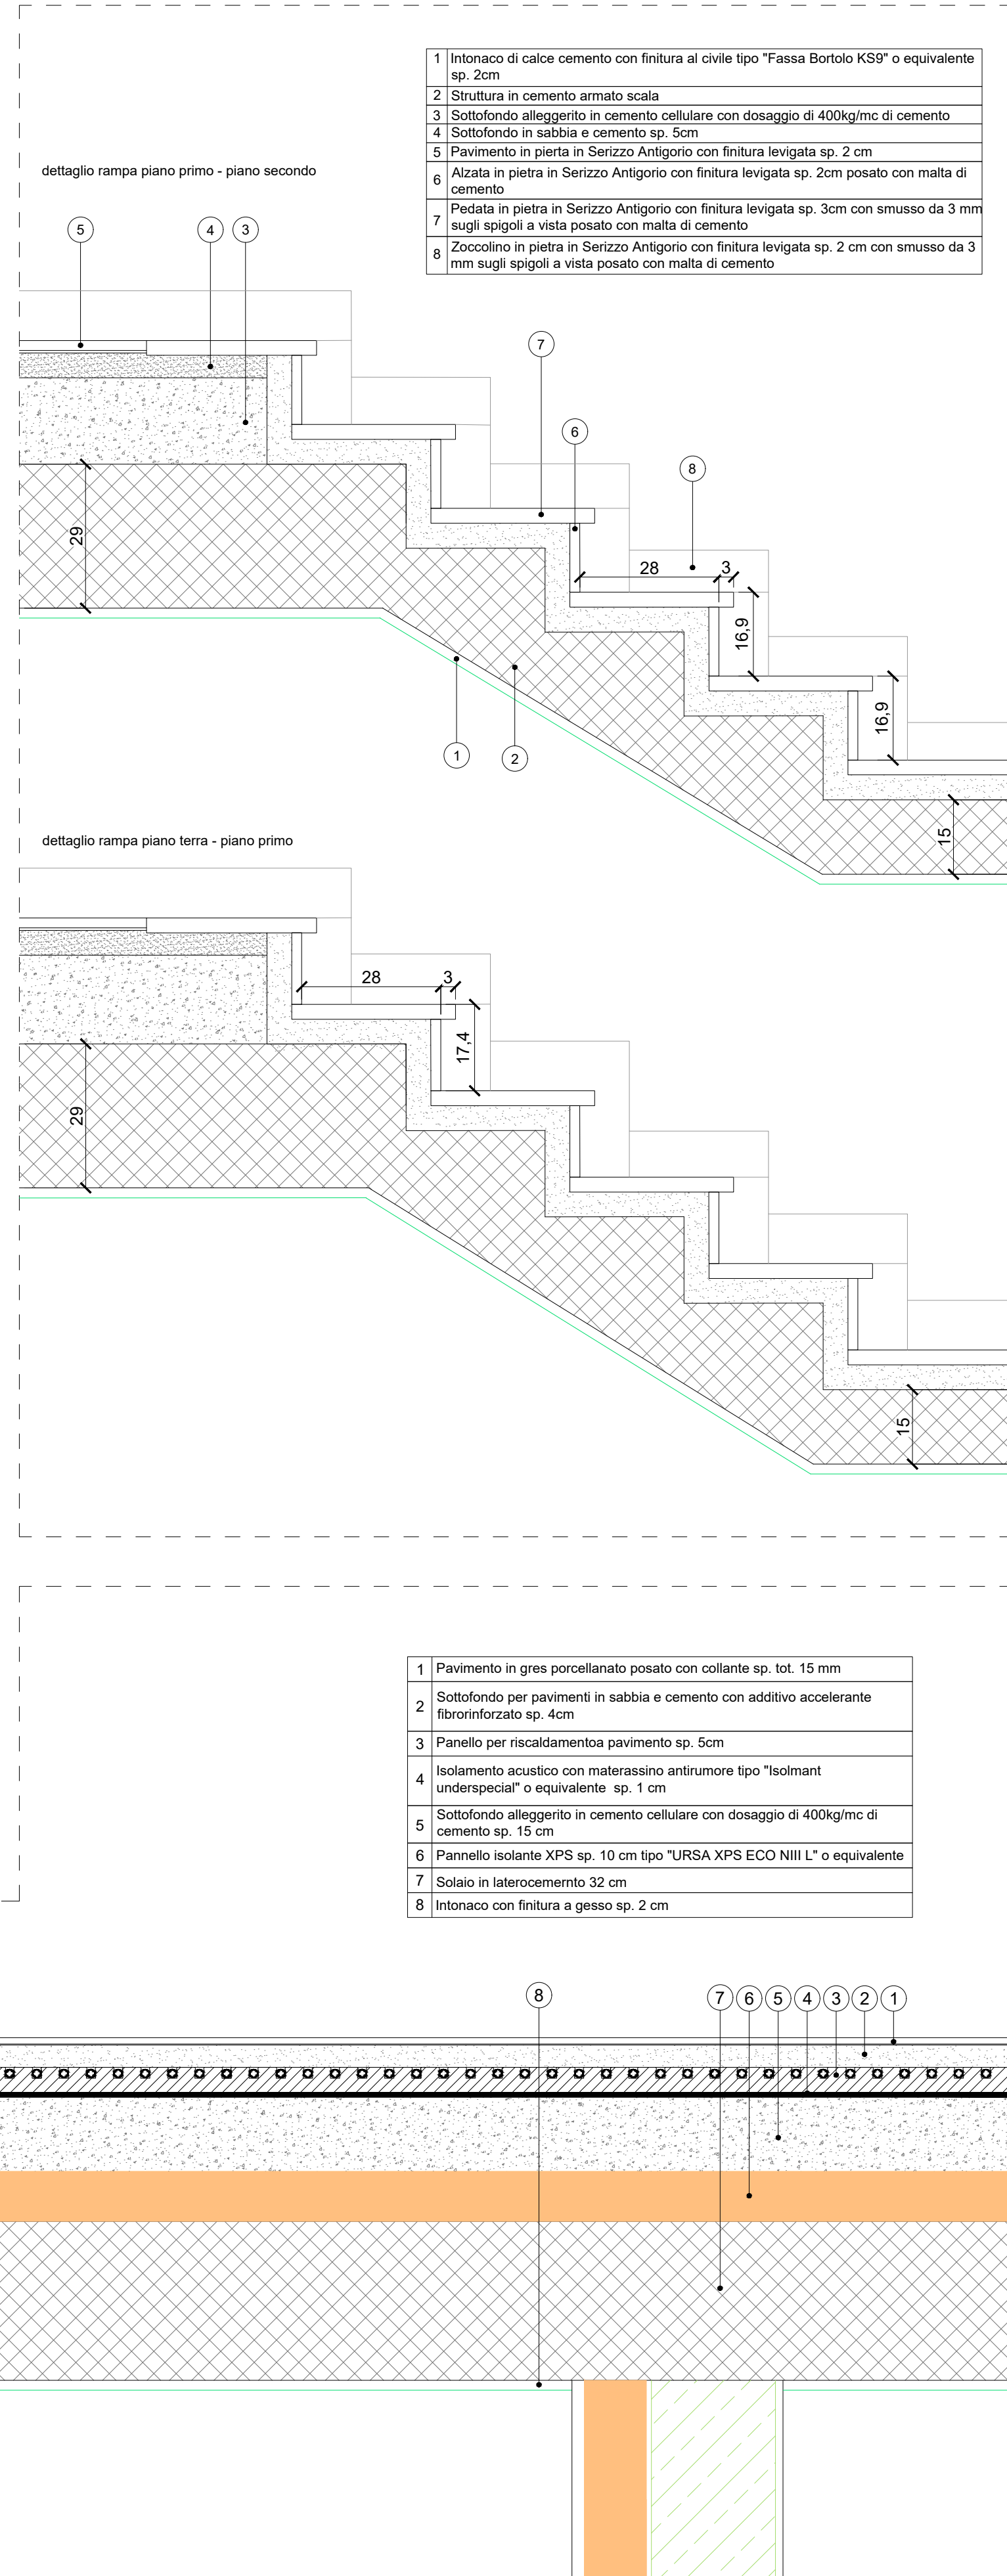
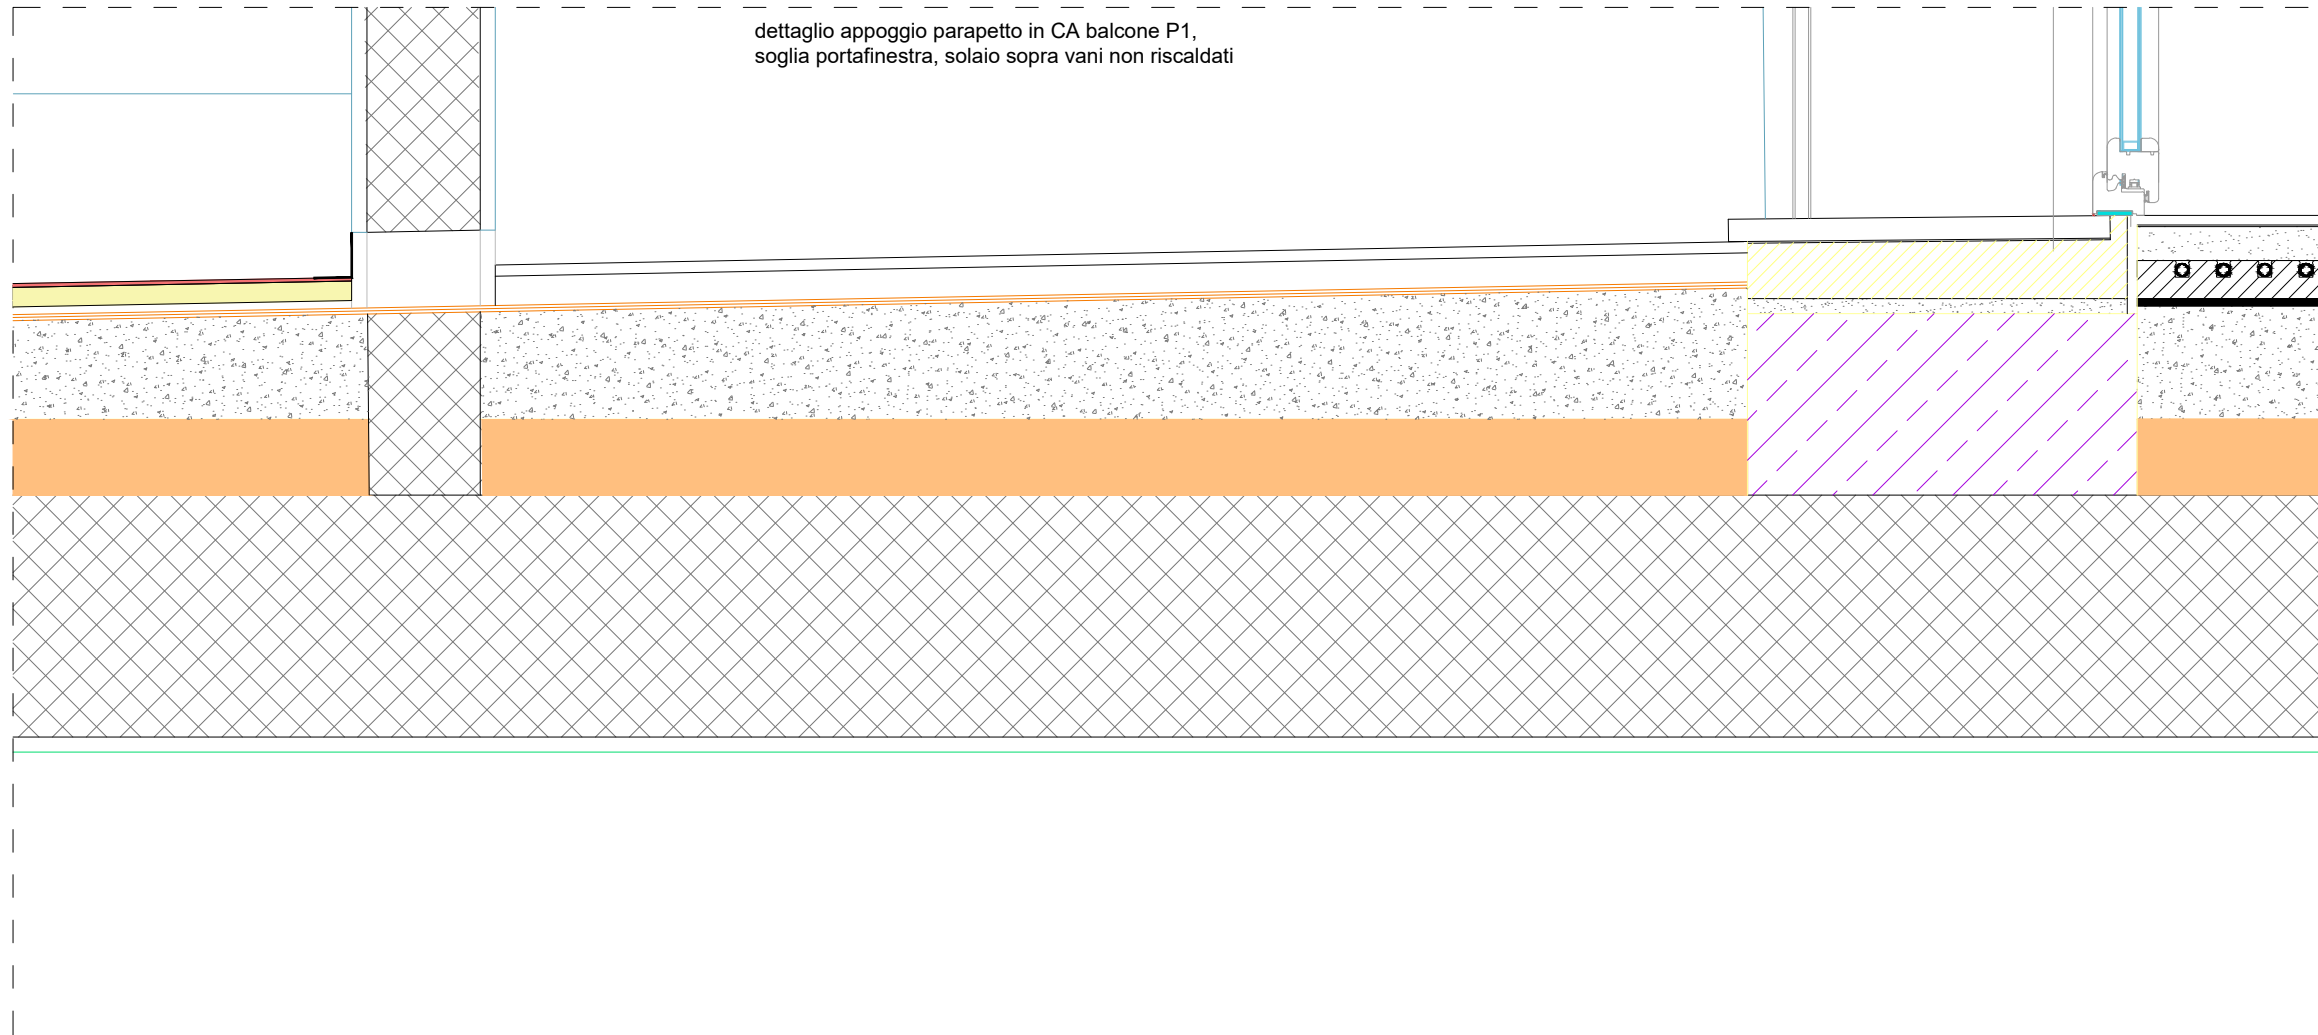


Pianta: nodo muro esterno e serramento, parete divisoria tra unità immobiliari e divisorio interno

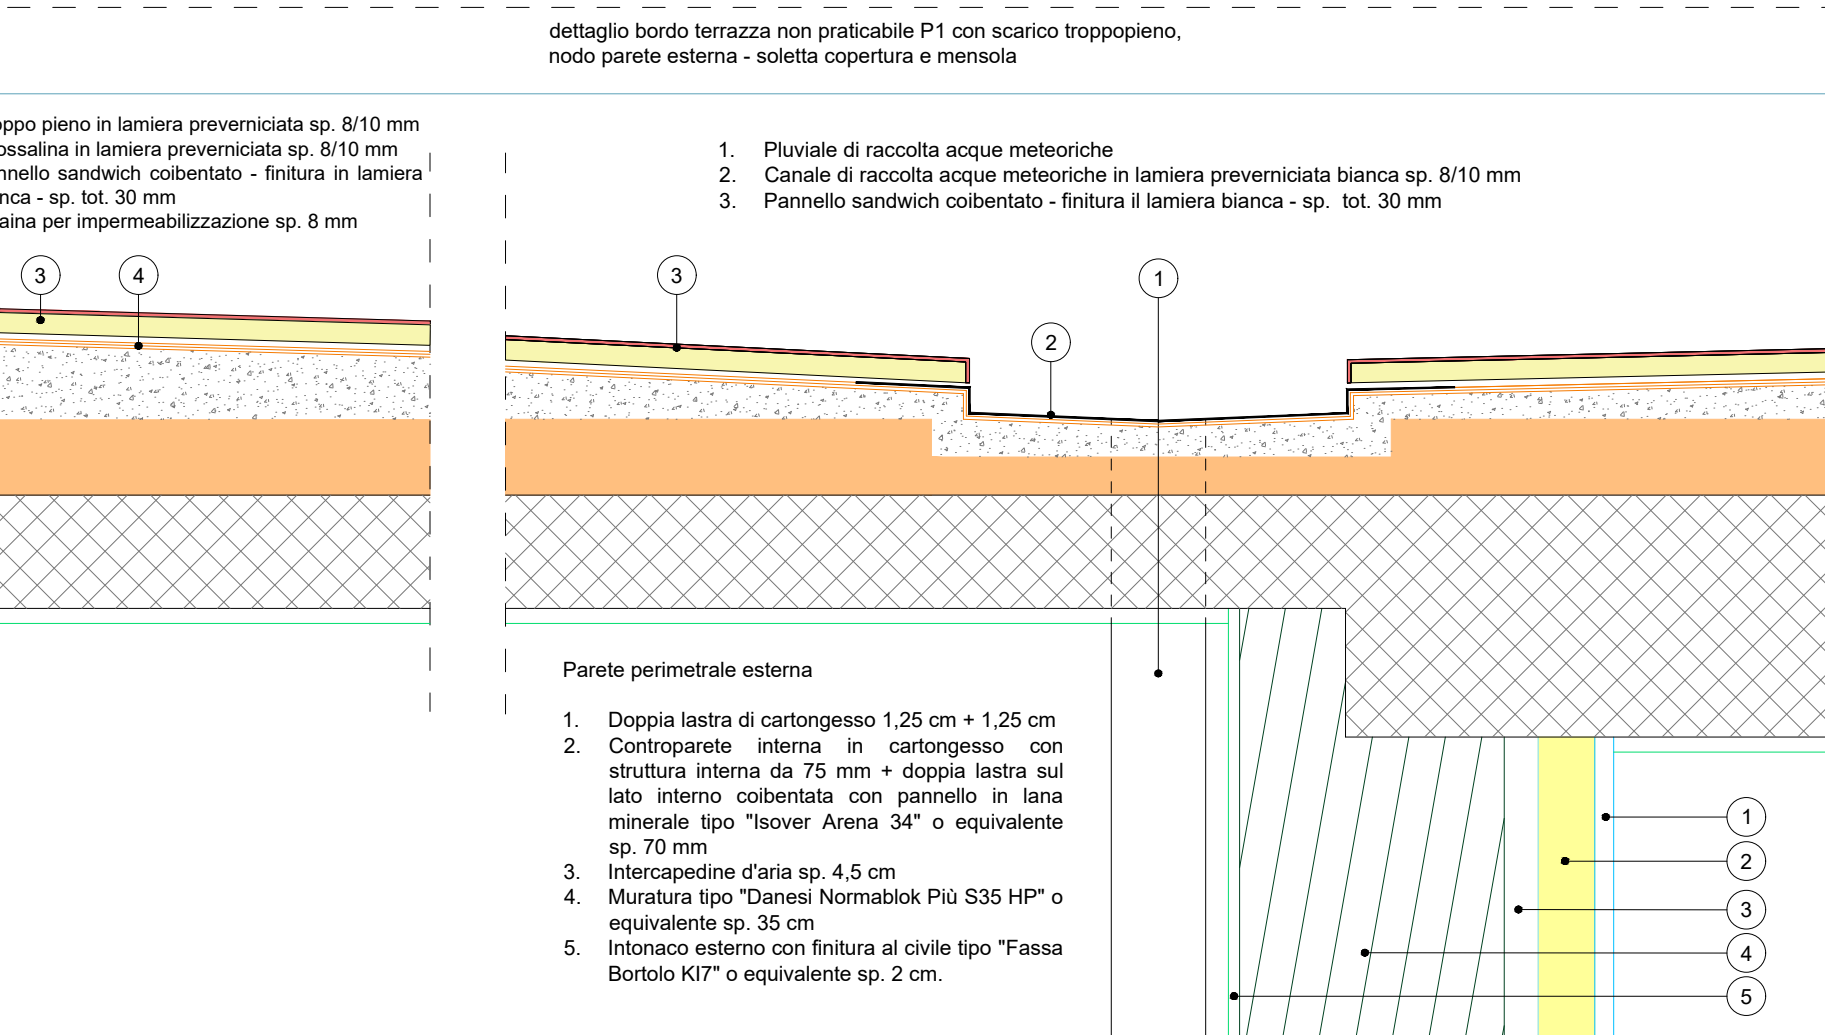

Tipo tavola ARCHITETTONICI		Tavola nr.		Orientamento
Serie PROGETTO ESECUTIVO		Tipo Tavola	ARCH	
Titolo PARTICOLARI COSTRUTTIVI		Sigla / Serie	ES	
		Numero / Variante	18	
		App.	00	