




Stato di fatto del fabbricato esistente 1:200

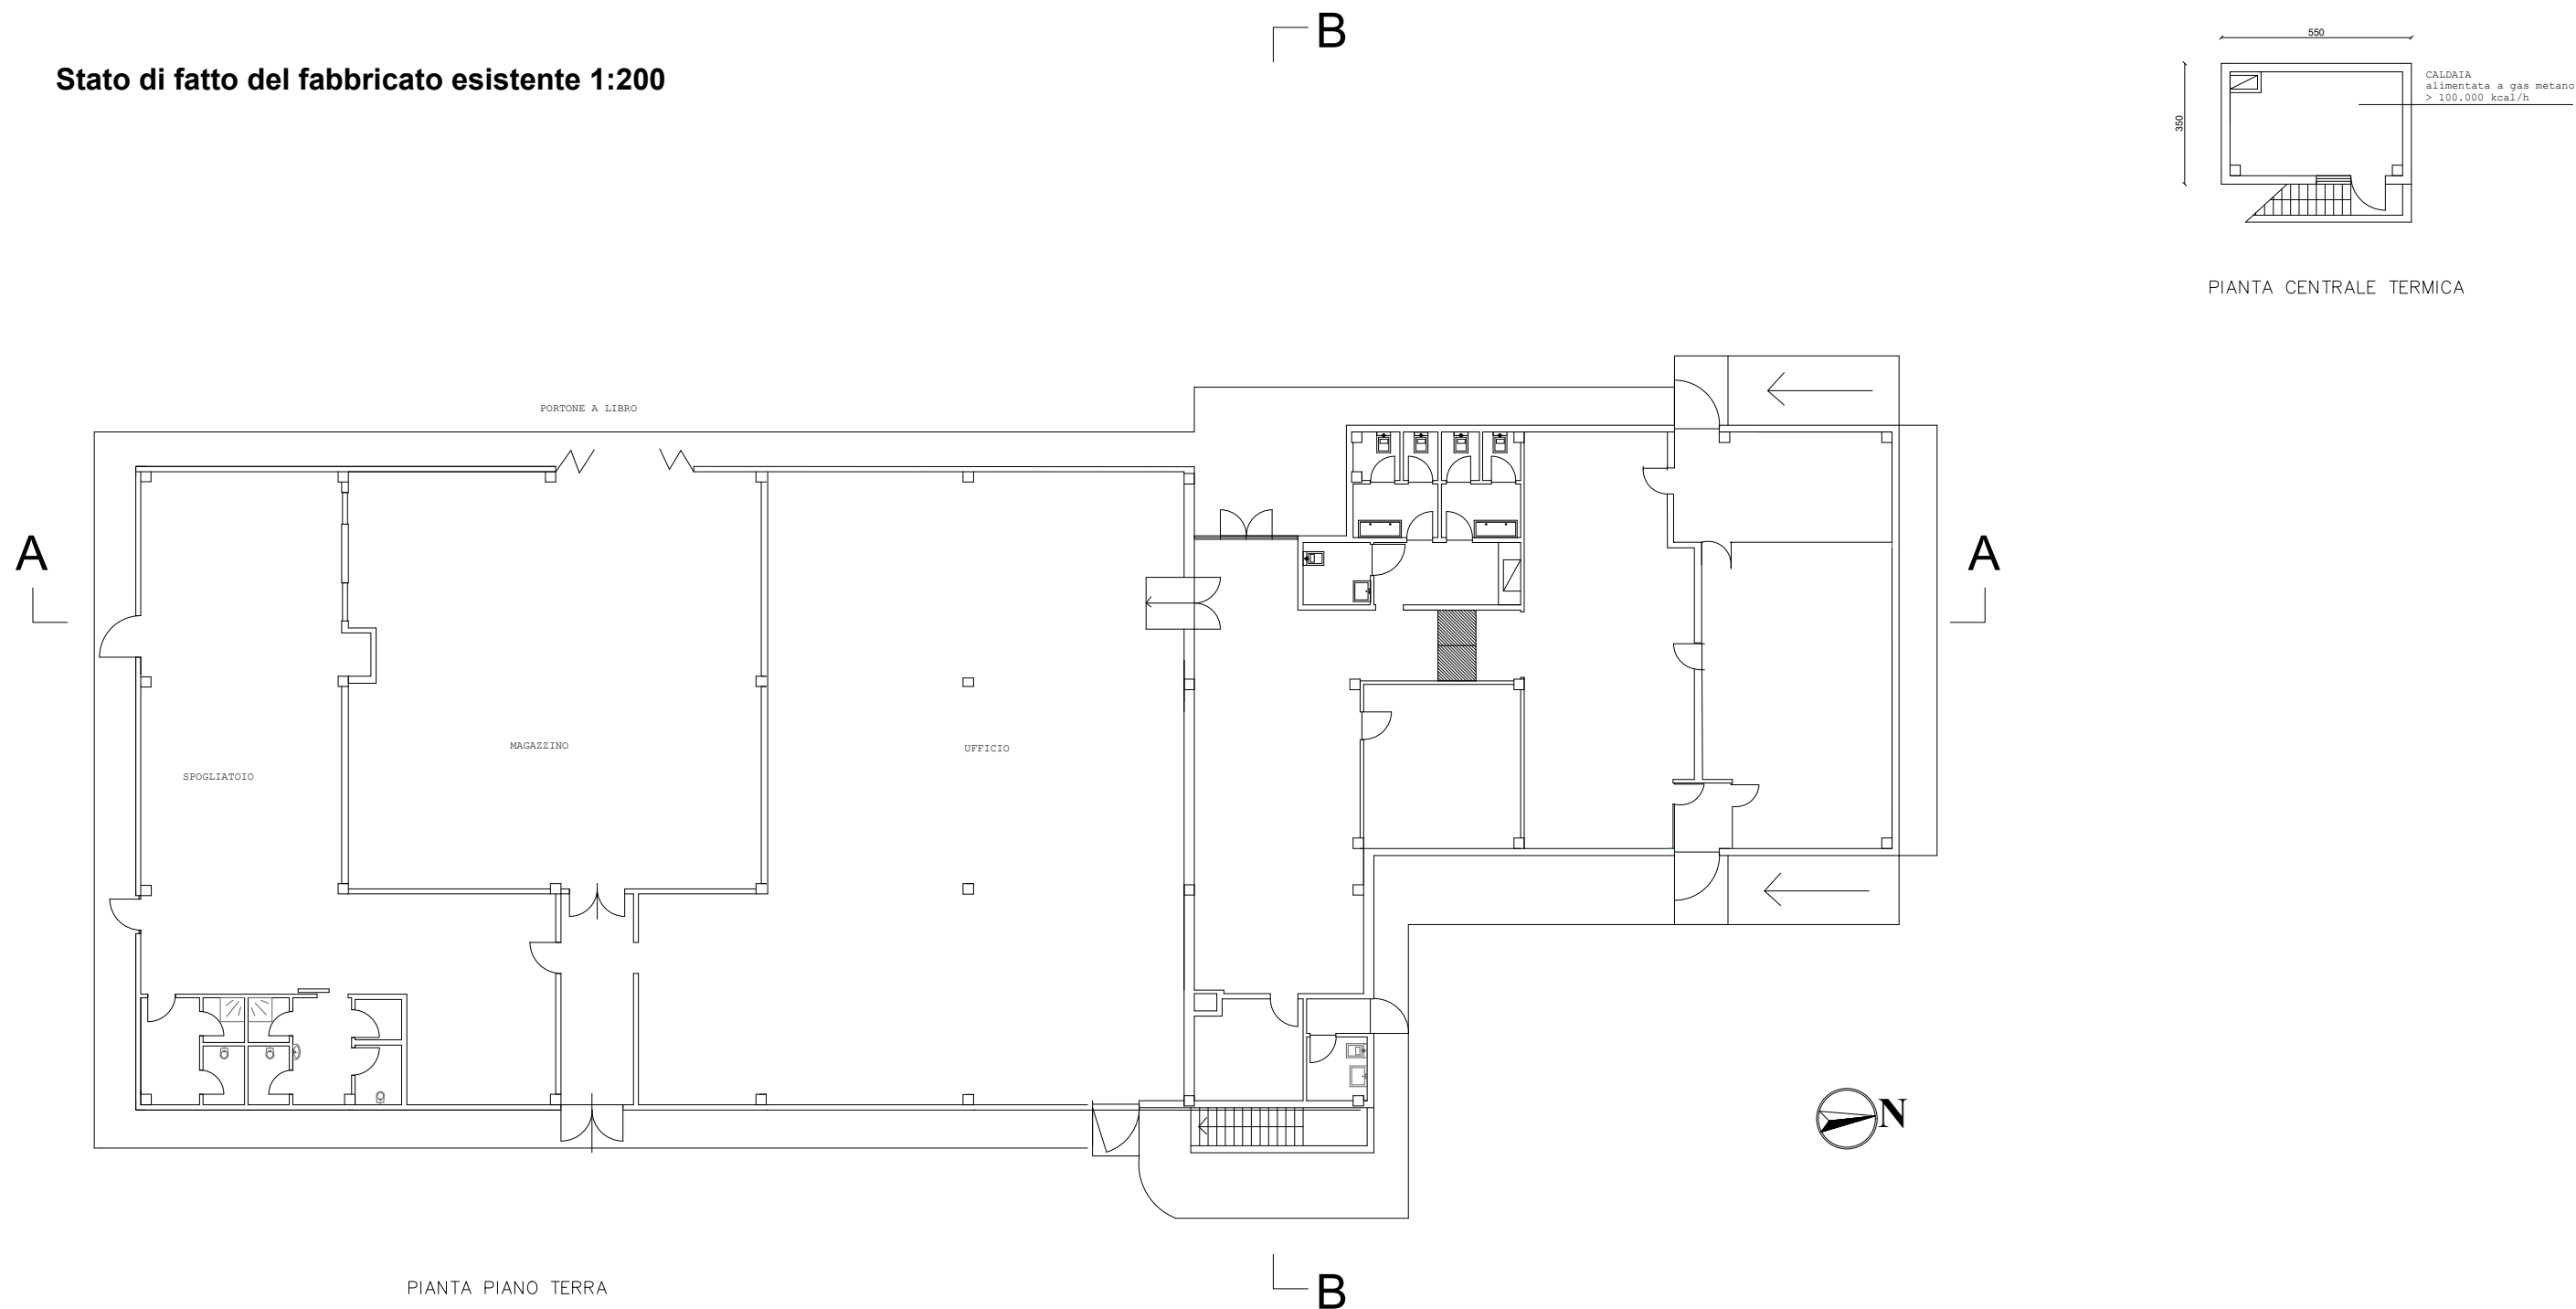



SEZIONE B-B

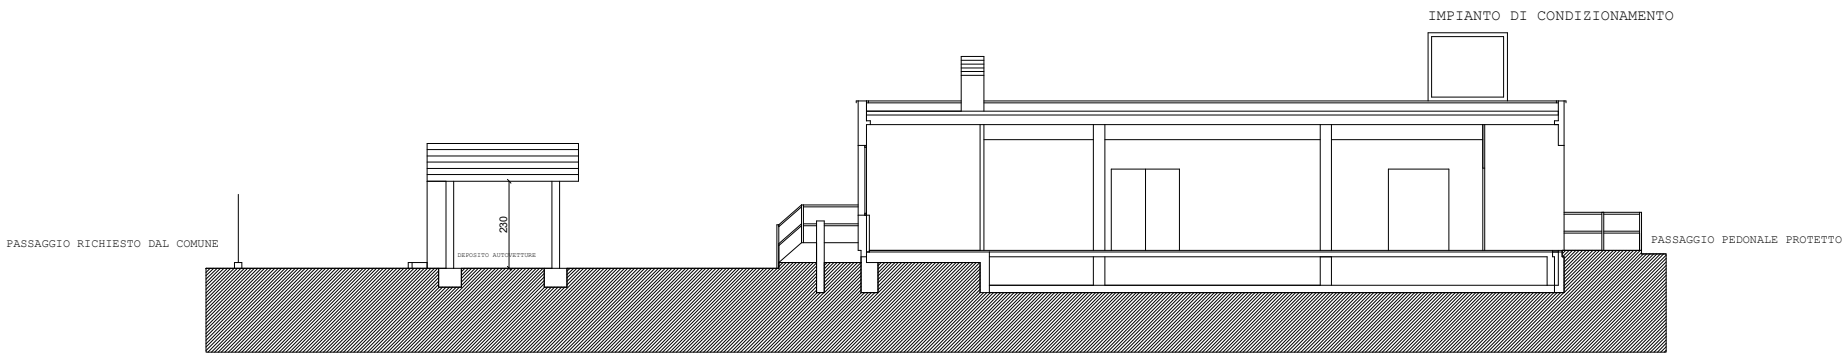


SEZIONE A-A

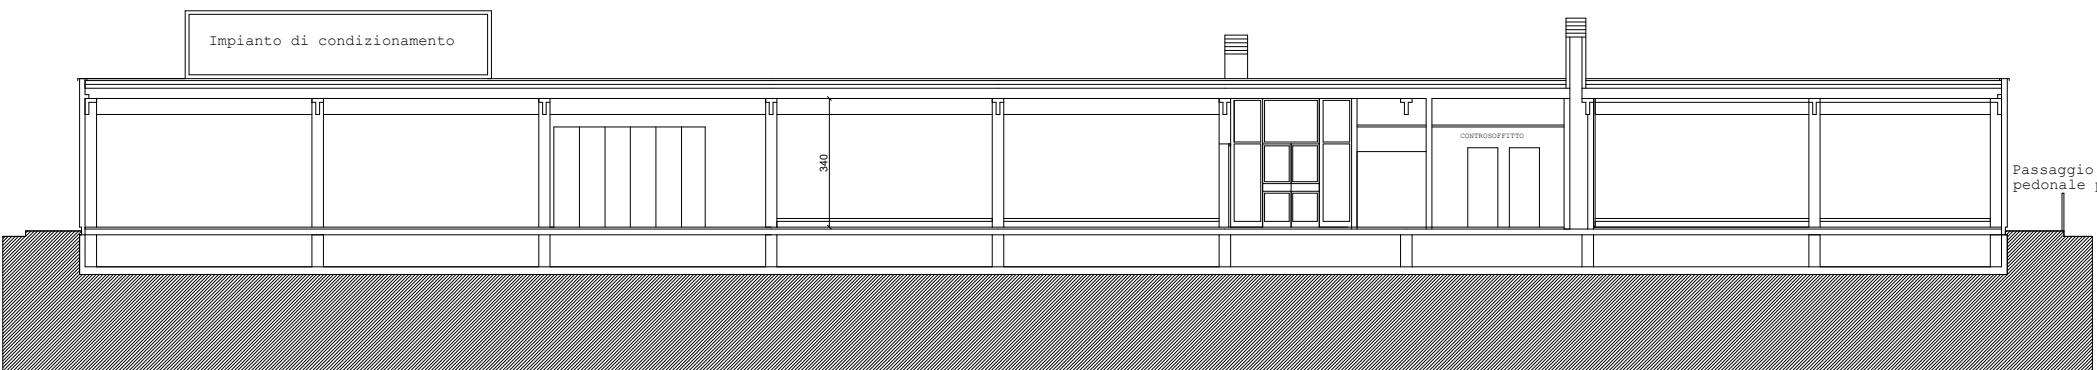

FRONTE EST

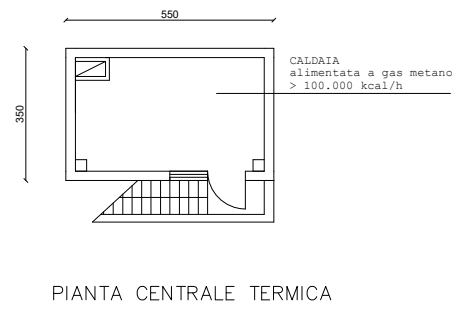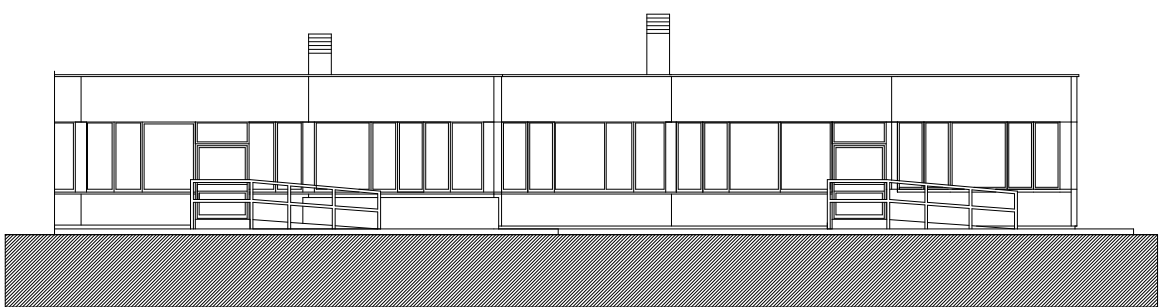

Legenda:

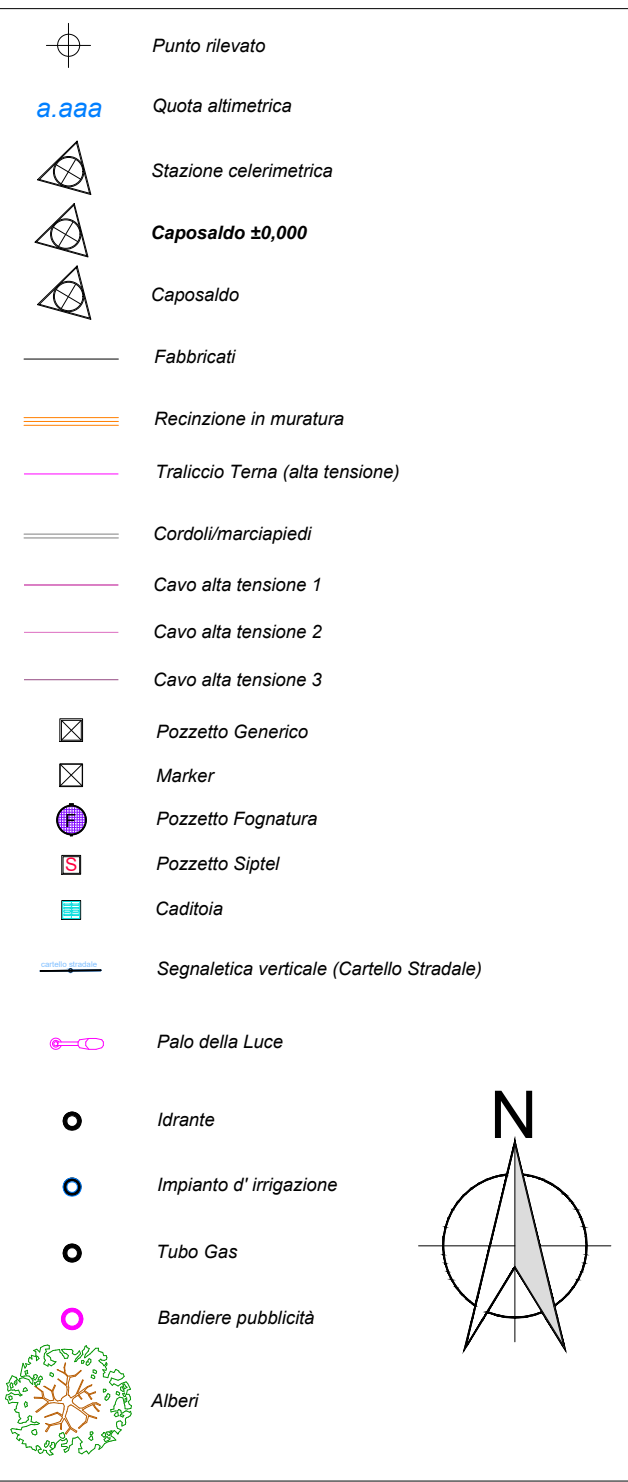

GB&PARTNERS
SERVIZI E PROGETTI IMMOBILIARI
Via Virgilio 27, 20141 Cologno Monzese (MI)
Tel. 02/7456111 - Fax 02/7456112
E-mail: info@gbpartners.it - web: www.gbpartners.it
Rivenditori autorizzati: Cologno Monzese (MI) - 02/7456111



COMUNE DI COLOGNO MONZESE (MI)
AREA Ex TORRIANI ARAS 01
PROGETTO ESECUTIVO
Progetto Servizi Abitativi Pubblici di via Pergolesi

N°	DATA	DESCRIZIONE MOTIVAZIONE DELL'AGGIORNAMENTO	STUDIO	DIS.
00	30/01/2026	Prima emissione	G.B.&P.	L.M.

Progetto	Proponente	Scala
PROGETTO ESECUTIVO Servizi Abitativi Pubblici Comune di Cologno Monzese(MI)	Officine Mak S.r.l. Corso Europa, 10 Milano 20122	1:200
		Data 30/01/2026

Tipo tavola	Tavola nr.
ARCHITETTONICI	
Serie PROGETTO ESECUTIVO	ARCH
Titolo RILIEVO AREA <i>Stato di fatto del fabbricato esistente</i>	Sigla / Serie ES
	Numero / Variante 04
	Agg. 00

Il Progettista



Il Direttore Lavori

Il Committente

Orientamento

