


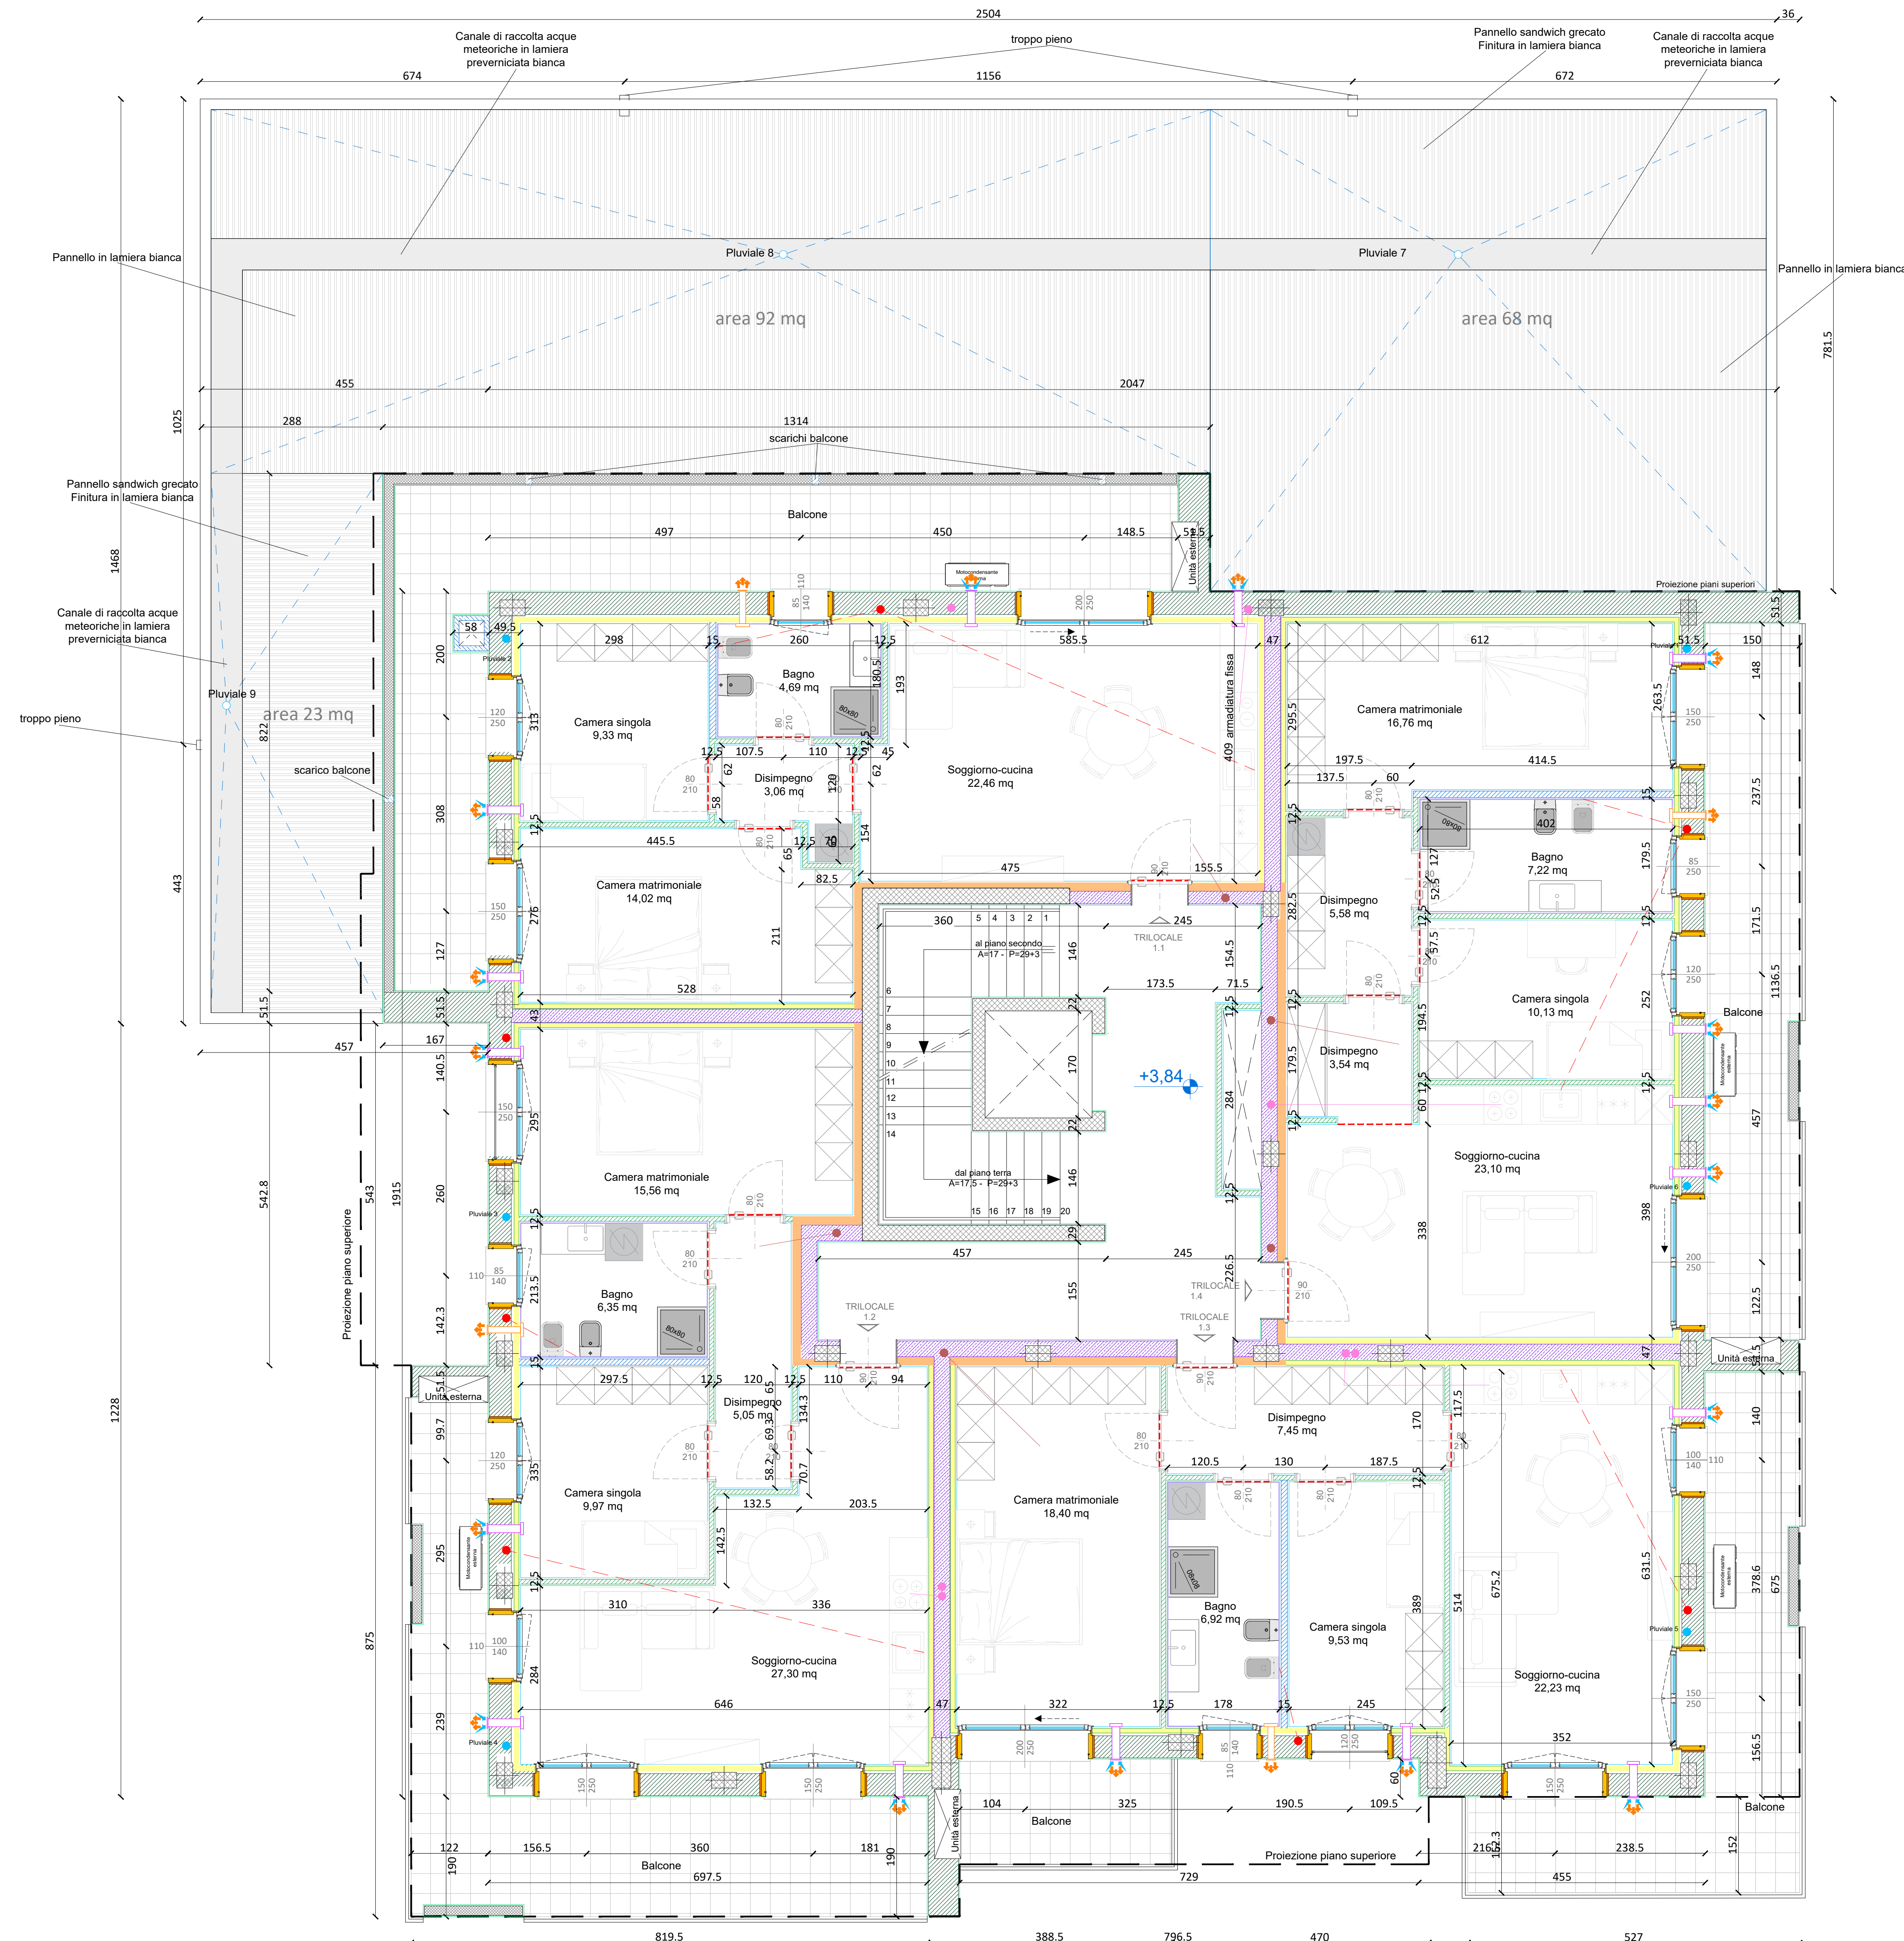

LEGENDA	
	Cemento armato
	Muratura in blocchi "Tipo Normablok" o equivalente sp. 35 cm
	Muratura in blocchi "Tipo Poroton serie P800" o equivalente sp. 25 cm
	Parete interna in cartongesso con struttura interna da 7,5 cm + doppia lastra su ogni lato
	Parete interna in cartongesso con struttura interna da 10 cm + doppia lastra su ogni lato
	Parete divisoria cantine in cls a vista spessore 12 cm
	Parete divisoria cantine in cls a vista spessore 20 cm
	Parete in CLS spessore 8 cm - canna esalazione locale rifiuti
	Pannello isolante di lana minerale "Tipo Isover Extrawall" o equivalente spessore 7,5 cm
	Pannello isolante, spessore 12,5 cm
	Intonaco esterno spessore 2 cm
	Doppia lastra in cartongesso 1,25 + 1,25 cm
	Rivestimento in gres 30x30cm posato a colla con fuga da 2mm H= 200cm
	Parapetto in C.A., h= 110 cm dal pavimento finito
	Parapetto in metallo, h= 110 cm dal pavimento finito
	Giunto pavimento
	Proiezione piano superiore
	Indicazione dell'utenza a cui si riferisce la colonna
	Colonna di scarico acque nere Ø110 mm - sezionato
	Colonna di scarico acque nere Ø110 mm - proiezione
	Colonna di estrazione bagno Ø10 mm - proiezione
	Colonna di scarico acque condensa Ø32 mm - sezionato
	Colonna di scarico acque condensa Ø32 mm - proiezione
	Indicazione dell'unità immobiliare a cui si riferisce la colonna condense
	Colonna cappa cucina Ø125 mm - sezionato
	Indicazione dell'unità immobiliare a cui si riferisce la cappa segnalata
	Colonna cappa cucina Ø125 mm - proiezione
	Pluviale / Discesa acque bianche Ø125 mm - sezionato
	Pluviale / Discesa acque bianche Ø125 mm - proiezione
	Unità di VMC decentralizzata Ø100mm e Ø150mm a singolo flusso continuo Marca "Aeraulig" - Modello "Quantum EX"
	Unità di VMC decentralizzata a singolo flusso alternato con recupero di calore Marca "Aeraulig" - Modello "Orion"

GB&PARTNERS
SERVIZI E PROGETTI IMMOBILIARI
Via Vigeo 30, 20122 Milano, Italia
Tel. 02 77 44 64 64
E-mail: comunicazione@gbpartners.it tecnico@gbpartners.it
Piazza Italia, 1 - 20121 Milano, Italia
R.G. n. 1/2008

COMUNE DI COLOGNO MONZESE (MI)
AREA Ex TORRIANI ARAS 01
PROGETTO ESECUTIVO
Progetto Servizi Abitativi Pubblici di via Pergolesi

N°	DATA	DESCRIZIONE	MOTIVAZIONE DELL'AGGIORNAMENTO	STUDIO	DIS.
00	30/01/2026	Prima emissione		G.B.&P.	L.M.
01	11/03/2026	Aggiornamento		G.B.&P.	L.T.

Il Progettista
Collegio Provinciale
Geometri e Geometri Laureati
di Lodi

Geometra
Gianpiero Bianchi

Il Direttore Lavori

Il Committente

Progetto
PROGETTO ESECUTIVO
Servizi Abitativi Pubblici
Comune di Cologno
Monzese(MI)

Proponente
Officine Mak S.r.l.
Corso Europa, 10
Milano 20122

Scala
1:50

Data
11/03/2026

Tipo tavola
ARCHITETTONICI

Serie
PROGETTO ESECUTIVO

Titolo
PIANTA PIANO PRIMO

Tavola nr.
Tipo
Tavola
ARCH

Sigla /
Serie
ES

Numero /
Variante
07

Agg.
01

Orientamento

Documento di proprietà della Società G.B. & Partners S.r.l. E' Vietata la riproduzione. Tutti i diritti sono riservati.