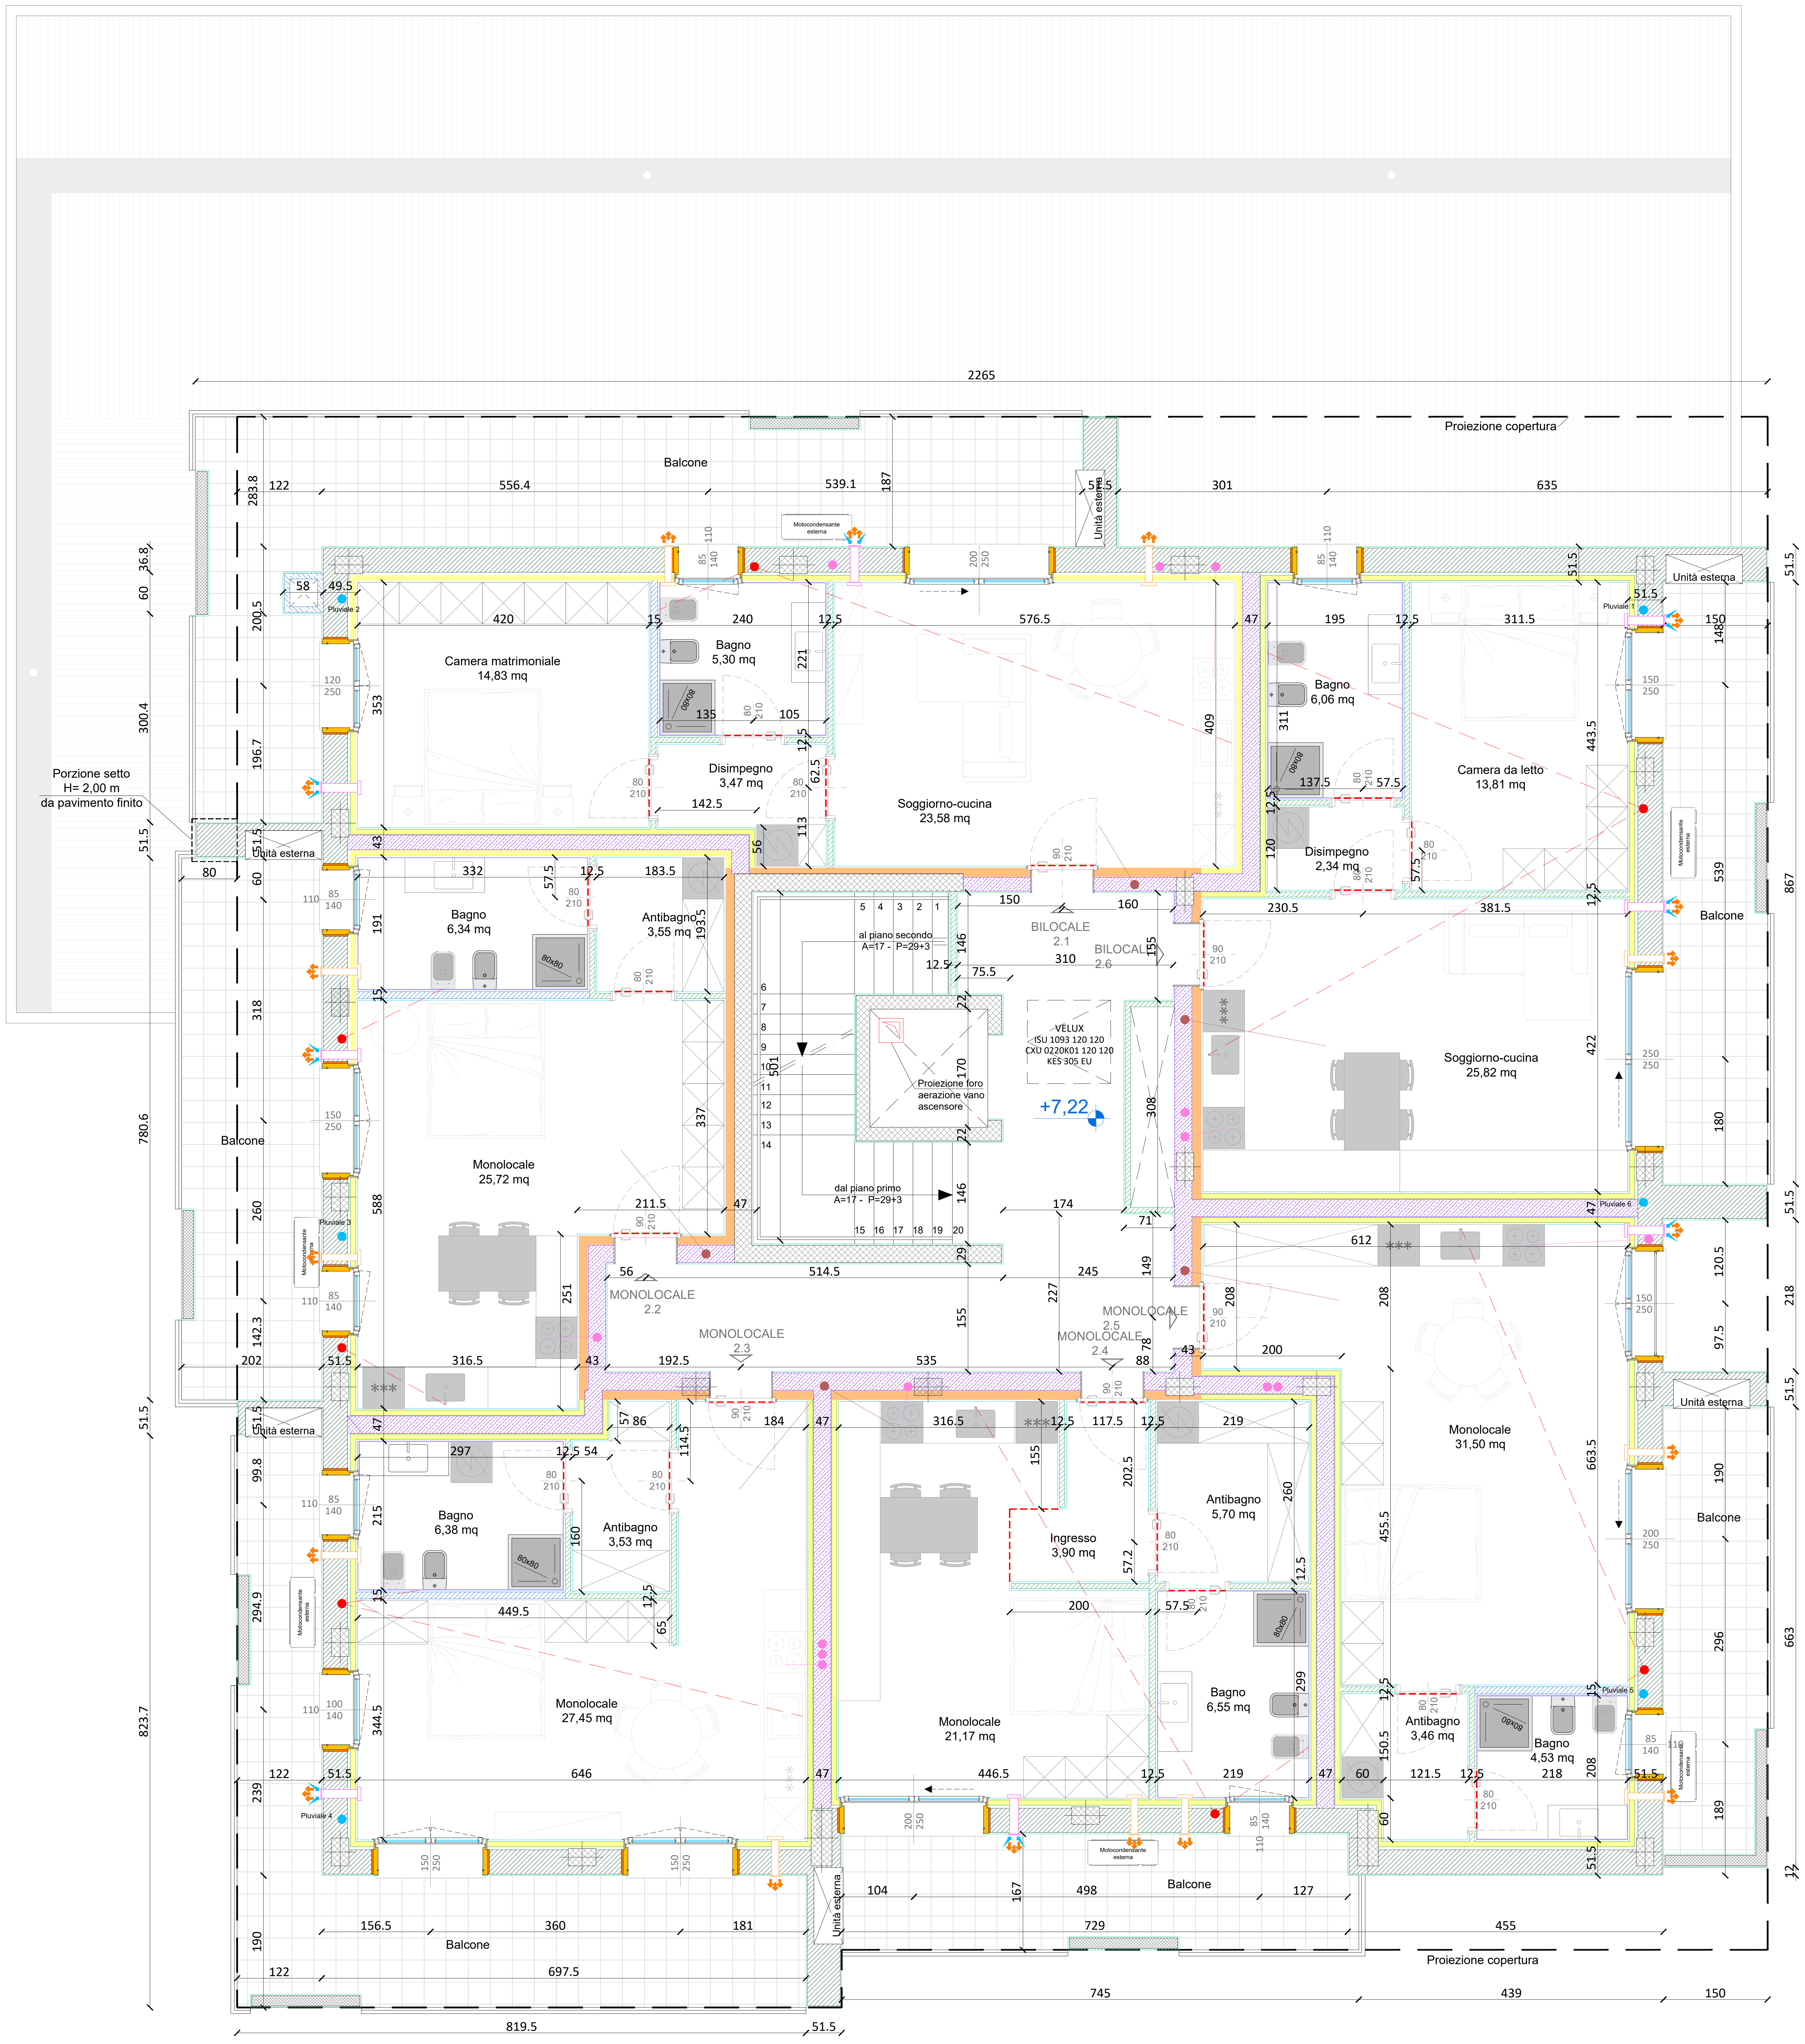

LEGENDA

▨	Cemento armato
▨	Muratura in blocchi "Tipo Normablok" o equivalente sp. 35 cm
▨	Muratura in blocchi "Tipo Poroton serie P800" o equivalente sp. 25 cm
▨	Parete interna in cartongesso con struttura interna da 7,5 cm + doppia lastra su ogni lato
▨	Parete interna in cartongesso con struttura interna da 10 cm + doppia lastra su ogni lato
▨	Parete divisoria cantine in cls a vista spessore 12 cm
▨	Parete divisoria cantine in cls a vista spessore 20 cm
▨	Parete in CLS spessore 8 cm - canna esalazione locale rifiuti
🟨	Pannello isolante di lana minerale "Tipo Isover Extrawall" o quivalente spessore 7,5 cm
🟧	Pannello isolante, spessore 12,5 cm
▭	Intonaco esterno spessore 2 cm
▭	Doppia lastra in cartongesso 1,25 + 1,25 cm
—	Rivestimento in gres 30x30cm posato a colla con fuga da 2mm H= 200cm
▬	Parapetto in C.A., h= 110 cm dal pavimento finito
═	Parapetto in metallo, h= 110 cm dal pavimento finito
- - -	Giunto pavimento
- - -	Proiezione piano superiore
● - -	Indicazione dell'utenza a cui si riferisce la colonna
●	Colonna di scarico acque nere Ø110 mm - sezionato
○	Colonna di scarico acque nere Ø110 mm - proiezione
○	Colonna di estrazione bagno Ø110 mm - proiezione
●	Colonna di scarico acque condensa Ø32 mm - sezionato
○	Colonna di scarico acque condensa Ø32 mm - proiezione
● —	Indicazione dell'unità immobiliare a cui si riferisce la colonna condense
●	Colonna cappa cucina Ø125 mm - sezionato
● —	Indicazione dell'unità immobiliare a cui si riferisce la cappa segnalata
○	Colonna cappa cucina Ø125 mm - proiezione
●	Pluviale / Discesa acque bianche Ø125 mm - sezionato
○	Pluviale / Discesa acque bianche Ø125 mm - proiezione
⇹	Unità di VMC decentralizzata Ø100mm e Ø150mm a singolo flusso continuo Marca "Aerauliqa" - Modello "Quantum EX"
⇹	Unità di VMC decentralizzata a singolo flusso alternato con recupero di calore Marca "Aerauliqa" - Modello "Orion"

GB&PARTNERS
SERVIZI E PROGETTI IMMOBILIARI
Via Varalli 37, 26845 Codogno (LO)
Telefono 0377 436099 - 0377 34691 - **Fax** 0377 436654
E-mail amministrazione@gbepartners.it - tecnico@gbepartners.it
www.gbepartners.it
REGISTRO IMPRESE DI LODI n°05966150962
PARTITA I.V.A / C.F. 05966150962
C.S. € 11.111,10 iv

UNI EN ISO 9001:2015
UNI EN ISO 14001:2015
Certificazione n. CR-2881PG/001
Norma: UNI/PdR 125:2022

COMUNE DI COLOGNO MONZESE (MI)
AREA Ex TORRIANI ARAS 01

PROGETTO ESECUTIVO
Progetto Servizi Abitativi Pubblici di via Pergolesi

Il Progettista

Collegio Provinciale Geometri e Geometri Laureati di Lodi
Iscrizione Albo N. 267
Geometra
Gianpiero Bianchi

ARCHITETTO
CRISTIANO SCHIAVI
421

N°	DATA	DESCRIZIONE MOTIVAZIONE DELL'AGGIORNAMENTO	STUDIO	DIS.
00	30/01/2026	Prima emissione	G.B.&P.	L.M.

Il Direttore Lavori

Progetto	Proponente	Scala
PROGETTO ESECUTIVO ***Servizi Abitativi Pubblici*** *Comune di Cologno Monzese(MI)*	***Officine Mak S.r.l.*** *Corso Europa, 10* *Milano 20122*	**1:50** Data 30/01/2026

Il Committente

Tipo tavola
ARCHITETTONICI

Serie
PROGETTO ESECUTIVO

Titolo
PIANTA PIANO SECONDO

Tavola nr.

Tipo Tavola	**ARCH**
Sigla / Serie	**ES**
Numero / Variante	**08**
Agg.	**00**

Orientamento

N

Documento di proprietà della Società G.B. & Partners S.r.l.. E' Vietata la riproduzione. Tutti i diritti sono riservati.