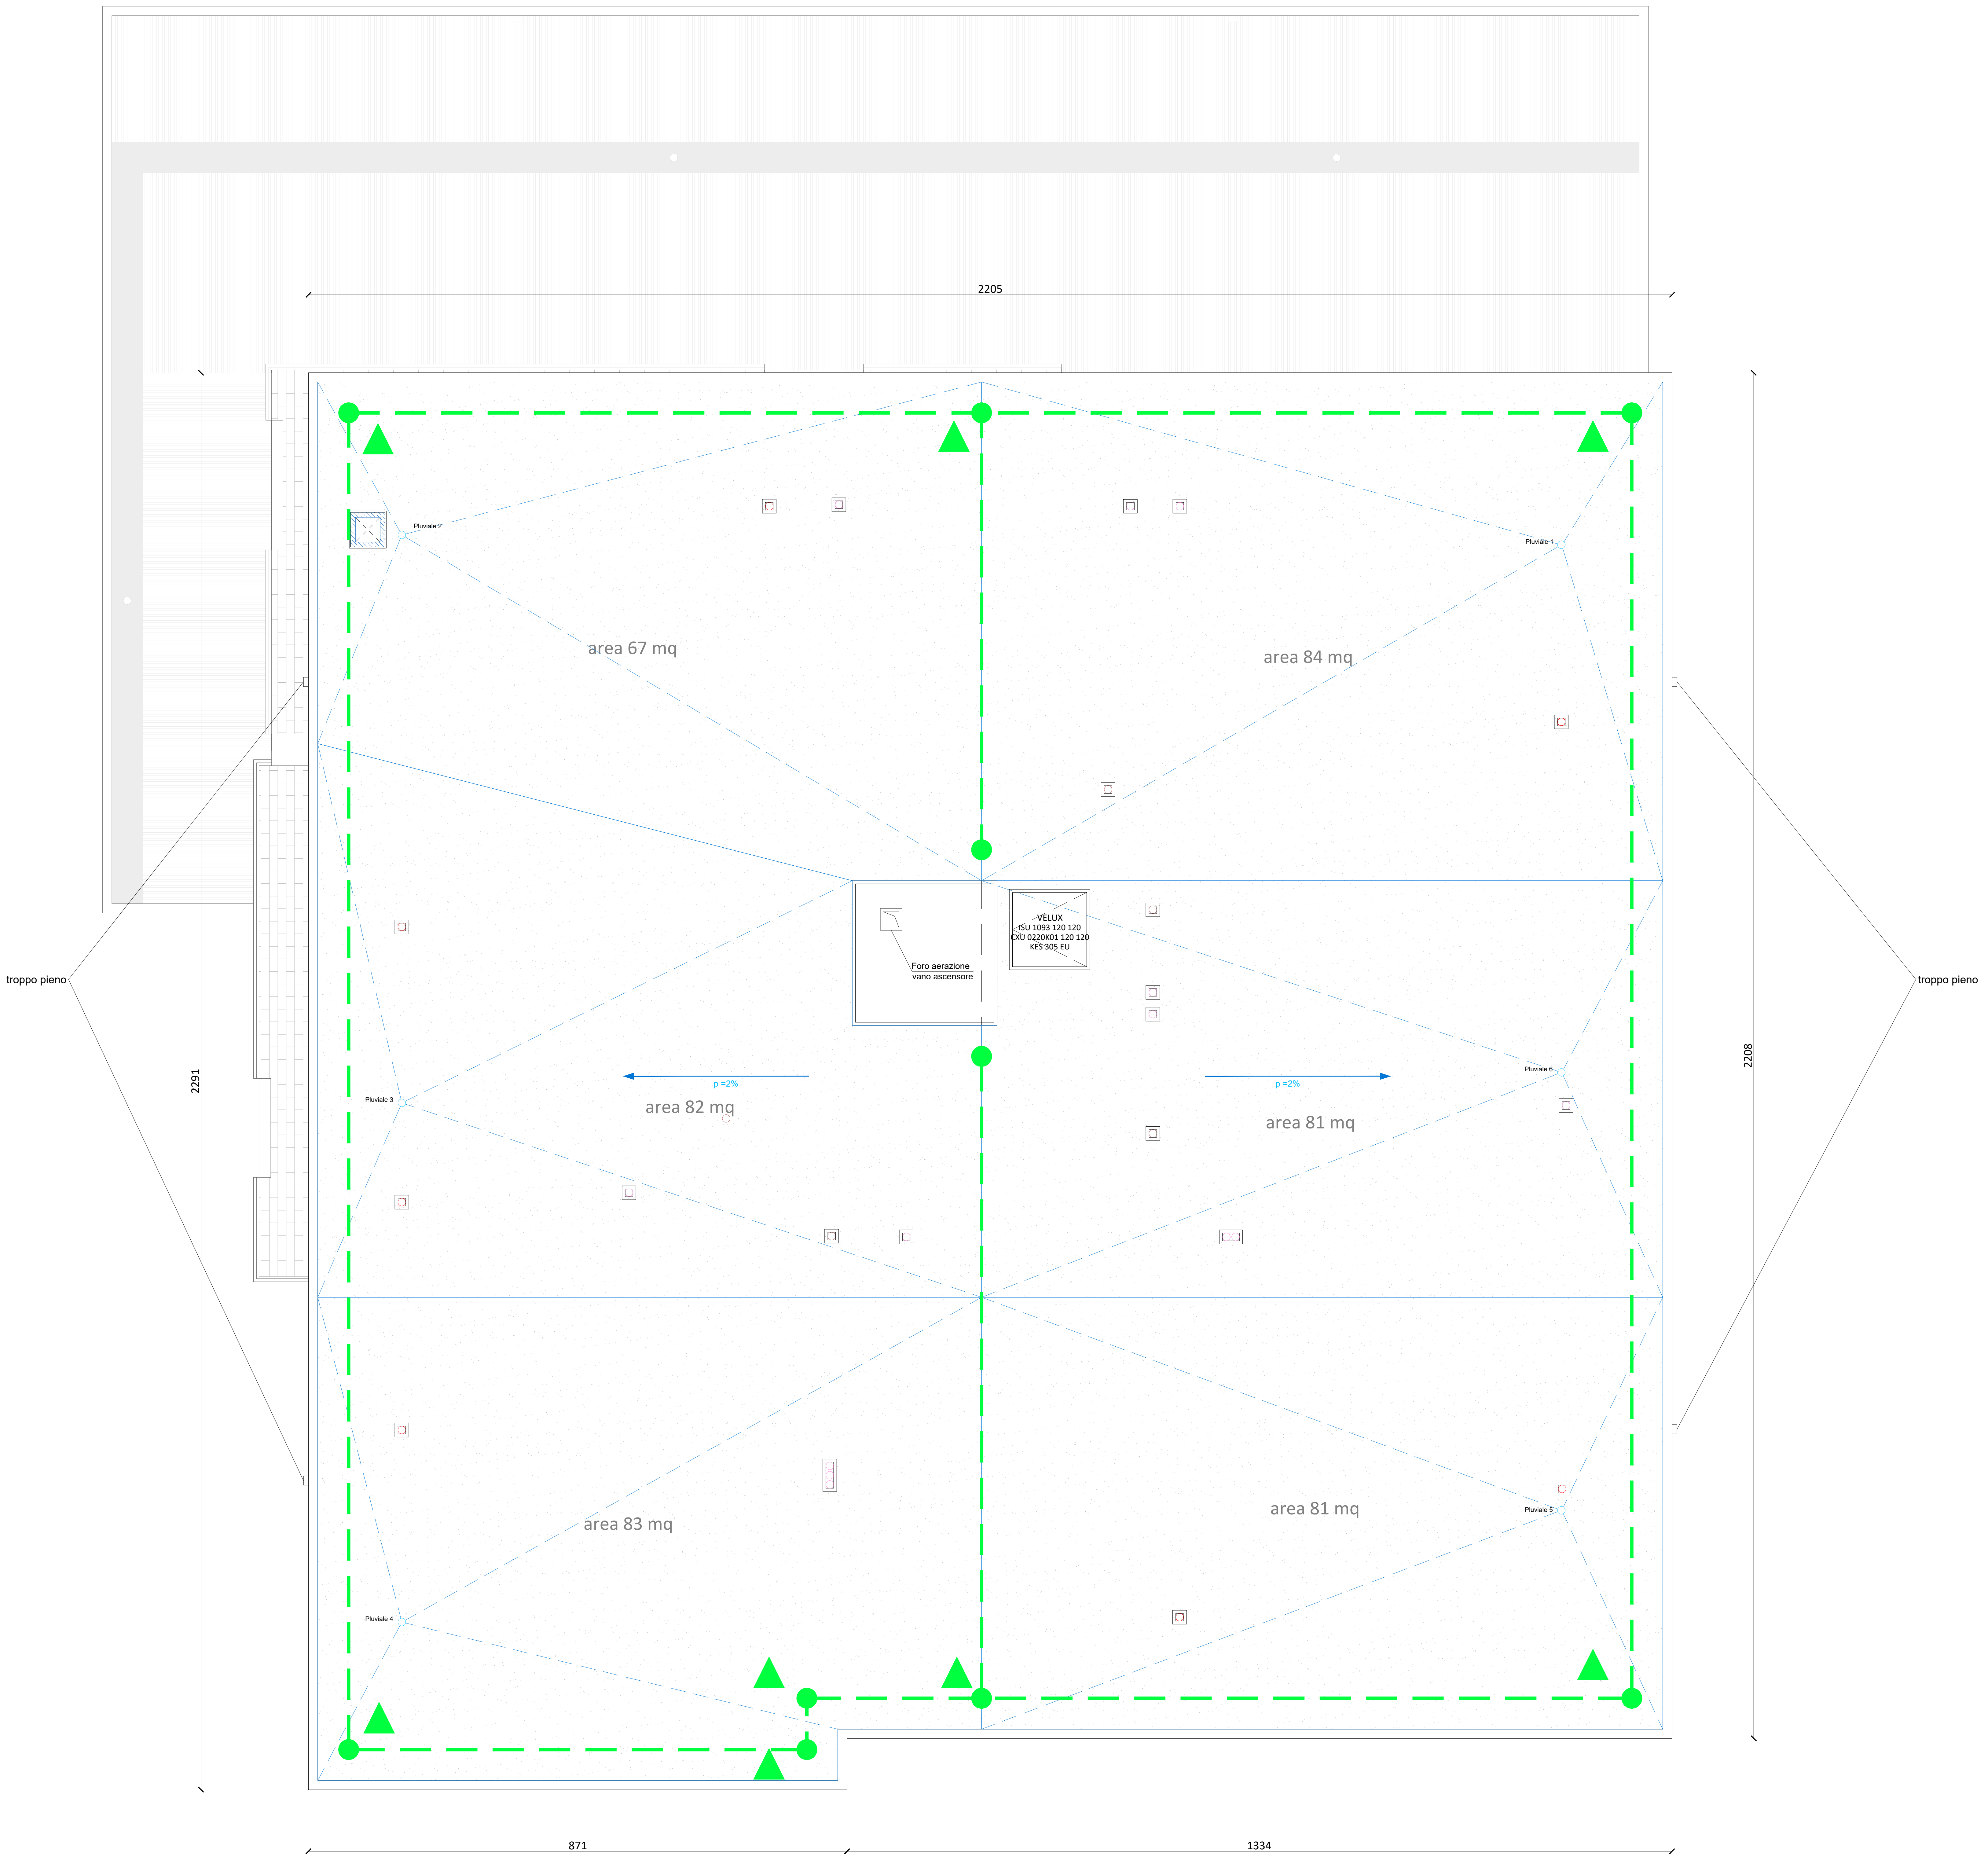

LEGENDA

▨	Parete in CLS spessore 8 cm - canna esalazione locale rifiuti
○	Colonna di scarico acque nere Ø110 mm - proiezione
○	Colonna di scarico acque condensa Ø32 mm - proiezione
○	Colonna cappa cucina Ø125 mm - proiezione
○	Pluviale / Discesa acque bianche Ø125 mm - proiezione
●	Punto di ancoraggio fisso classe "A2"
▲	Punto di deviazione di caduta
- - -	Linea vita

GB&PARTNERS
SERVIZI E PROGETTI IMMOBILIARI
Via Varalli 37, 26845 Codogno (LO)
Telefono 0377 436099 - 0377 34691 - **Fax** 0377 436654
E-mail amministrazione@gbepartners.it - tecnico@gbepartners.it
www.gbepartners.it
REGISTRO IMPRESE DI LODI n°05966150962
PARTITA I.V.A / C.F. 05966150962
C.S. € 11.111,10 iv

UNI EN ISO 9001:2015
UNI EN ISO 14001:2015
Certificazione n. CR-2881PG/001
Norma: UNI/PdR 125:2022

COMUNE DI COLOGNO MONZESE (MI)
AREA Ex TORRIANI ARAS 01
PROGETTO ESECUTIVO
Progetto Servizi Abitativi Pubblici di via Pergolesi

N°	DATA	DESCRIZIONE MOTIVAZIONE DELL'AGGIORNAMENTO	STUDIO	DIS.
00	30/01/2026	Prima emissione	G.B.&P.	L.M.

Il Progettista

Collegio Provinciale
Geometri e Geometri Laureati
di Lodi
Iscrizione Albo
N. 267
Geometra
Gianpiero Bianchi

CRISTIANO SCHIAVI
421
LODI

Il Direttore Lavori

Il Committente

Progetto	Proponente	Scala
PROGETTO ESECUTIVO ***Servizi Abitativi Pubblici*** *Comune di Cologno Monzese(MI)*	***Officine Mak S.r.l.*** *Corso Europa, 10* *Milano 20122*	**1:50** Data 30/01/2026

Tipo tavola
ARCHITETTONICI

Serie
PROGETTO ESECUTIVO

Titolo
PIANTA COPERTURA

Tavola nr.

Tipo Tavola	**ARCH**
Sigla / Serie	**ES**
Numero / Variante	**09**
Agg.	**00**

Orientamento

N

Documento di proprietà della Società G.B. & Partners S.r.l.. E' Vietata la riproduzione. Tutti i diritti sono riservati.