

IMMAGINI TIPOLOGICHE




Copertura per unità esterna condizionatore piano terra




Ringhiera metallica balcone




Recinzione giardini privati a servizio degli appartamenti, in acciaio zincato a caldo tipo "Talia Ventus" e muretto in cls a vista

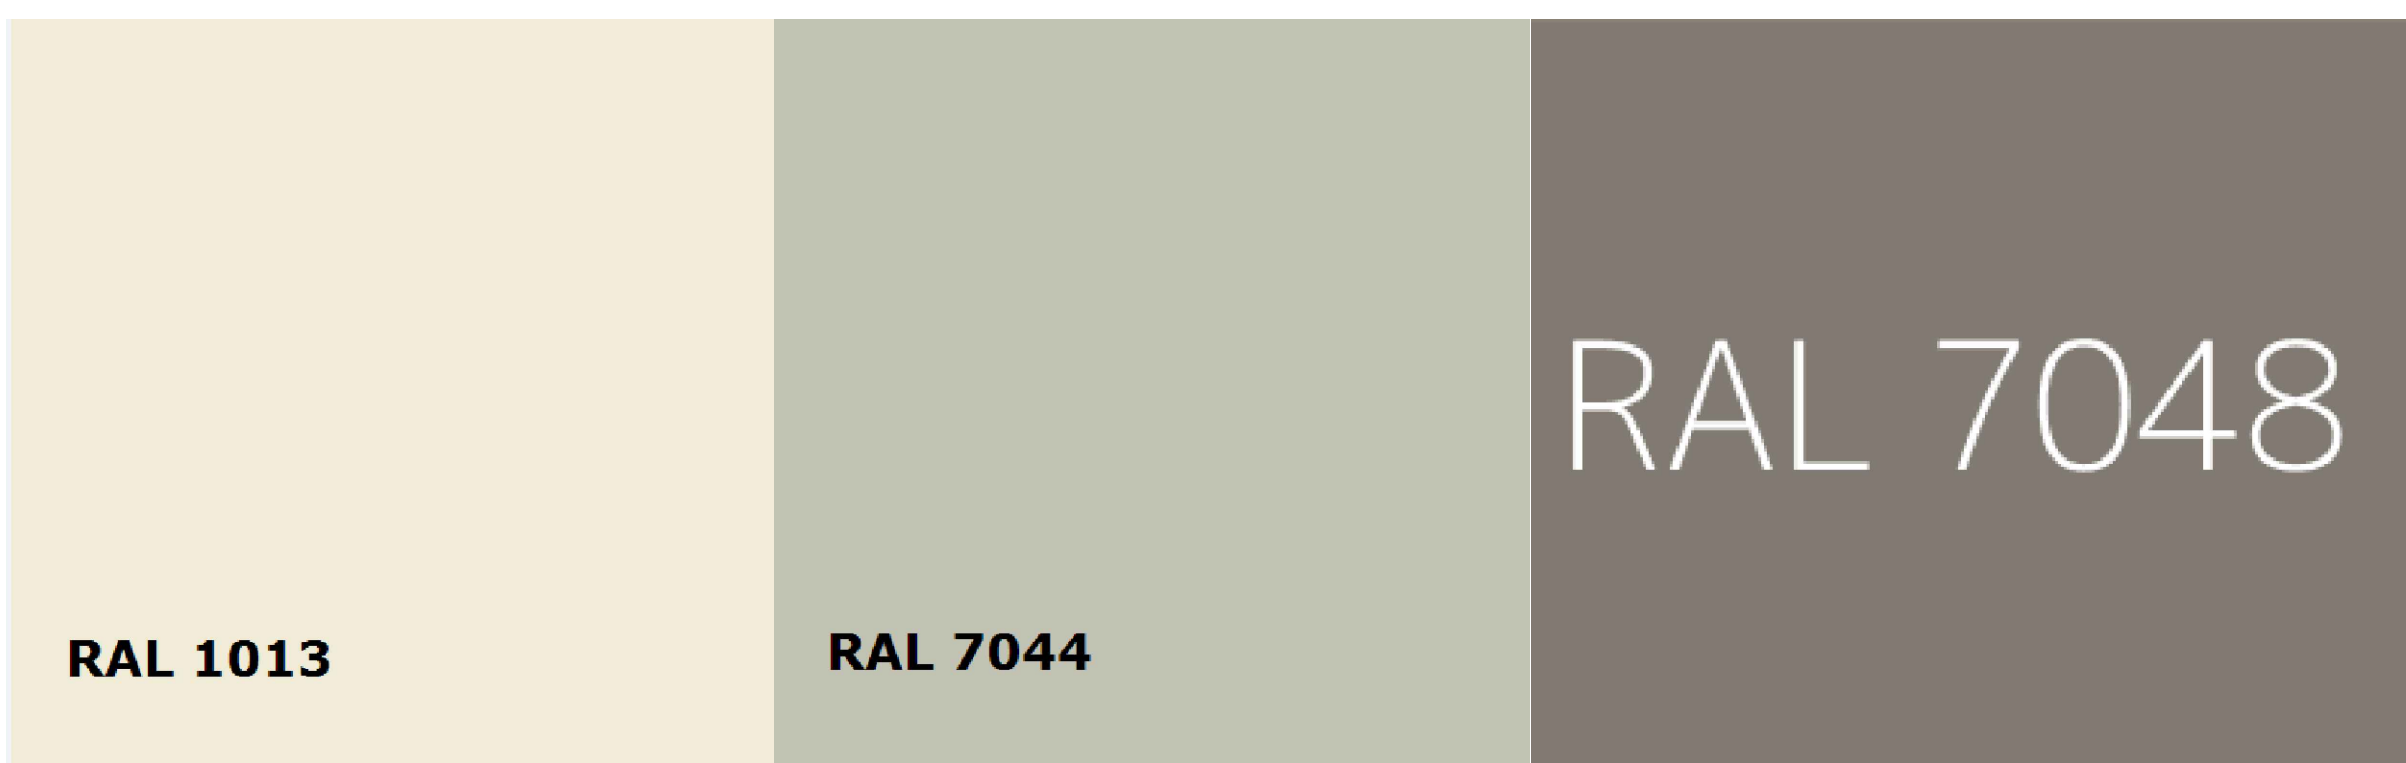

Tinteggiature muri esterni

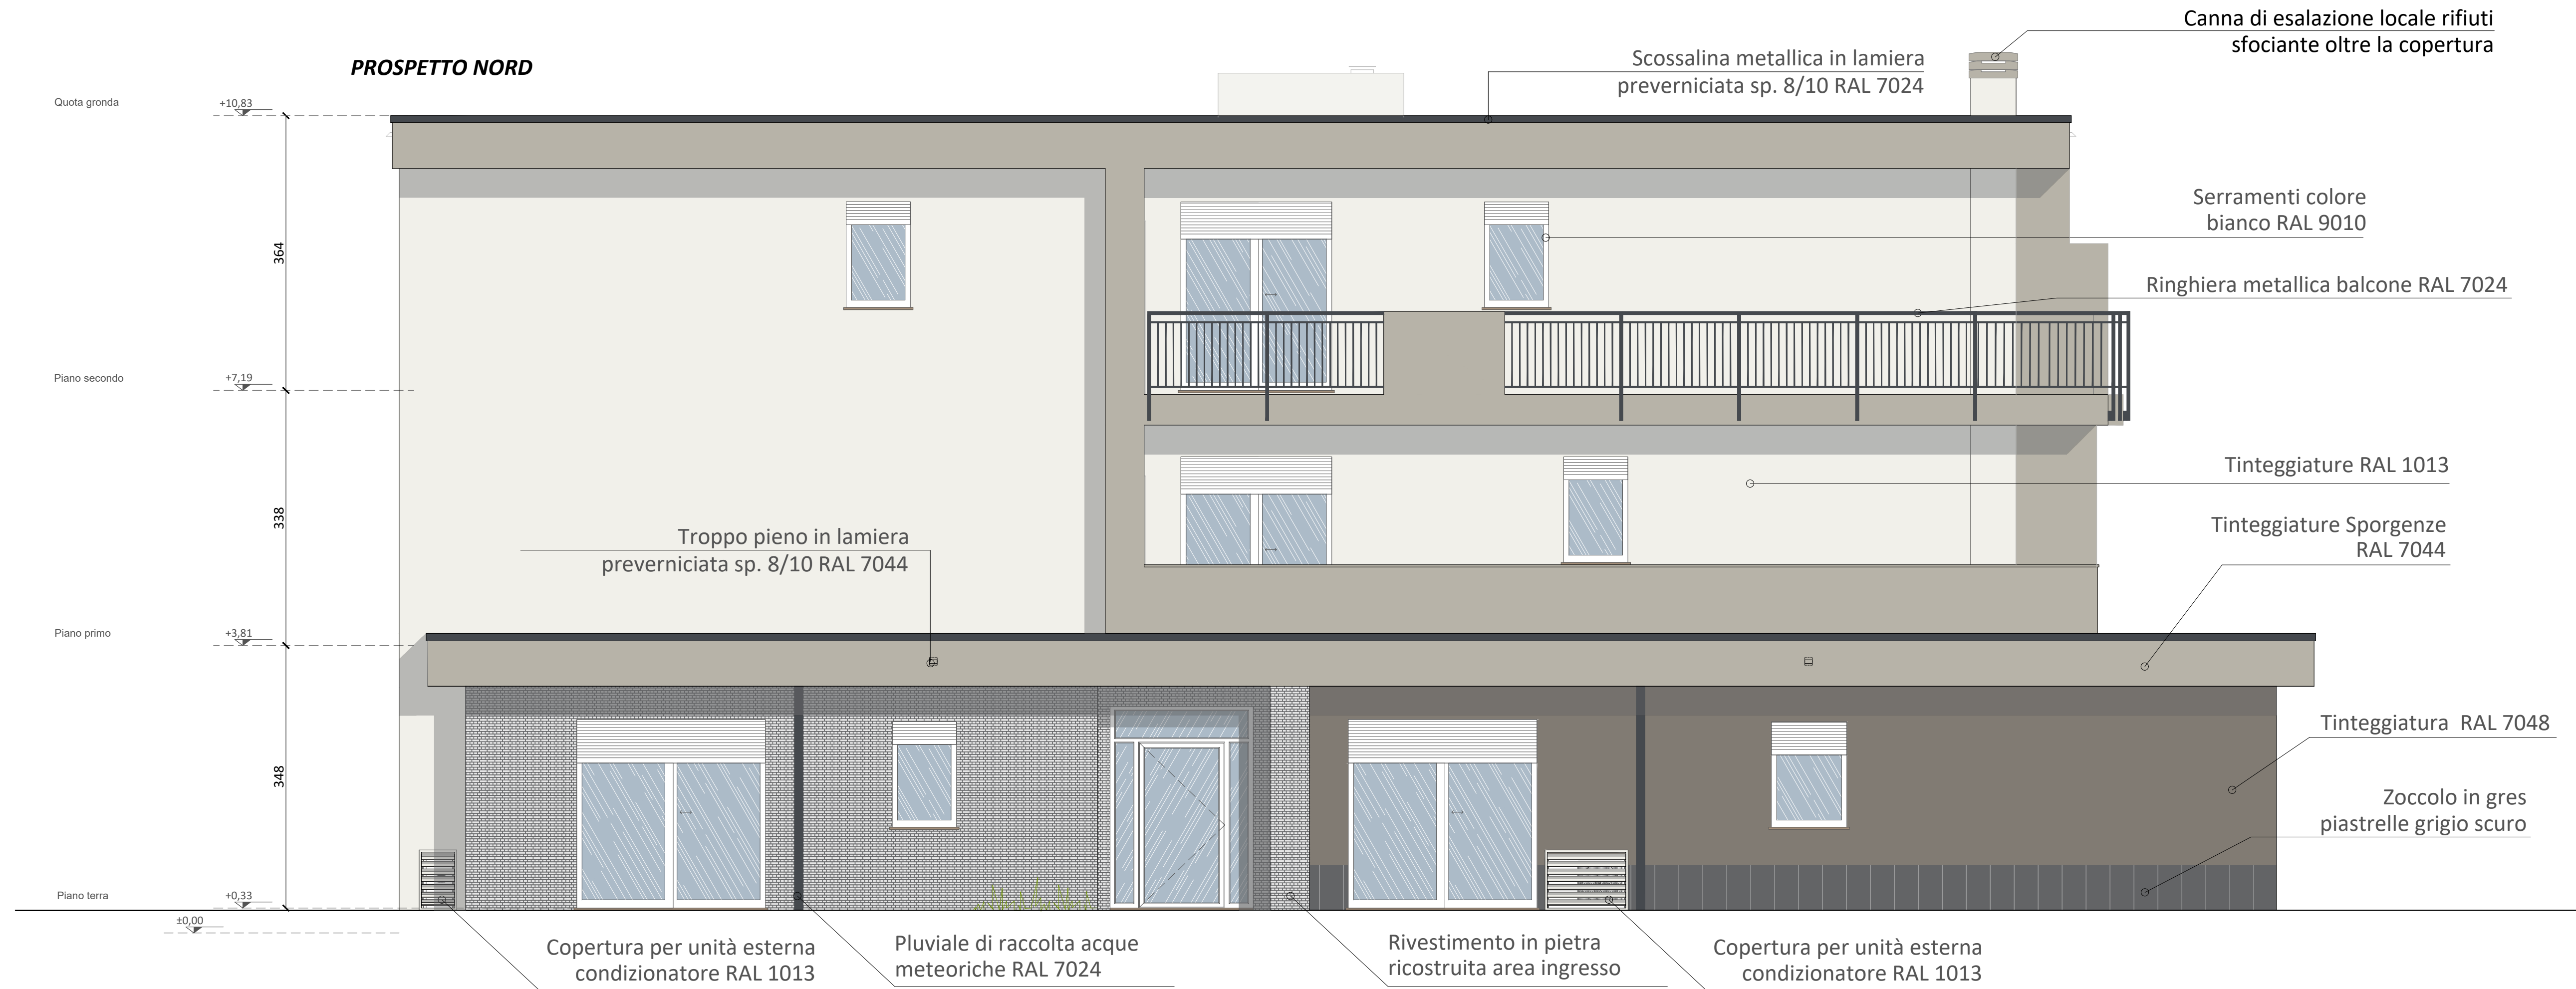

KEYPLAN

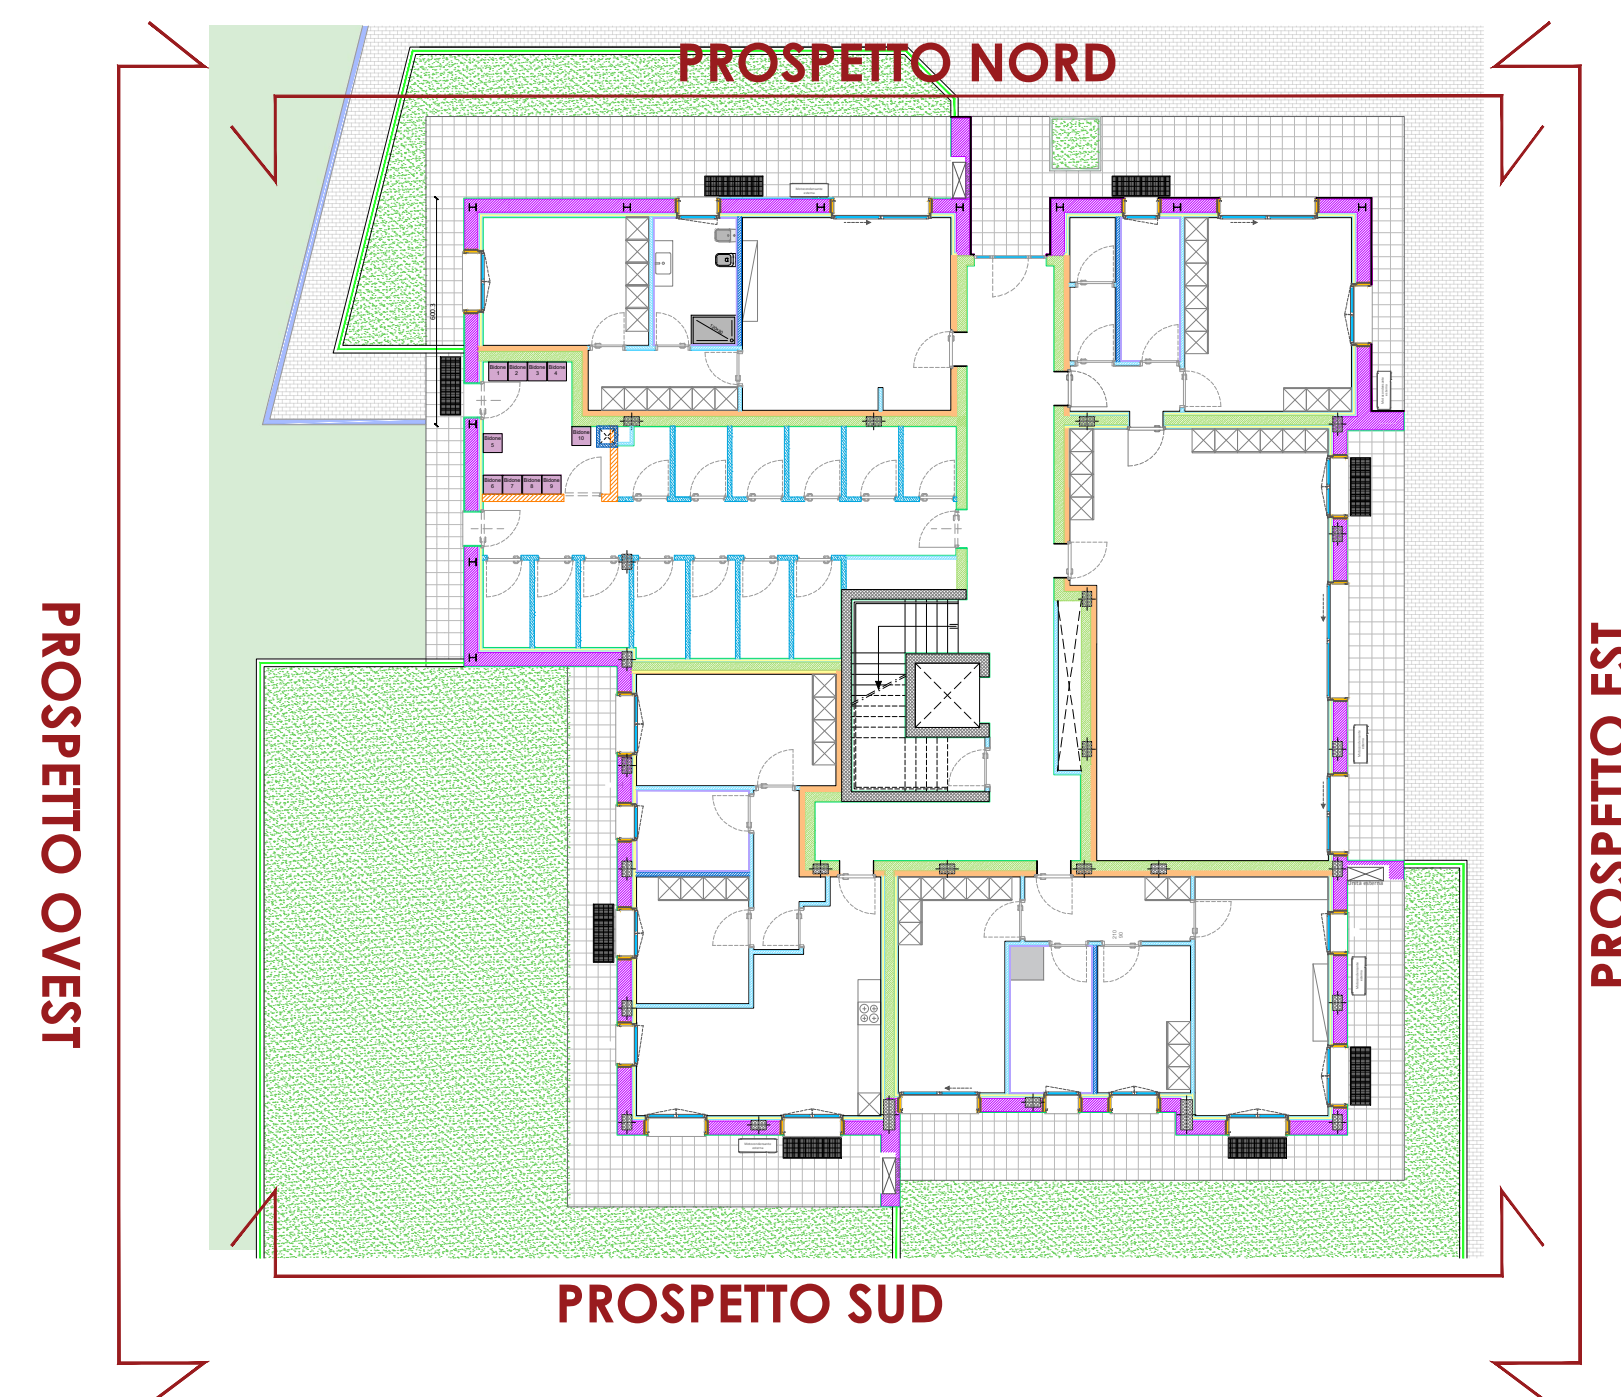

|   |  |   |  |
|---|--|---|--|
| <b>GB&amp;PARTNERS</b><br>SERVIZI E PROGETTI IMMOBILIARI<br>Via Roma, 100 - 20122 Milano<br>Tel. 02 58 58 58 58<br>www.gbpartners.it                                            |  |   |  |
| Il Progettista<br><b>COMUNE DI COLOGNO MONZESE (MI)</b><br><b>AREA Ex TORRIANI ARAS 01</b><br><b>PROGETTO ESECUTIVO</b><br>Progetto Servizi Abitativi Pubblici di via Pergolesi |  | Il Direttore Lavori<br>                                                                                                  |  |
| N° DATA DESCRIZIONE MOTIVAZIONE DELL'AGGIORNAMENTO STUDIO DIS.<br>00 30/03/2025 Prima emissione G.B.&P. L.M.<br>01 11/03/2026 Aggiornamento G.B.&P. L.T.                        |  | Il Committente<br>Progetto<br><b>PROGETTO ESECUTIVO</b><br>Servizi Abitativi Pubblici<br>Comune di Cologno Monzese (MI)  |  |
| PropONENTE<br><b>Officine Mak S.r.l.</b><br>Corso Europa, 10<br>Milano 20122   |  | Scala<br><b>1:50</b>   |  |
| Data<br><b>11/03/2026</b>   |  | Orientamento<br>   |  |
| Tipo tavola<br><b>ARCHITETTONICI</b><br>Serie<br><b>PROGETTO ESECUTIVO</b><br>Titolo<br><b>Stato di progetto</b><br>Prospetti                                                   |  | Tavola nr.<br><b>ARCH</b><br>Tipo<br><b>Tavola</b><br>Scala /<br><b>ES</b><br>Numero /<br><b>11</b><br>Agg.<br><b>01</b> |  |
| Documento di proprietà della Società G.B. & Partners S.r.l. È vietata la riproduzione. Tutti i diritti sono riservati.                                                          |  |   |  |