


Corografia - scala 1:10.000

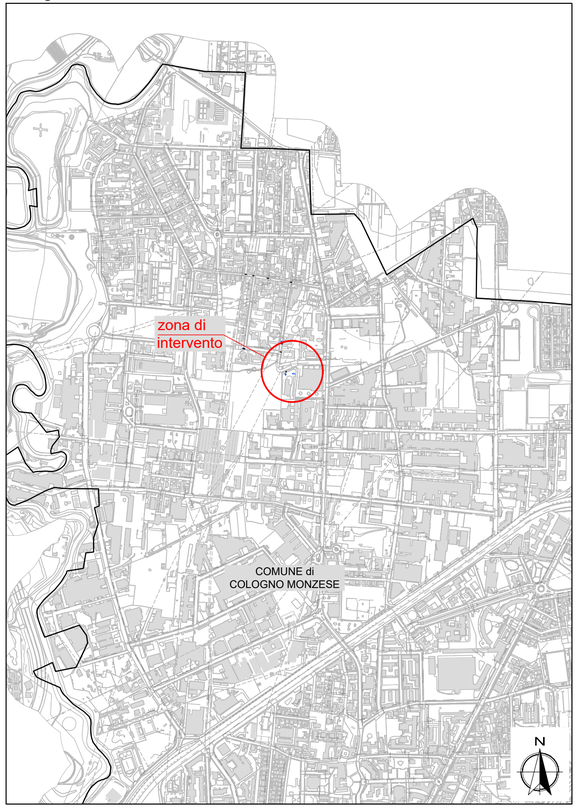


Planimetria stato di fatto - scala 1:1000

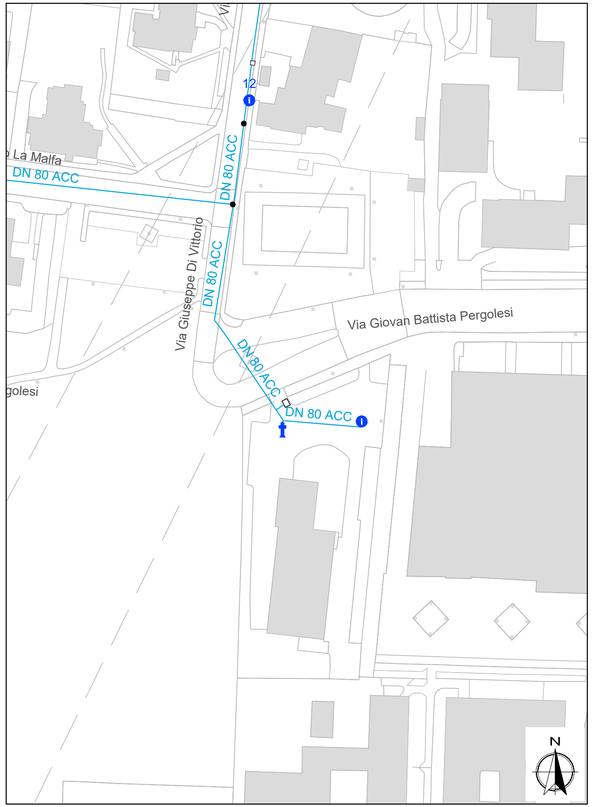

Planimetria di dismissione - scala 1:1000

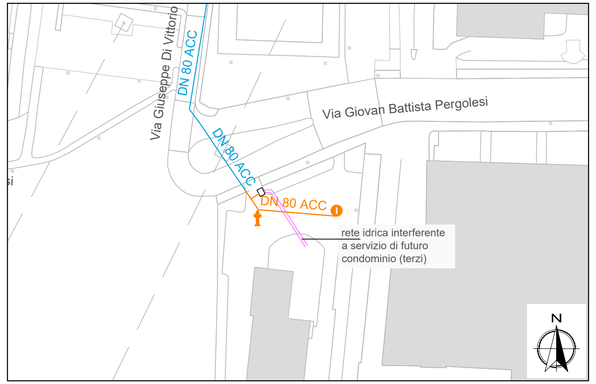

Planimetria di progetto - scala 1:1000

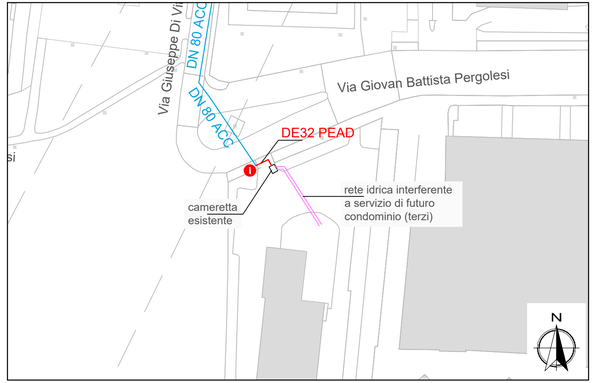

COMUNE DI COLOGNO MONZESE
ACQUEDOTTO

Risoluzione interferenza idrica
Via Pergolesi n.12

STATO DI FATTO / PROGETTO
Corografia - Planimetrie

Legenda:

	esistente	progetto	dismissione
rete idrica			
idrante sottosuolo con saracinesca			
idrante soprasuolo con saracinesca			

Rev	Data	Elaborato	Progettato	Autorizzato	Descrizione
A	09/02/2026	Degradi	ing. Dall'Asta	P.I. Fava	Prima emissione

FILE

Ambito	Anno	Numero CASE	Fase	Categoria	Disciplina	Tavola N°	Rev.	Tipo Elaborato
A	26	H26AURG02	PE	T	GEN	001	A	PLA

Elaborato realizzato da: Ufficio Supporto Progetti
supporto.progetti@gruppocap.it
Progettazione realizzata da: Settore gestione acquedotto

Scala: indicata

Disciplina: GEN
Tavola N°: 001

CAP Holding spa - Via Rimini, 38 - 20142 Milano (MI)
Tel. 02 825021 - info@gruppocap.it - PEC:capholding@legalmail.it

Questo disegno è di nostra proprietà esclusiva ed è posto sotto tutela della legge, ne è proibita la riproduzione anche parziale e la cessione a terzi senza nostra autorizzazione scritta.

CAP ACQUA CHE GENERA FUTURO