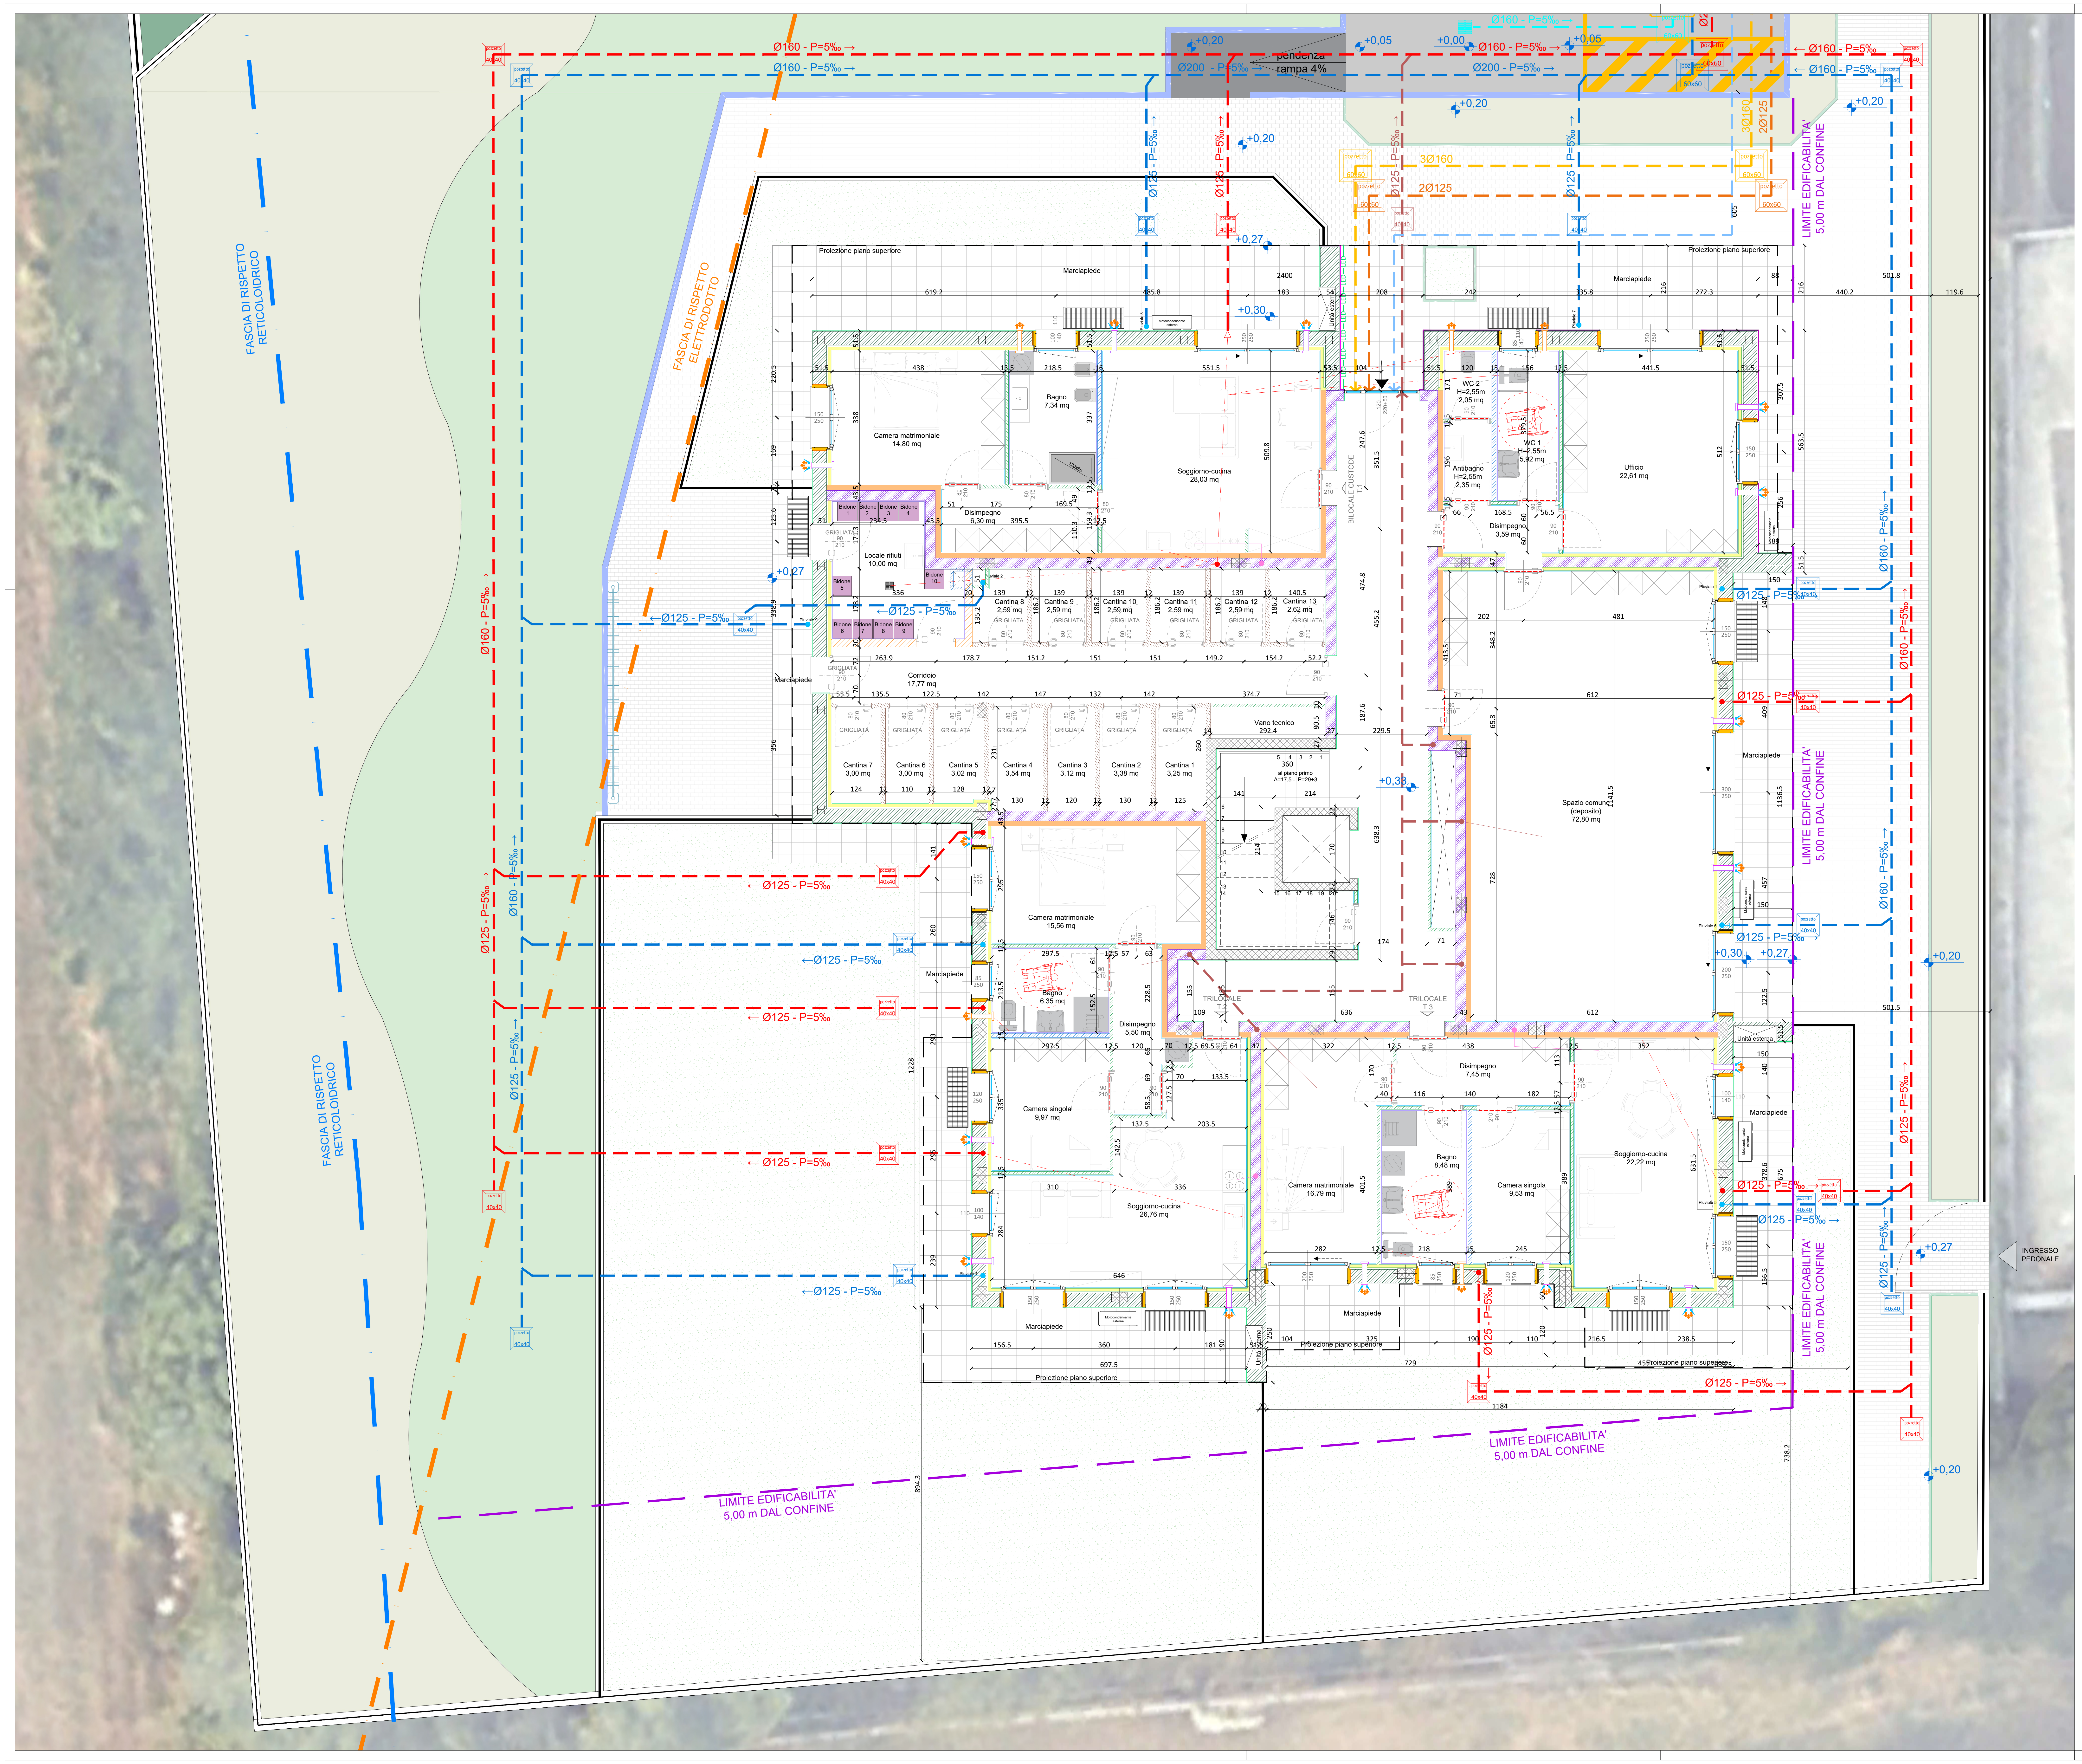

LEGENDA

▦	Pavimentazione in autobloccante filtrante
▩	Cemento armato
▨	Muratura in blocchi "Tipo Normablok" o equivalente sp. 35 cm
▨	Muratura in blocchi "Tipo Poroton serie P800" o equivalente sp. 25 cm
▨	Parete interna in cartongesso con struttura interna da 7,5 cm + doppia lastra su ogni lato
▨	Parete interna in cartongesso con struttura interna da 10 cm + doppia lastra su ogni lato
▨	Parete divisoria cantine in cls a vista spessore 12 cm
▨	Parete divisoria cantine in cls a vista spessore 20 cm
▨	Parete in CLS spessore 8 cm - canna esalazione locale rifiuti
🟨	Pannello isolante di lana minerale "Tipo Isover Extrawall" o quivalente spessore 7,5 cm
🟧	Pannello isolante, spessore 12,5 cm
═	Intonaco esterno spessore 2 cm
═	Doppia lastra in cartongesso 1,25 + 1,25 cm
━	Rivestimento in gres 30x30cm posato a colla con fuga da 2mm H= 200cm
━	Rivestimento in pietra ricostruita a tutta altezza (area ingresso alla palazzina)
LED━LED━LED	Profilo led flessibile tipo "FiloFlex" a parete
━	Recinzione metallica tassellata su muretto in CA
- - -	Giunto pavimento
- - -	Proiezione piano superiore
● - - -	Indicazione dell'utenza a cui si riferisce la colonna
●	Colonna di scarico acque nere Ø110 mm - sezionato
○	Colonna di scarico acque nere Ø110 mm - proiezione
●	Colonna di scarico acque condensa Ø32 mm - sezionato
○	Colonna di scarico acque condensa Ø32 mm - proiezione
●──	Indicazione dell'unità immobiliare a cui si riferisce la colonna condense
●	Colonna cappa cucina Ø125 mm - sezionato
●──→	Indicazione dell'unità immobiliare a cui si riferisce la cappa segnalata
○	Colonna cappa cucina Ø125 mm - proiezione
●	Pluviale / Discesa acque bianche Ø125 mm - sezionato
○	Pluviale / Discesa acque bianche Ø125 mm - proiezione
▤	Piletta di raccolta acque di lavaggio locale rifiuti
⇶	Unità di VMC decentralizzata Ø100mm e Ø150mm a singolo flusso continuo Marca "Aerauliqa" - Modello "Quantum EX"
⇶	Unità di VMC decentralizzata a singolo flusso alternato con recupero di calore Marca "Aerauliqa" - Modello "Orion"
- - -	Rete a terra condense
- - -	Rete a terra acque nere
- - -	Rete a terra acque meteoriche pluviali
- - -	Rete a terra acque meteoriche caditoie
- - -	Rete a terra adduzione idrica
- - -	Rete Linea Telecom
- - -	Rete Linea Enel
━	Cordolo larghezza 7 cm
━	Cordolo larghezza 15 cm

GB&PARTNERS
SERVIZI E PROGETTI IMMOBILIARI
Via Varalli 37, 26845 Codogno (LO)
Telefono 0377 436099 - 0377 34691 - **Fax** 0377 436654
E-mail amministrazione@gbepartners.it - tecnico@gbepartners.it
www.gbepartners.it
REGISTRO IMPRESE DI LODI n°05966150962
PARTITA I.V.A / C.F. 05966150962
C.S. € 11.111,10 iv

UNI EN ISO 9001:2015
UNI EN ISO 14001:2015
Certificazione n. CR-2881PG/001
Norma: UNI/PdR 125:2022

COMUNE DI COLOGNO MONZESE (MI)
AREA Ex TORRIANI ARAS 01
PROGETTO ESECUTIVO
Progetto Servizi Abitativi Pubblici di via Pergolesi

N°	DATA	DESCRIZIONE MOTIVAZIONE DELL'AGGIORNAMENTO	STUDIO	DIS.
00	30/01/2026	Prima emissione	G.B.&P.	L.M.
01	11/03/2026	Aggiornamento	G.B.&P.	L.T.

Il Progettista

Collegio Provinciale Geometri e Geometri Laureati di Lodi
Iscrizione Albo N. 267
Geometra
Gianpiero Bianchi

Architetto Cristiano Schiavi 421

Il Direttore Lavori

Il Committente

Progetto	Proponente	Scala
PROGETTO ESECUTIVO ***Servizi Abitativi Pubblici*** *Comune di Cologno Monzese(MI)*	***Officine Mak S.r.l.*** *Corso Europa, 10* *Milano 20122*	**1:50** Data 11/03/2026

Tipo tavola
ARCHITETTONICI

Serie
PROGETTO ESECUTIVO

Titolo
PIANTA PIANO TERRA
Aree interne al fabbricato

Tavola nr.

Tipo Tavola	**ARCH**
Sigla / Serie	**ES**
Numero / Variante	**06**
Agg.	**01**

Orientamento

N

Documento di proprietà della Società G.B. & Partners S.r.l.. E' Vietata la riproduzione. Tutti i diritti sono riservati.