

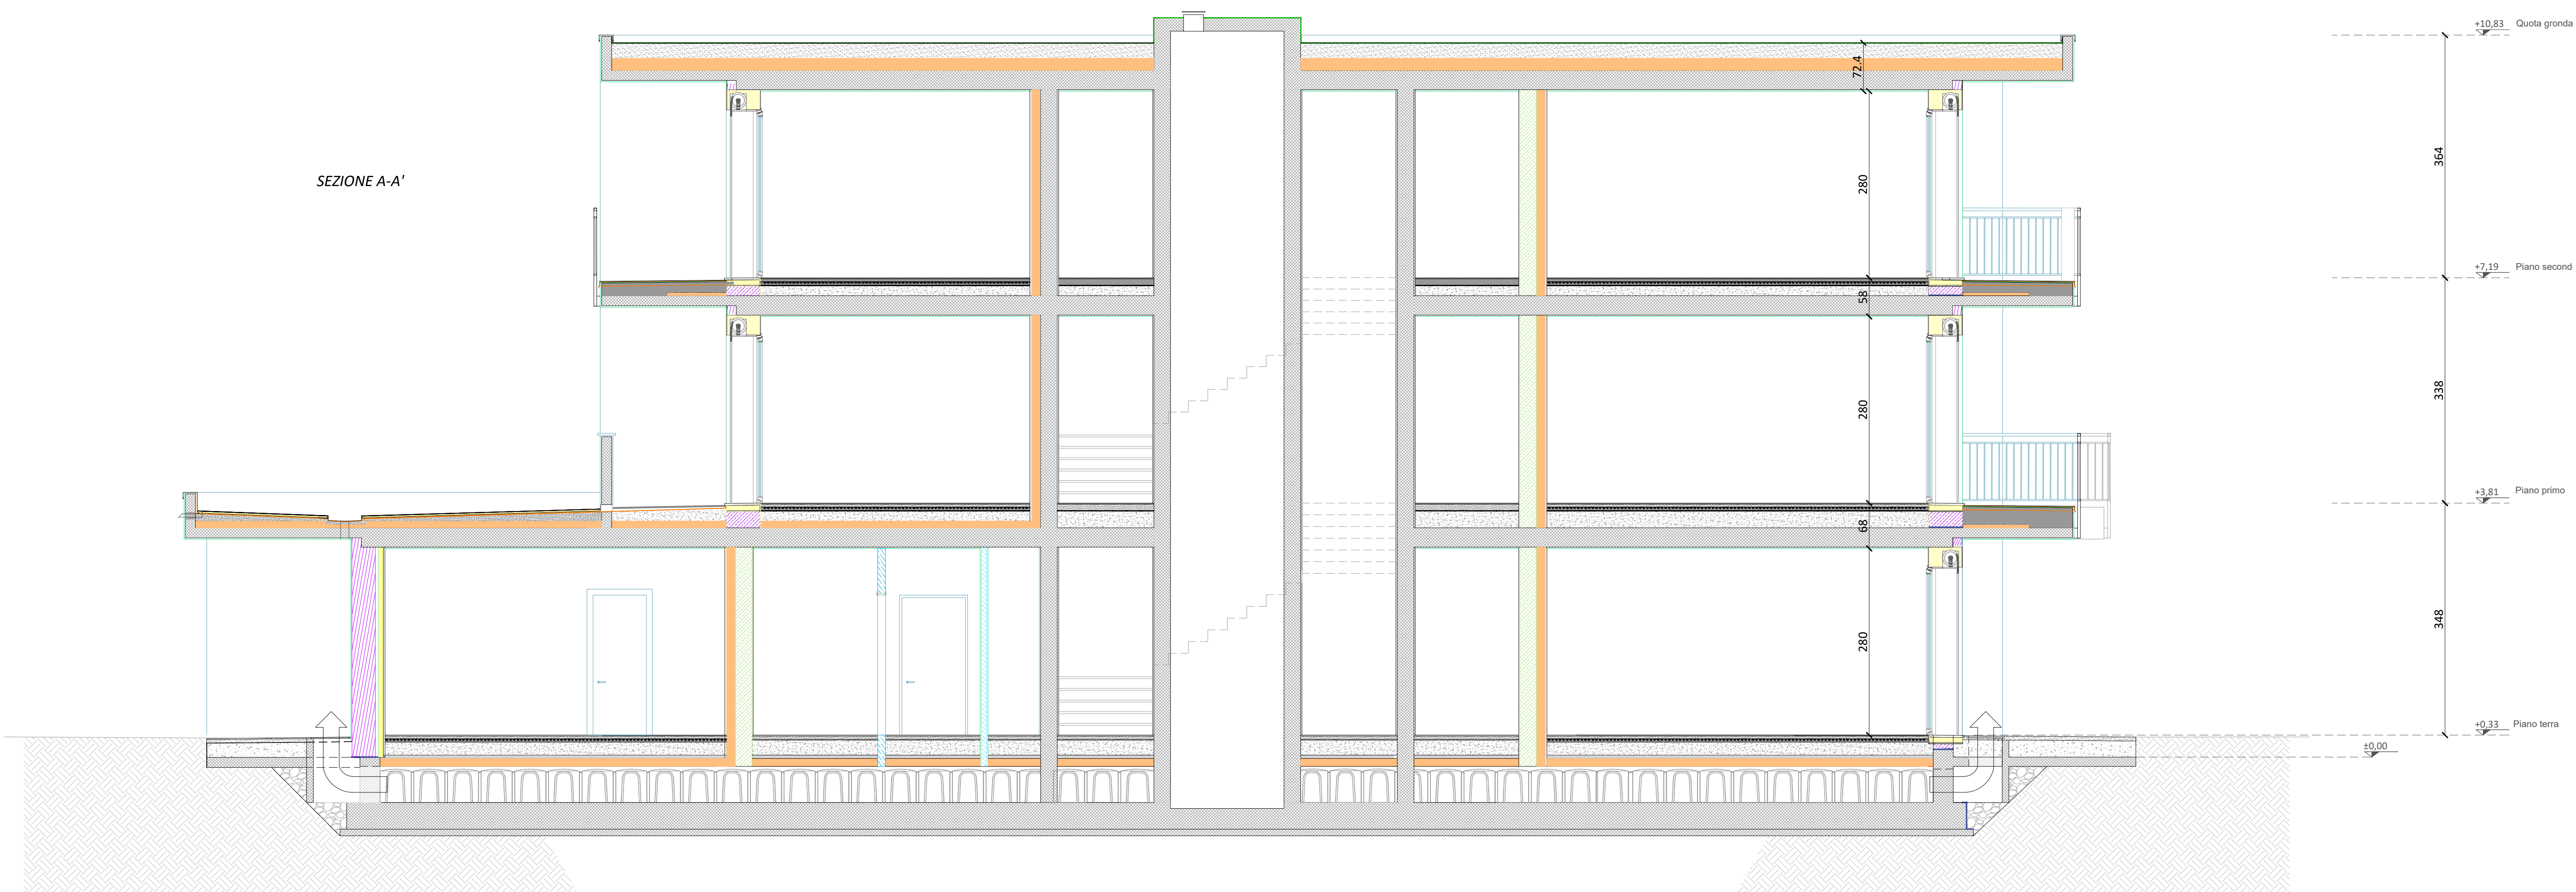
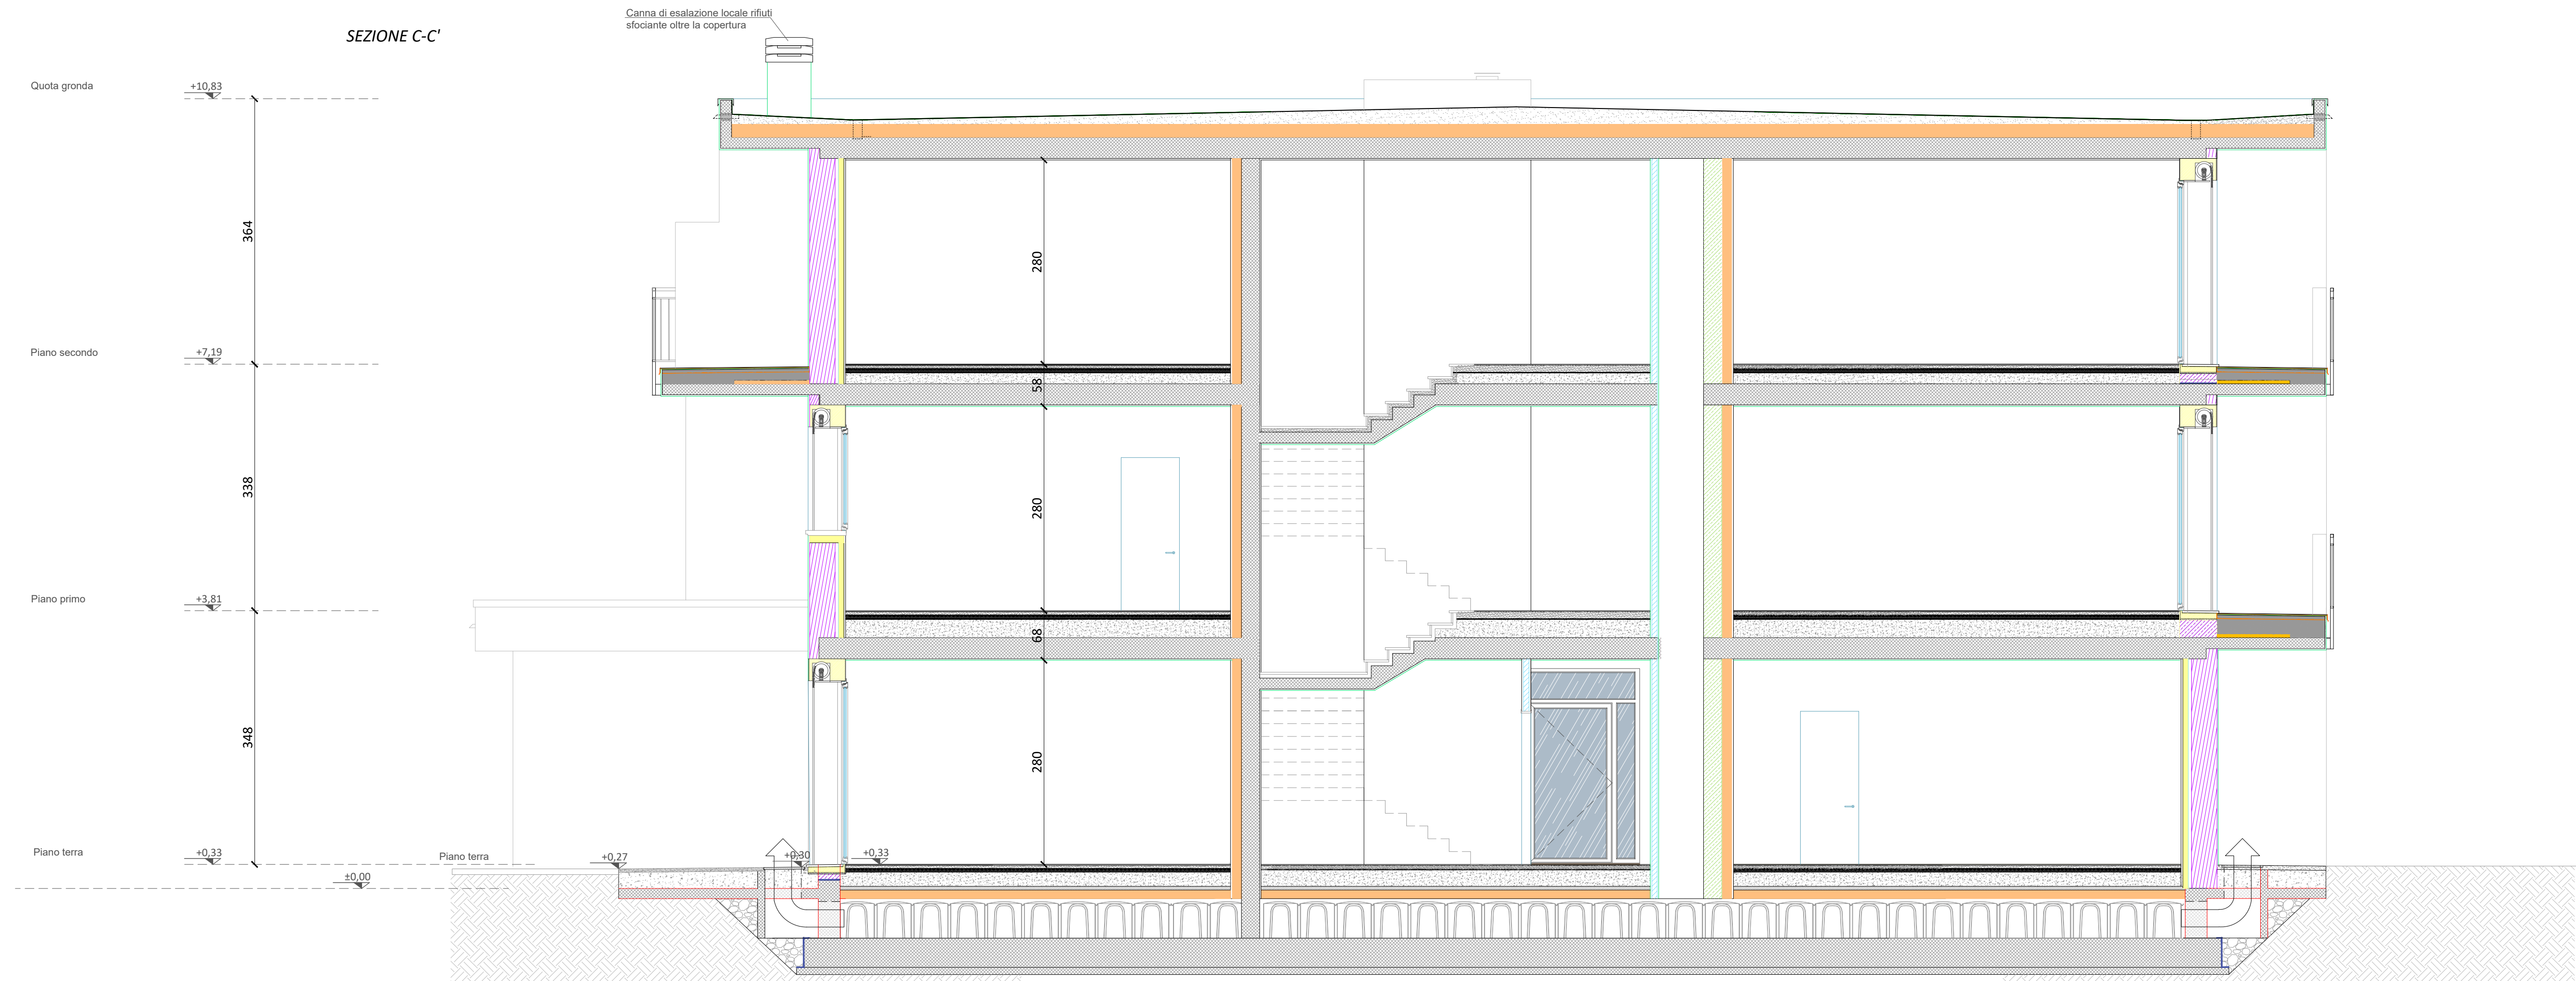


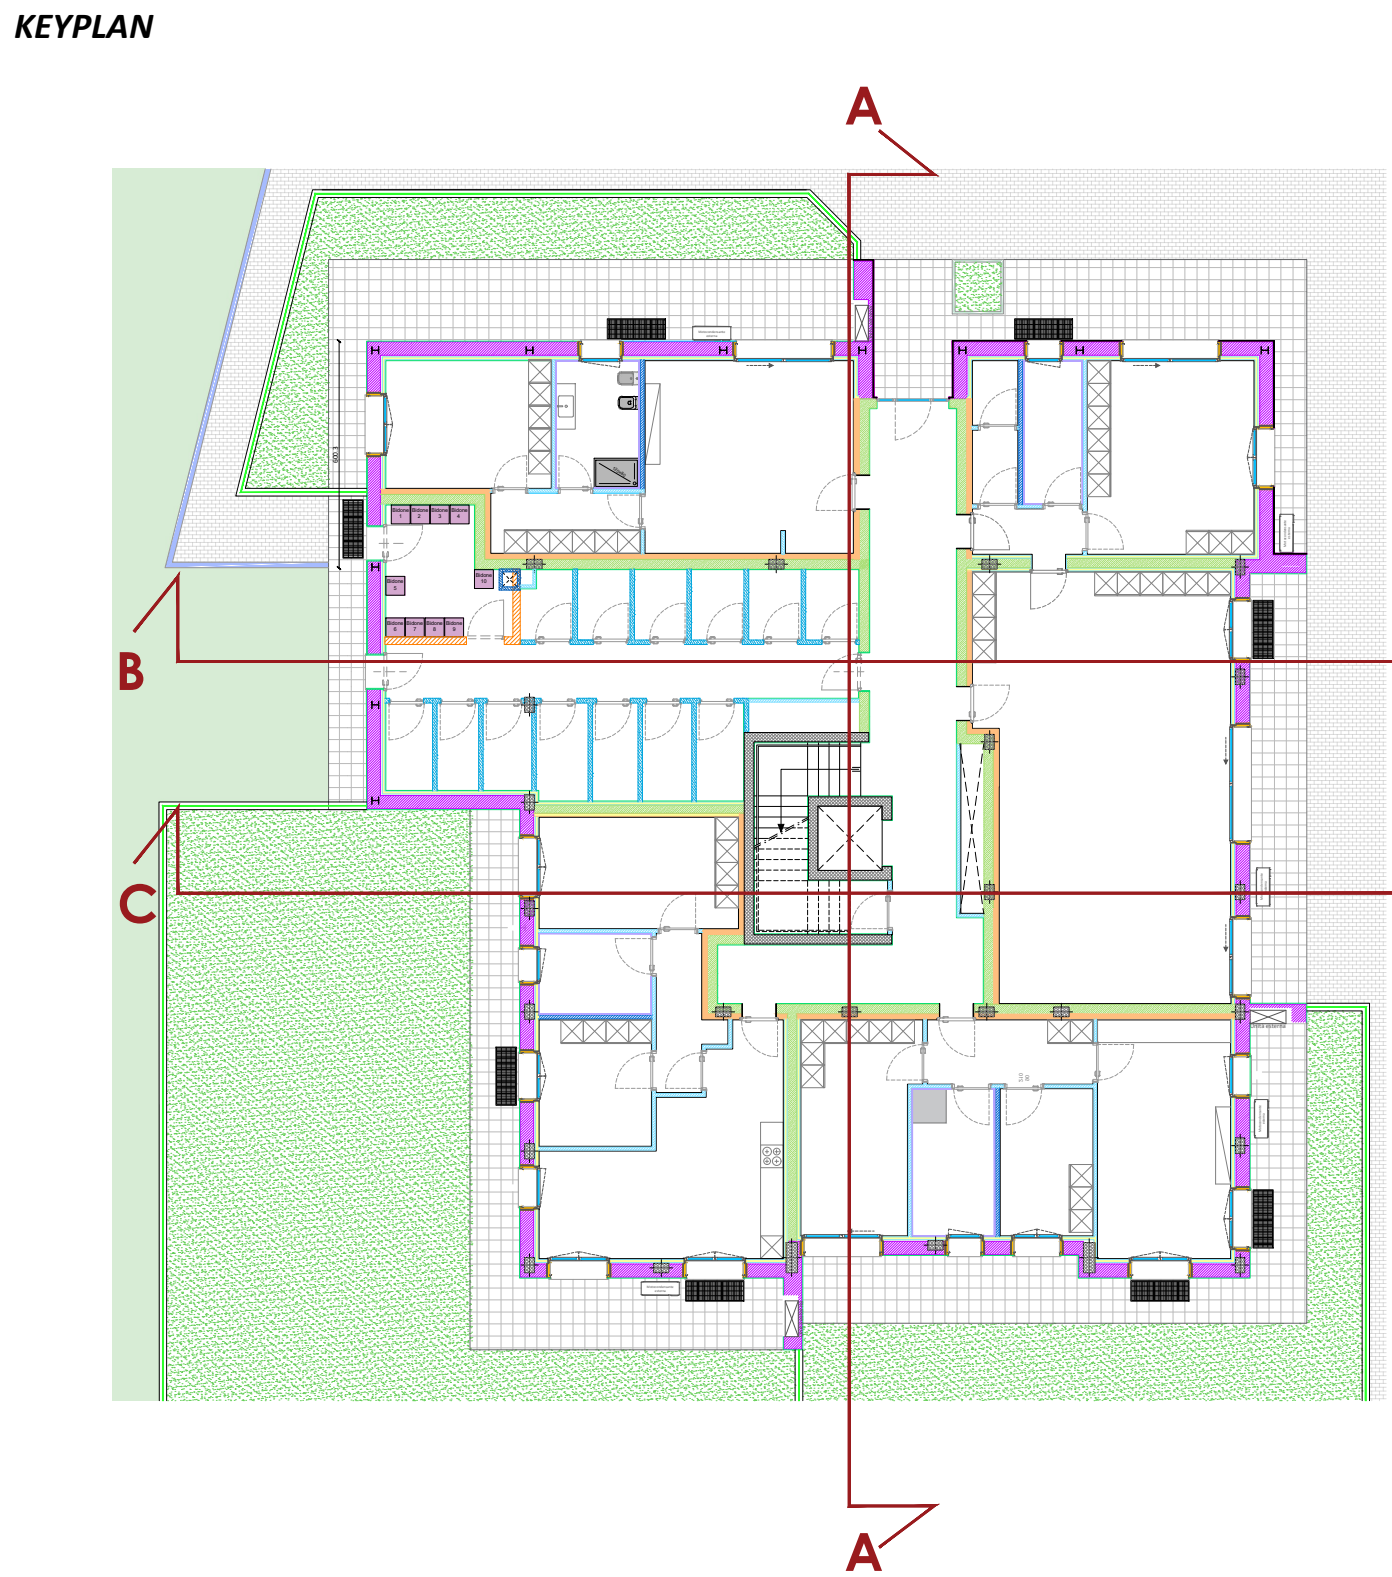

LEGENDA	
Piani fuori terra	
	Cemento armato
	Muratura in blocchi "Tipo Poroton serie P800" o equivalente sp. 35 cm
	Muratura in blocchi "Tipo Poroton serie P800" o equivalente sp. 25 cm
	Parete interna in cartongesso con struttura interna da 7,5 cm + doppia lastra su ogni lato
	Parete interna in cartongesso con struttura interna da 10 cm + doppia lastra su ogni lato
	Parete in blocchi di cemento a vista spess. 12 cm
	Pannello isolante, spessore 12,5 cm
	Intonaco esterno spessore 2 cm
	Doppia lastra in cartongesso 1,25 + 1,25 cm

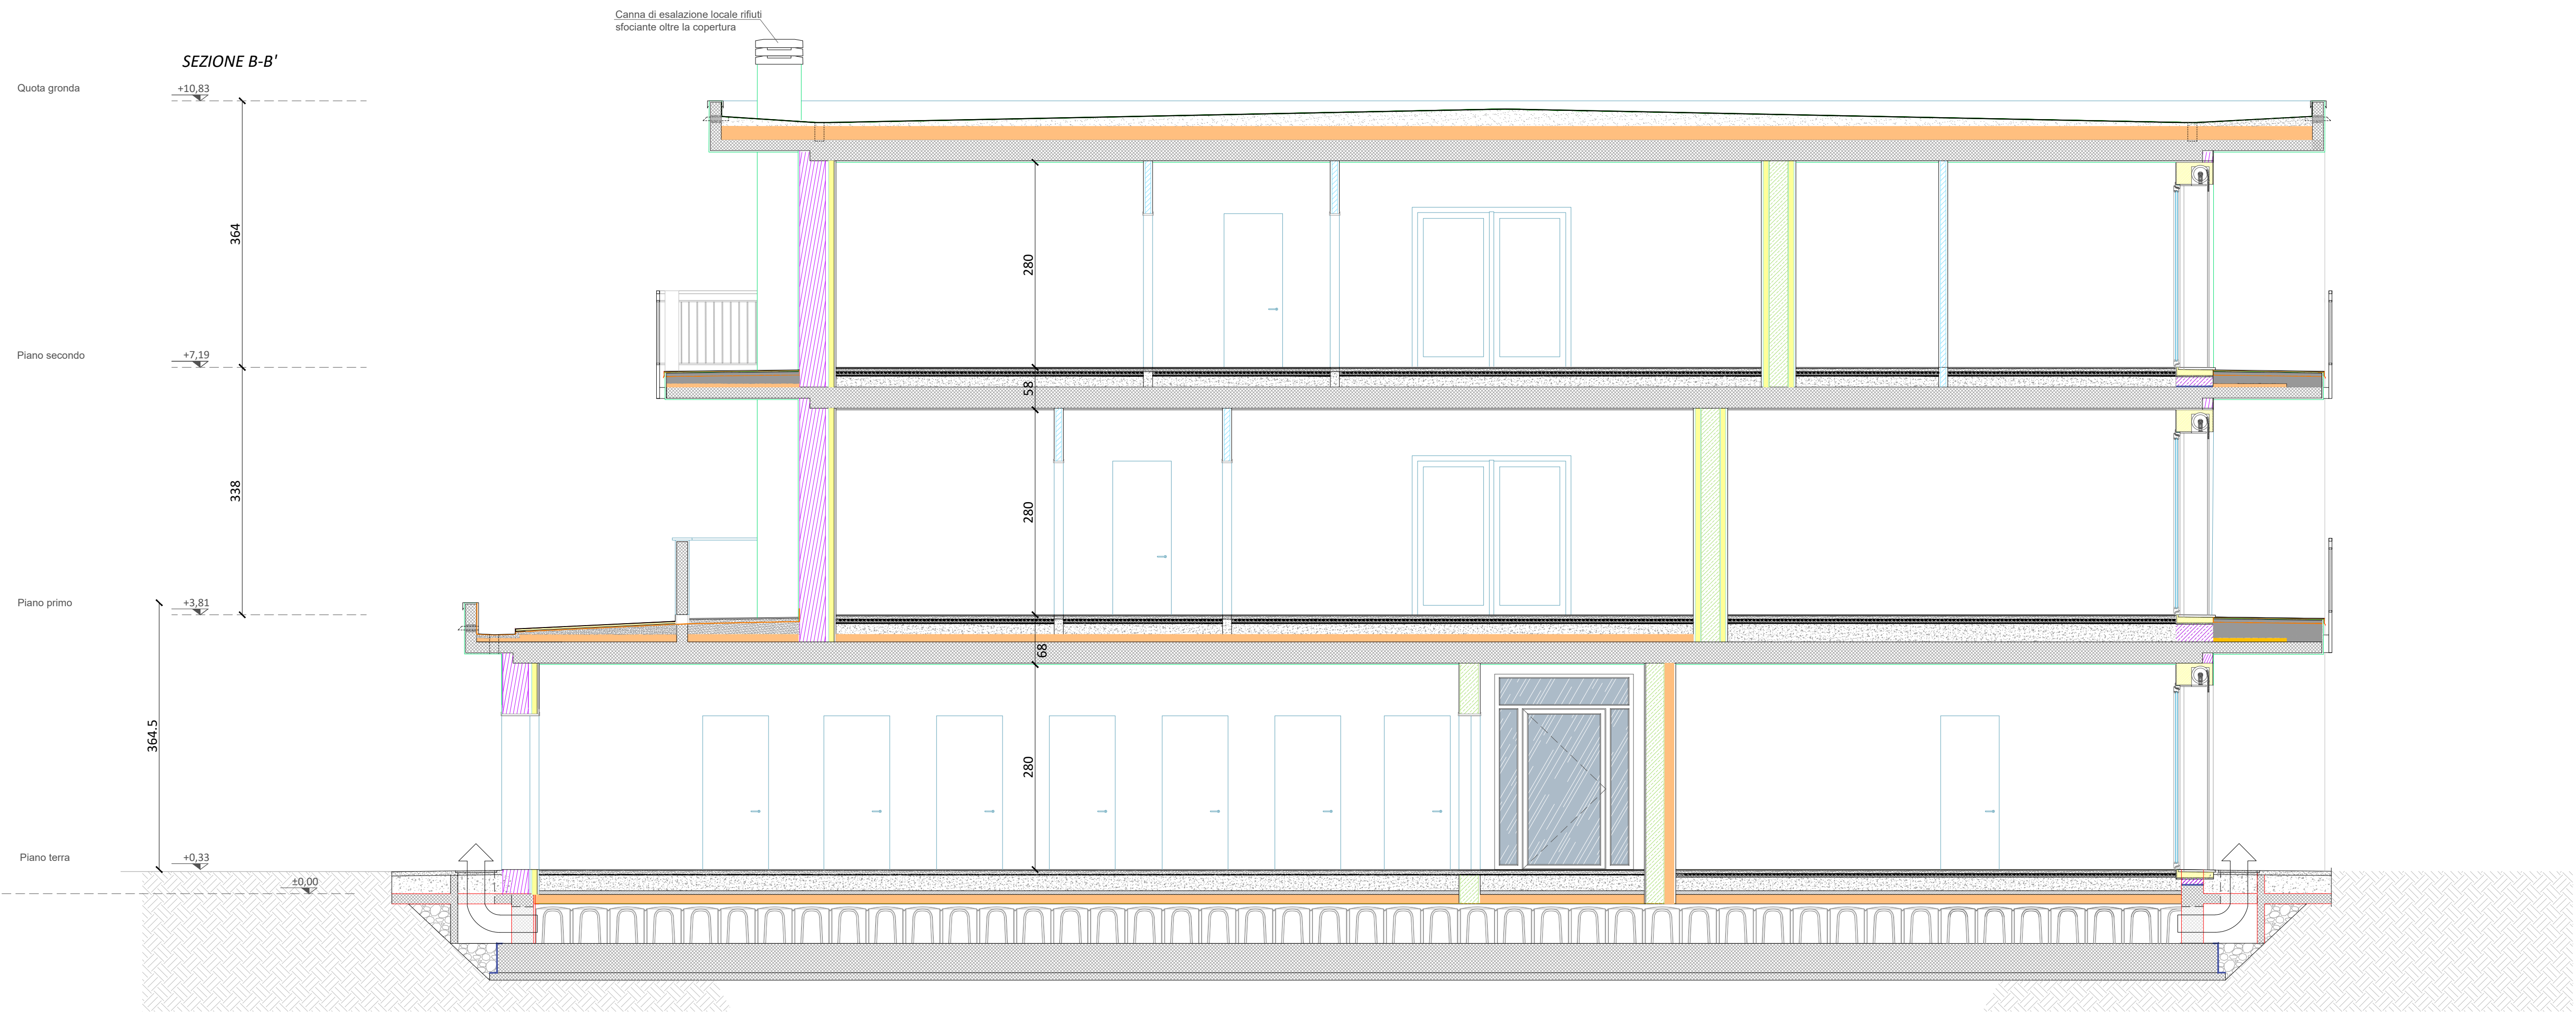

GB&PARTNERS
SERVIZI PROGETTI IMMOBILIARI
Via Dante 30, 20121 Milano (MI) - Tel. 02 48121111 - Fax 02 48121112
E-mail: gb@gbpartners.it - gbpartners.it

COMUNE DI COLOGNO MONZESE (MI)
AREA Ex TORRIANI ARAS 01
PROGETTO ESECUTIVO
Progetto Servizi Abitativi Pubblici di via Pergolesi

N°	DATA	DESCRIZIONE	MOTIVAZIONE DELL'AGGIORNAMENTO	STUDIO	DIS.
00	30/01/2026	Prima emissione		G.B.&P.	L.M.

Progetto PROGETTO ESECUTIVO Servizi Abitativi Pubblici Comune di Cologno Monzese(MI)	Proponente Officine Mak S.r.l. Corso Europa, 10 Milano 20122	Scala 1:50 Data 30/01/2026
---	--	--

Tipo tavola ARCHITETTONICI Serie PROGETTO ESECUTIVO Titolo SEZIONI	Tavola nr. Tipo Tavola ARCH Serie ES Numero / Variante 11 Agg. 00
--	--

Il Progettista

Gianpietro Bianchi

Il Direttore Lavori

Il Committente

Orientamento

Documento di proprietà della Società G.B. & Partners S.r.l. E' vietata la riproduzione. Tutti i diritti sono riservati.