

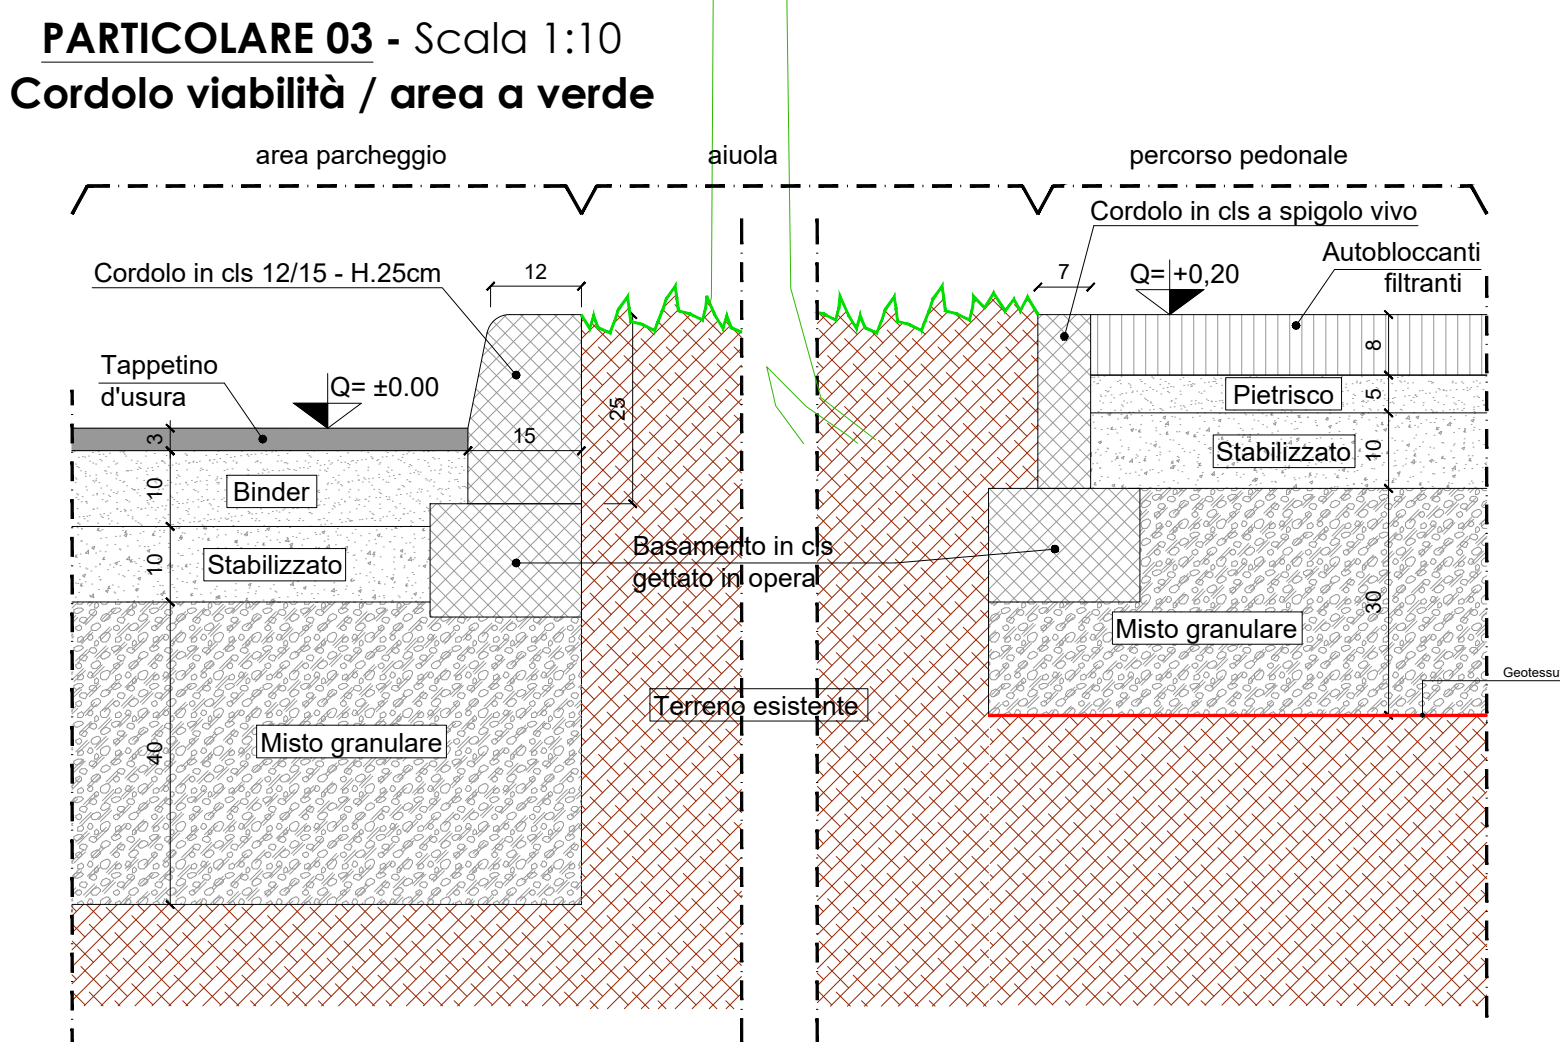
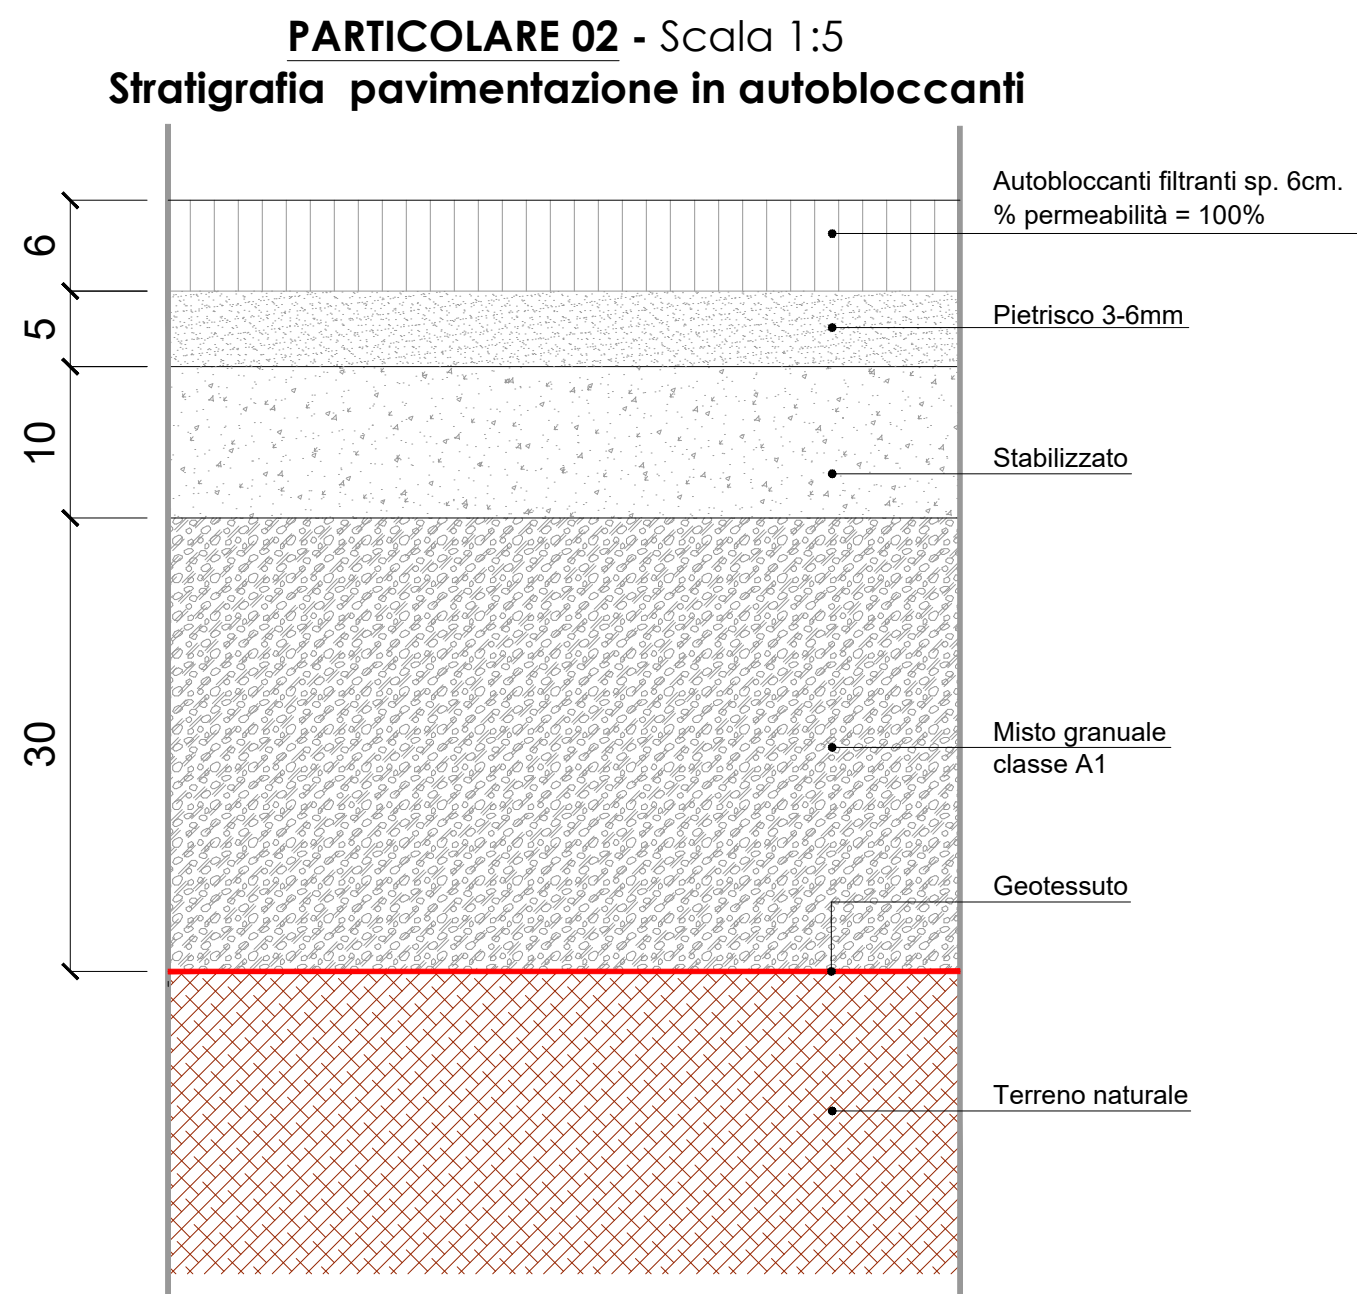
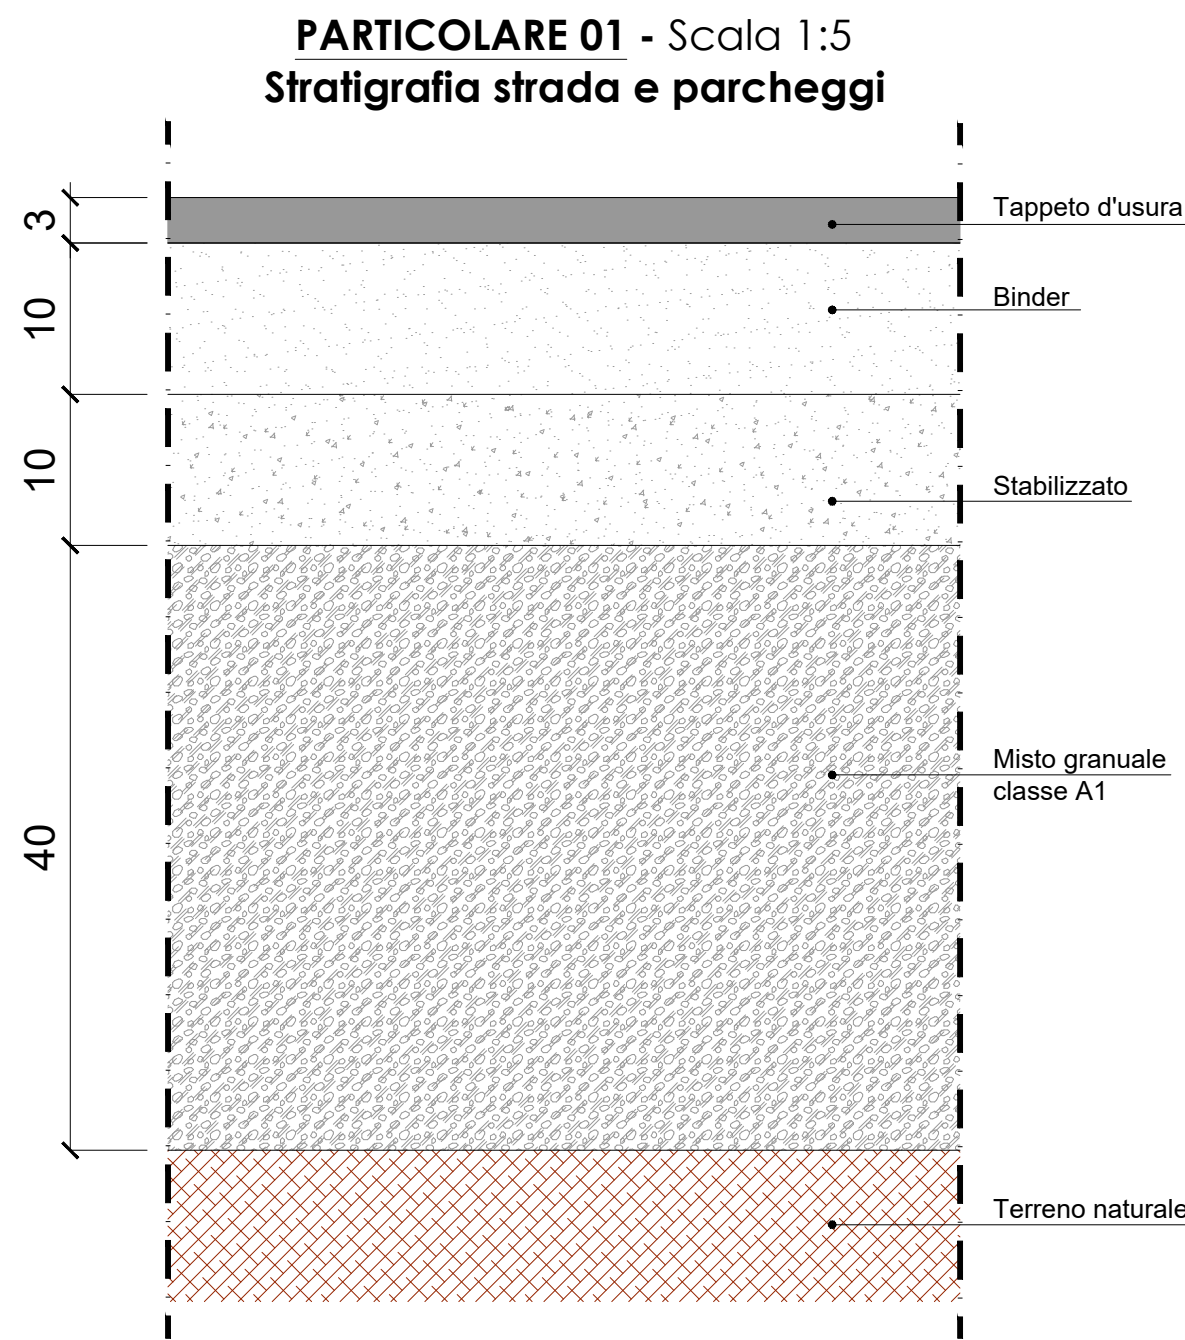


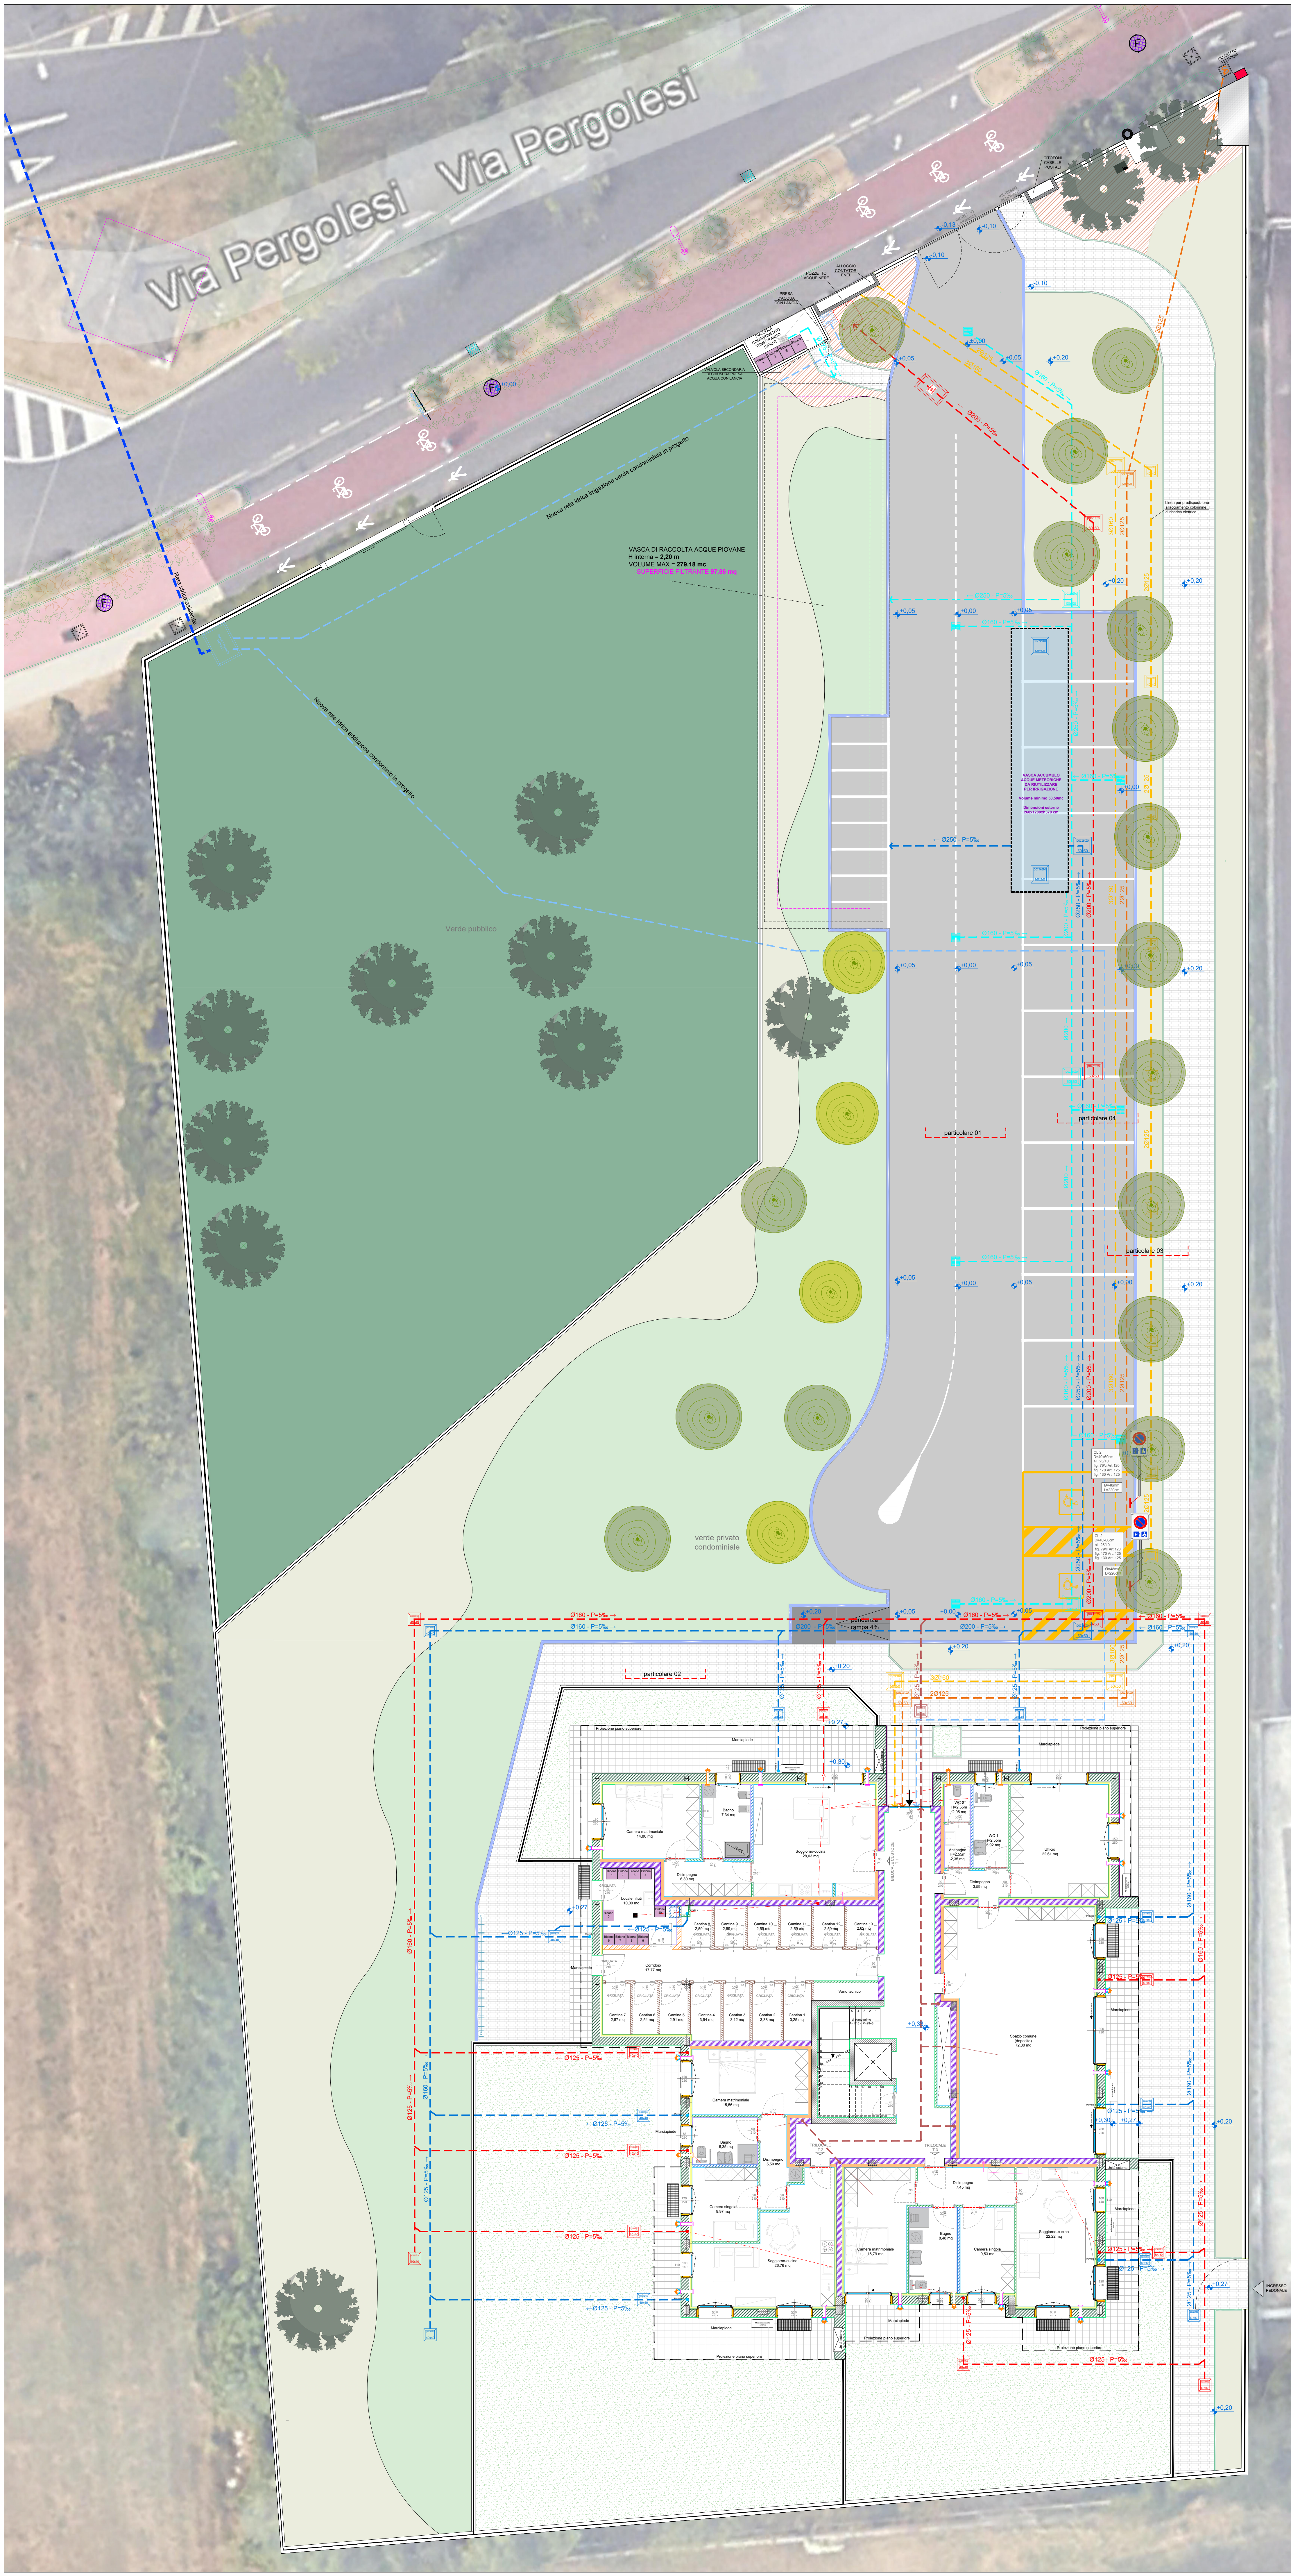

PARTICOLARE 04 - Scala 1:20
PARTICOLARE CADITOIA E COLLEGAMENTO CONDOTTA

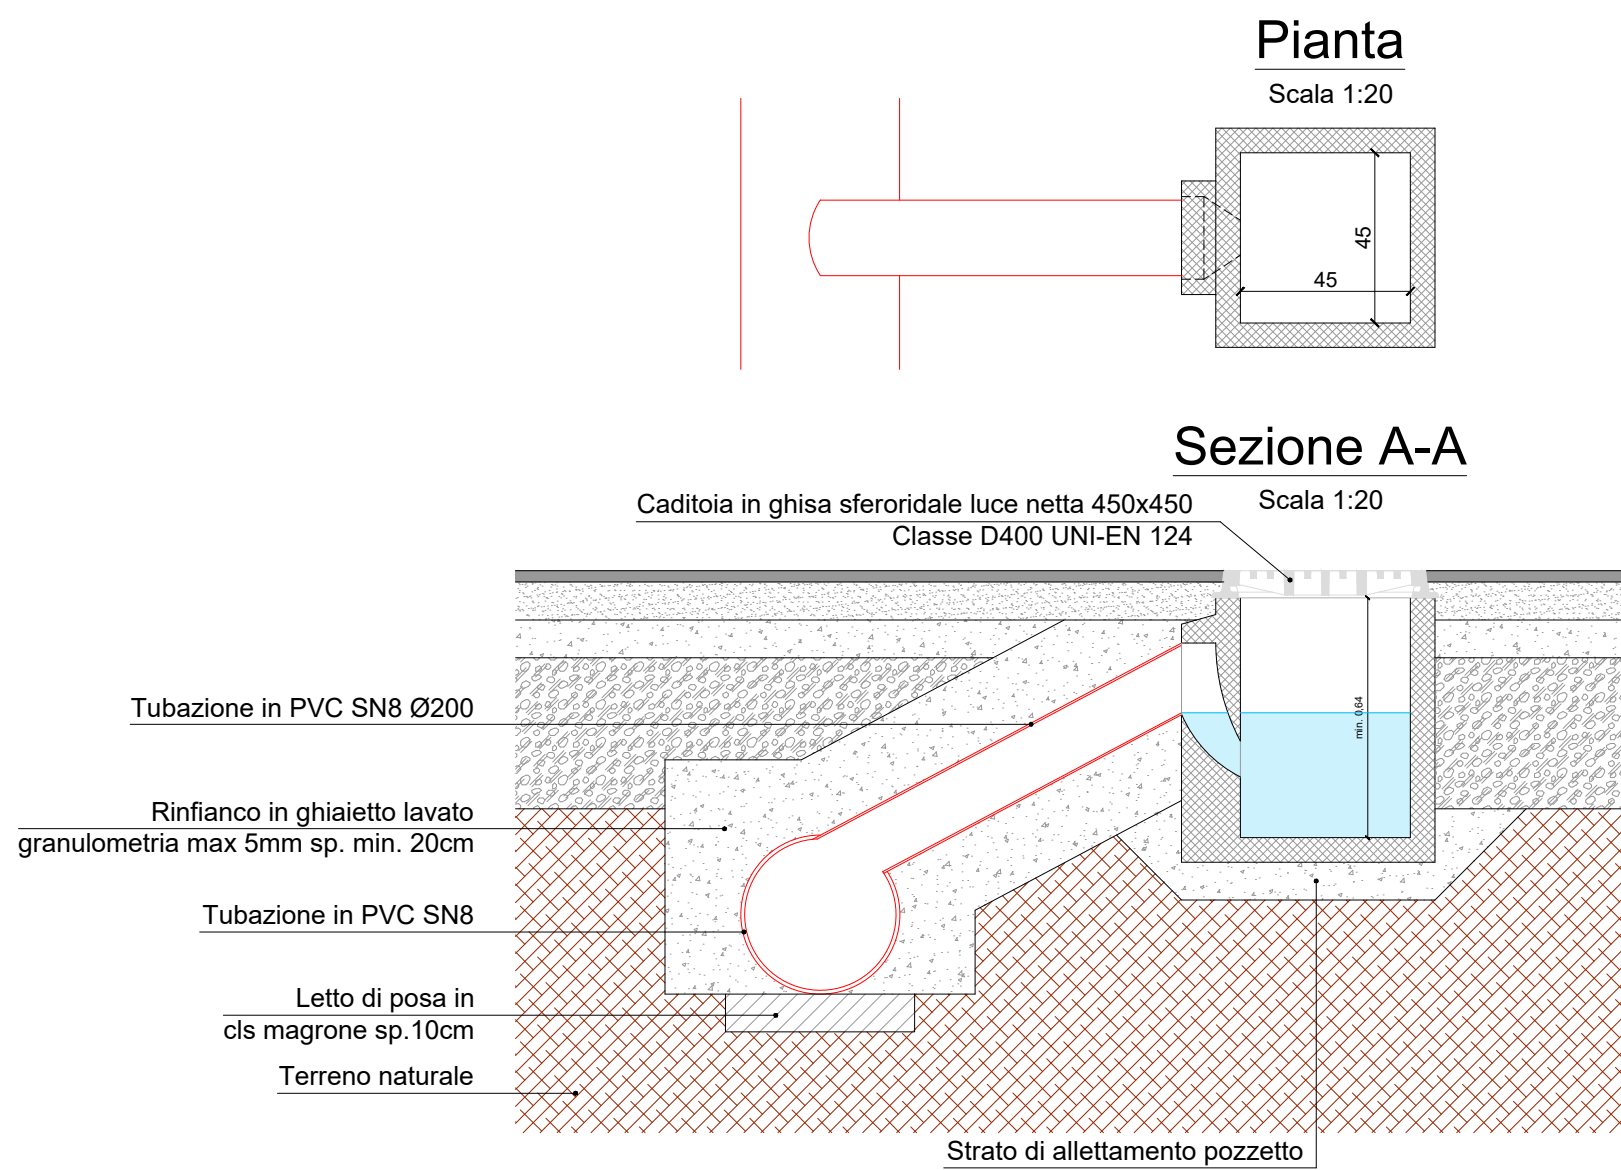

LEGENDA	
	CORDOLO IN CLS 12 / 15 cm
	CORDOLO IN CLS 7 cm
	Proiezione piano superiore
	Rete di scarico acque nere palazzina
	Pozzetto ISB 120x60
	Rete di scarico acque di condensa palazzina
	Rete di scarico acque meteoriche palazzina
	Caditoia acque meteoriche strada e parcheggi
	Rete di scarico acque meteoriche strada e parcheggi
	Linea adduzione idrica in progetto
	Linea telecomunicazioni in progetto
	Linea elettrica in progetto
	Linea elettrica in progetto - predisposizione allacciamento cabine di ricarica elettrica

GB&PARTNERS
SERVIZI E PROGETTI IMMOBILIARI
Via Verdi 10 - 20122 Milano (MI)
Tel. 02 58 58 58 58
Fax 02 58 58 58 58
E-mail: gb@gbpartners.it
www.gbpartners.it

COMUNE DI COLOGNO MONZESE (MI)
AREA Ex TORRIANI ARAS 01
PROGETTO ESECUTIVO
Progetto Servizi Abitativi Pubblici di via Pergolesi

Il Progettista
Cologno Monzese (MI)
Via Verdi 10
020122
02 58 58 58 58
gb@gbpartners.it
www.gbpartners.it
Giampiero Binioli

Il Direttore Lavori
Cologno Monzese (MI)
Via Verdi 10
020122
02 58 58 58 58
gb@gbpartners.it
www.gbpartners.it
Giampiero Binioli

Il Committente
Progetto
PROGETTO ESECUTIVO
Servizi Abitativi Pubblici
Comune di Cologno Monzese (MI)

Proponente
Officine Mak S.r.l.
Corso Europa, 10
Milano 20122

Scala
1:100

Data
30/01/2026

Tavola nr.
ARCH

Serie
ES

Numero / Valore
12

Pag.
00

Documentazione di proprietà della Società G.B. & Partners S.r.l. E' vietata la riproduzione. Tutti i diritti sono riservati.