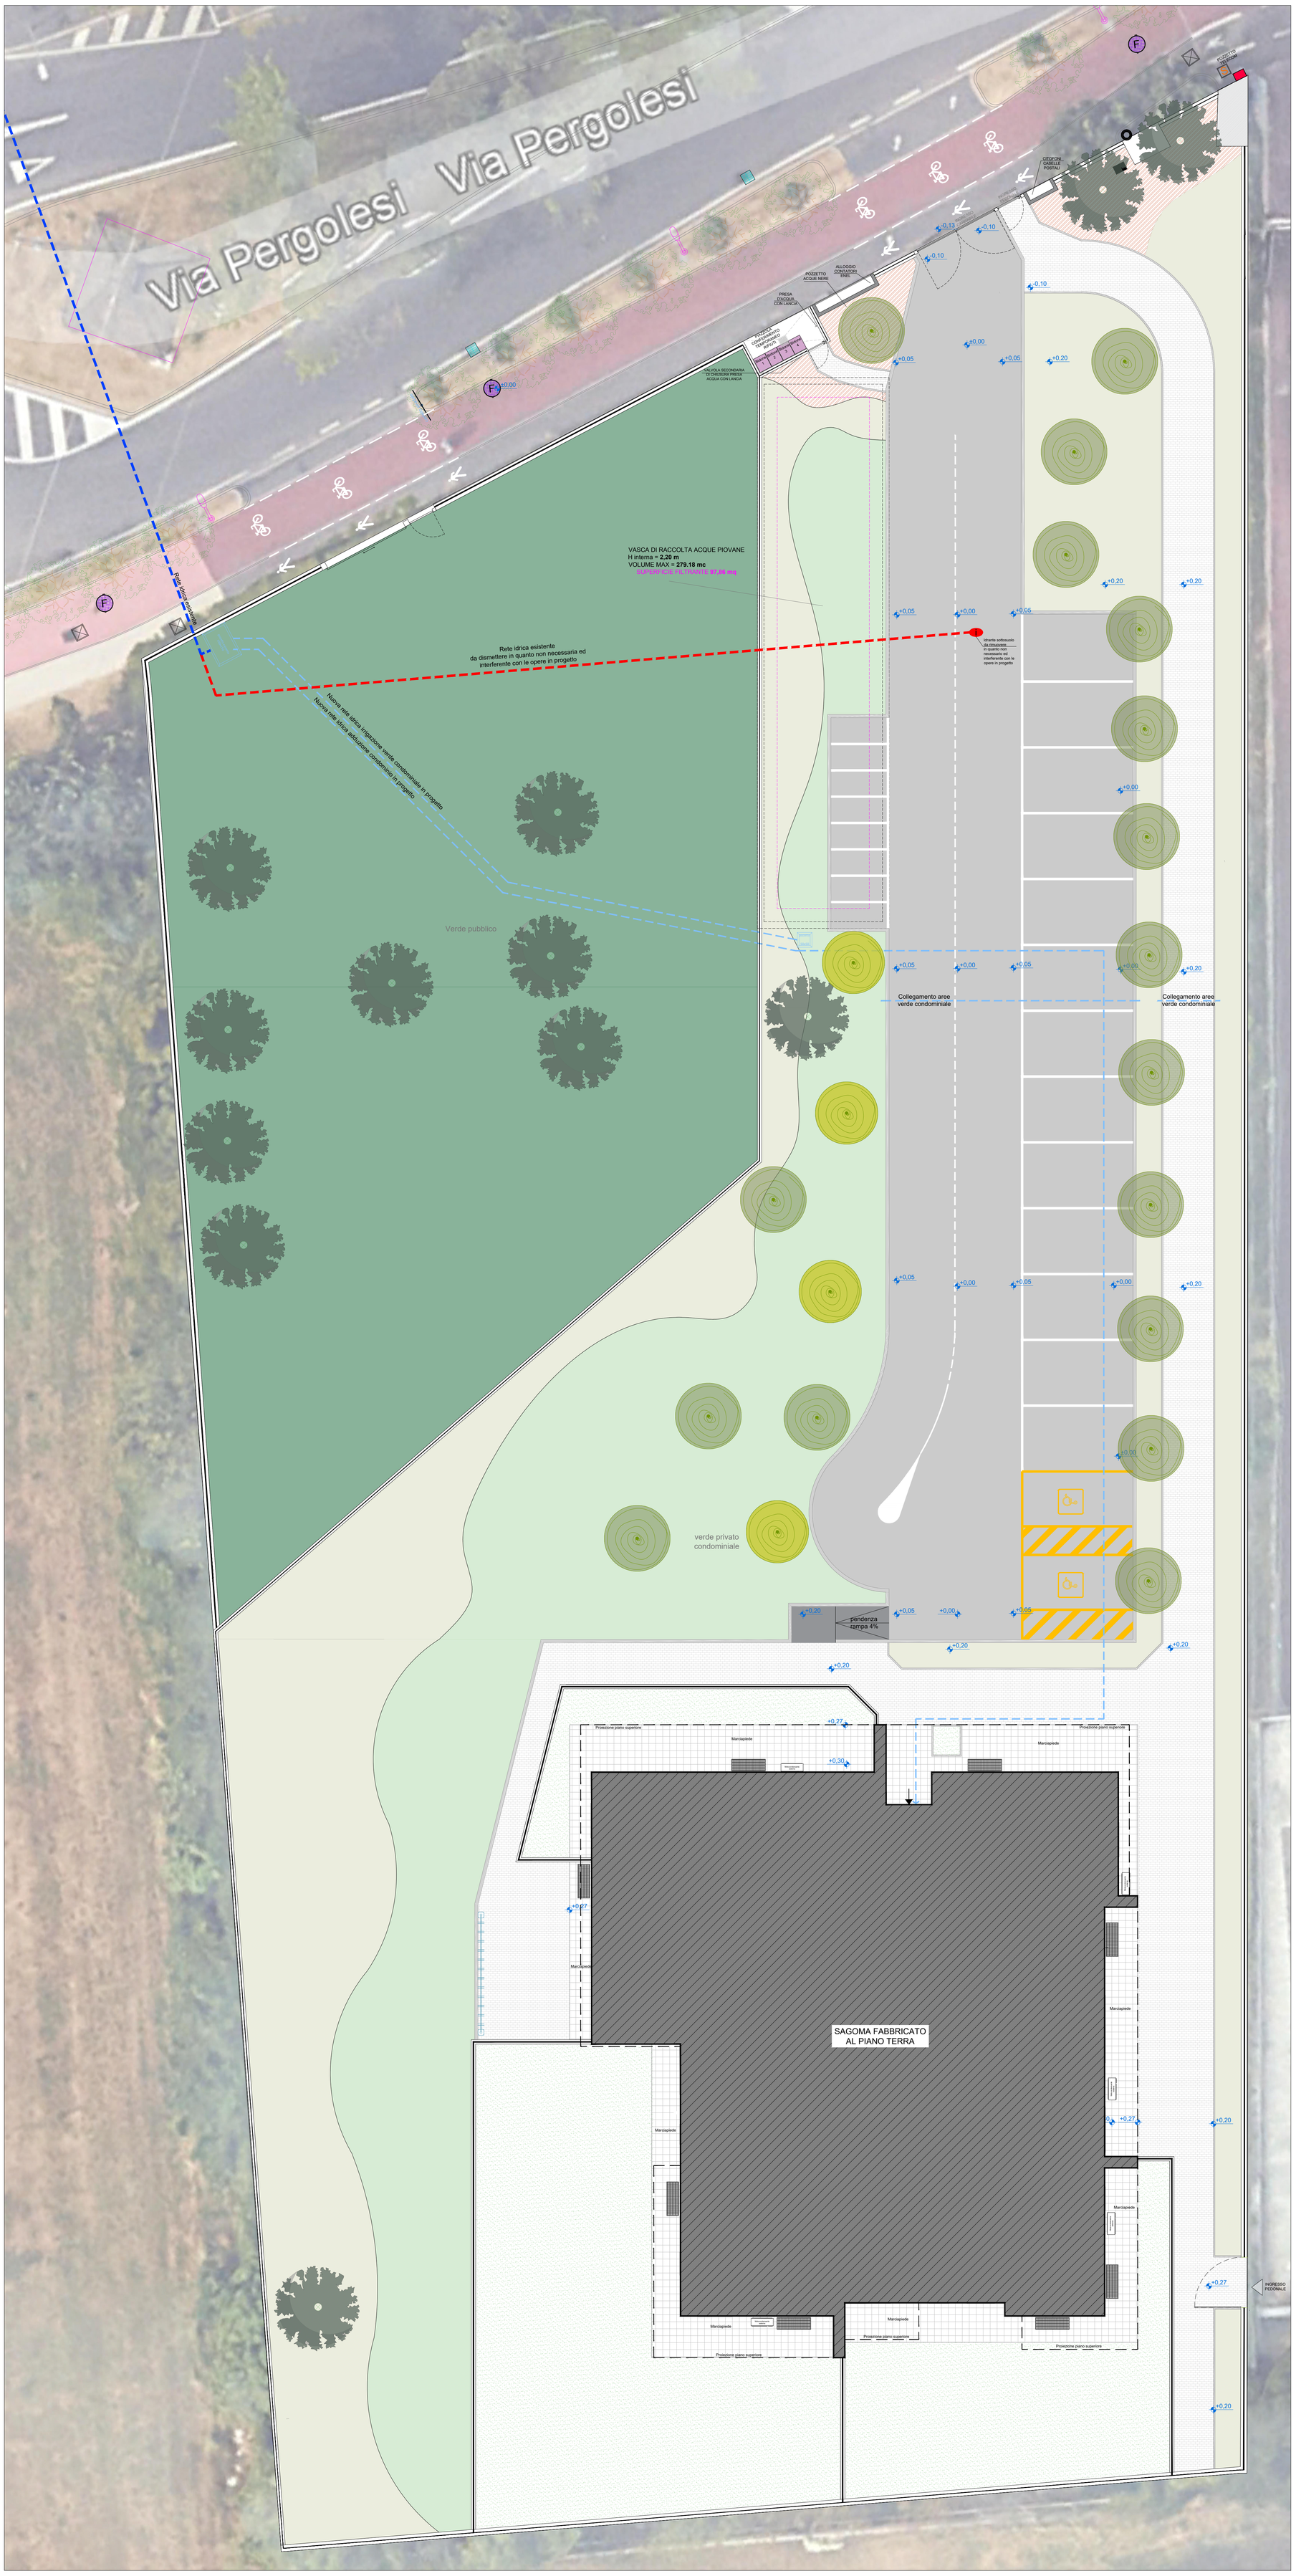


LEGENDA

	Rete idrica esistente
	Rete idrica esistente da rimuovere in quanto non necessaria e interferente con le opere in progetto
i	Idrante sottosuolo da rimuovere in quanto non necessario e interferente con le opere in progetto
	Rete idrica in progetto

GB&PARTNERS
SERVIZI E PROGETTI IMMOBILIARI
Via Volturi 37, 26845 Codogno (LO)
Telefono 0377 436099 \ 0377 34491 - Fax 0377 436654
E-mail: ordinaria@gbepartners.it - tecnico@gbepartners.it
www.gbepartners.it
REGISTRO IMPRESE di LODI 07015410962
PARTITA IVA / C.F. 07015410962
R.E.A. n. 1176574

Il Progettista

Collegio Provinciale Geometri e Geometri Laureati di Lodi
Iscrizione Albo n. 421
Geometra Gianpiero Bianchi

Il Direttore Lavori

Il Committente

Orientamento

N

COMUNE DI COLOGNO MONZESE (MI)
AREA Ex TORRIANI ARAS 01
PROGETTO ESECUTIVO
Progetto Servizi Abitativi Pubblici di via Pergolesi

N°	DATA	DESCRIZIONE MOTIVAZIONE DELL'AGGIORNAMENTO	STUDIO	DIS.
00	30/01/2026	Prima emissione	G.B.&P.	L.M.

Progetto
PROGETTO ESECUTIVO
Servizi Abitativi Pubblici
Comune di Cologno Monzese(MI)

Proponente
Officine Mak S.r.l.
Corso Europa, 10
Milano 20122

Scala
1:100

Data
30/01/2026

Tipo tavola
ARCHITETTONICI

Serie
PROGETTO ESECUTIVO

Titolo
INDIVIDUAZIONE INTERFERENZE
Rete idrica esistente - opere in progetto

Tavola nr.

Tipo Tavola	**ARCH**
Sigla / Serie	**ES**
Numero / Variante	**21**
Agg.	**00**

Documento di proprietà della Società G.B. & Partners S.r.l.. E' Vietata la riproduzione. Tutti i diritti sono riservati.