TAVOLE DI RIFERIMENTO			
S00			SPECIFICHE TECNICHE
S01			PIANTA TRACCIAMENTO
S02	*		PIANTA FONDAZIONI
S03	*		PIANTA PRIMO IMPALCATO
S04	*		PIANTA SECONDO IMPALCATO
S05	*		PIANTA COPERTURA
S06			ABACO PILASTRI
S07			VANO SCALA E ASCENSORE
*			ATTENZIONE!!!! BLOCCO TAVOLE ELEMENTO STRUTTURALE

TRACCIAMENTO

scala 1:100

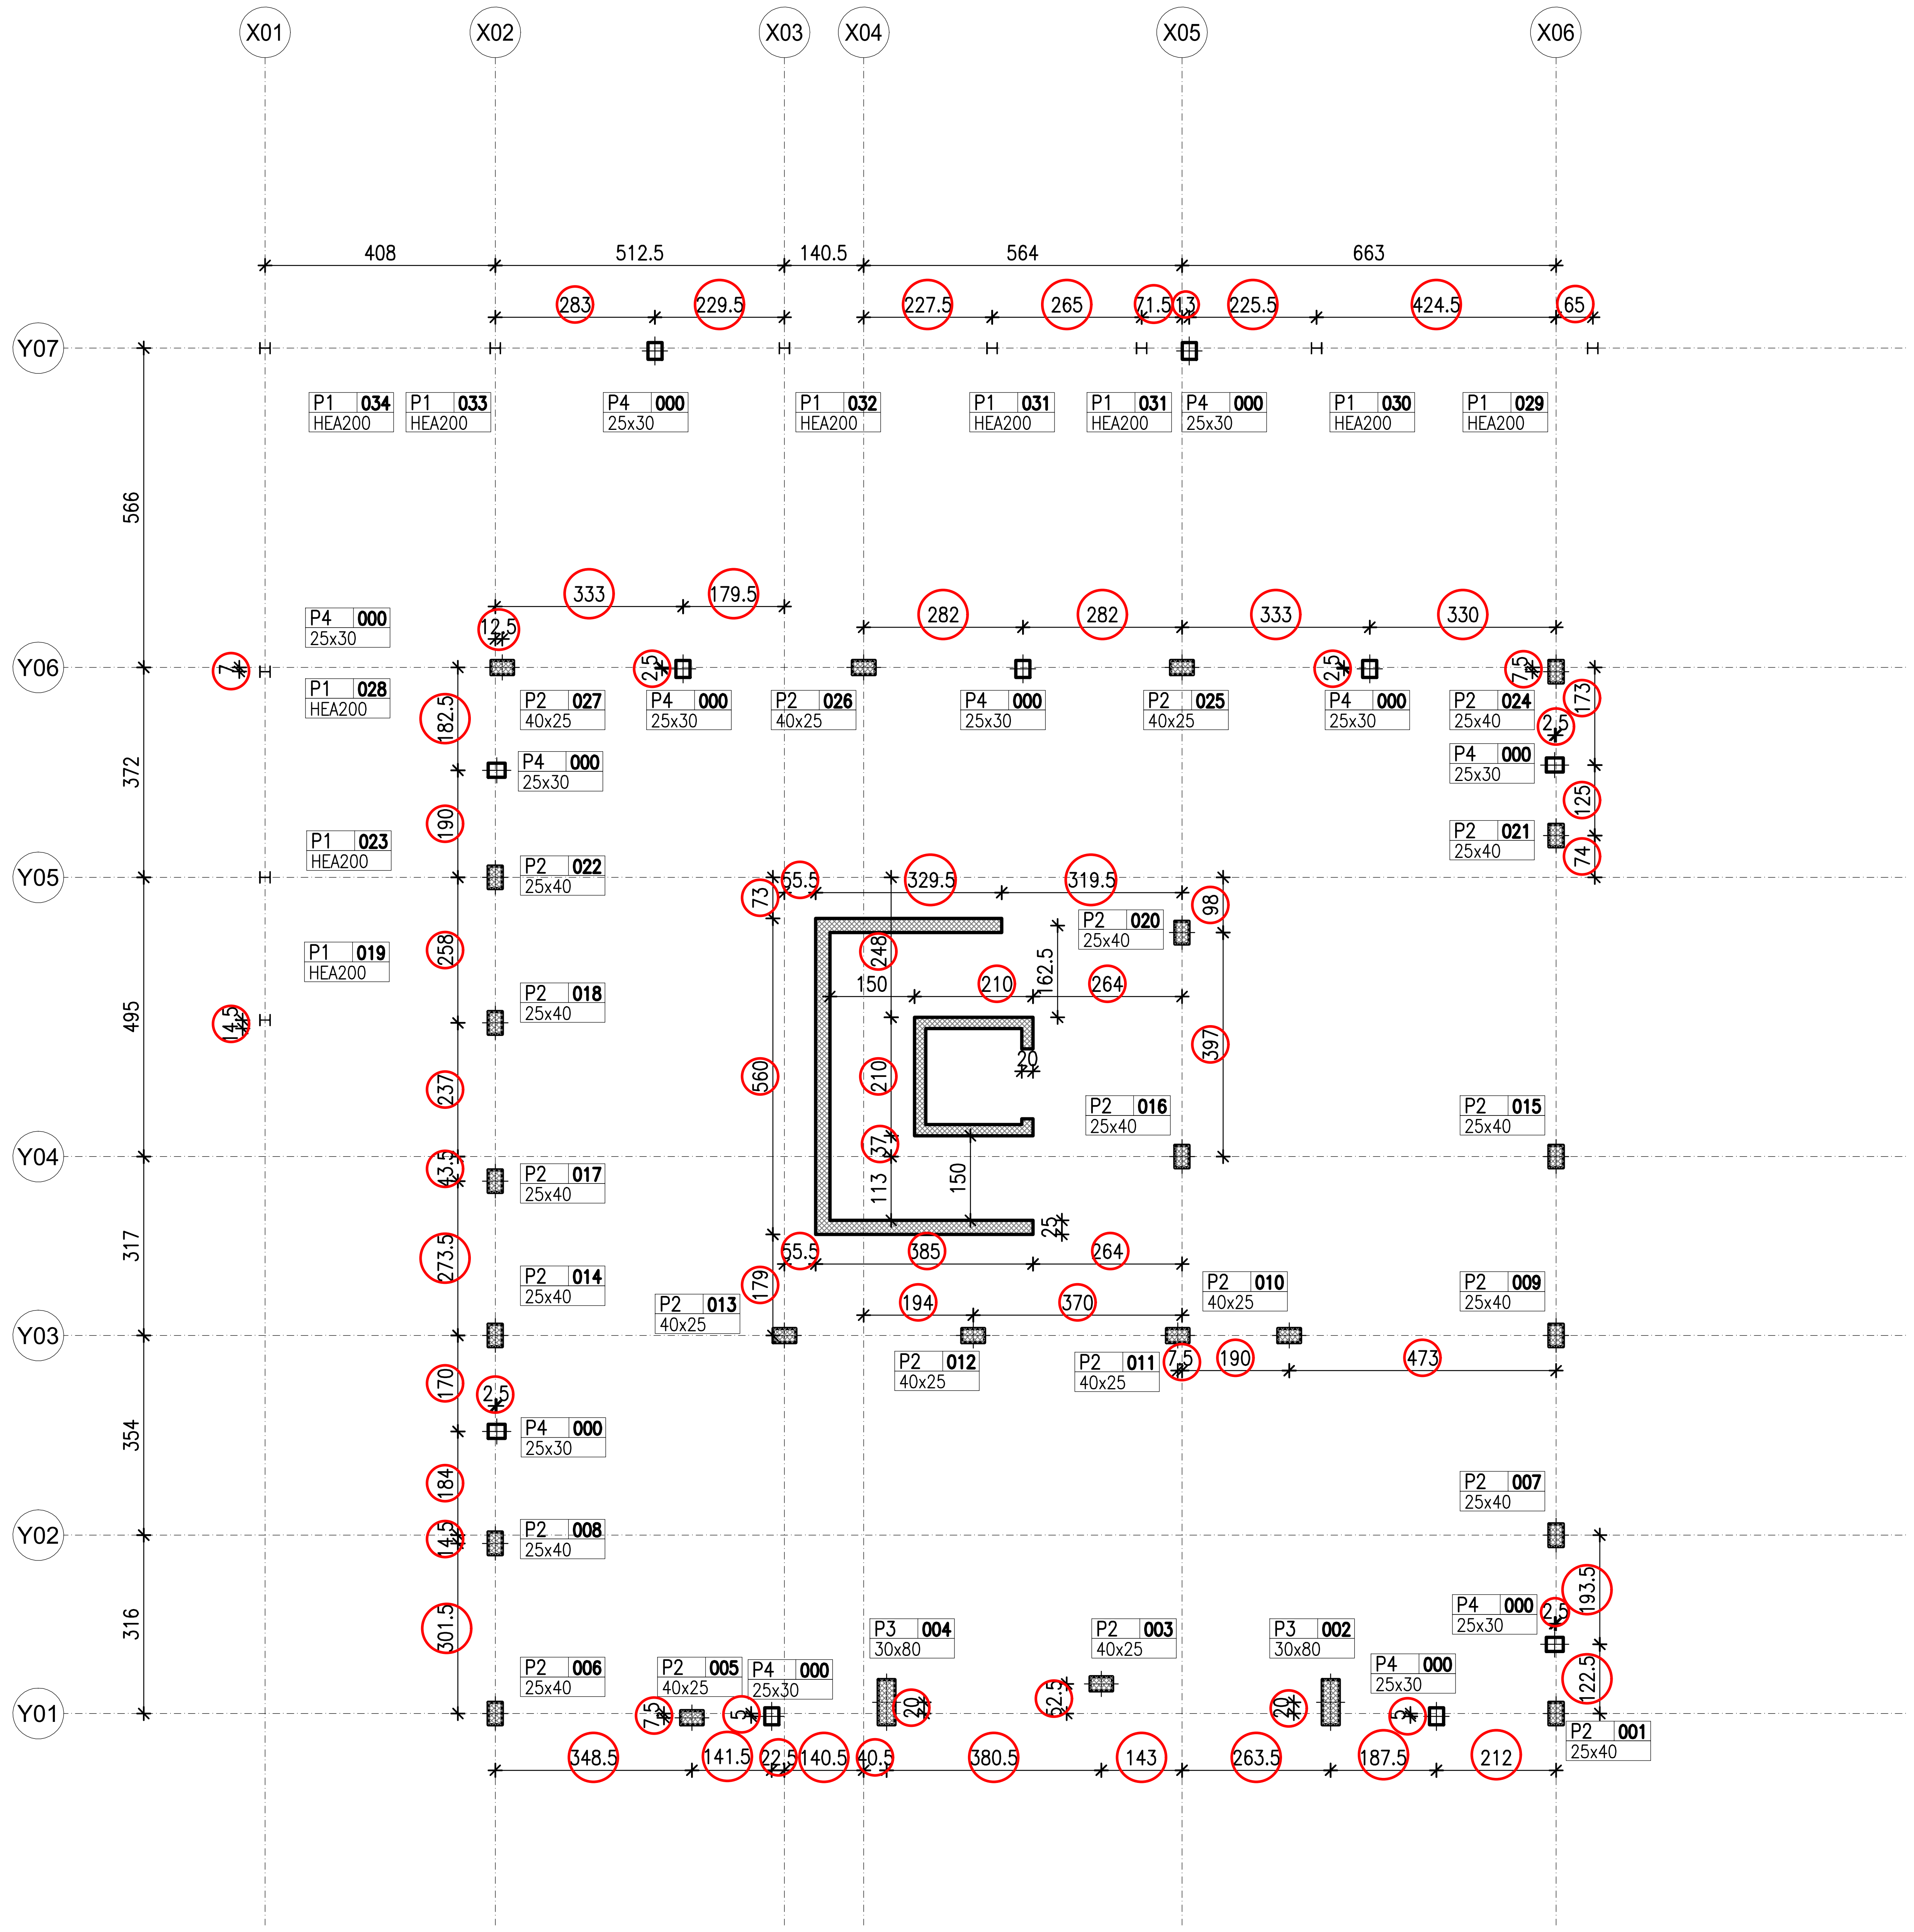

CHIAVE DI LETTURA ETICHETTE:

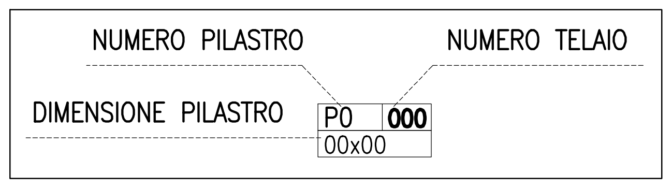

CHIAVE DI LETTURA QUOTE:

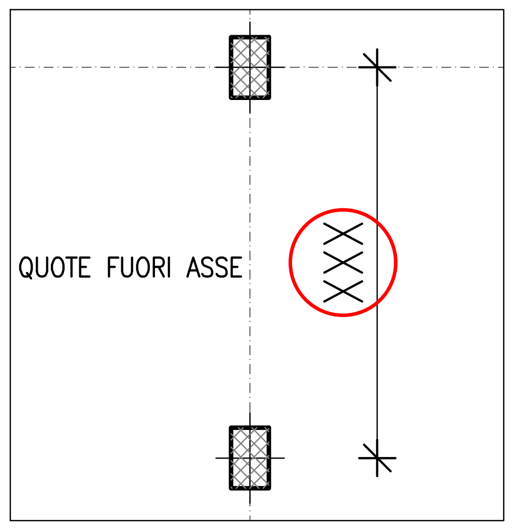

PER SPECIFICHE MATERIALI E DETTAGLI COSTRUTTIVI VEDERE TAVOLA ES-00-00_SPECIFICHE TECNICHE

GB&PARTNERS
SERVIZI E PROGETTI IMMOBILIARI

Via Varalli 37, 26845 Codogno (LO)
Telefono 0377 436099 - 0377 34691 - Fax 0377 436654
E-mail amministrazione@gbepartners.it - tecnico@gbepartners.it
www.gbepartners.it
REGISTRO IMPRESE DI LODI n°05966150962
PARTITA I.V.A / C.F. 05966150962
C.S. € 11.111,10 iv

UNI EN ISO 9001:2015
UNI EN ISO 14001:2015

Progetto strutturale:

STEN STRUCTURAL ENGINEERING

Ing. Alessandro Bertozzi
Piazza Alpini, 2
25039 Travagliato (BS)
Cell. 3890777193
E-mail: alessandro@bertozzingegneria.it

COMUNE DI COLOGNO MONZESE (MI)
AREA Ex TORRIANI ARAS 01
PROGETTO ESECUTIVO
Progetto Servizi Abitativi Pubblici di via Pergolesi

N°	DATA	DESCRIZIONE MOTIVAZIONE DELL'AGGIORNAMENTO	STUDIO	DIS.
00	22/05/2025	Prima emissione	STEN	LC
01	29/05/2025	Revisione generale	STEN	LC
02	09/06/2025	Pilastro P4	STEN	LC
03	26/01/2026	Aggiornamento architett 260118	STEN	ST
04	05/02/2026	Modifica muri vano scala	STEN	ST

Il Progettista

Collegio Provinciale
Geometri e Geometri Laureati
di Lodi
Iscrizione Albo
N. 267
Geometra
Gianpiero Bianchi

ARCHITETTO
CRISTIANO
SCHIAVI
421

Il Proponente

Progetto	Proponente	Scala
PROGETTO ESECUTIVO ***Servizi Abitativi Pubblici*** *Comune di Cologno Monzese(MI)*	***Officine Mak S.r.l.*** *Corso Europa, 10* *Milano 20122*	**1:100** Data **05/02/2026**

Tipo tavola
ESECUTIVI
Serie
STRUTTURE
Titolo
TRACCIAMENTO

Tavola nr.

Tipo Tavola	**E**
Sigla / Serie	**S**
Numero / Variante	**01**
Agg.	**04**

Orientamento

N

Documento di proprietà della Società G.B. & Partners S.r.l.. E' Vietata la riproduzione. Tutti i diritti sono riservati.