
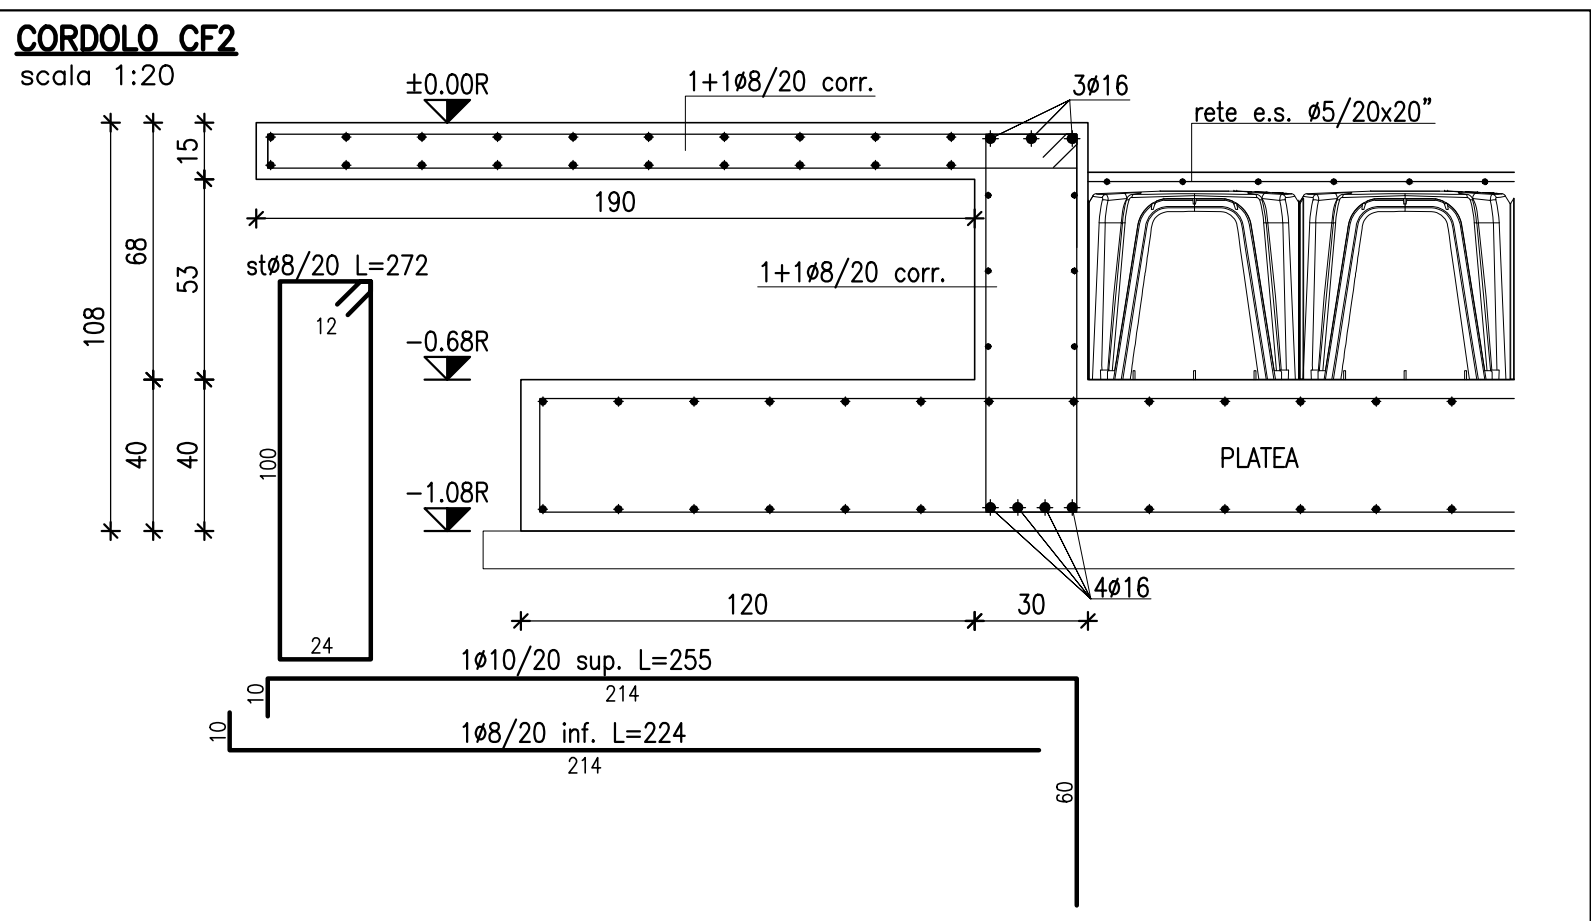
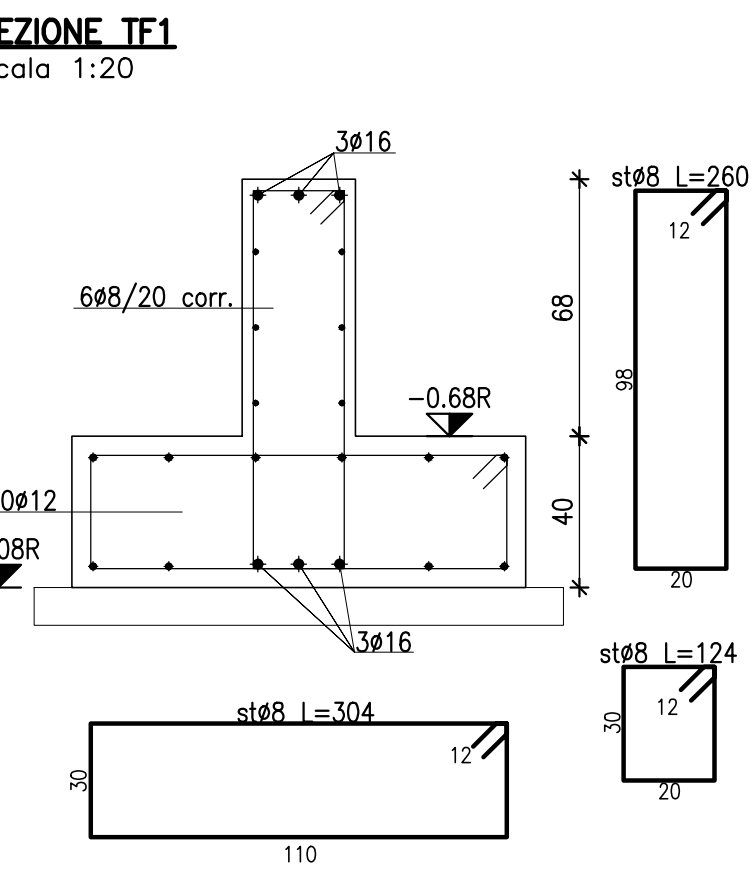
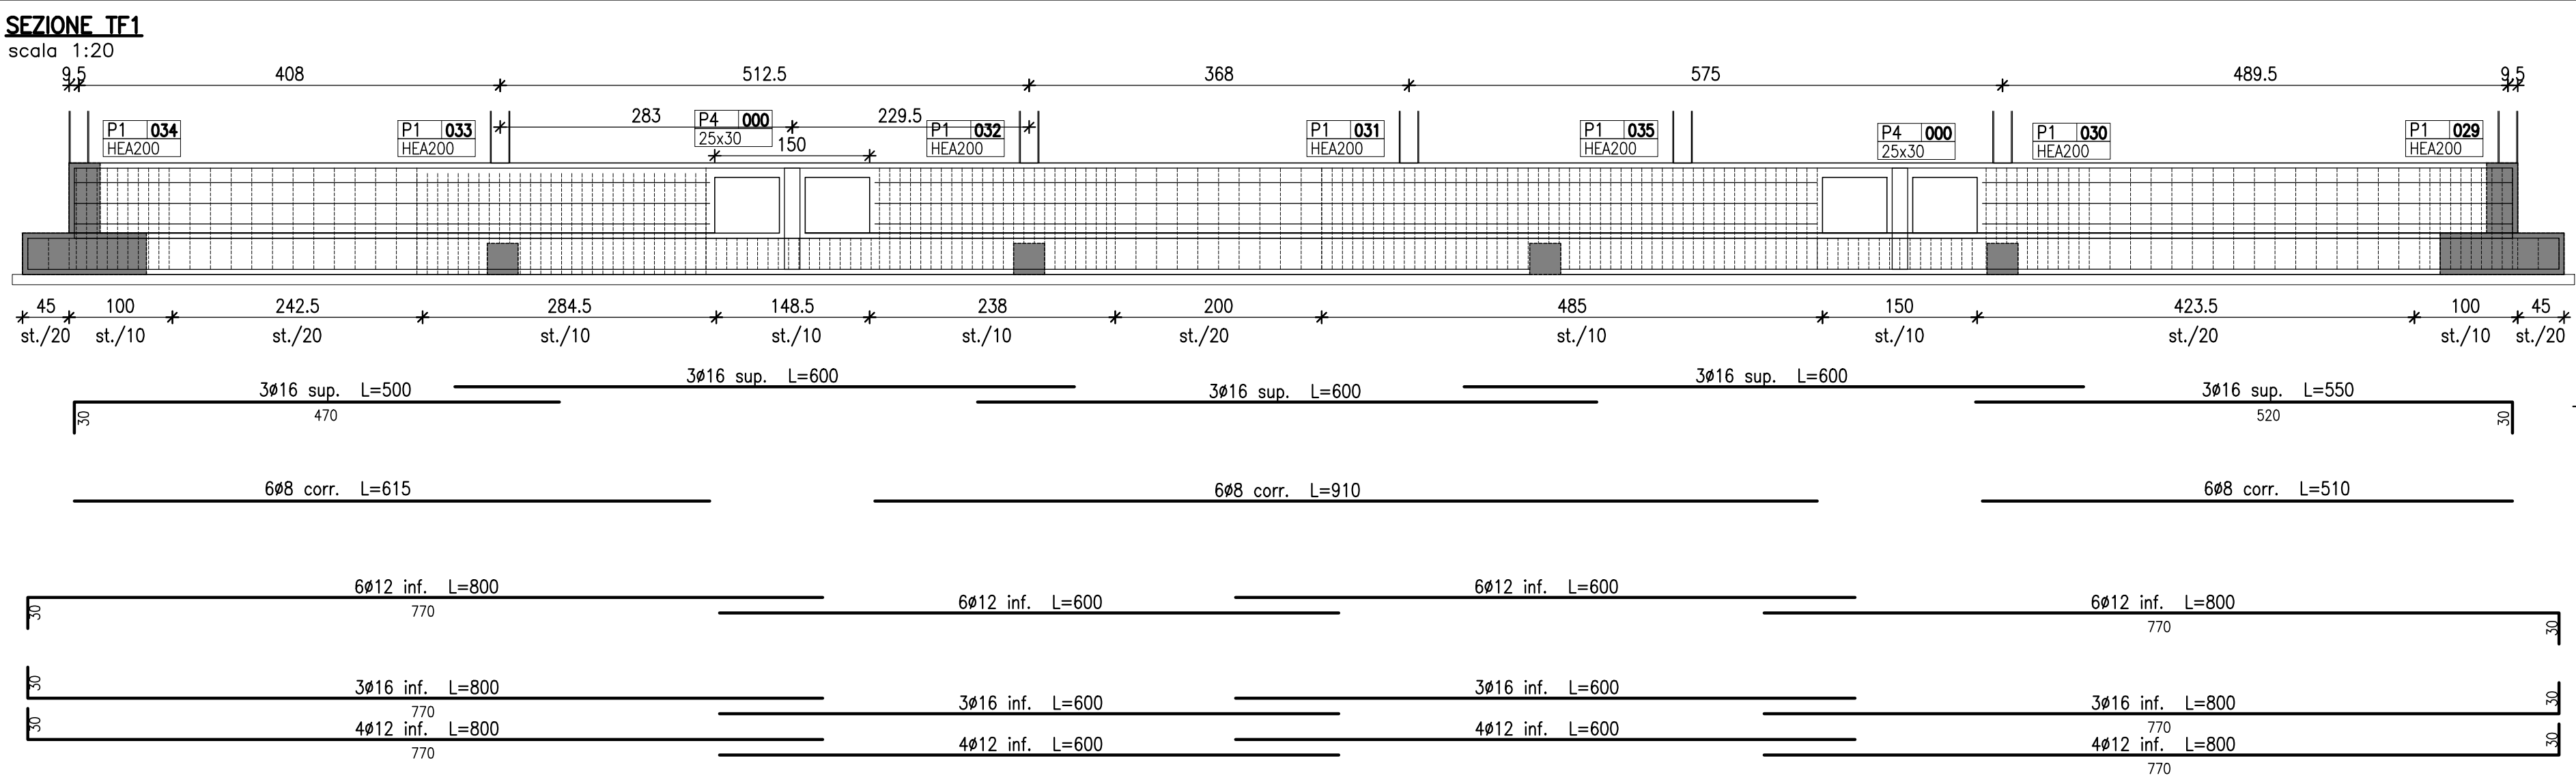
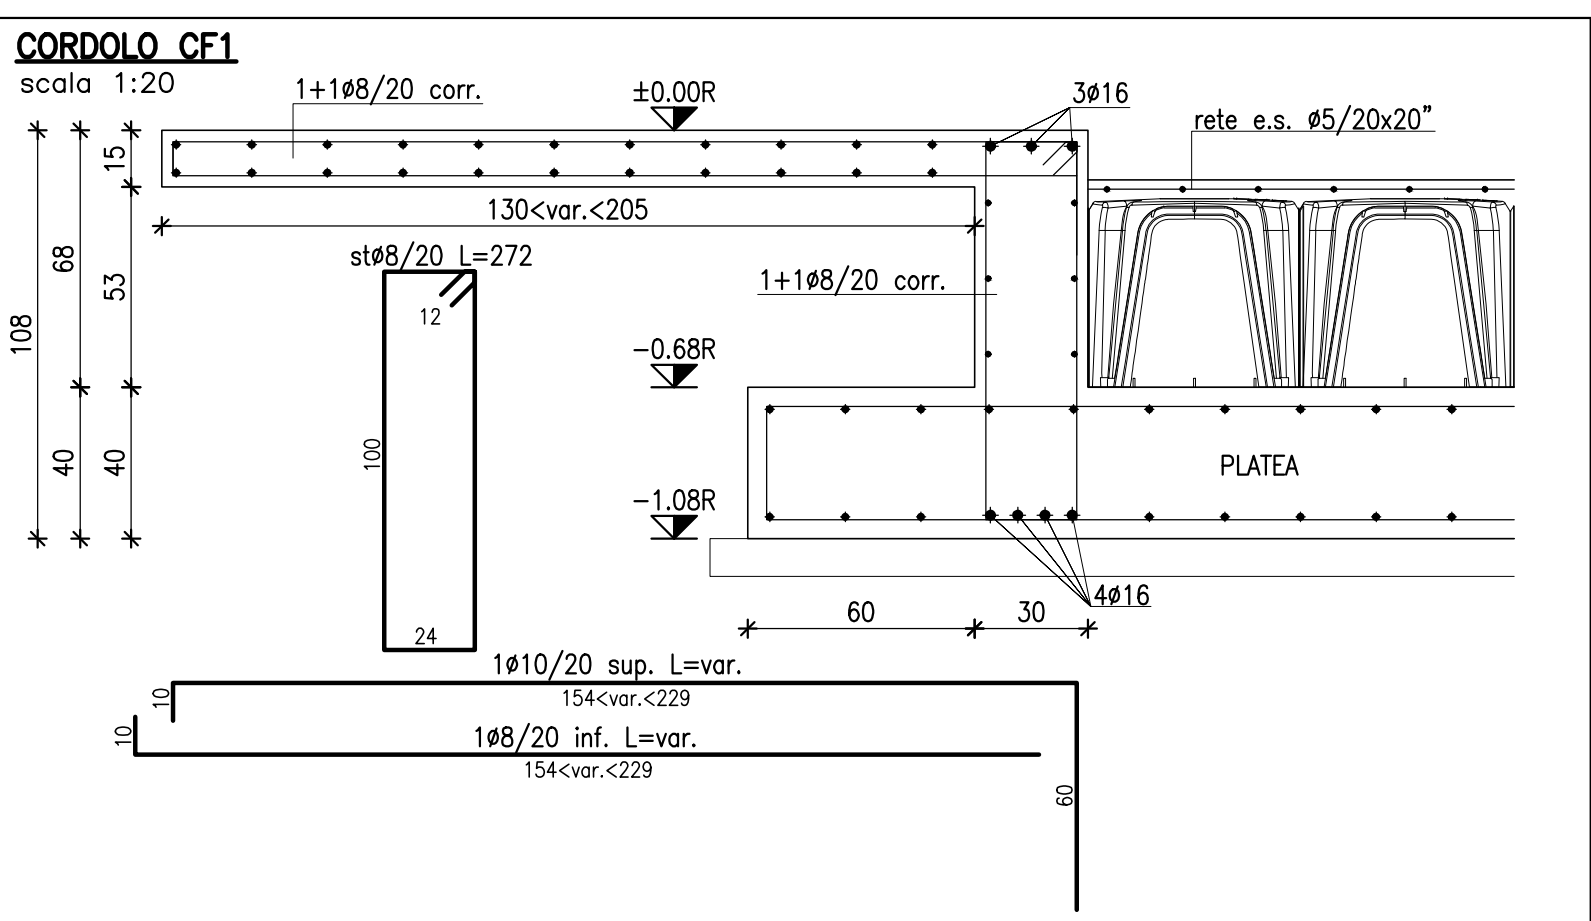
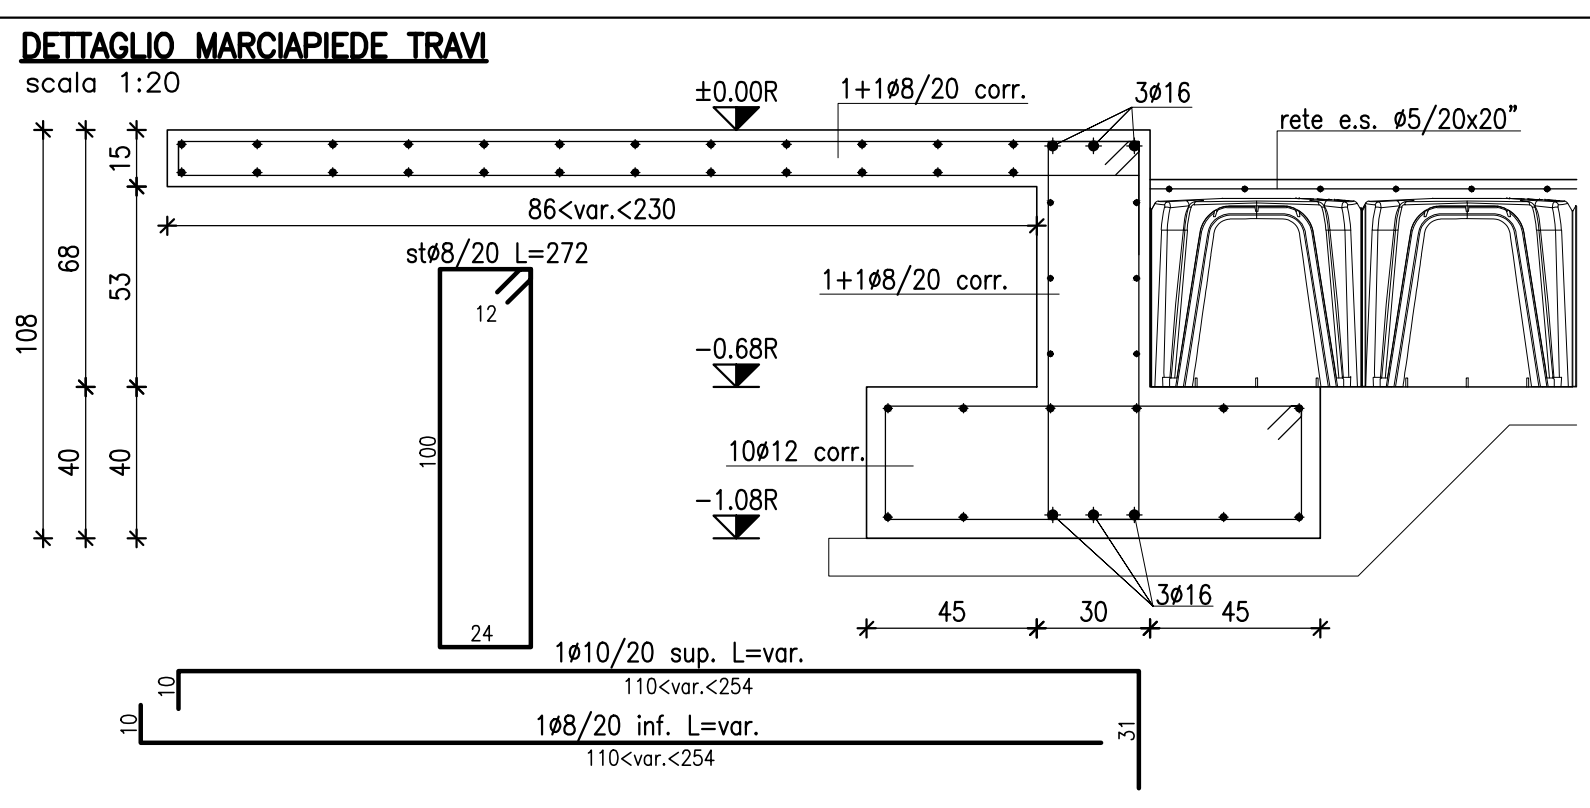
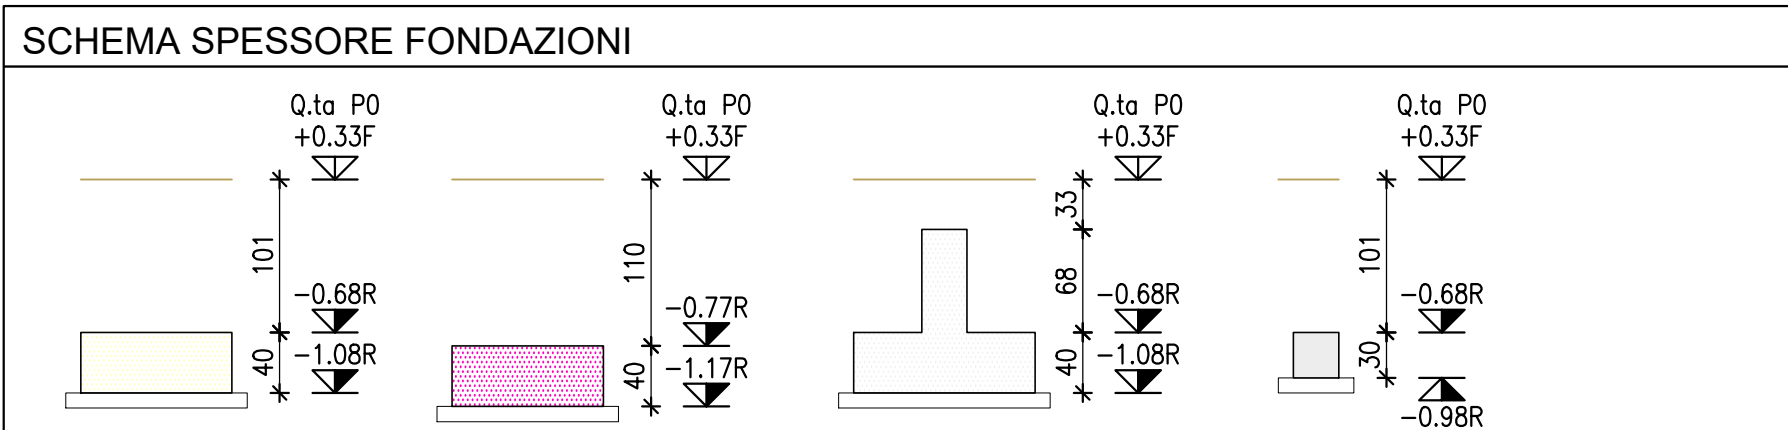
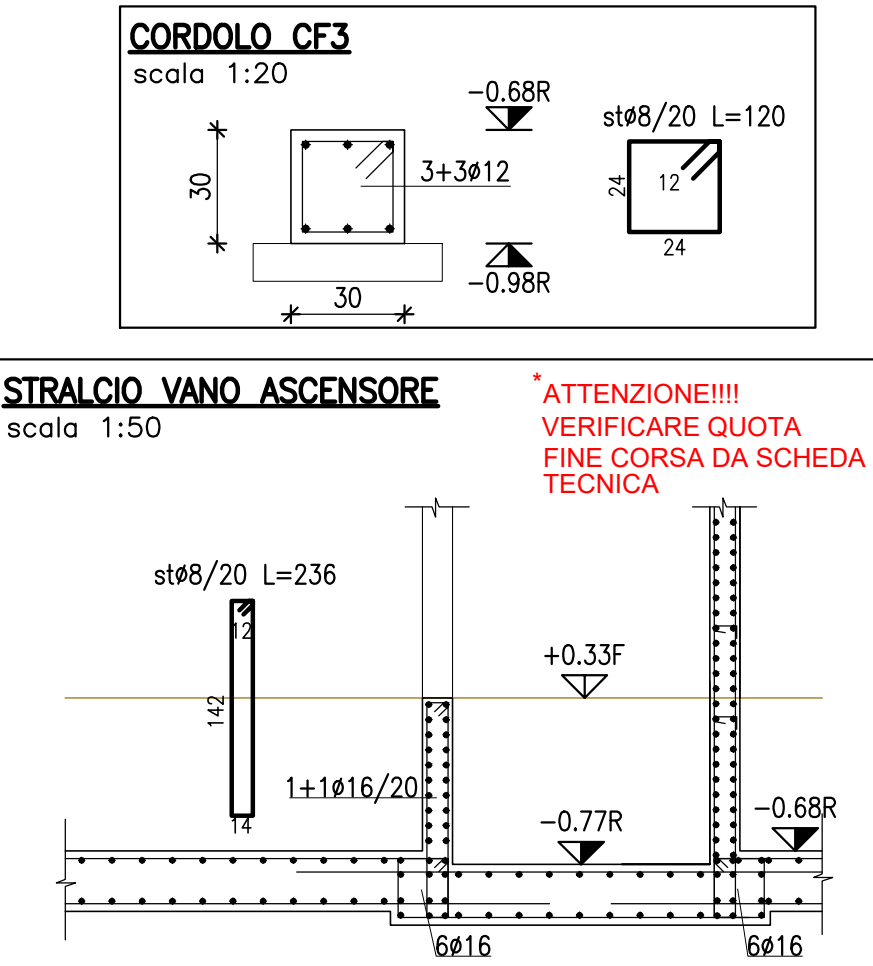
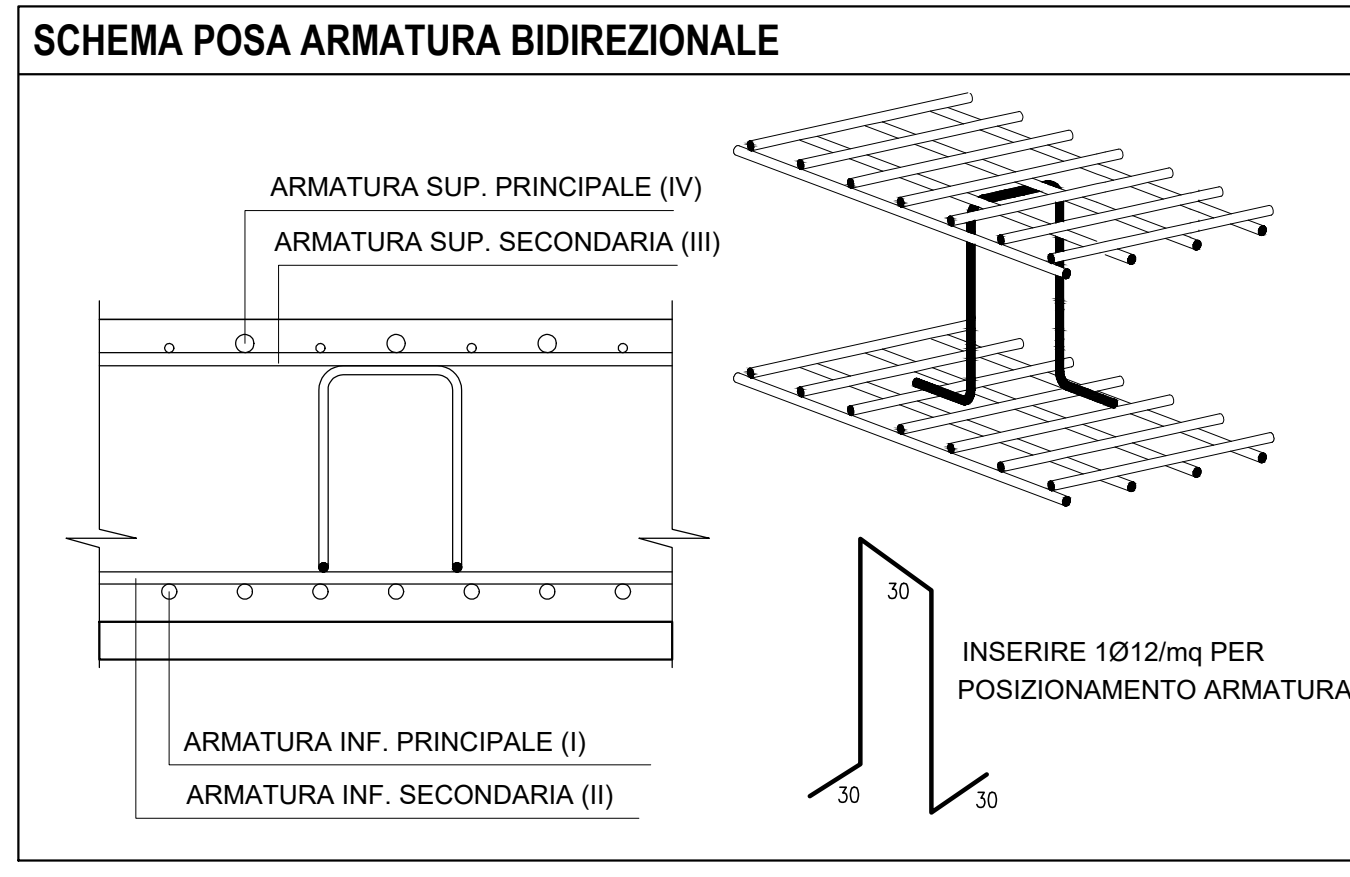
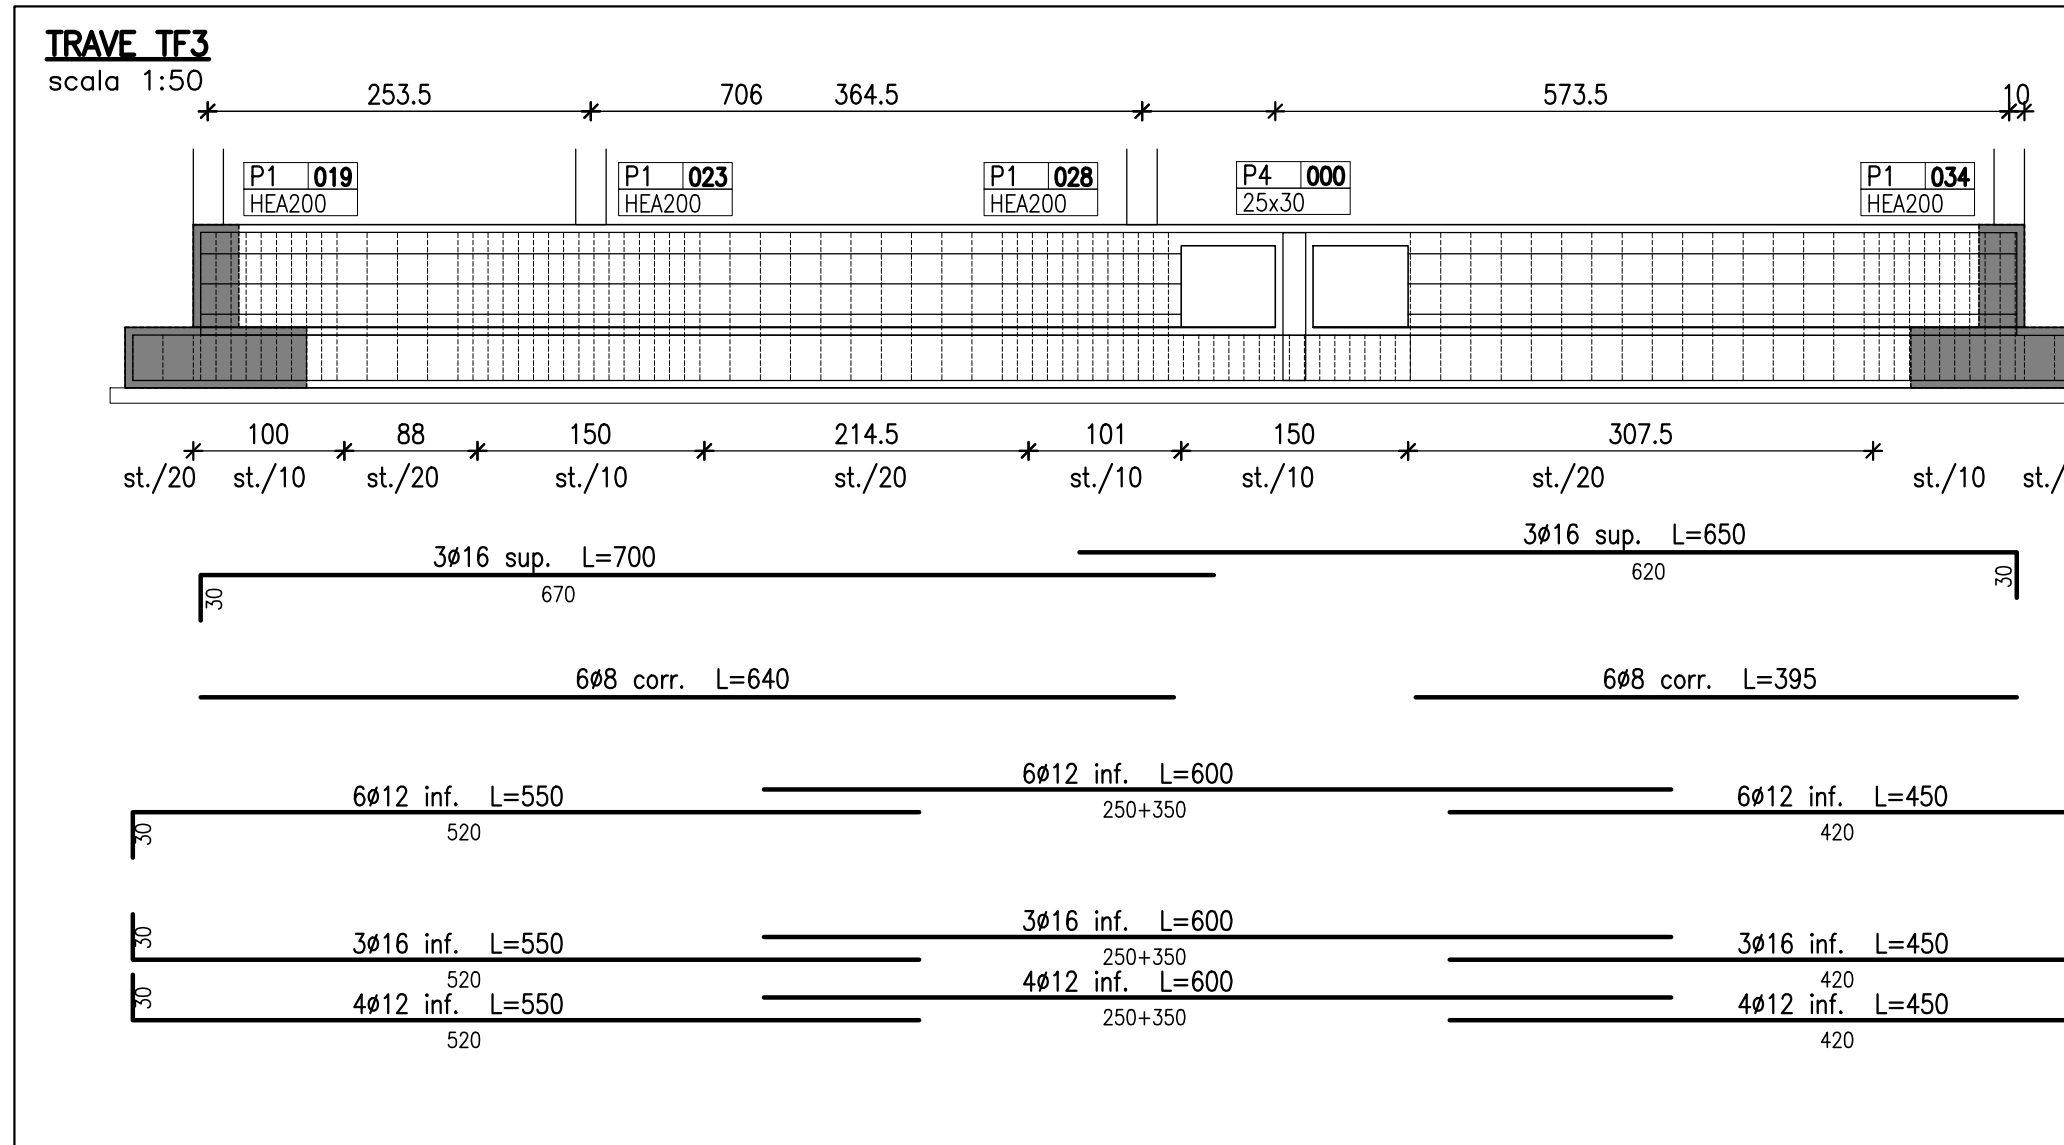
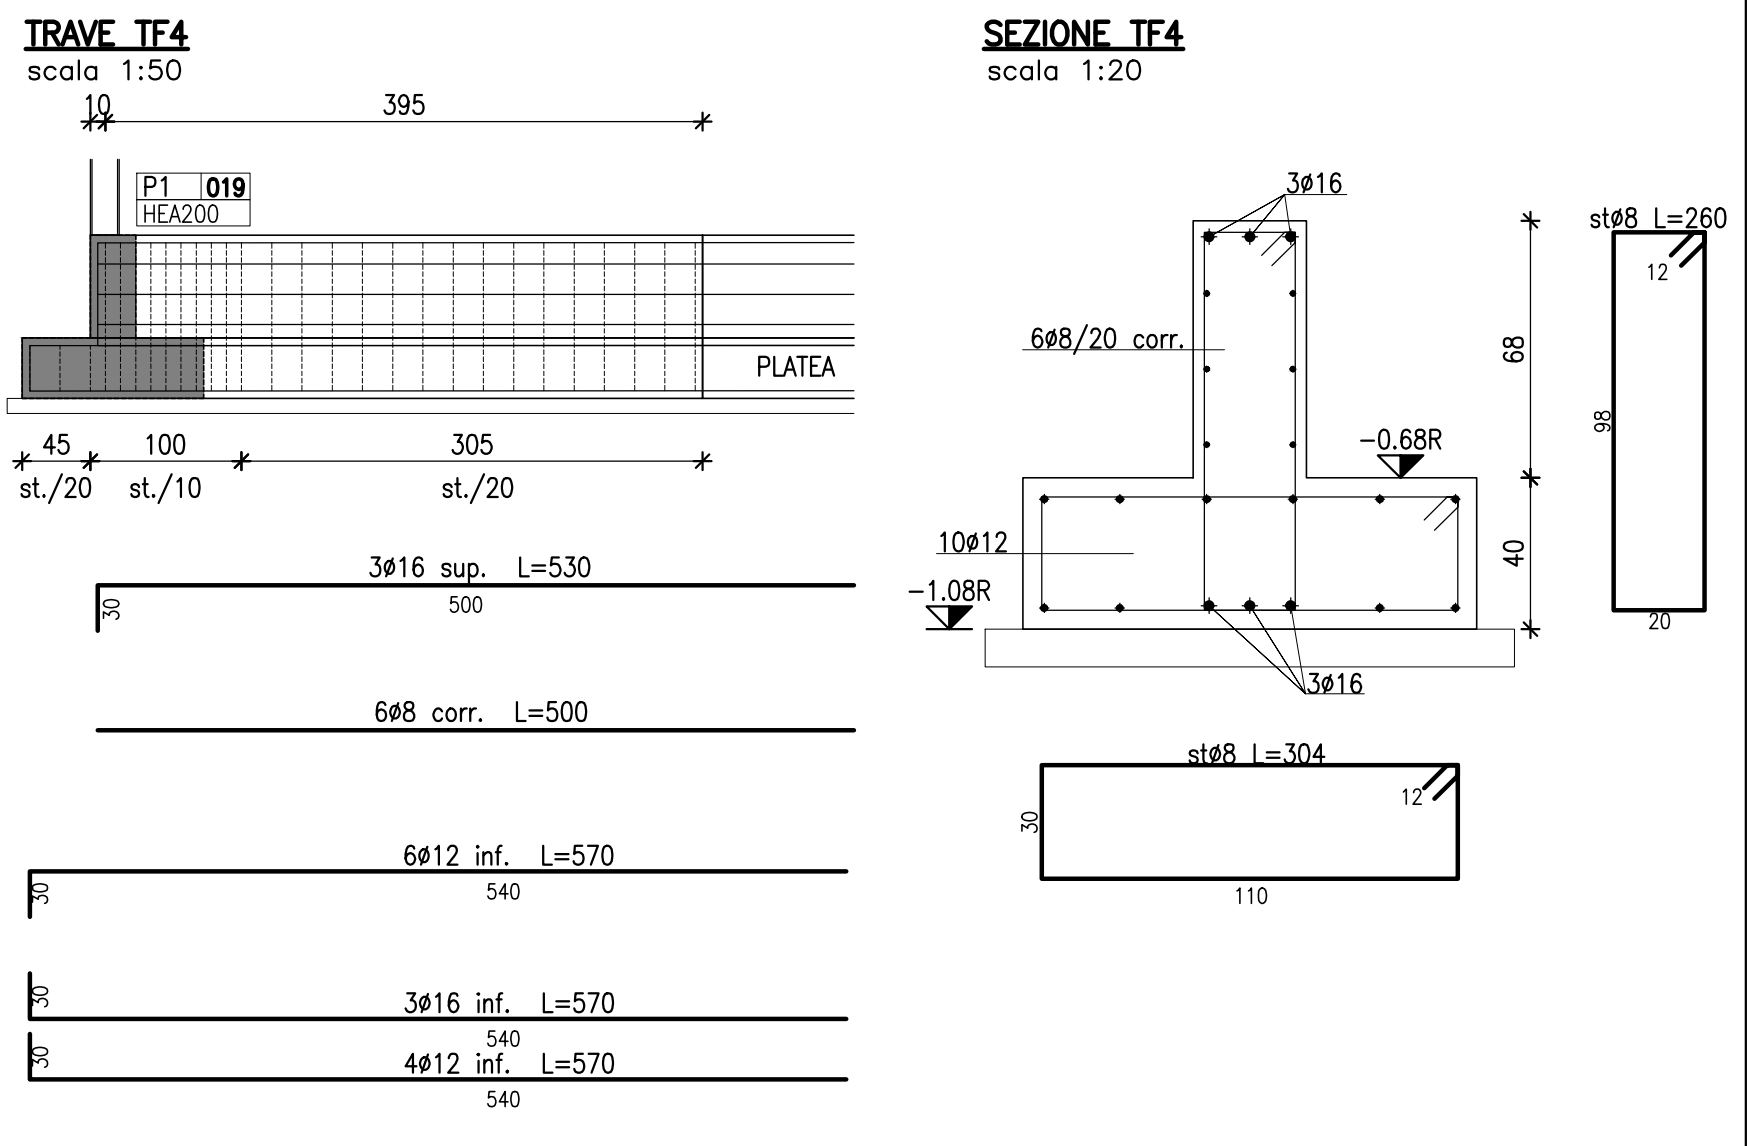
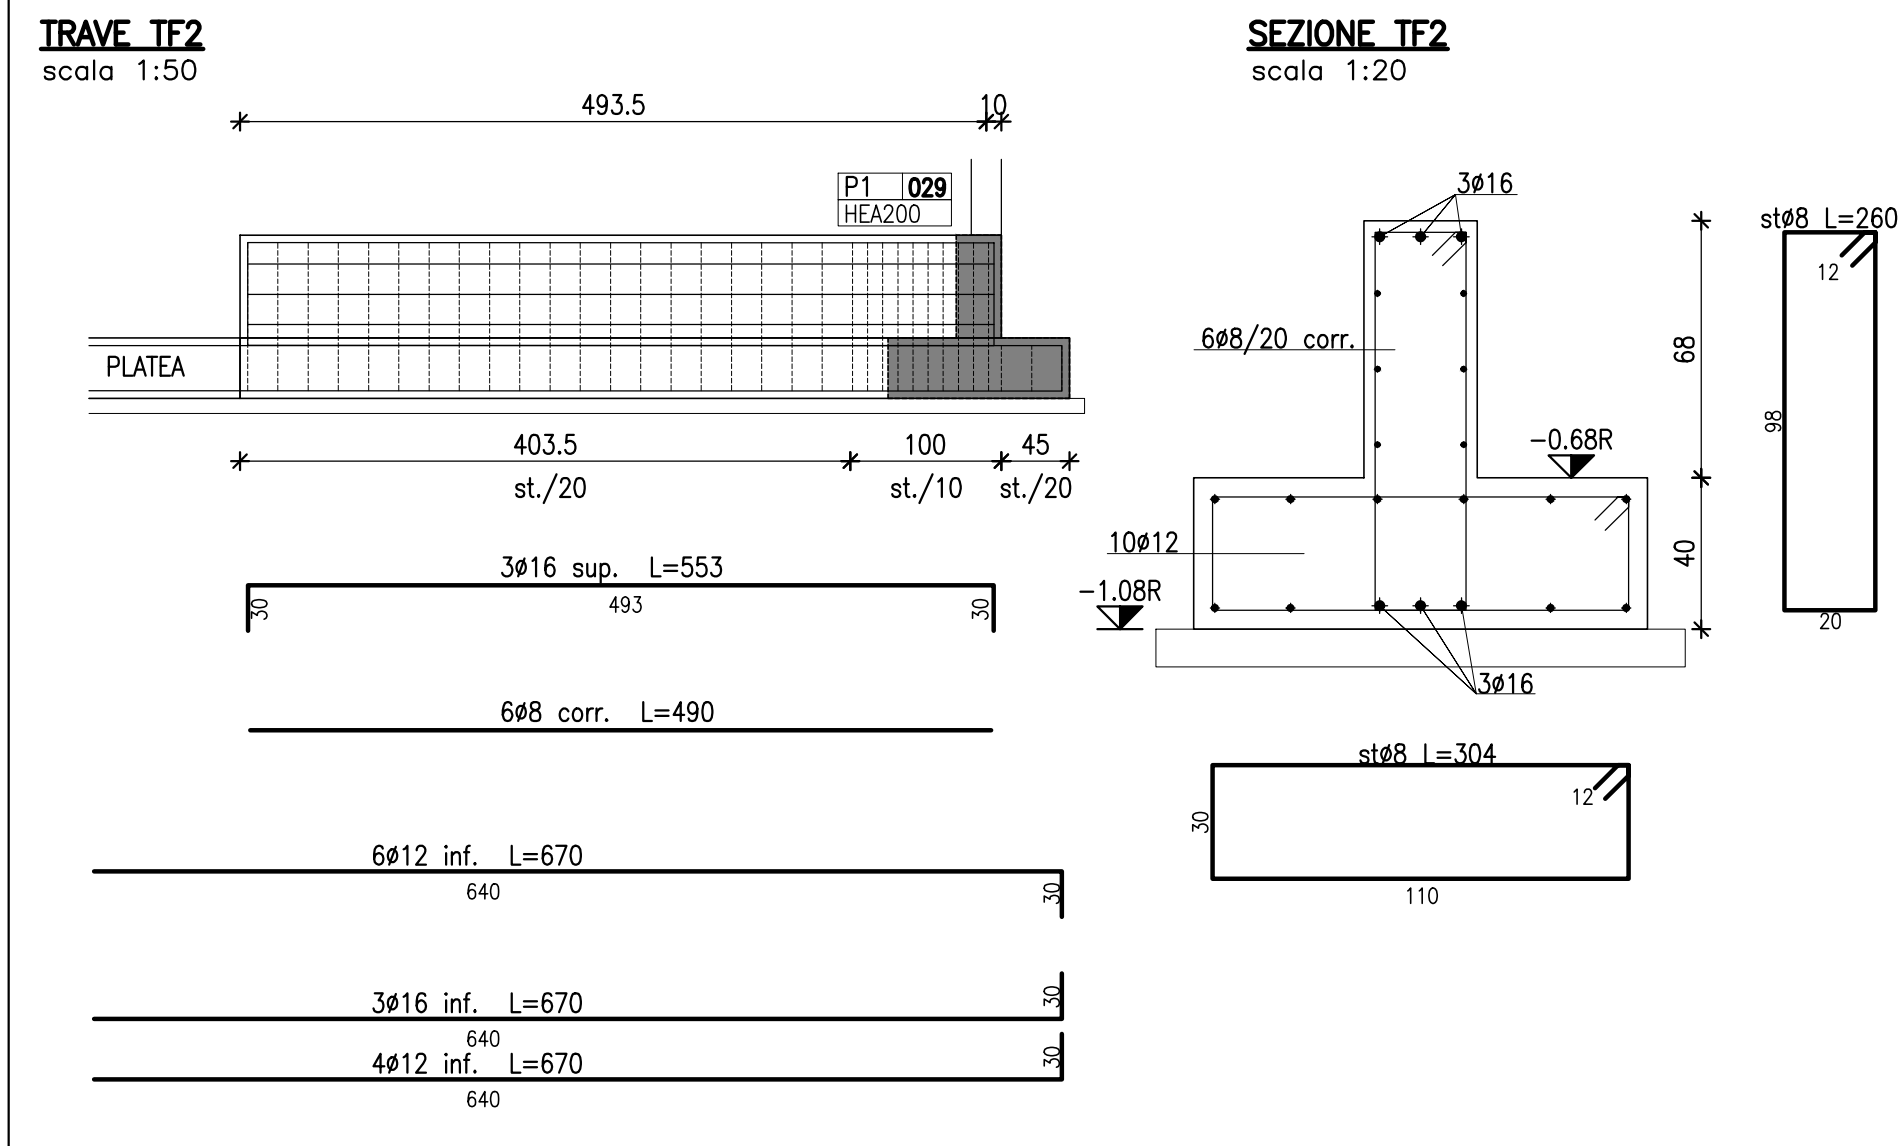


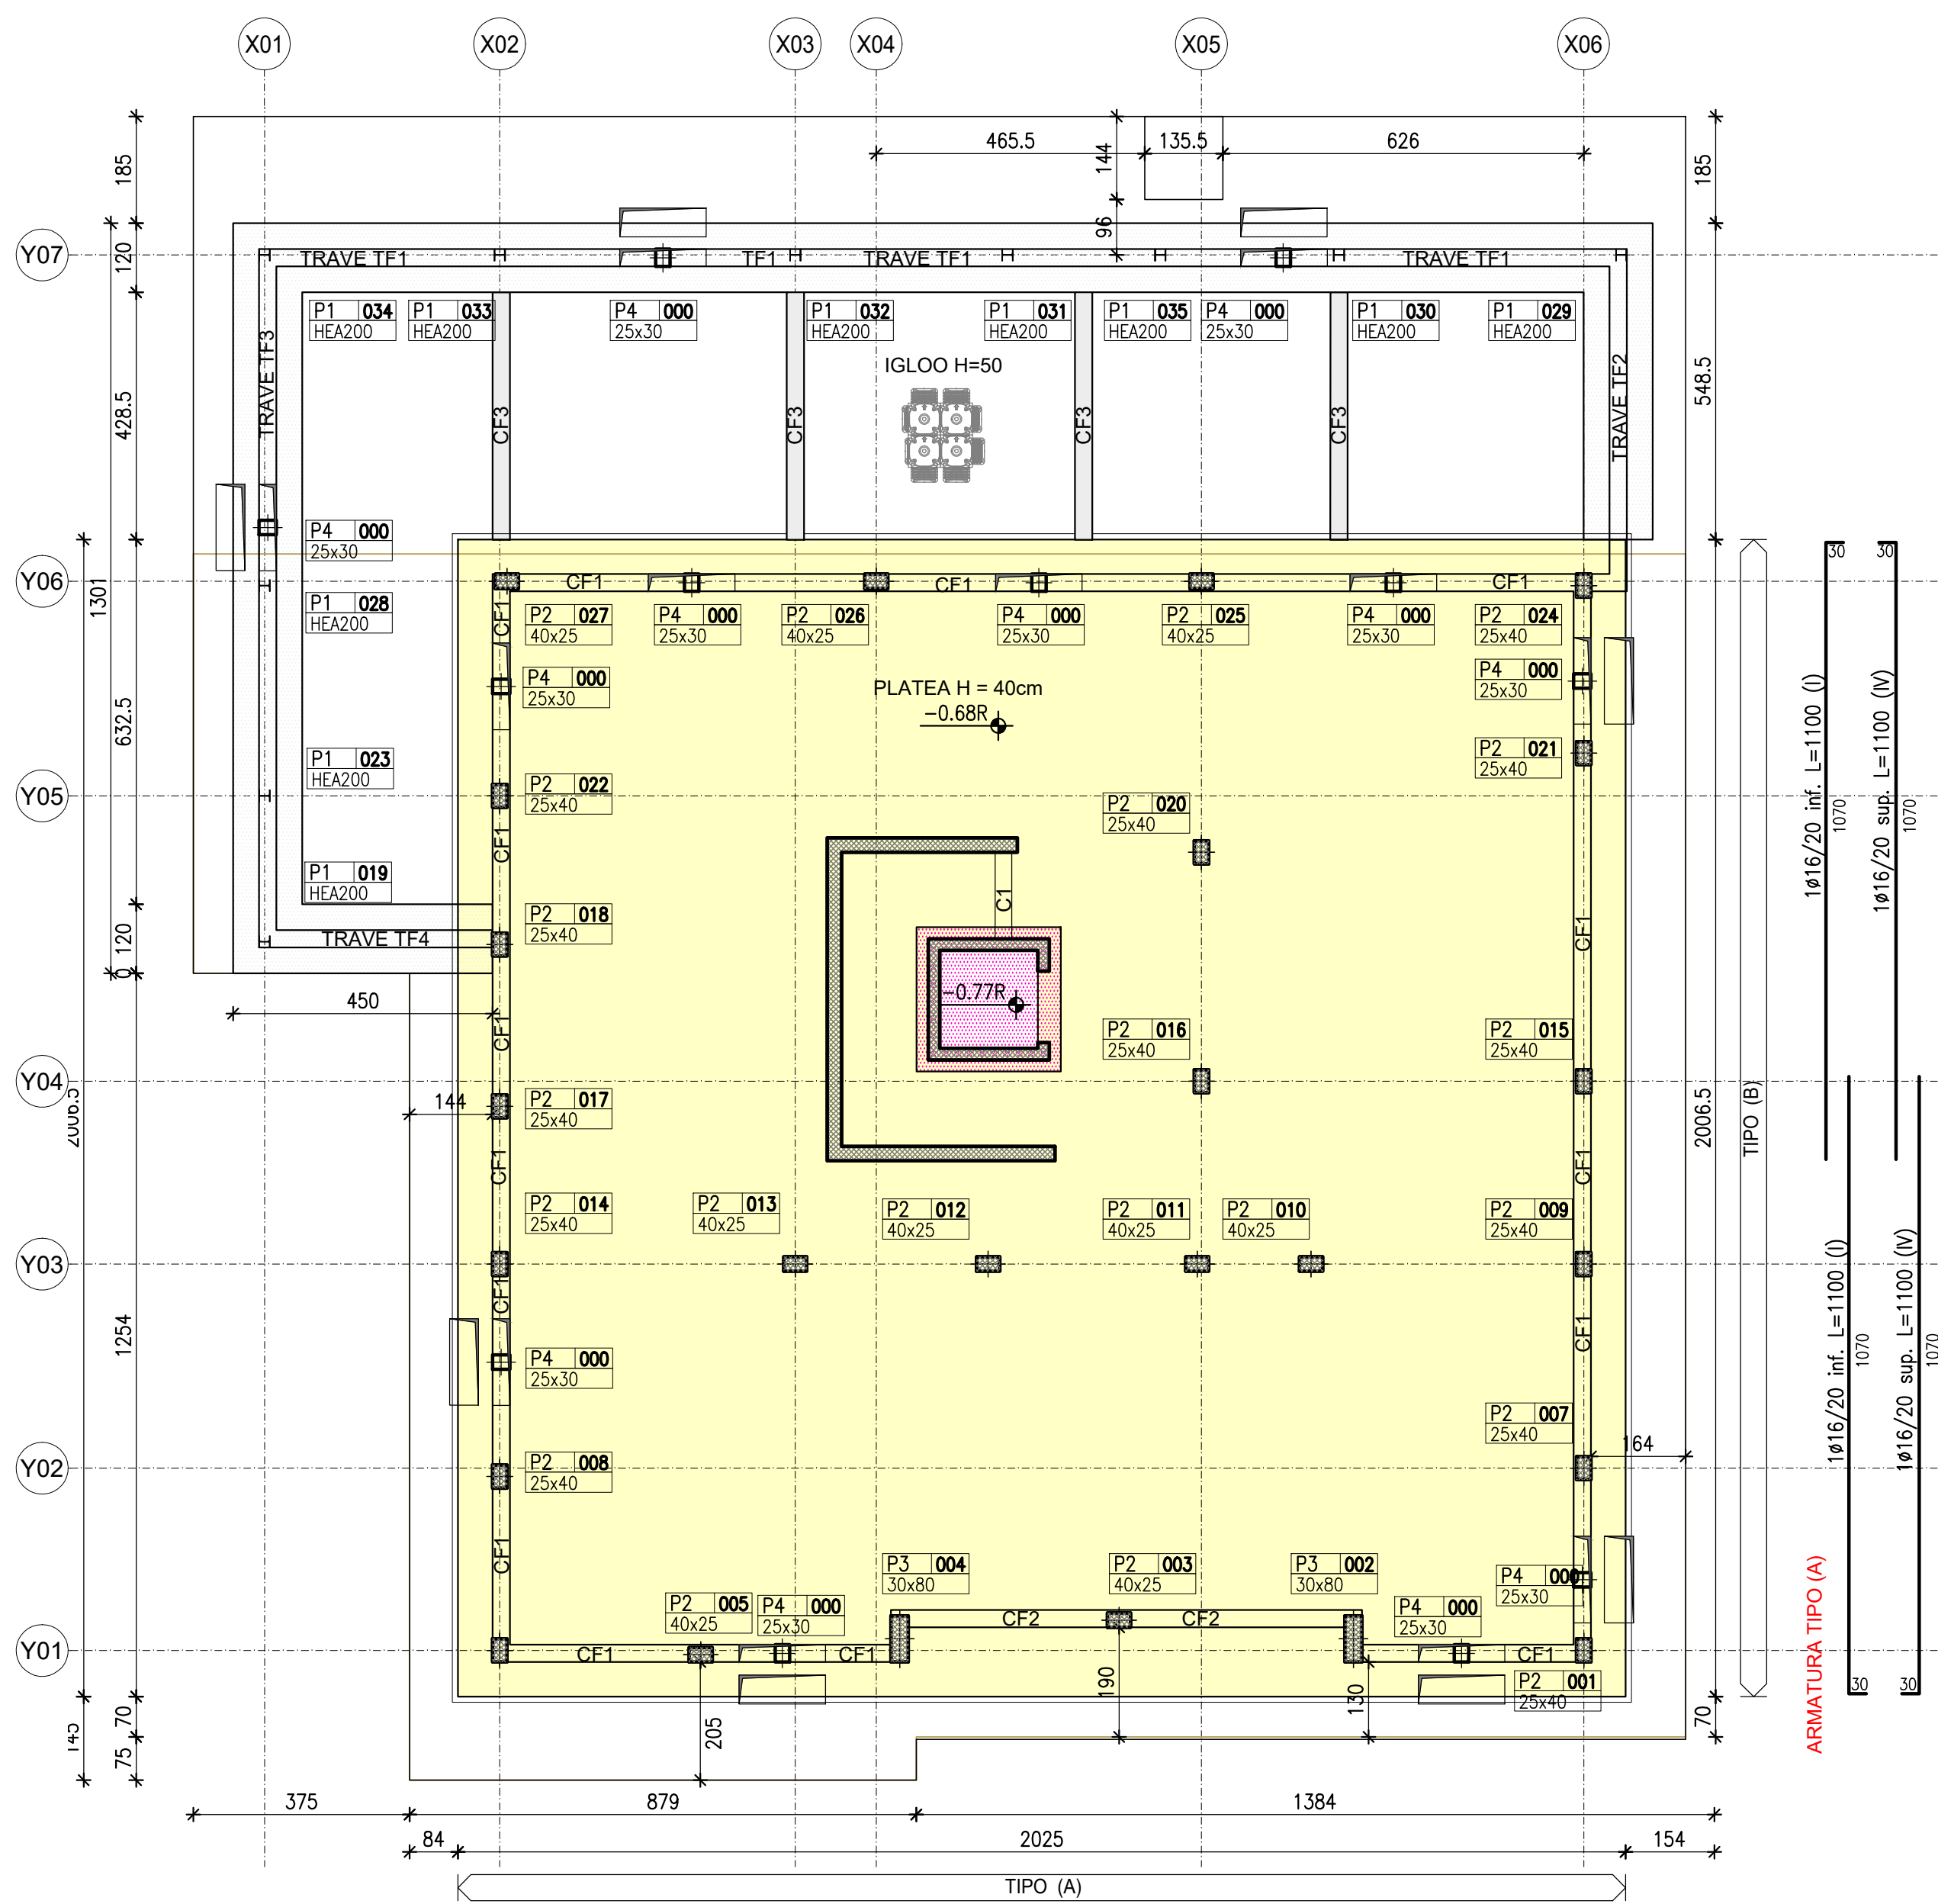

TAVOLE DI RIFERIMENTO			
S00			SPECIFICHE TECNICHE
S01			PIANTA TRACCIAMENTO
S02	*		PIANTA FONDAZIONI
S02a			ARMATURA AGGIUNTIVA PLATEA
S03	*		PIANTA PRIMO IMPALCATO
S04	*		PIANTA SECONDO IMPALCATO
S05	*		PIANTA COPERTURA
S06			ABACO PILASTRI
S07			VANO SCALA E ASCENSORE
*			ATTENZIONE!!! BLOCCO TAVOLE ELEMENTO STRUTTURALE

PER SPECIFICHE MATERIALI E DETTAGLI COSTRUTTIVI VEDERE TAVOLA ES-00-00_SPECIFICHE TECNICHE

ATTENZIONE! PER CORDOLO C1 SCALA VEDERE TAV.ES-07-00_VANO SCALA E ASCENSORE

GB&PARTNERS
SOCIETÀ A RESPONSABILITÀ LIMITATA
Via S. Maria 10 - 20122 Milano
Tel. 02 58 10 10 10 - Fax 02 58 10 10 11
E-mail: gb@gbpartners.it

STEN
STRUCTURAL ENGINEERING

Progetto strutturale:
Ing. Alessandro Bertozzi
Piazza Alpini, 2
25039 Travagliato (BS)
Cell. 3890777193
E-mail: alessandro@bertozzingegneria.it

COMUNE DI COLOGNO MONZESE (MI)
AREA Ex TORRIANI ARAS 01
PROGETTO ESECUTIVO
Progetto Servizi Abitativi Pubblici di via Pergolesi

Il Progettista
Collegio Provinciale
Geometri e Geometri Laureati
di Lodi
Ing. Roberto Albini
N. 277
Geometra
Gianpiero Bianchi

N°	DATA	DESCRIZIONE MOTIVAZIONE DELL'AGGIORNAMENTO	STUDIO	DIS.
00	22/05/2025	Prima emissione	STEN	LC
01	29/05/2025	Revisione generale	STEN	LC
02	09/06/2025	Forometrie e piastrino P4	STEN	LC
03	26/01/2026	Aggiornamento architettonico 260118	STEN	ST

Progetto
PROGETTO ESECUTIVO
Servizi Abitativi Pubblici
Comune di Cologno
Monzese(MI)

Proponente
Officine Mak S.r.l.
Corso Europa, 10
Milano 20122

Scala
1:100
Data
26/01/2026

Tipo tavola ESECUTIVI Serie STRUTTURE Titolo PIANTA FONDAZIONI	Tavola nr. <table><tr><td>E</td><td>S</td></tr><tr><td>02</td><td>03</td></tr></table>	E	S	02	03
E	S				
02	03				