


PIANTA FOROMETRIE FONDAZIONI

scala 1:50

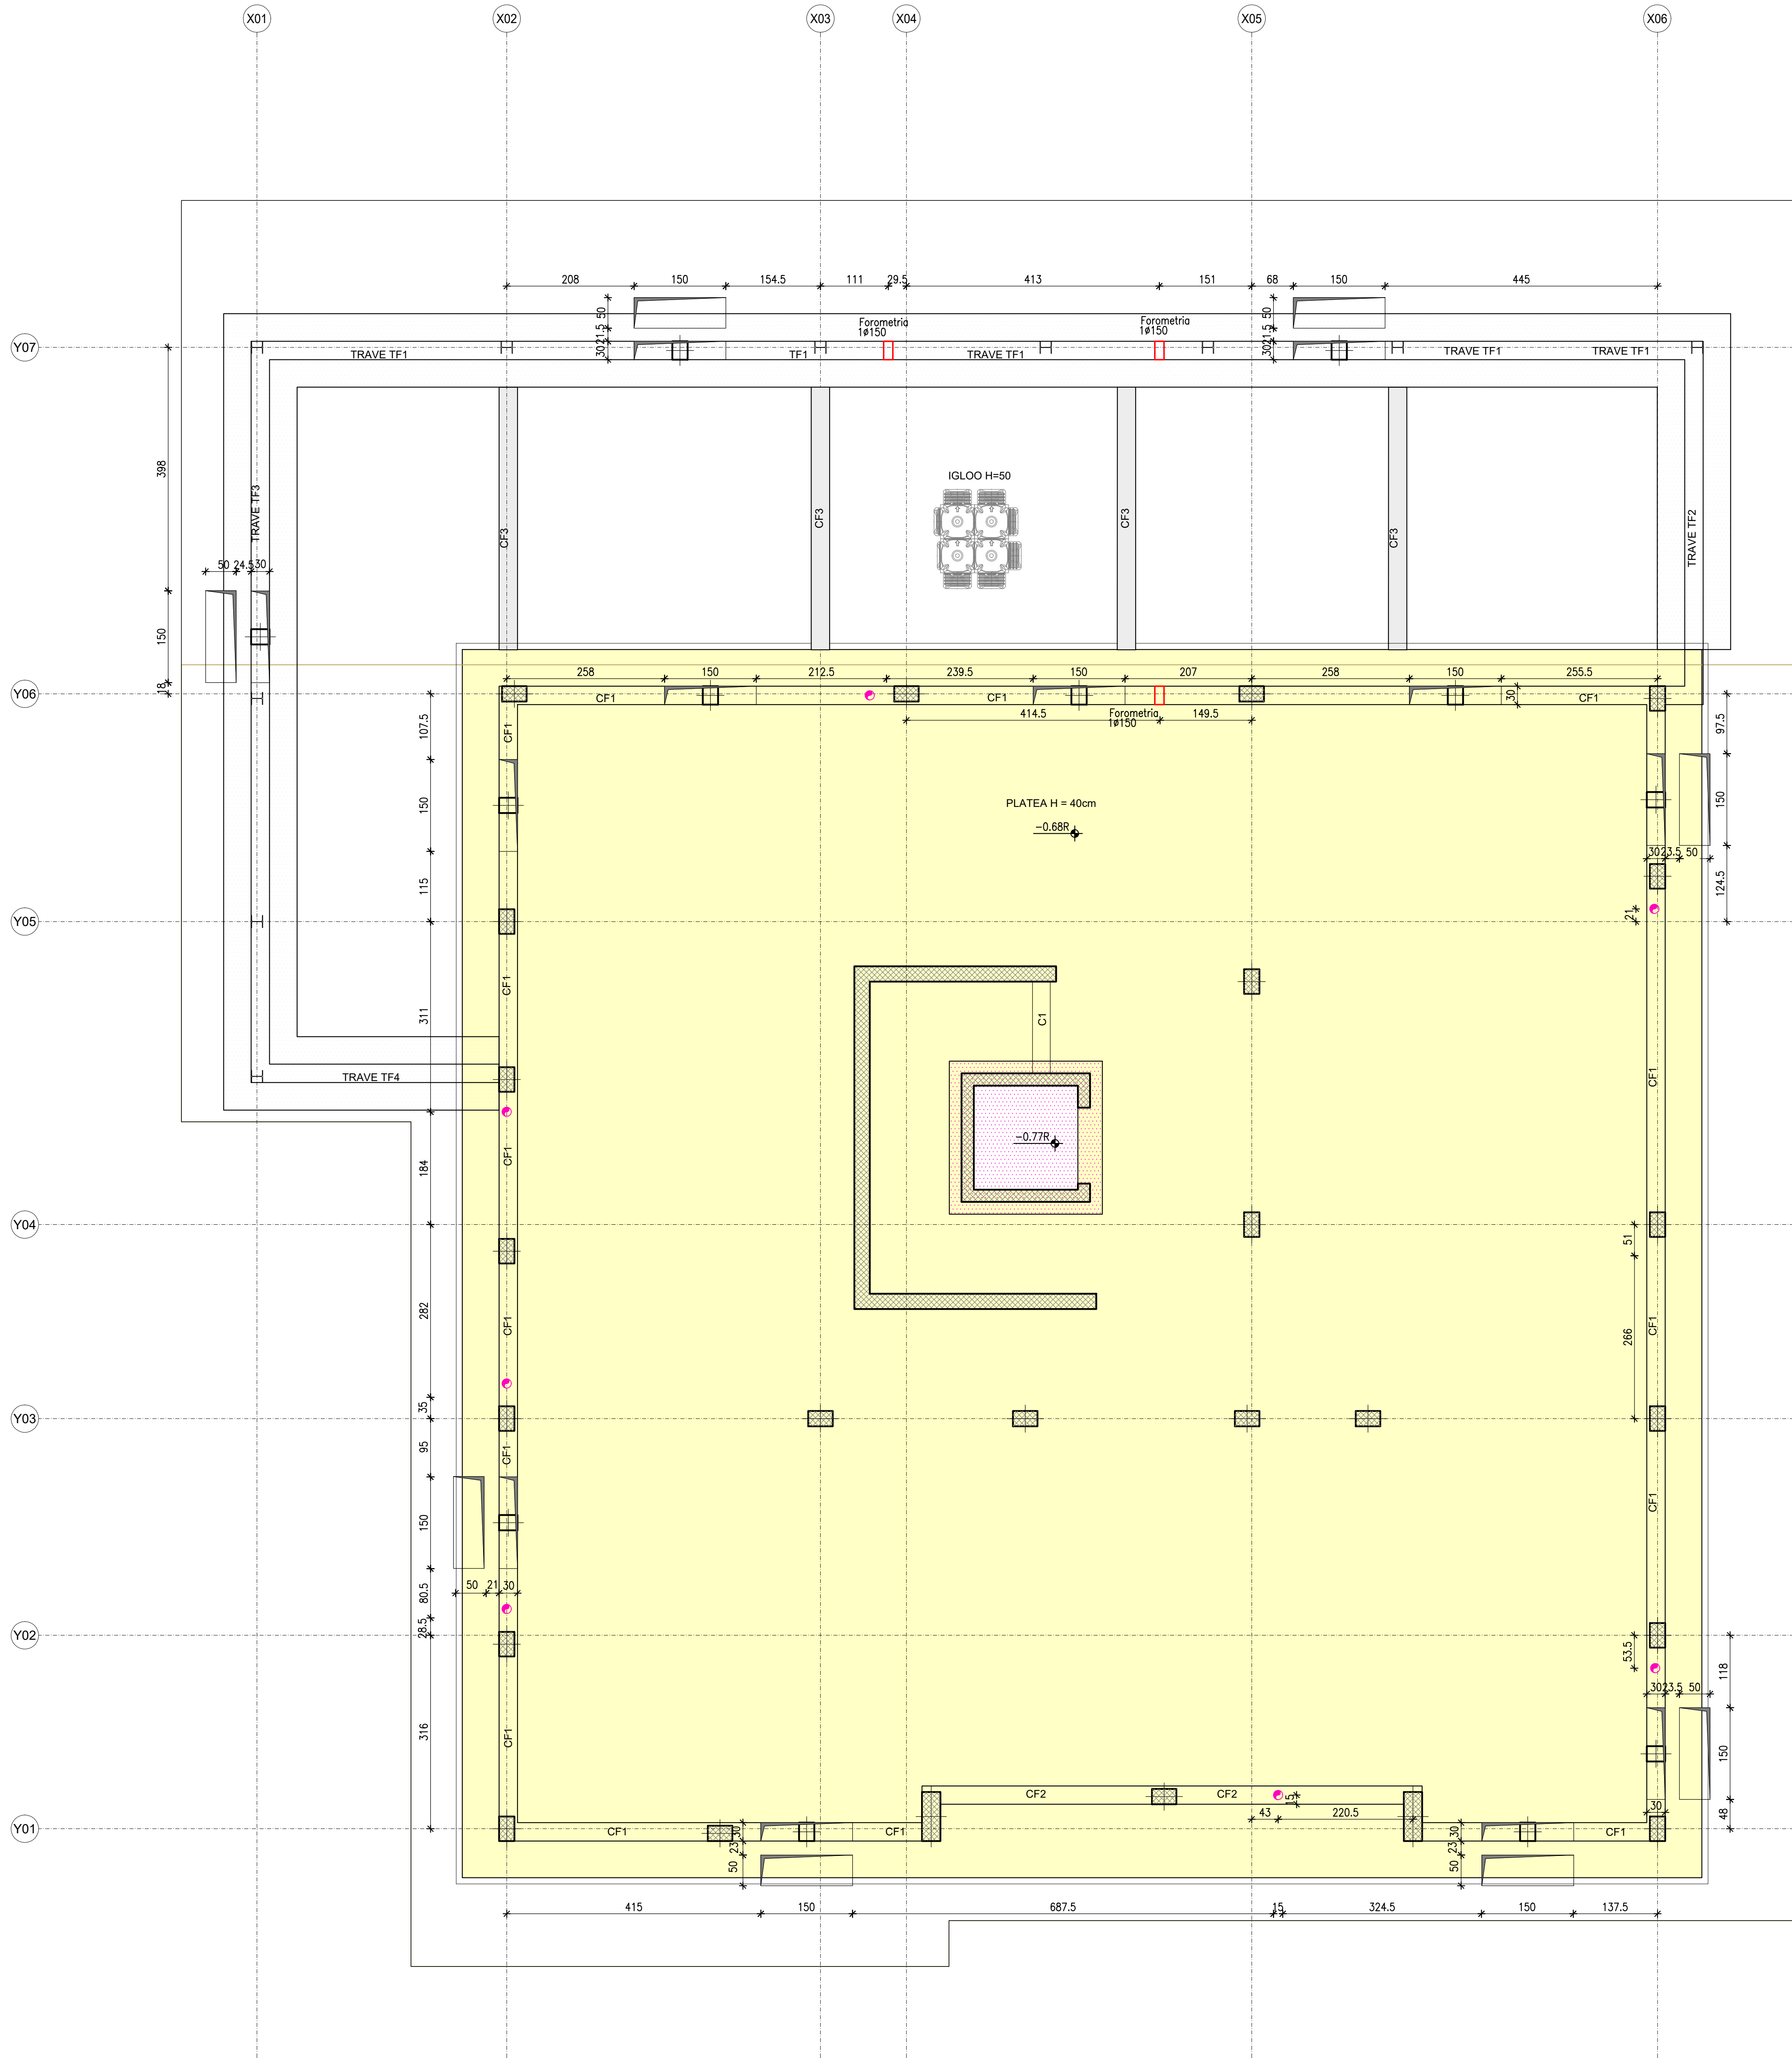

TAVOLE DI RIFERIMENTO			
S00			SPECIFICHE TECNICHE
S01			PIANTA TRACCIAMENTO
S02			PIANTA FONDAZIONI
	S02*		PIANTA FOROMETRIE FONDAZIONI
	S02a		ARMATURA AGGIUNTIVA PLATEA
S03	*		PIANTA PRIMO IMPALCATO
S04	*		PIANTA SECONDO IMPALCATO
S05	*		PIANTA COPERTURA
S06			ABACO PILASTRI
S07			VANO SCALA E ASCENSORE
*			ATTENZIONE!!! BLOCCO TAVOLE ELEMENTO STRUTTURALE

PER SPECIFICHE MATERIALI E DETAGLI COSTRUTTIVI VEDERE TAVOLA ES-00-00, SPECIFICHE TECNICHE


ATTENZIONE! POSIZIONARE AI LATI DELLE FOROMETRIE NELLE TRAVI DUE STAFFE ACCOPIATE

COLONNA
Ø150




DETAGLIO ARMATURA AGGIUNTIVA FORO SOLAIO

scala 1:20

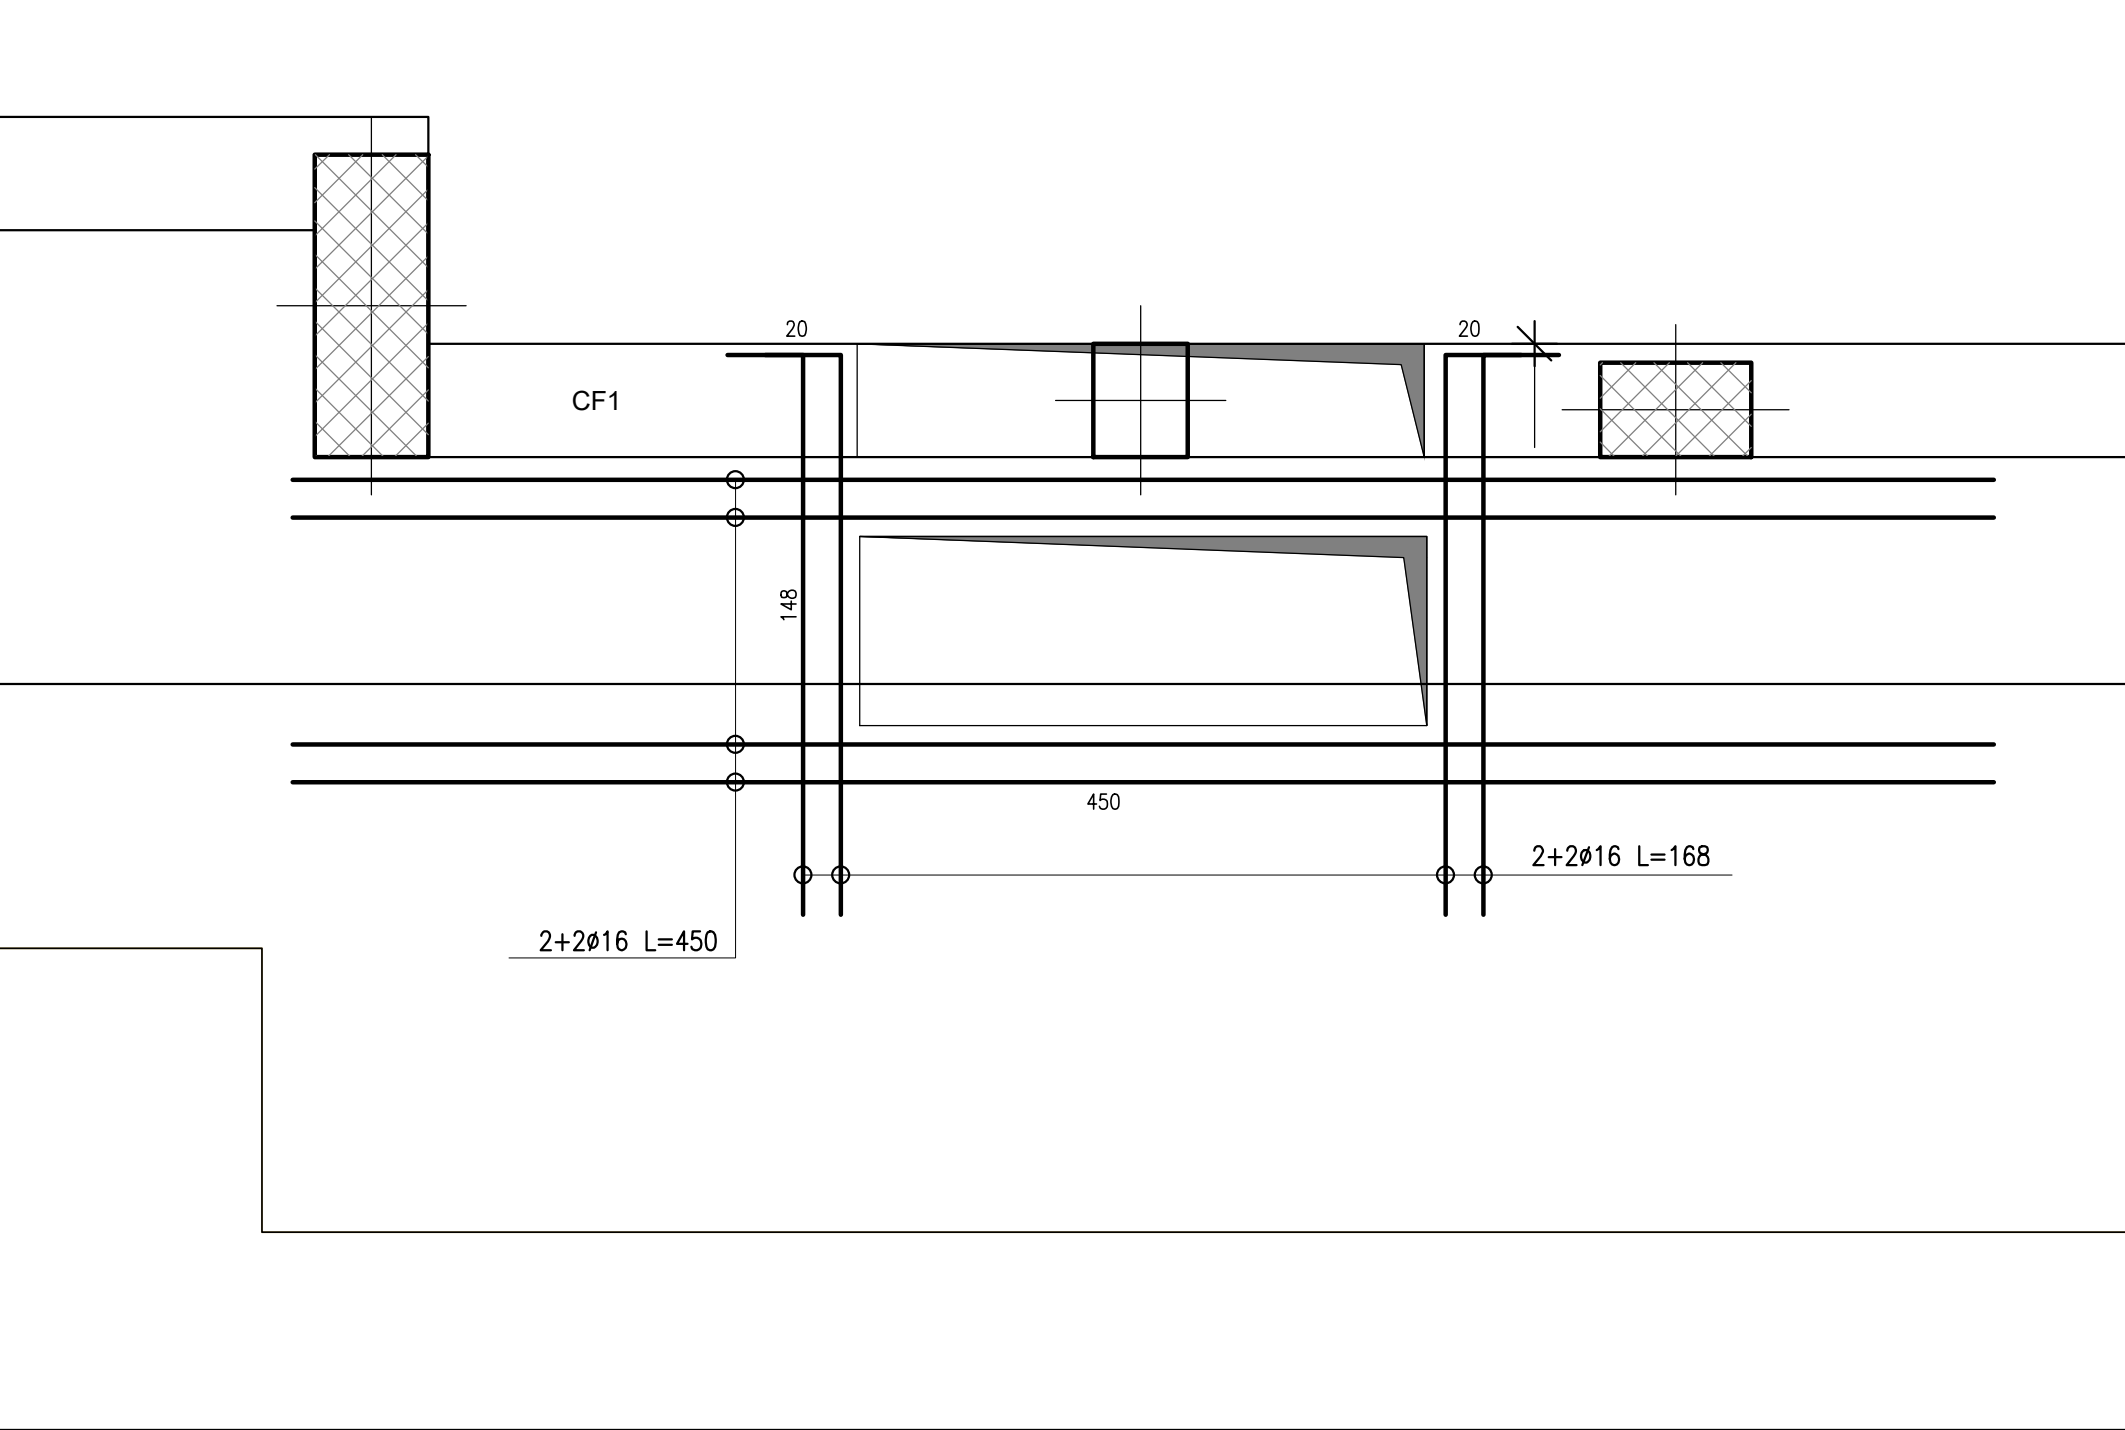

DETAGLIO APERTURE VENTILAZIONE VESPAIO

scala 1:20

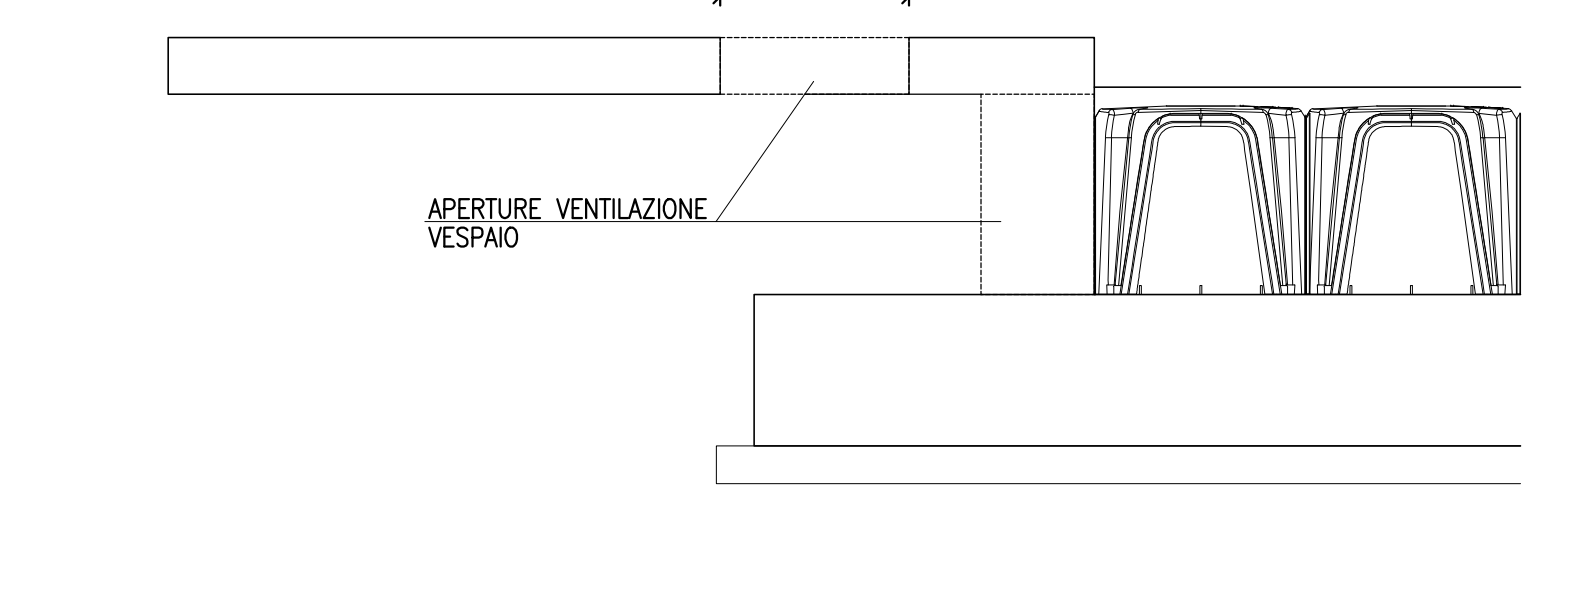

GB&PARTNERS
INGEGNERIA E ARCHITETTURA

STEN
STUDIO TECNICO E NORMATIVO

Progetto strutturale:
Ing. Alessandro Bertozzi
Piazza Alpini, 2
25039 Travagliato (BS)
Cell. 3890777193
E-mail: alessandro@bertozzingegneria.it

COMUNE DI COLOGNO MONZESE (MI)
AREA Ex TORRIANI ARAS 01
PROGETTO ESECUTIVO
Progetto Servizi Abitativi Pubblici di via Pergolesi

N°	DATA	DESCRIZIONE MOTIVAZIONE DELL'AGGIORNAMENTO	STUDIO	DIS.
00	09/06/2025	Prima emissione	STEN	ST
01	26/01/2026	Modifiche architettoniche 260118	STEN	ST

Progetto
PROGETTO ESECUTIVO
Servizi Abitativi Pubblici
Comune di Cologno Monzese (MI)

Proponente
Officine Mak S.r.l.
Corso Europa, 10
Milano 20122

Scala
1:50
Data
26/01/2025

Tipo tavola
ESECUTIVI
Serie
STRUTTURE
Titolo
PIANTA FOROMETRIE FONDAZIONI

Tavola nr.
Tipo
Tavola
E
Siga /
Serie
S
Numero /
Variante
02*
Agg.
01

Il Progettista
Gianpietro Bidinchi

Il Proponente

Orientamento
N

Documento di proprietà della Società G.B. & Partners S.r.l. E' vietata la riproduzione. Tutti i diritti sono riservati.