



scala 1:100

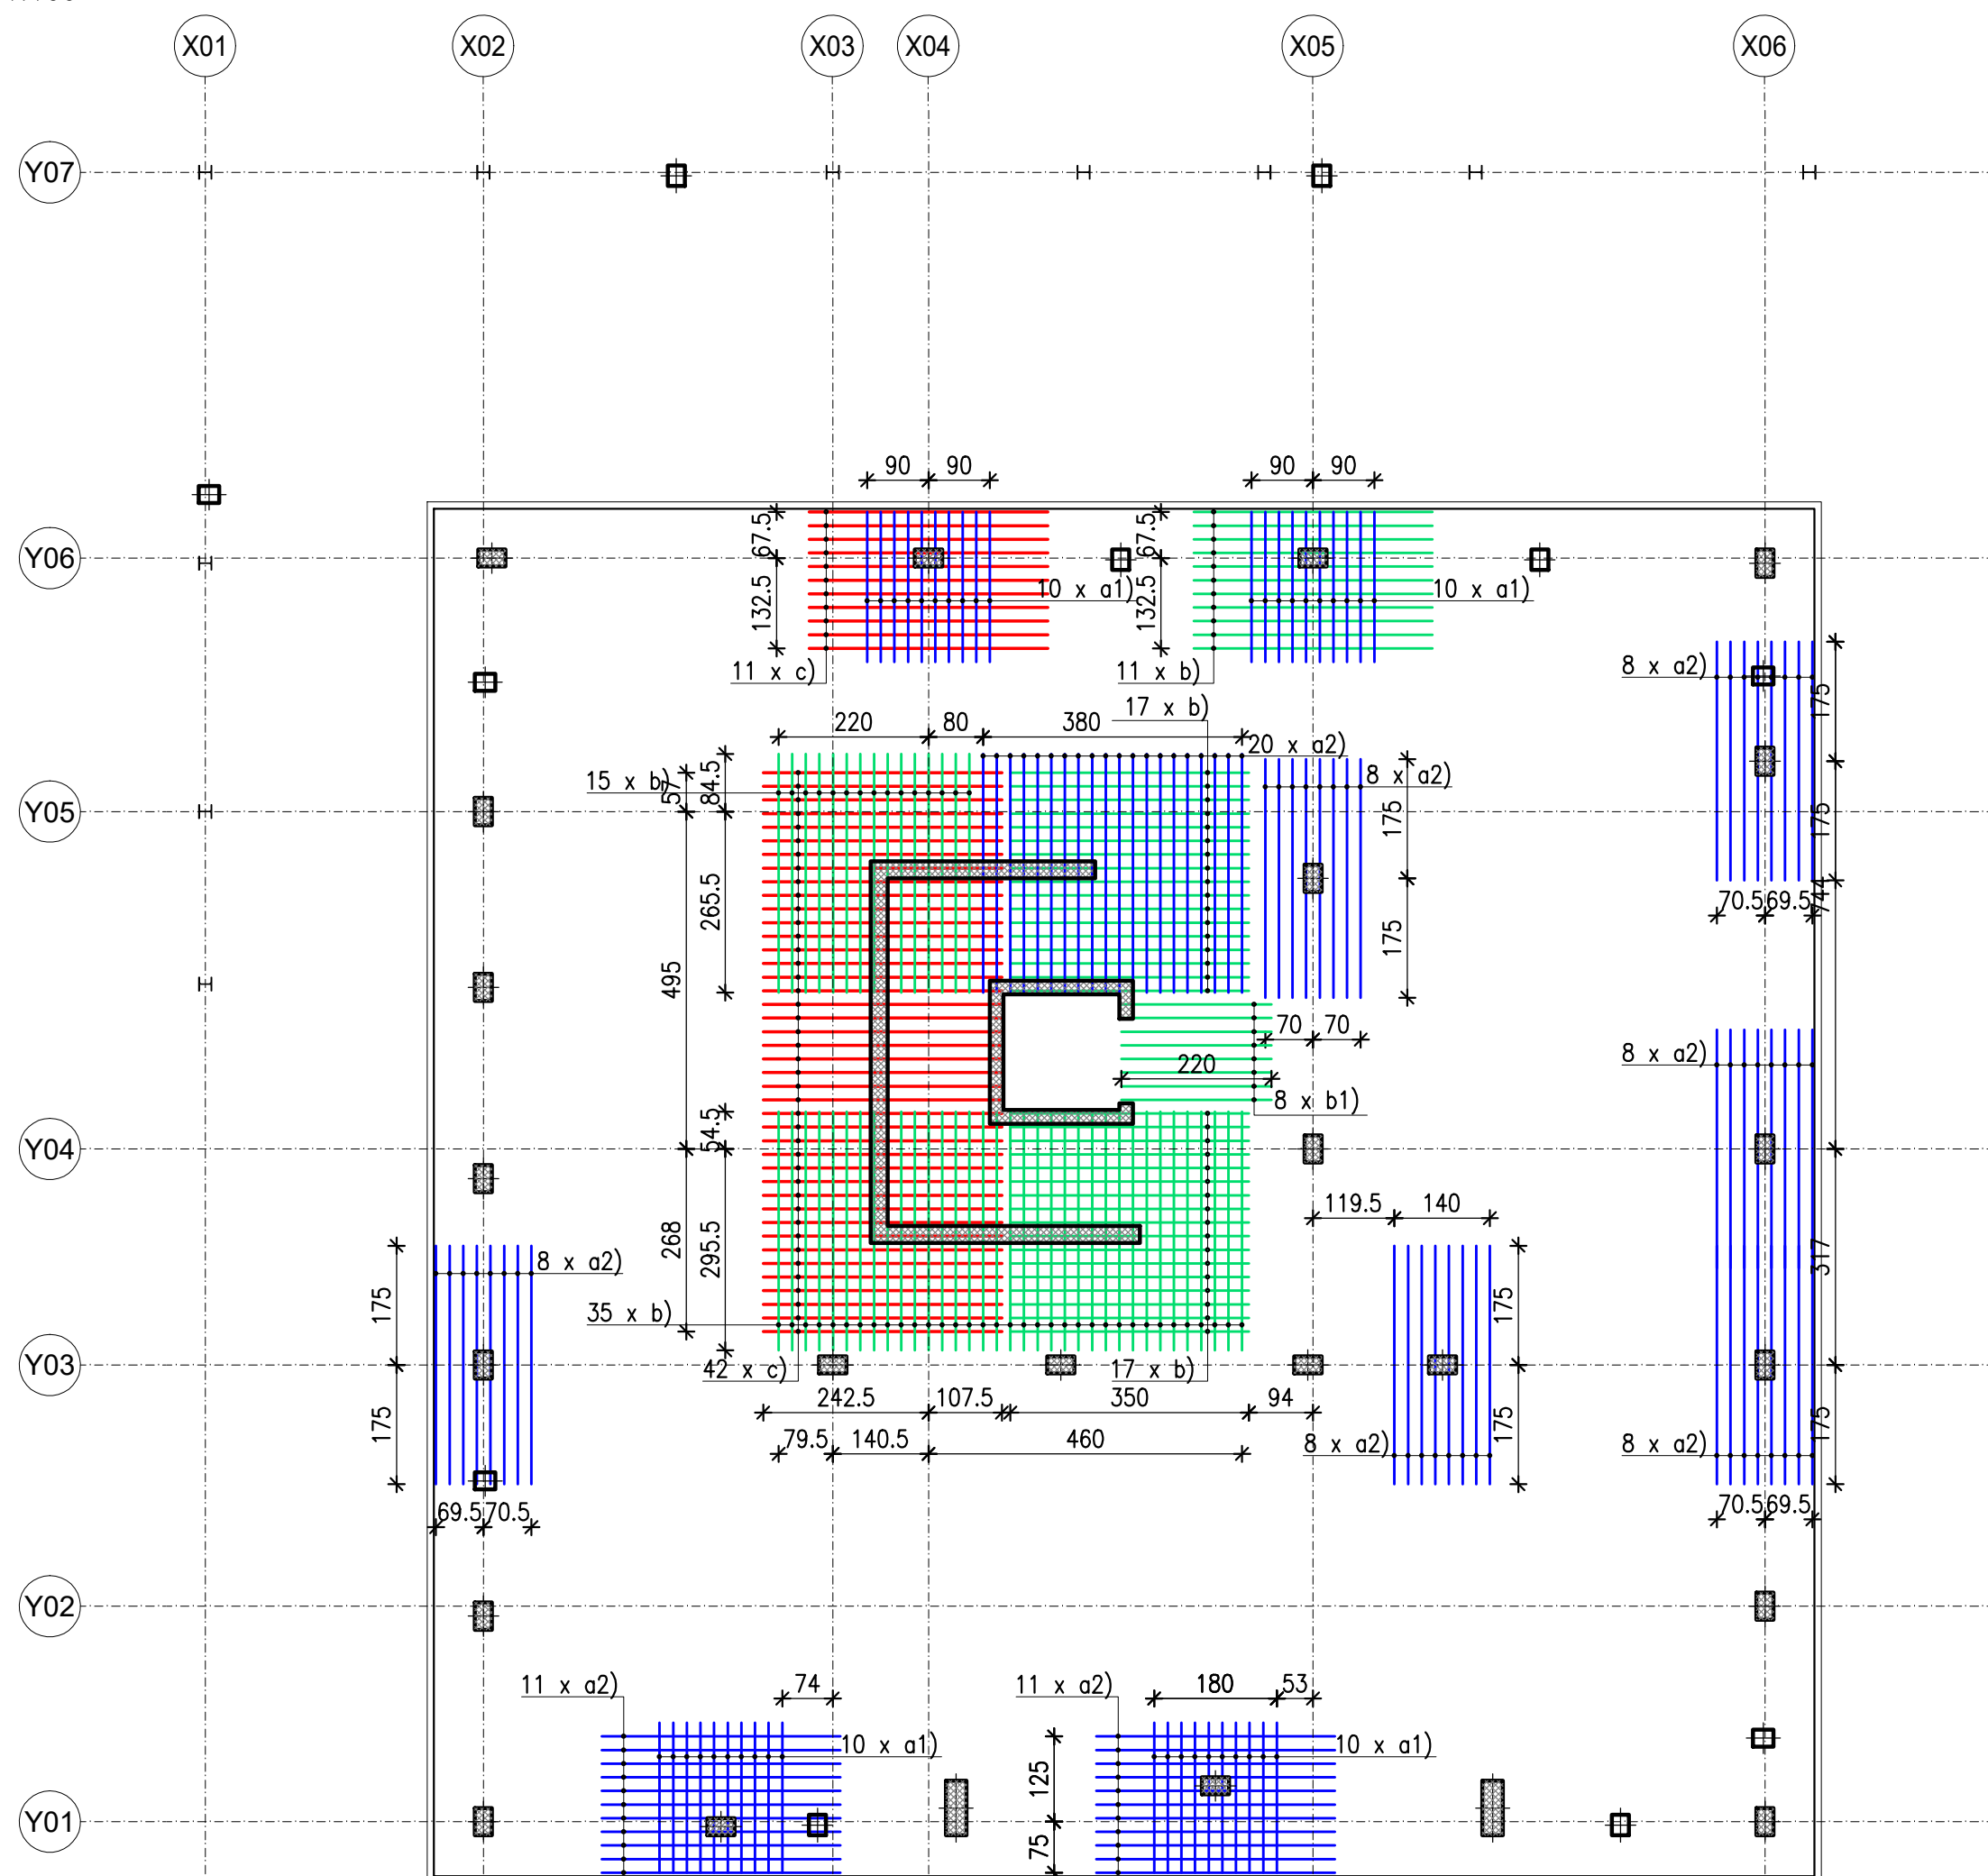


scala 1:100

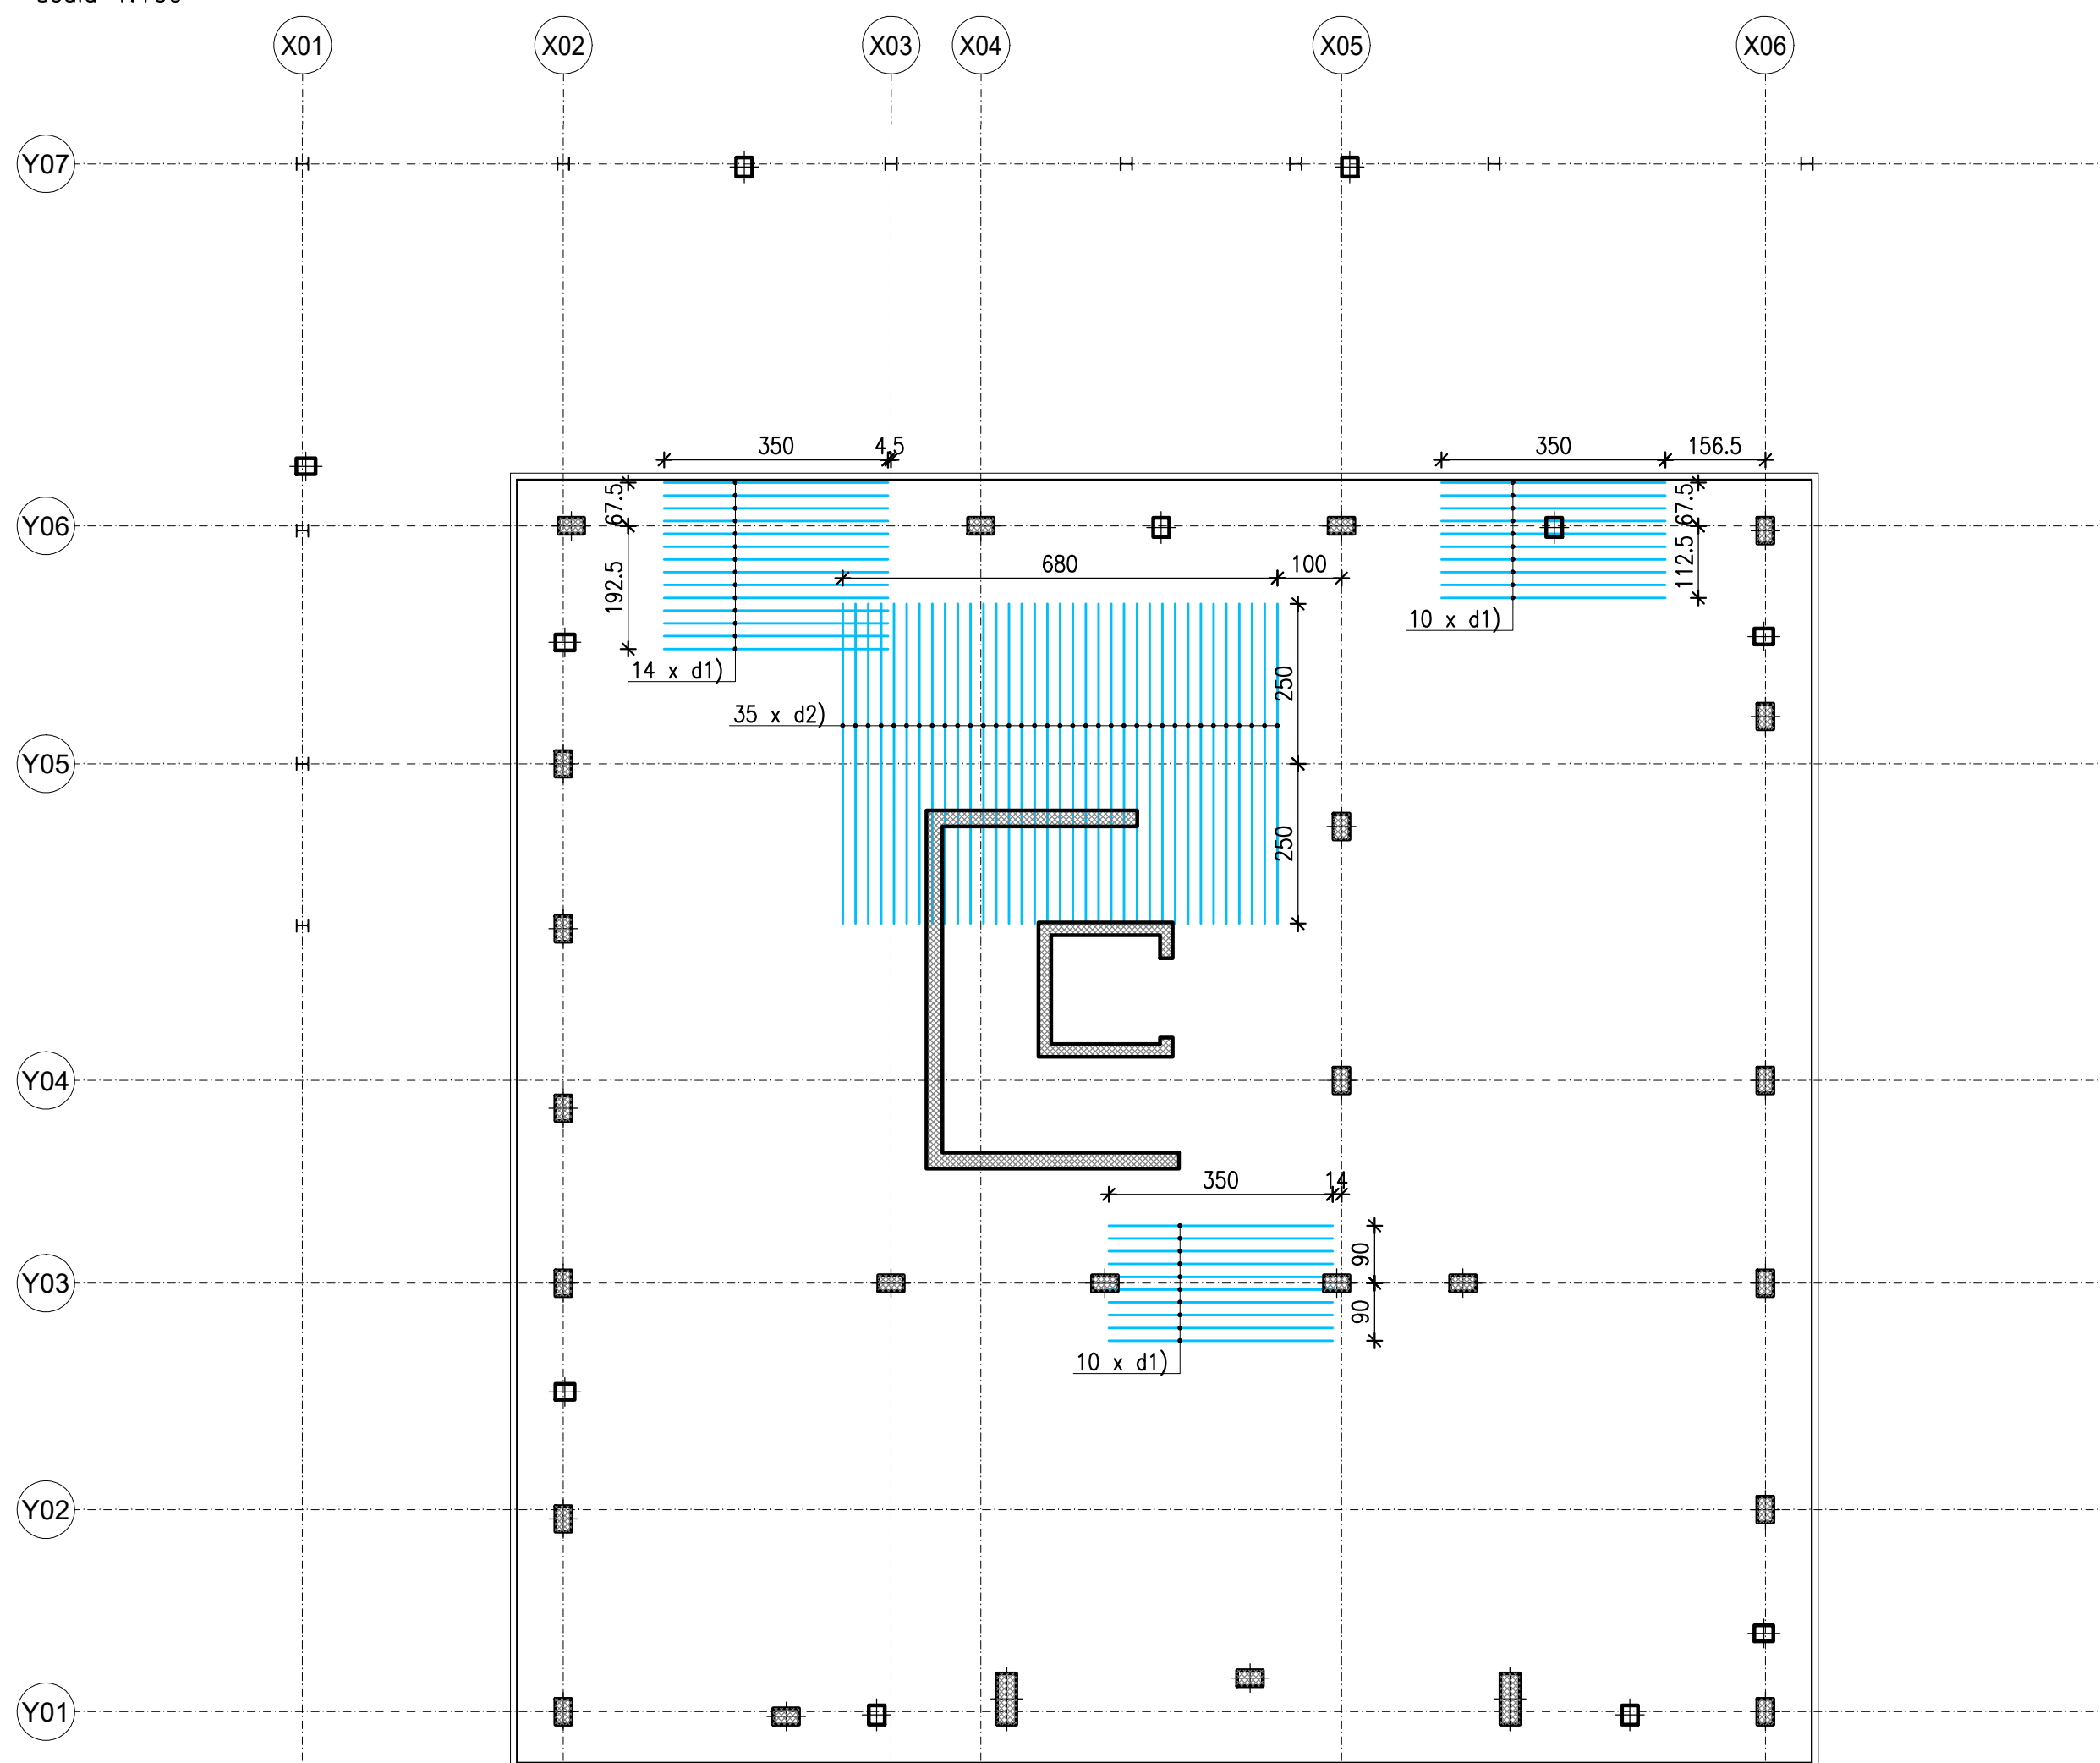

S00			SPECIFICHE TECNICHE
S01			PIANTA TRACCIAMENTO
S02	*		PIANTA FONDAZIONI
	S02a		ARMATURA AGGIUNTIVA PLATEA
S03	*		PIANTA PRIMO IMPALCATO
S04	*		PIANTA SECONDO IMPALCATO
S05	*		PIANTA COPERTURA
S06			ABACO PILASTRI
S07			VANO SCALA E ASCENSORE
*			ATTENZIONE!!!! BLOCCO TAVOLE ELEMENTO STRUTTURALE

scala 1:50

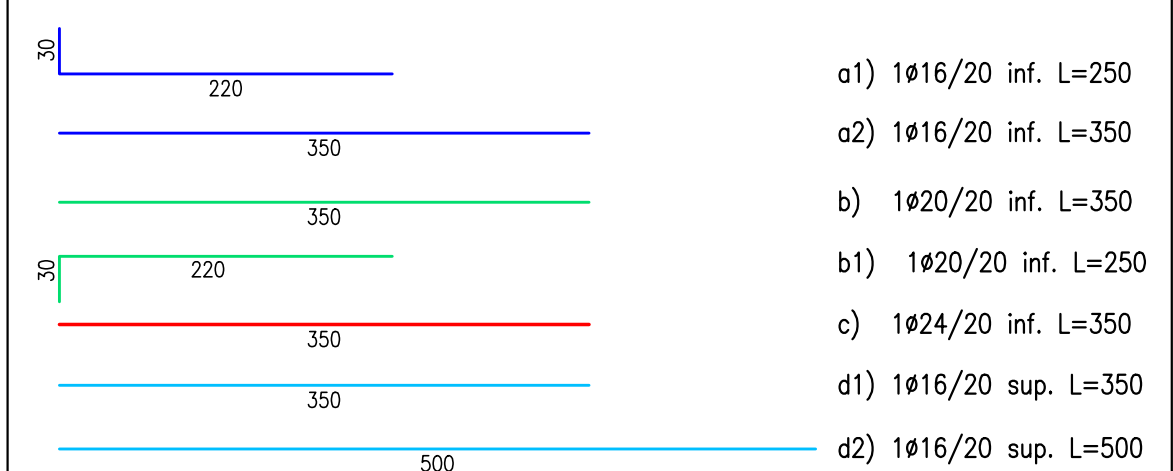

PER SPECIFICHE MATERIALI E DETTAGLI COSTRUTTIVI VEDERE TAVOLA ES-00-00 SPECIFICHE TECNICHE



GB&PARTNERS
SERVIZIO PROGETTI (IMMOBILIARI)

Via Ivrea 10/24 - 00187 Roma
 Telefono: 06/6784.300.00
 E-mail: info@gbpartners.it
 Web: www.gbpartners.it

Partita IVA 01500001000
 P.IVA 01500001000
 Registro Imprese Roma 10000001000
 C.C.I.A.A. Roma 10000001000



2012 181 1001 9001 2018



2012 181 1001 14001 2018

Progetto strutturale:

Ing. Alessandro Bertozzi
 Piazzo Alpini, 2
 25039 Travagliato (BS)
 Cell. 3890777193
 E-mail: alessandro@bertozzingegneria.it

COMUNE DI COLOGNO MONZESE (MI)
AREA Ex TORRIANI ARAS 01
PROGETTO ESECUTIVO
Progetto Servizi Abitativi Pubblici di via Pergolesi

N°	DATA	DESCRIZIONE MOTIVAZIONE DELL'AGGIORNAMENTO	STUDIO	DIS.
00	22/05/2025	Prima emissione	STEN	LC
01	26/01/2026	Modifiche architettonico 260118	STEN	ST

Il Progettista



Il Proponente

Progetto
PROGETTO ESECUTIVO
Servizi Abitativi Pubblici
Comune di Cologno
Monzese (MI)

Proponente
Officine Mak S.r.l.
Corso Europa, 10
Milano 20122

Scala

1:100

26/01/2026

Tipo tavola

ESECUTIVI

Serie

STRUTTURE


Titolo

ARMATURA AGGIUNTIVA PLATEA

Tavola nr.

Tipo Tavola	E
Sigla / Serie	S
Numero / Variante	02a
Agg.	01

Orientamento

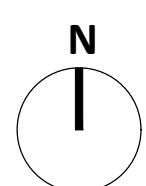

Documento di proprietà della Società G.B. & Partners S.r.l.. E' Vietata la riproduzione. Tutti i diritti sono riservati.