




TRAVE T1
scala 1:50

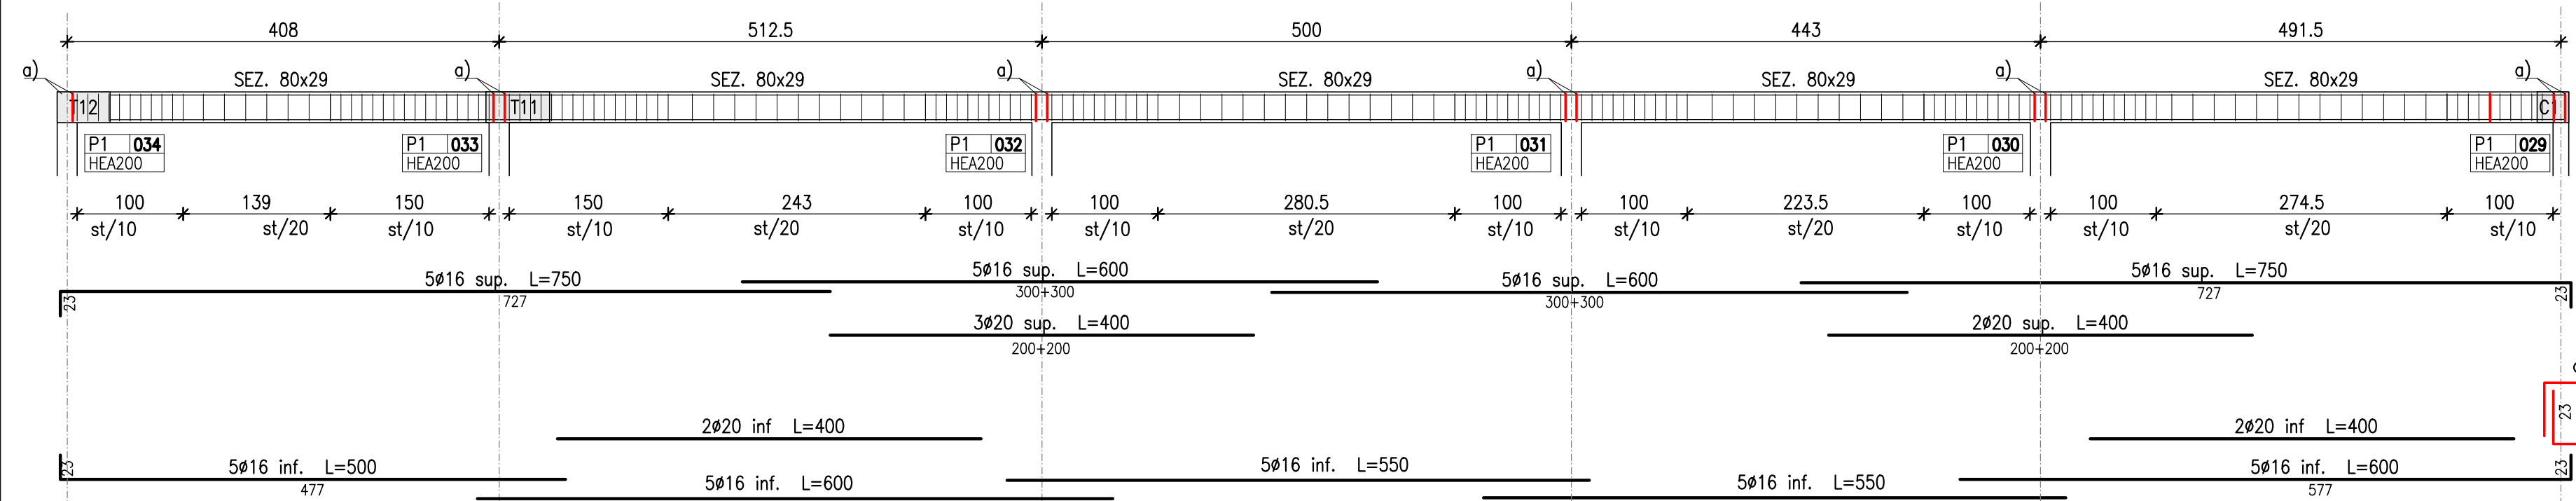


SEZIONE
scala 1:20

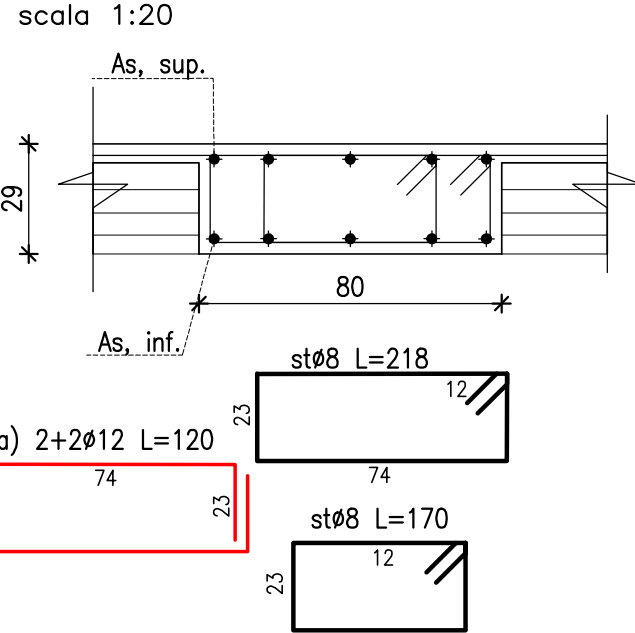


TRAVE T4
scala 1:50

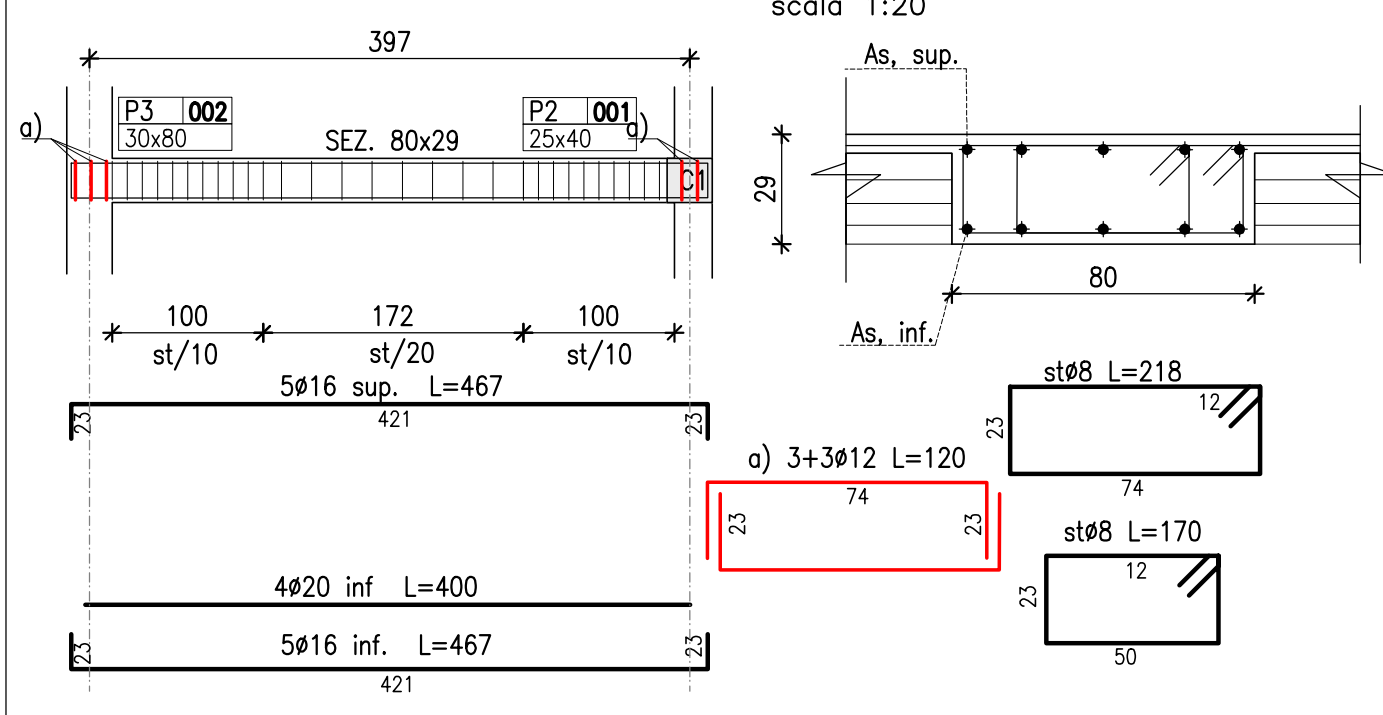


SEZIONE
scala 1:20

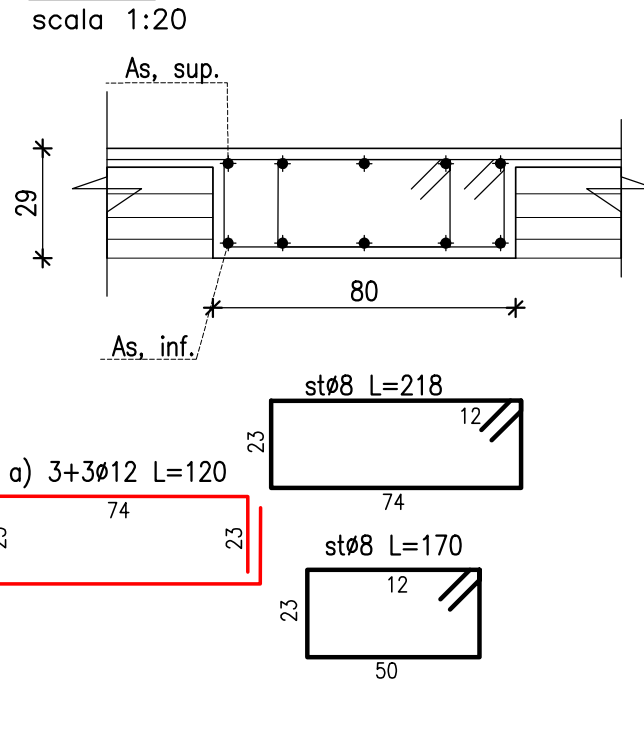


TRAVE T2
scala 1:50

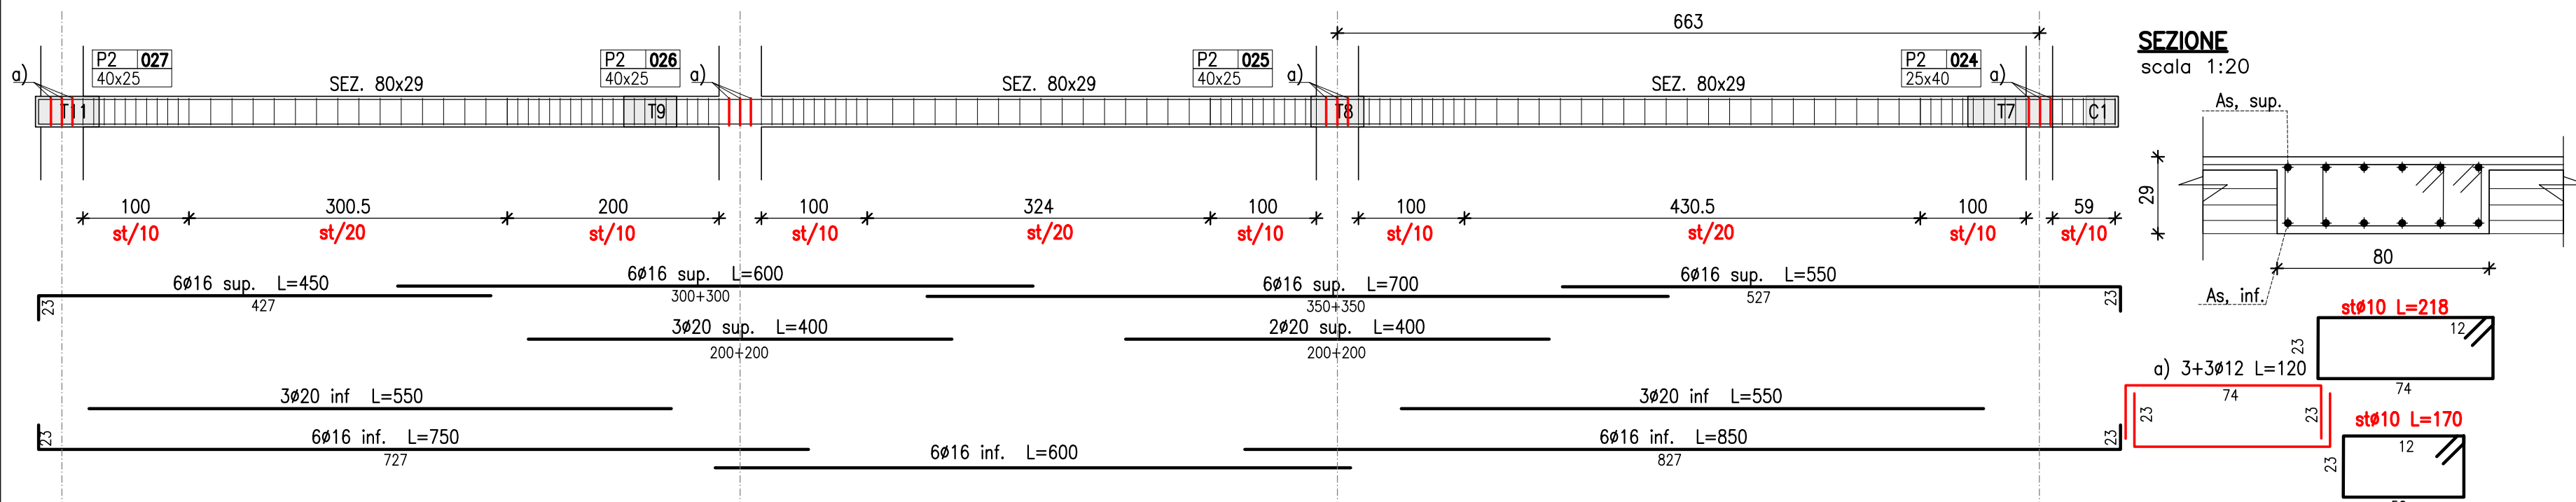


SEZIONE
scala 1:20

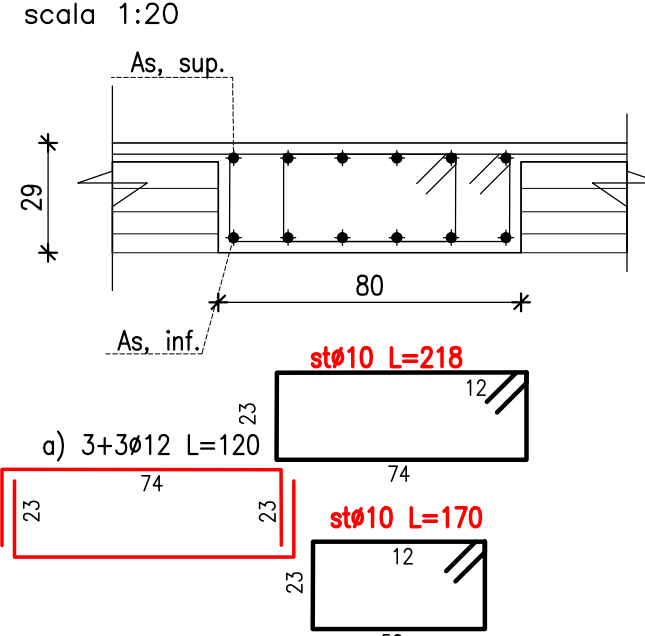


TRAVE T5
scala 1:50

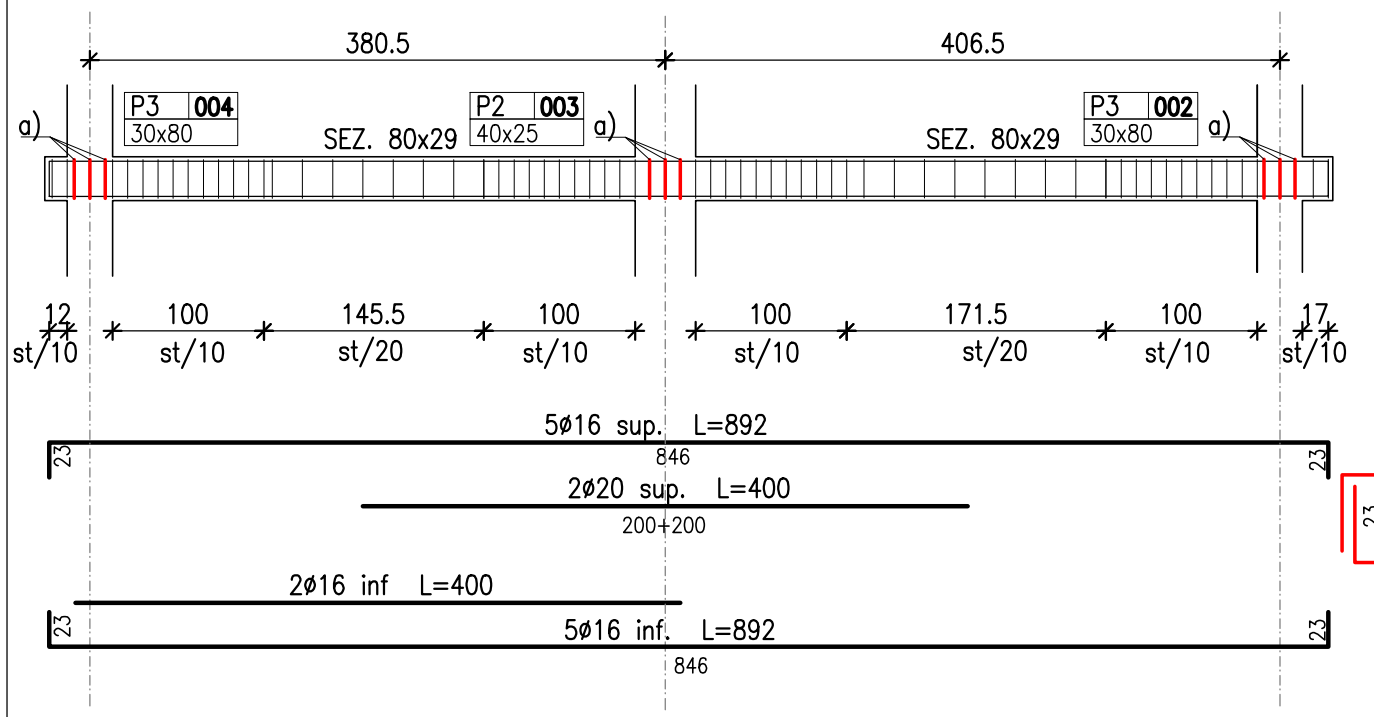


SEZIONE
scala 1:20

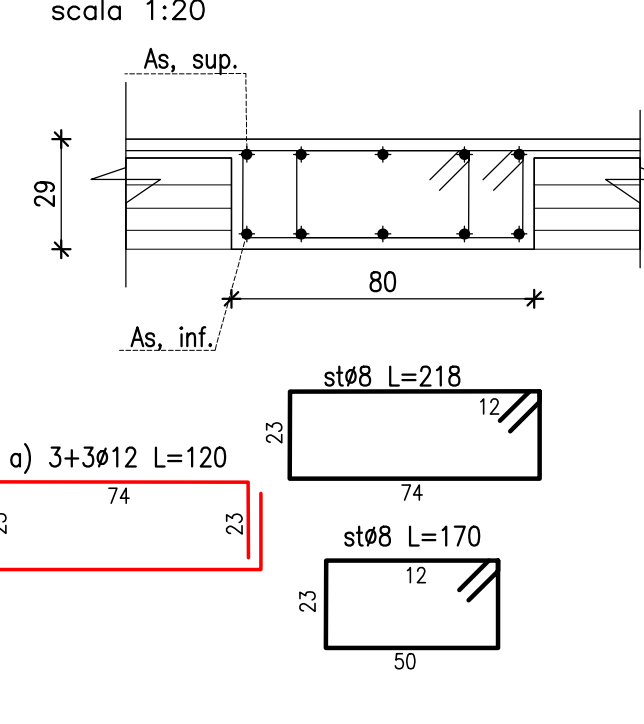


TRAVE T6
scala 1:50

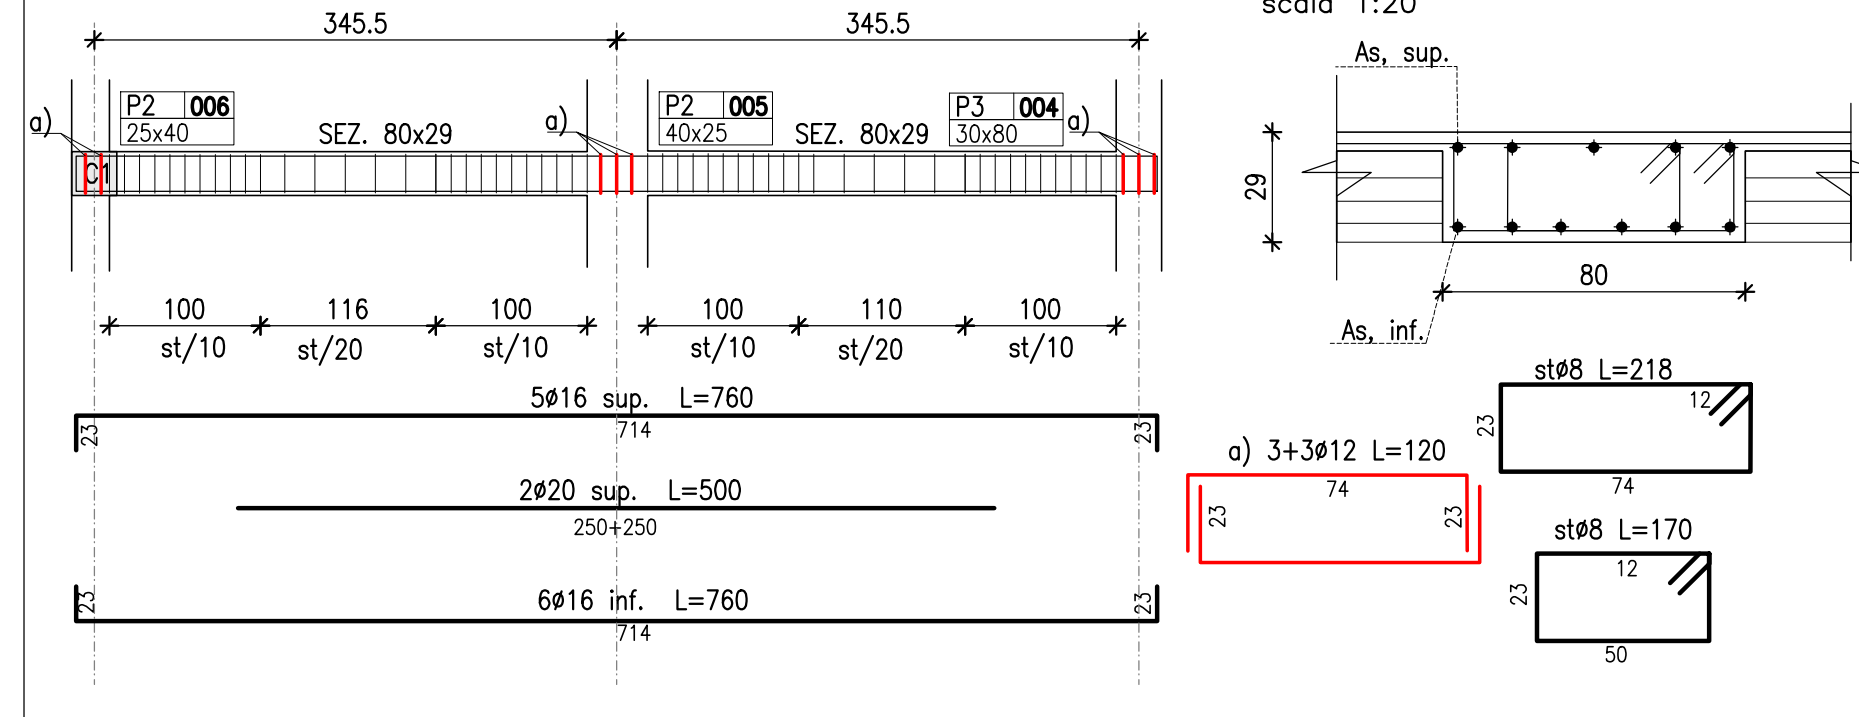


SEZIONE
scala 1:20

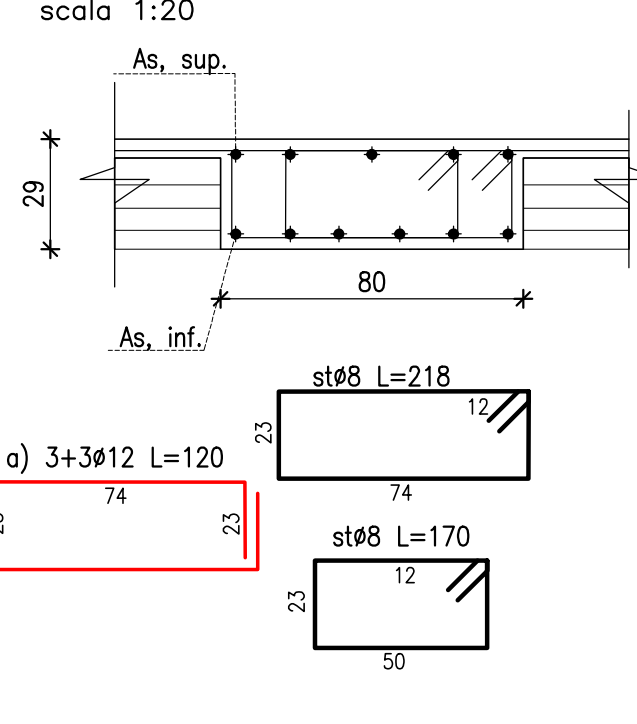


TRAVE T3
scala 1:50

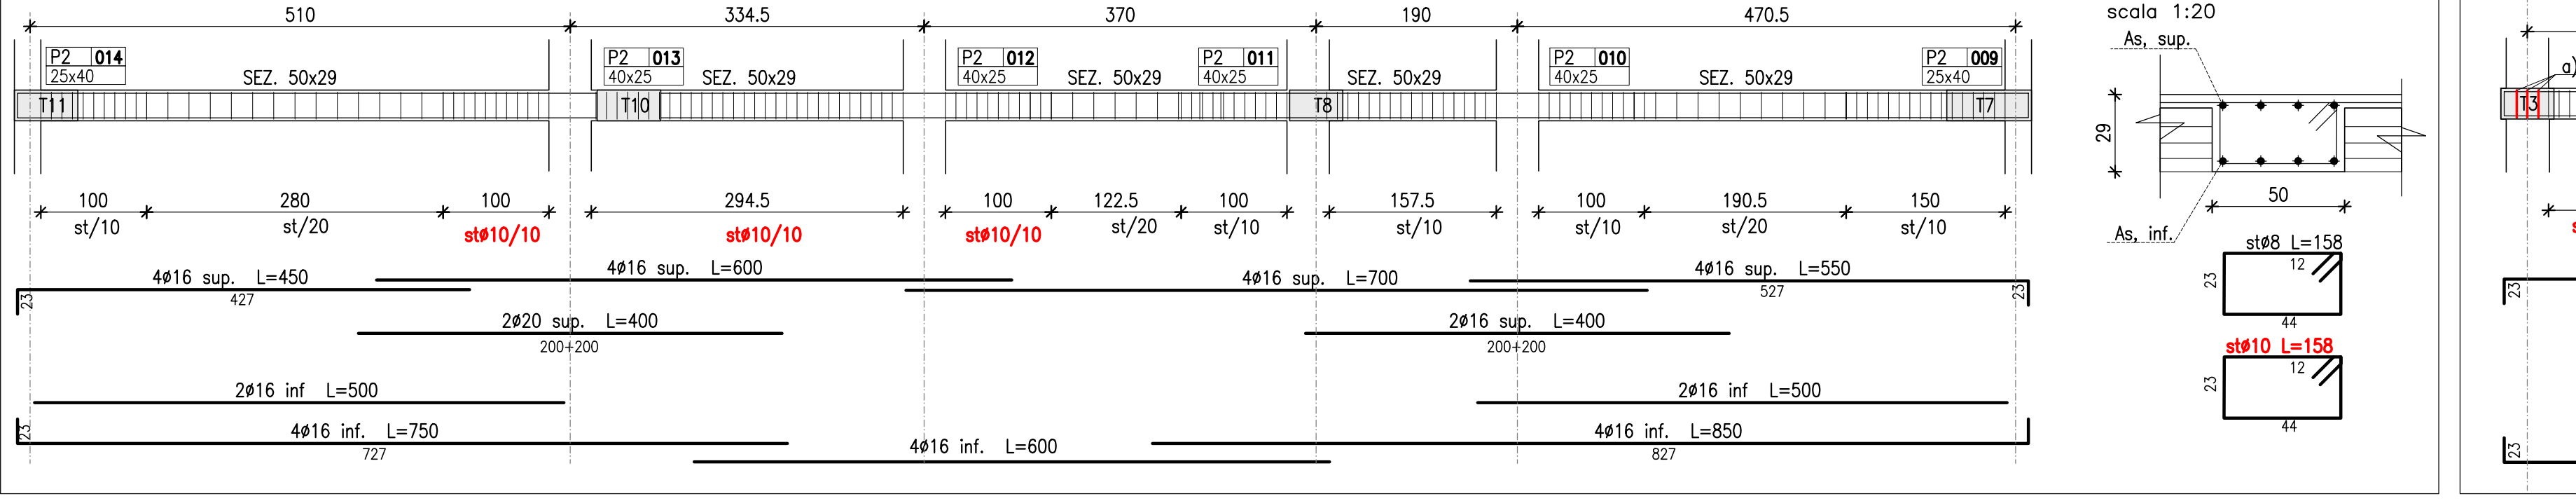


SEZIONE
scala 1:20

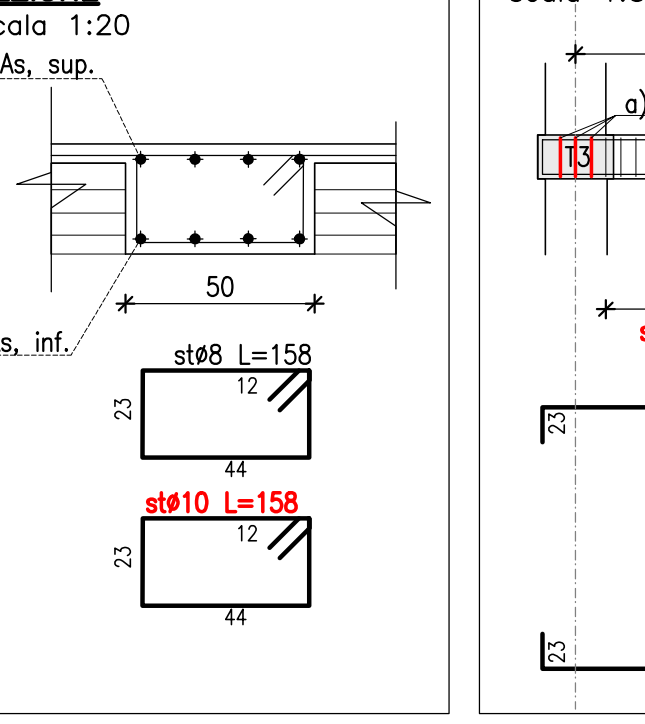


TRAVE T7
scala 1:50

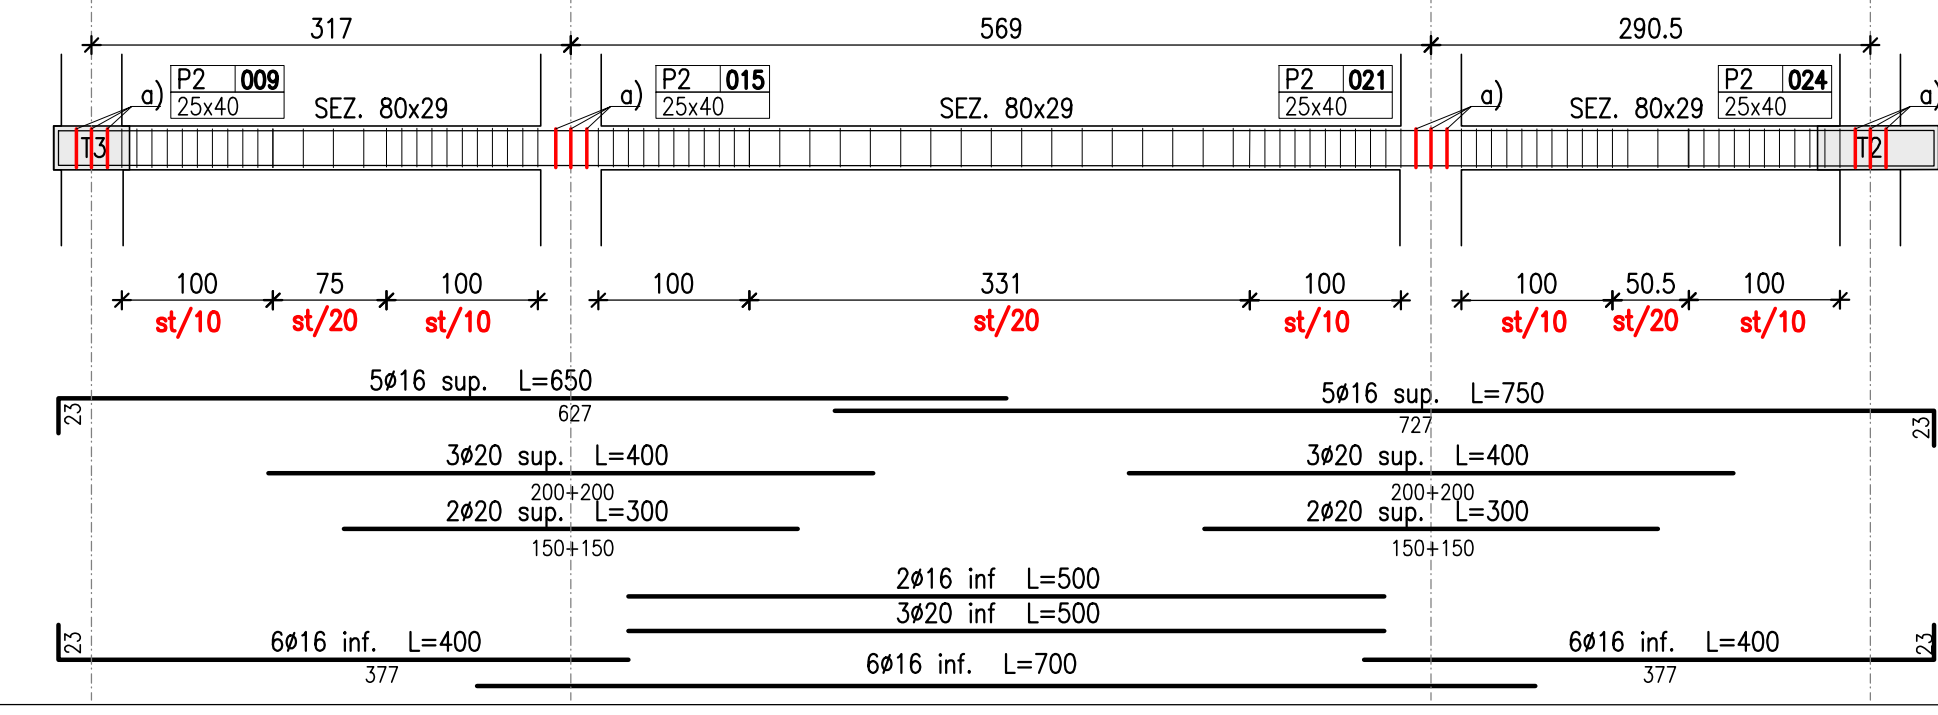


SEZIONE
scala 1:20

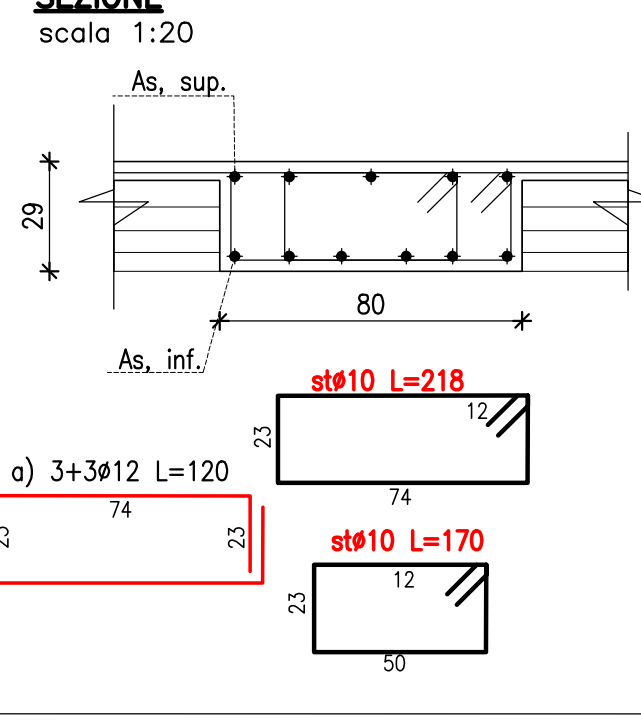


TRAVE T8
scala 1:50

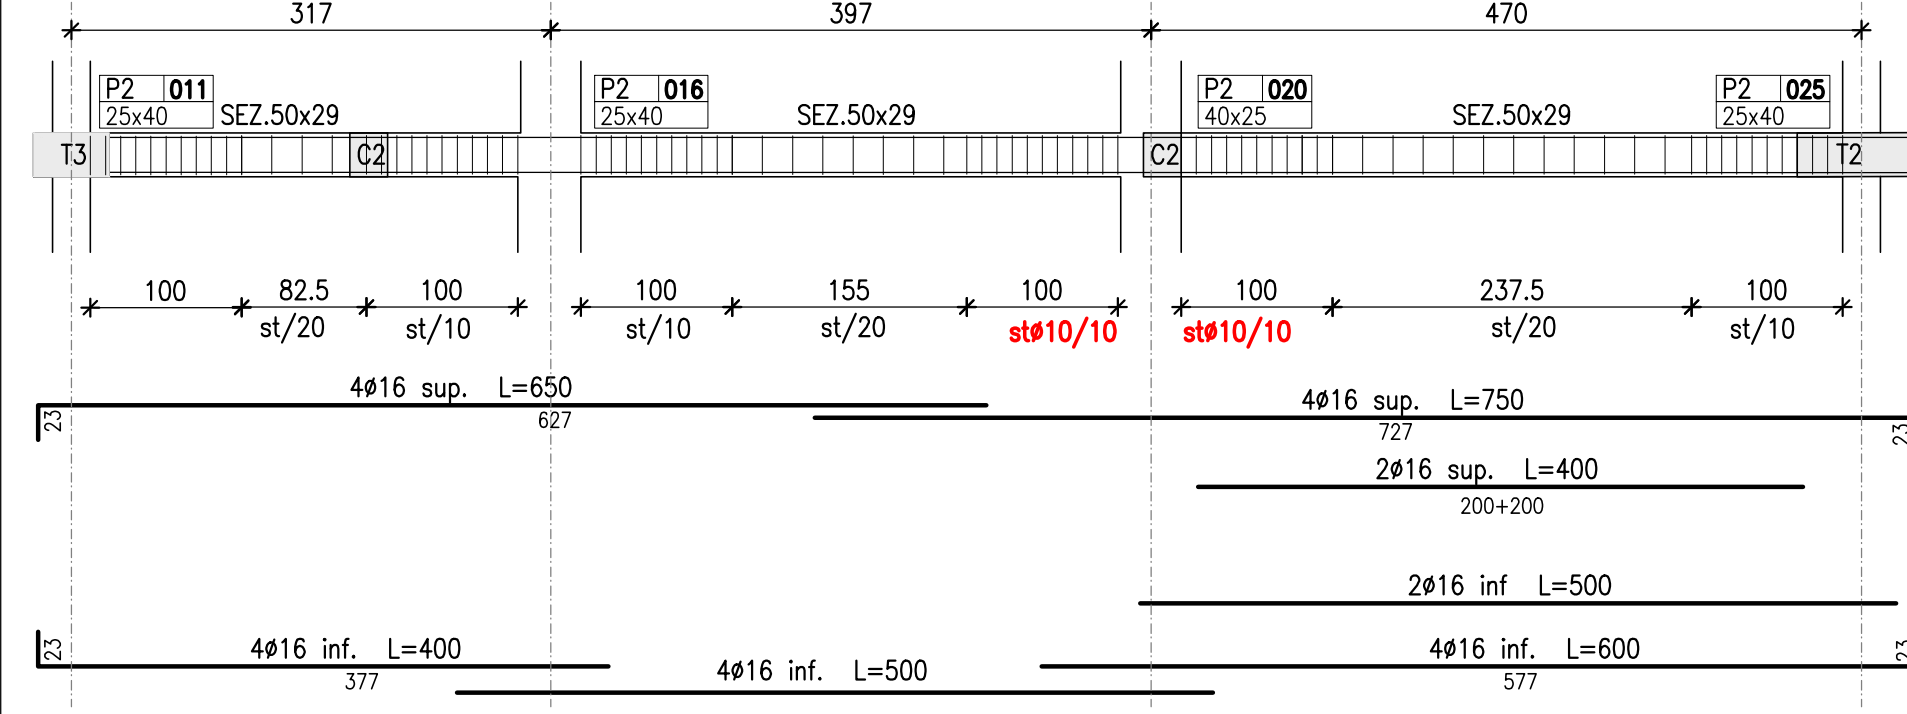


SEZIONE
scala 1:20

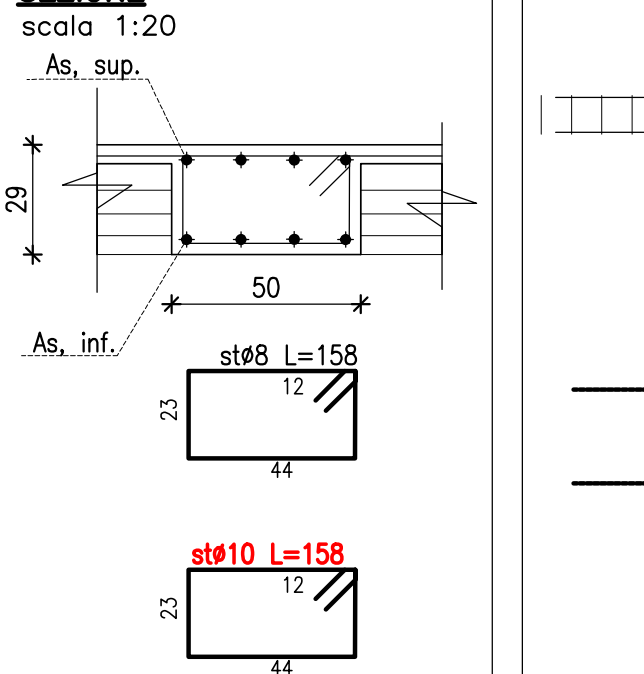


TRAVE T9
scala 1:50

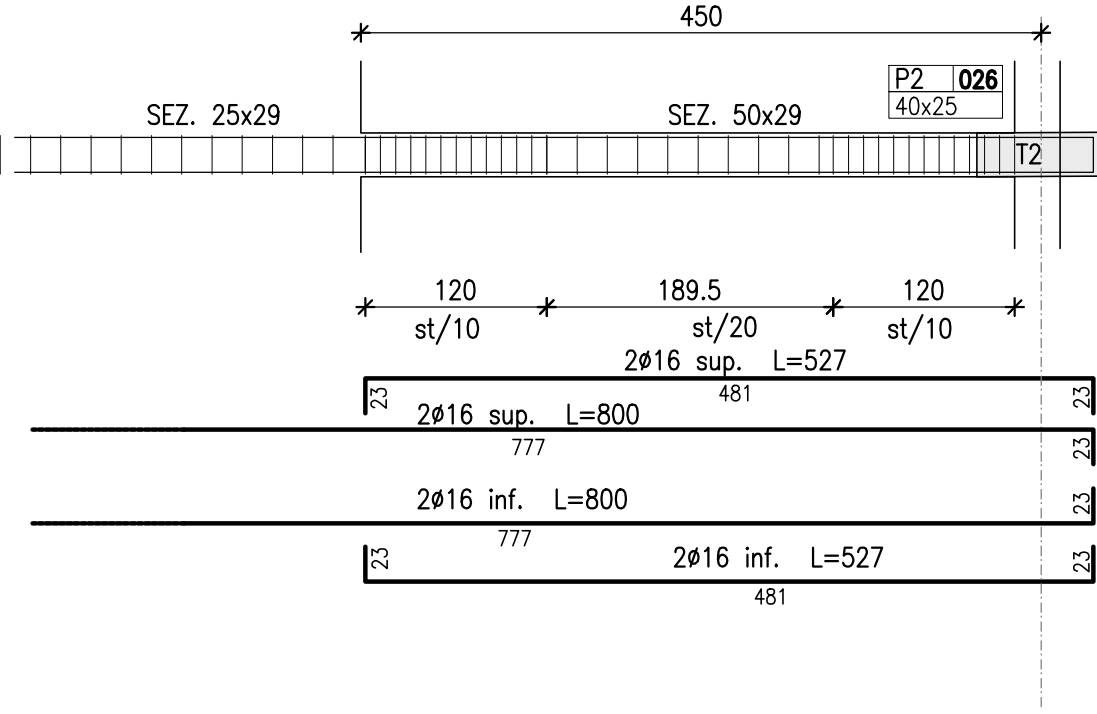


SEZIONE
scala 1:20

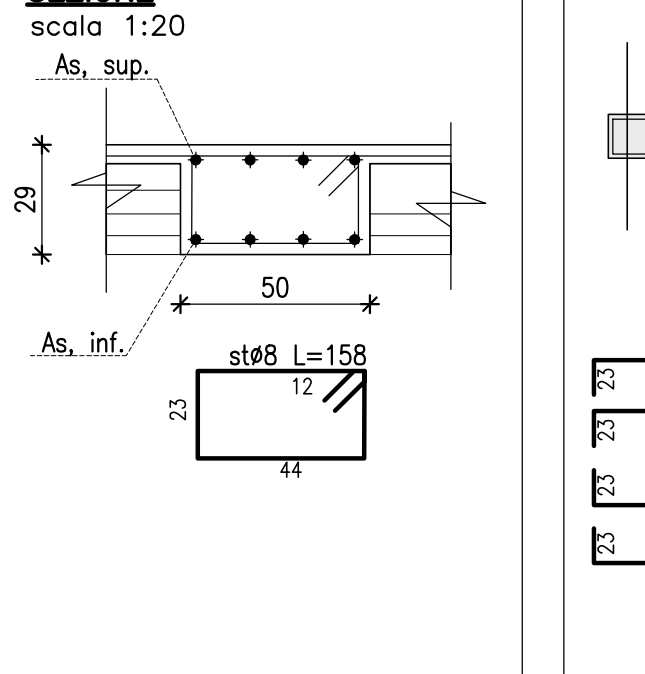


TRAVE T10
scala 1:50

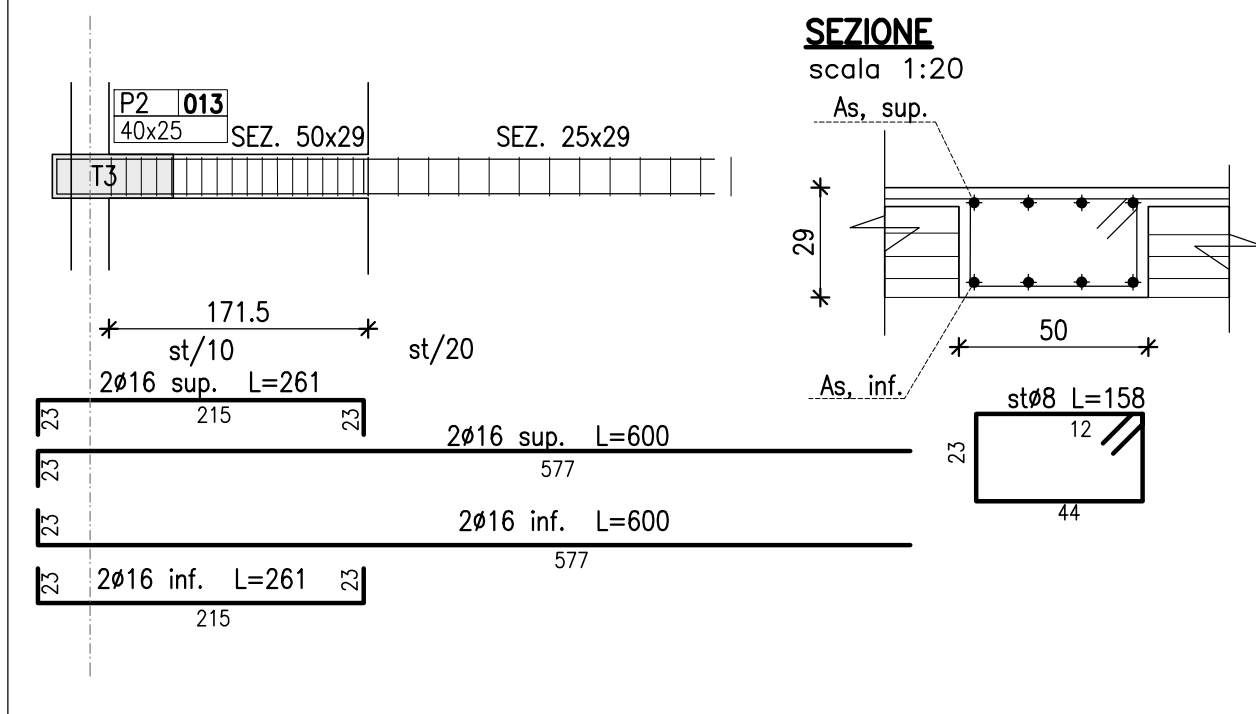


SEZIONE
scala 1:20

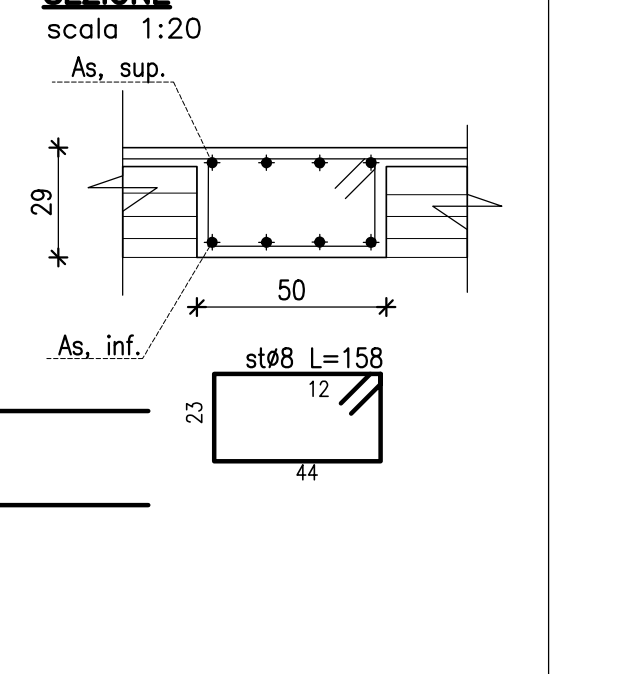


TRAVE T11
scala 1:50

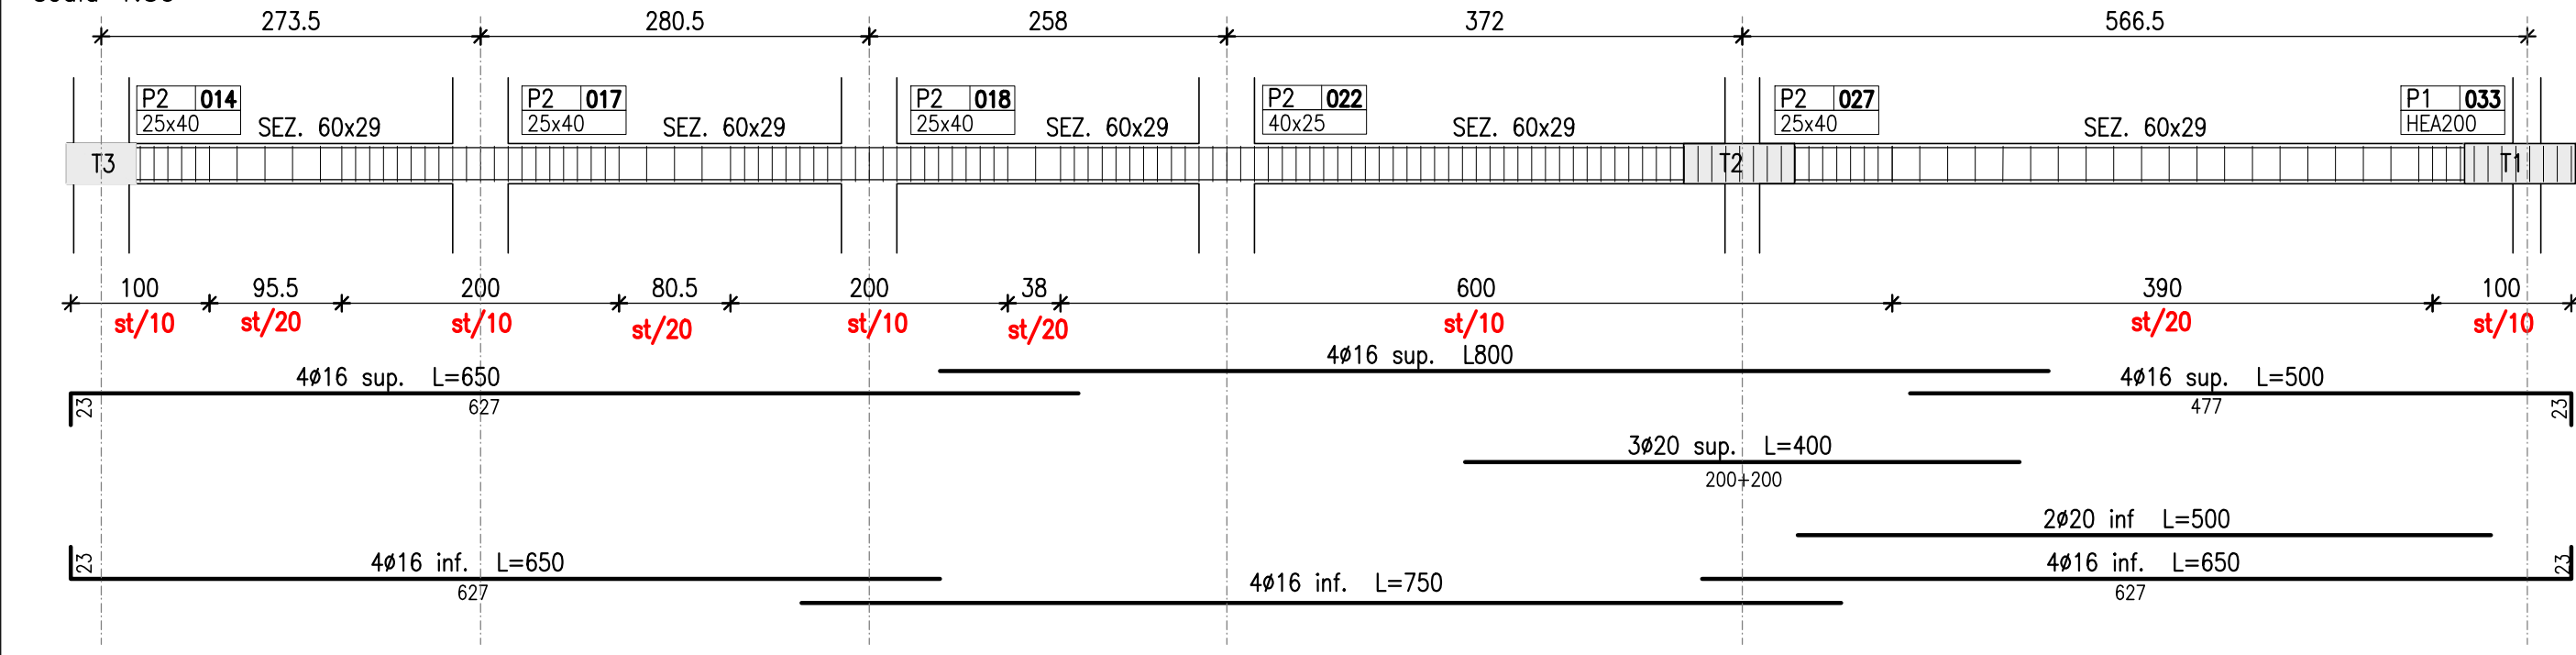


SEZIONE
scala 1:20

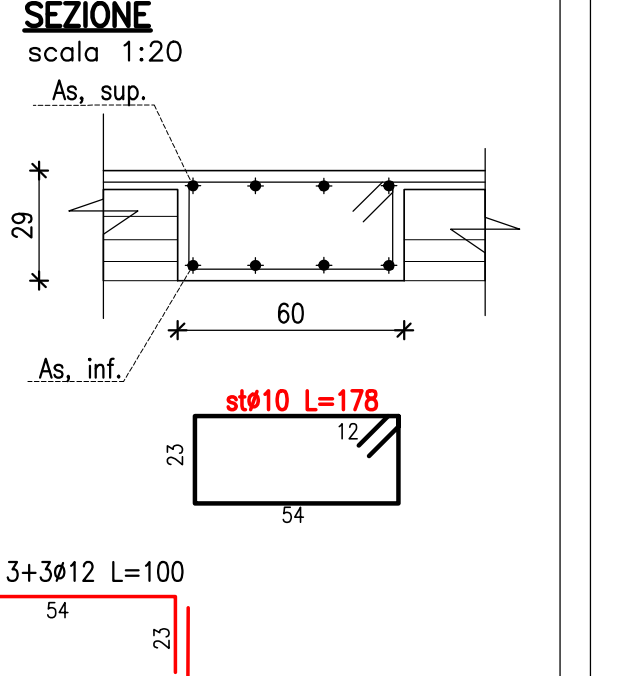

TRAVE T12
scala 1:50

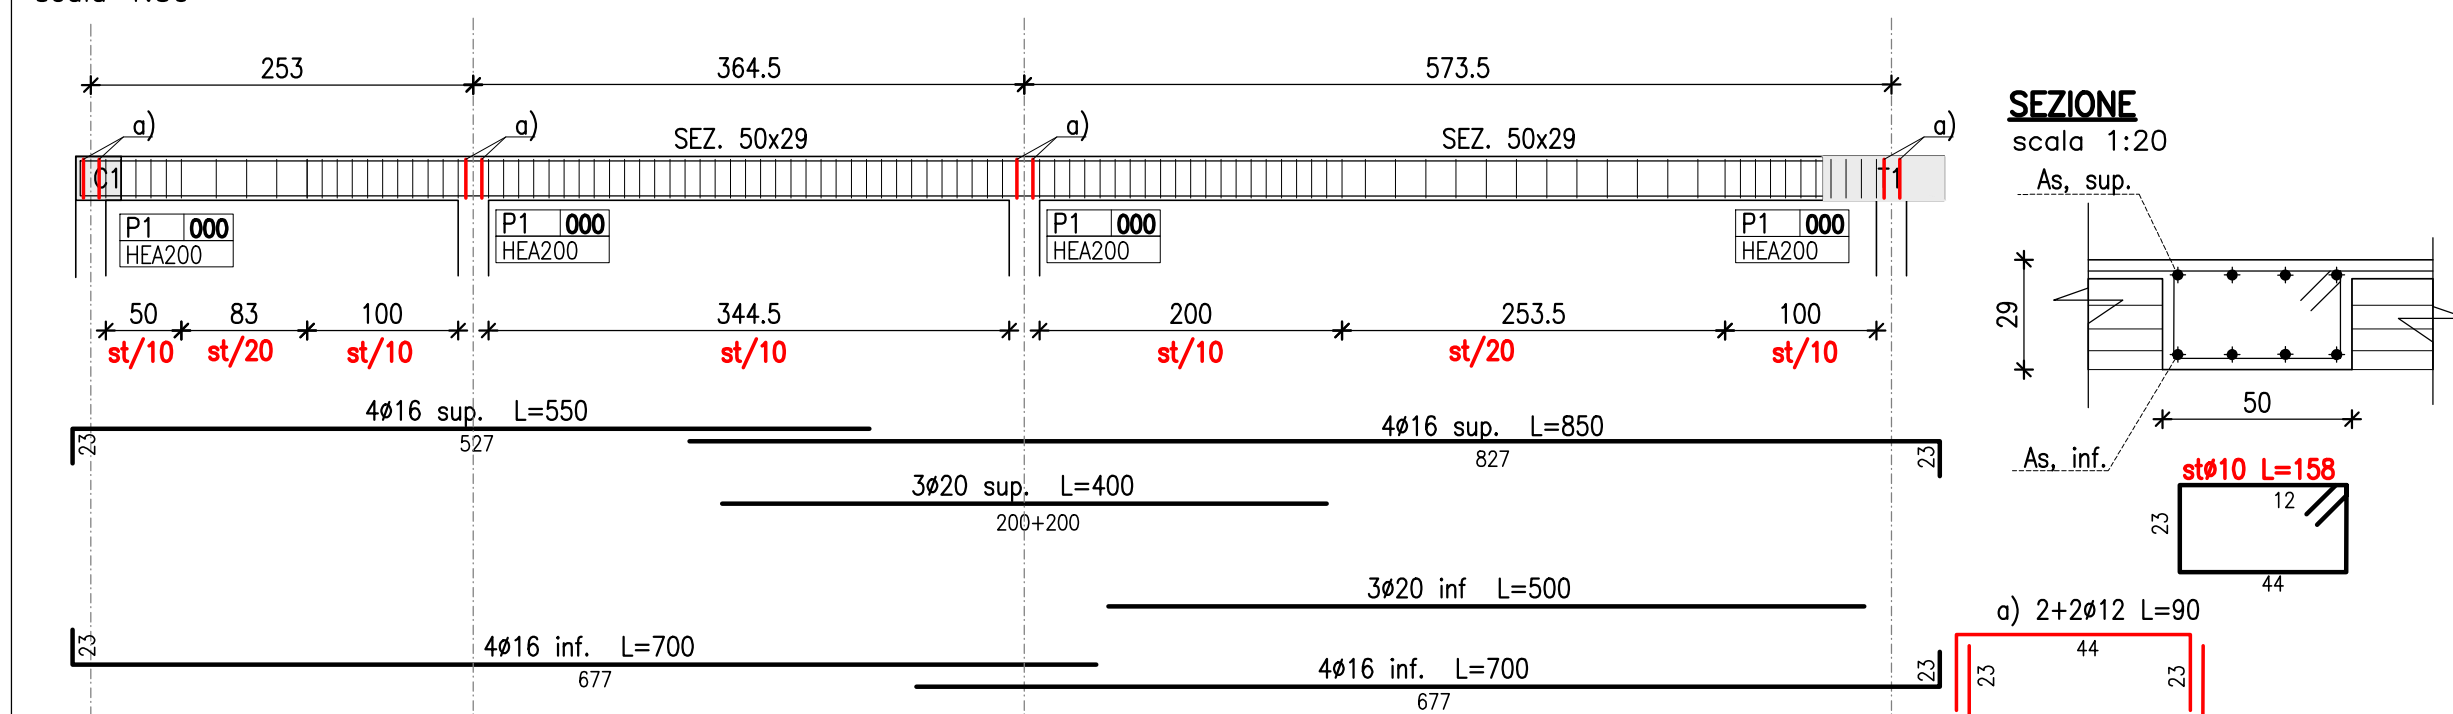

SEZIONE
scala 1:20

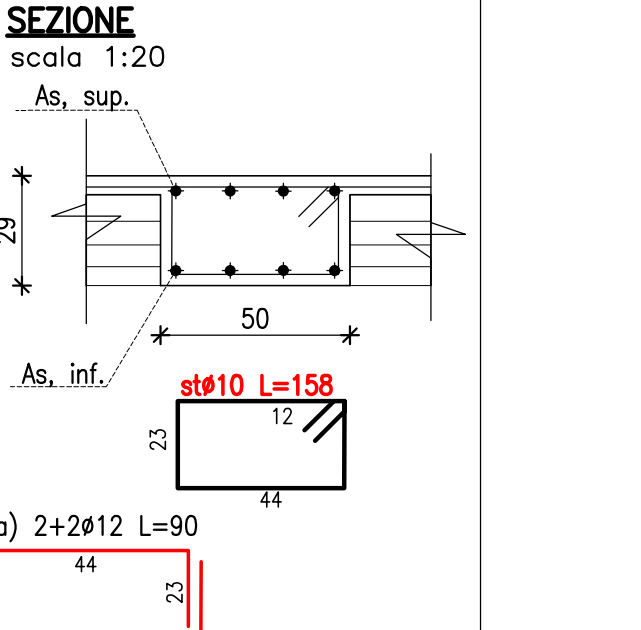

TAVOLE DI RIFERIMENTO			
S00			SPECIFICHE TECNICHE
S01			PIANTA TRACCIAMENTO
S02	*		PIANTA FONDAZIONI
	S02a		ARMATURA AGGIUNTIVA PLATEA
S03	*		PIANTA PRIMO IMPALCATO
	S03a		TRAVI PRIMO IMPALCATO
S04	*		PIANTA SECONDO IMPALCATO
S05	*		PIANTA COPERTURA
S06			ABACO PILASTRI
S07			VANO SCALA E ASCENSORE
*			ATTENZIONE!!! BLOCCO TAVOLE ELEMENTO STRUTTURALE

PER SPECIFICHE MATERIALI E DETTAGLI COSTRUTTIVI VEDERE TAVOLA ES-00-00 SPECIFICHE TECNICHE

GB&PARTNERS
SCIENZE PROGETTI IMMOBILIARI
Architettura, Ingegneria, Urbanistica
Via Salaria 100 - 00198 Roma
Tel. 06/49811111 - Fax 06/49811112
E-mail: gbpartners@gbpartners.it

STEN
STRUCTURAL ENGINEERING
Via Salaria 100 - 00198 Roma
Tel. 06/49811111 - Fax 06/49811112
E-mail: sten@sten.it

Progetto strutturale:
Ing. Alessandro Bertozzi
Piazza Alpini, 2
25039 Travagliato (BS)
Cell. 3890777193
E-mail: alessandro@bertozzingegneria.it

COMUNE DI COLOGNO MONZESE (MI)
AREA Ex TORRIANI ARAS 01
PROGETTO ESECUTIVO
Progetto Servizi Abitativi Pubblici di via Pergolesi

N° DATA DESCRIZIONE MOTIVAZIONE DELL'AGGIORNAMENTO STUDIO DIS.

00	22/05/2025	Prima emissione	STEN	ST
01	26/01/2026	Modifica architettonica 260118	STEN	ST

Progetto

PROGETTO ESECUTIVO

Servizi Abitativi Pubblici
Comune di Cologno Monzese(MI)

Proponente

Officine Mak S.r.l.
Corso Europa, 10
Milano 20122

Scala

1:50

Data

22/05/2025

Tipo tavola

ESECUTIVI

Serie

STRUTTURE

Titolo

TRAVI PRIMO IMPALCATO

Tavola nr.

E

S

03a

00

Progetto

PROGETTO ESECUTIVO

Servizi Abitativi Pubblici
Comune di Cologno Monzese(MI)

Proponente

Officine Mak S.r.l.
Corso Europa, 10
Milano 20122

Scala

1:50

Data

22/05/2025

Tipo tavola

ESECUTIVI

Serie

STRUTTURE

Titolo

TRAVI PRIMO IMPALCATO

Tavola nr.

E

S

03a

00

Documentazione di proprietà della Società G.B. & Partners S.r.l. E' vietata la riproduzione. Tutti i diritti sono riservati.

Orientamento

N