


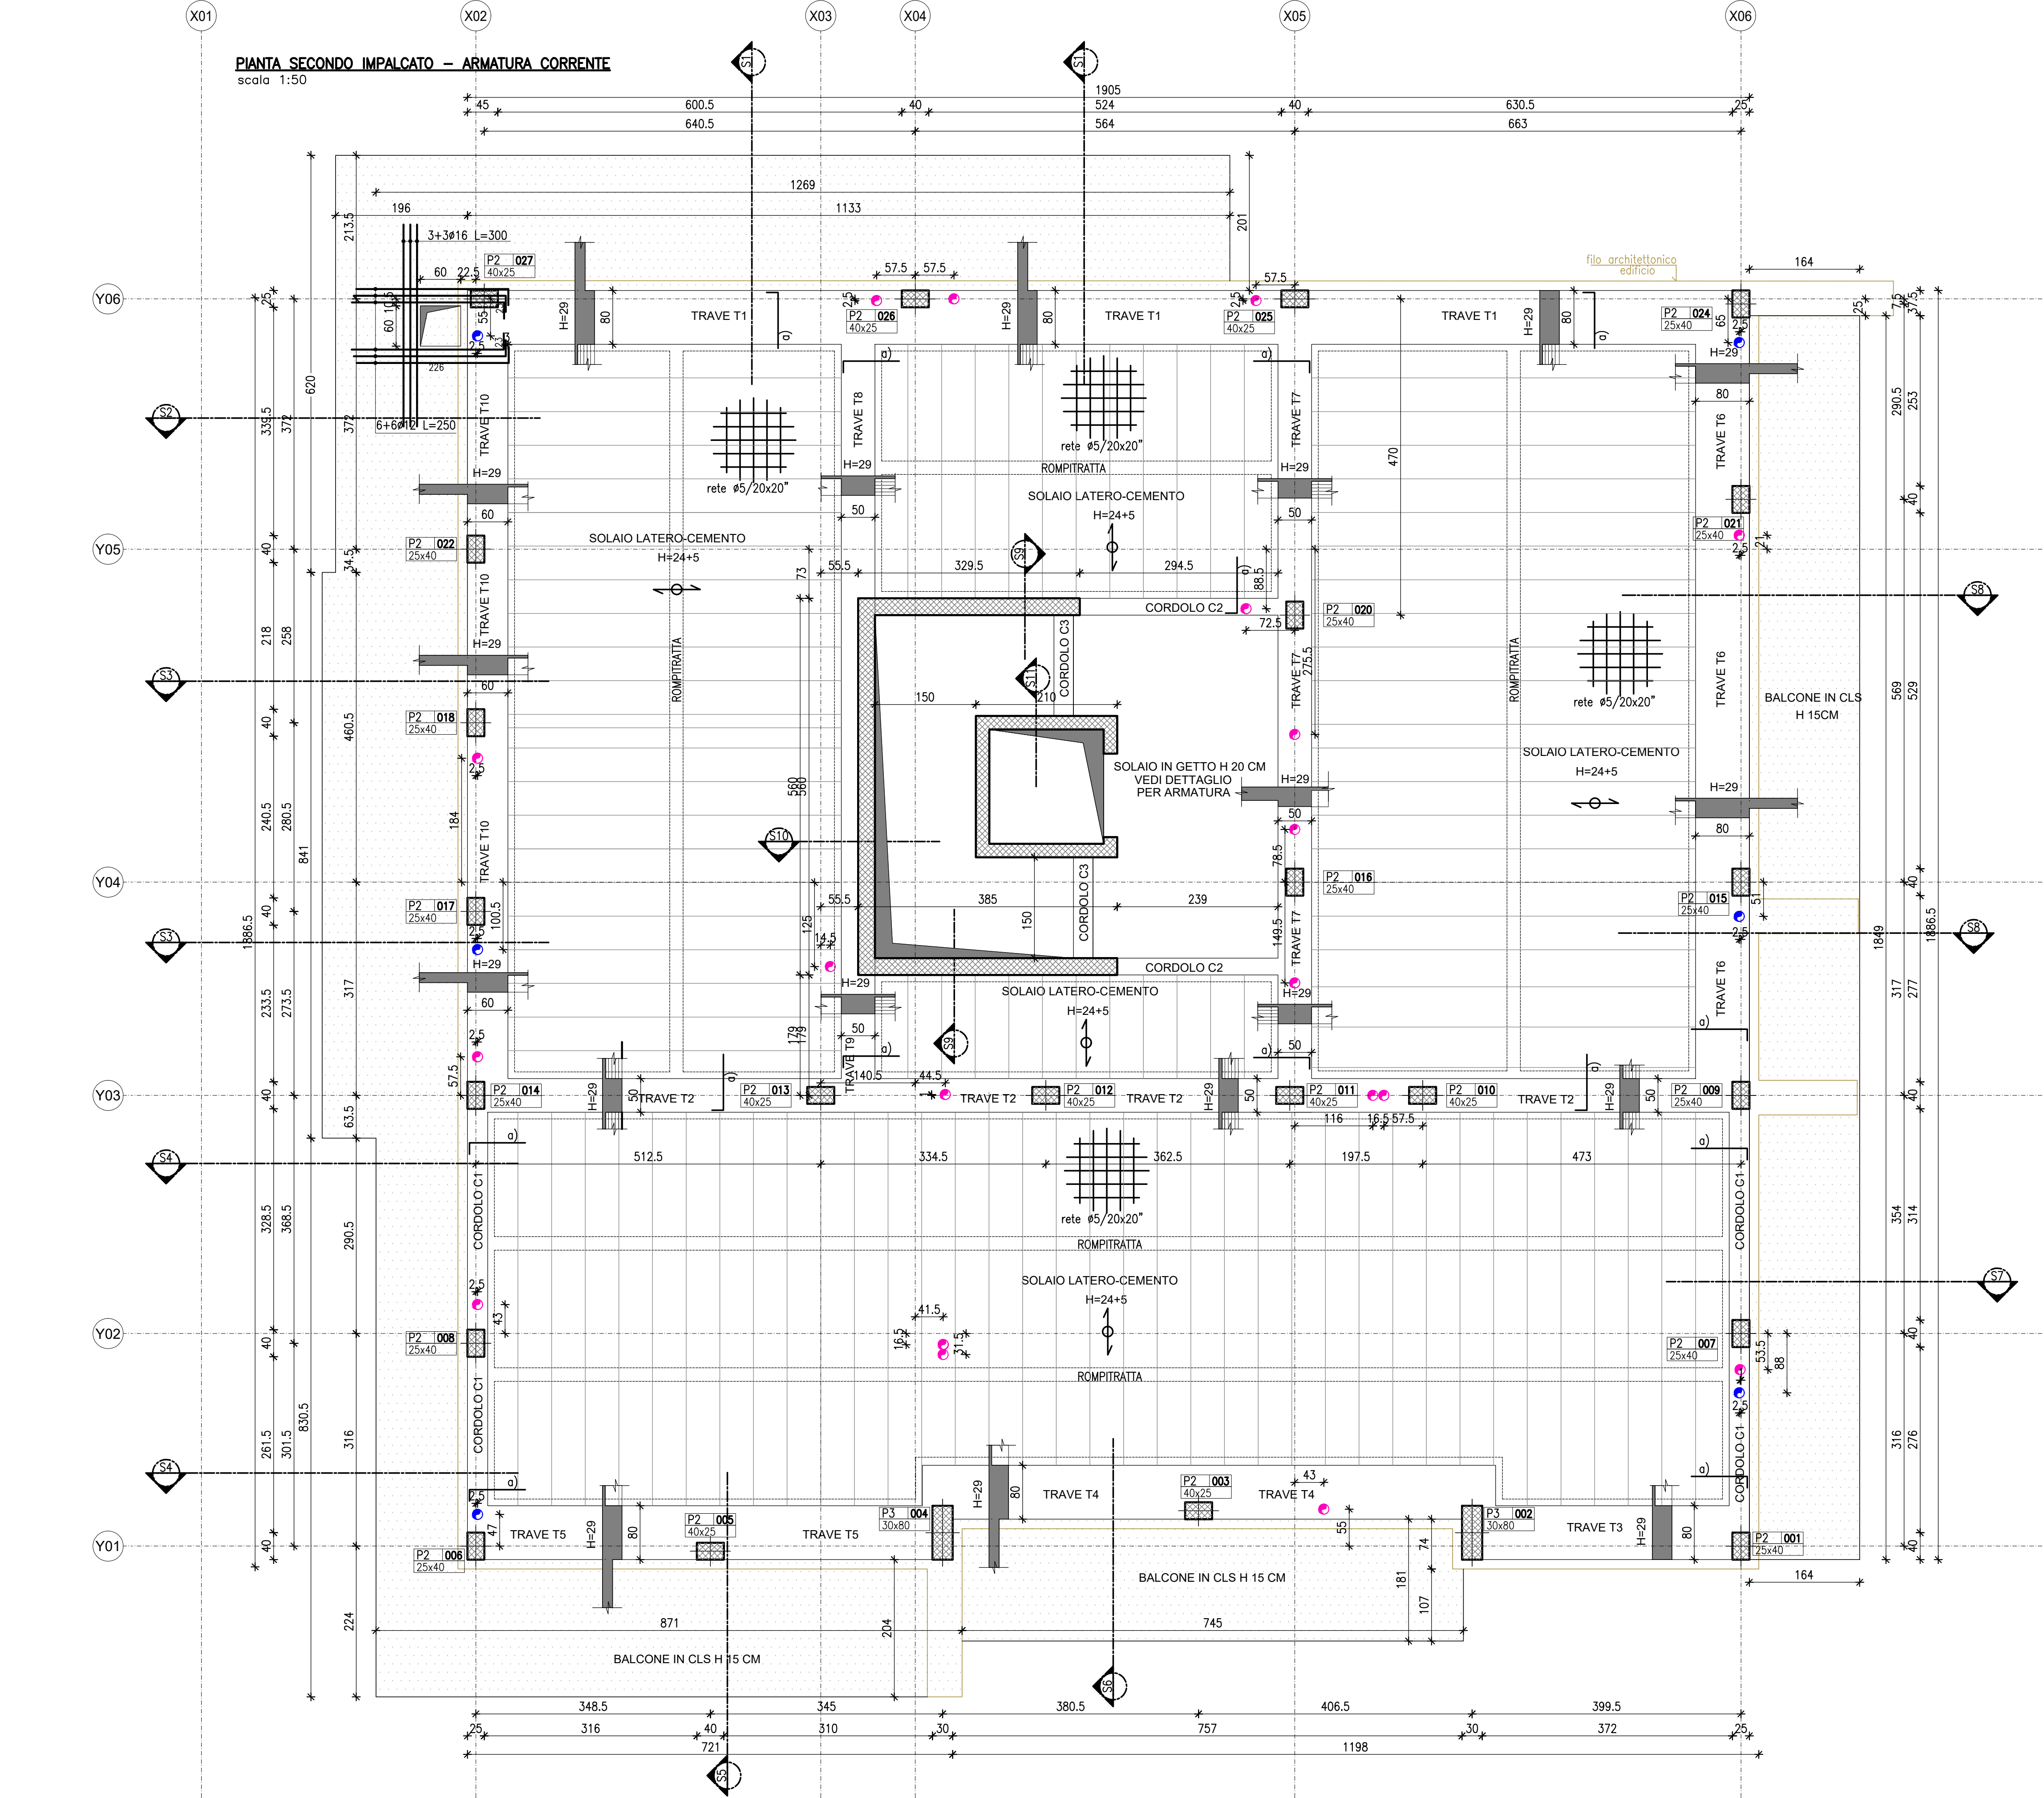

TAVOLE DI RIFERIMENTO		
S00		SPECIFICHE TECNICHE
S01		PIANTA TRACCIAMENTO
S02	*	PIANTA FONDAZIONI
S03	*	PIANTA PRIMO IMPALCATO
S04	*	PIANTA SECONDO IMPALCATO
	S04a	TRAVI SECONDO IMPALCATO
S05	*	PIANTA COPERTURA
S06		ABACO PILASTRI
S07		VANO SCALA E ASCENSORE
*		ATTENZIONE!!! BLOCCO TAVOLE ELEMENTO STRUTTURALE

CARICHI SOLAIO S1

PESO PROPRIO SOLAIO 24+5	360 kg/mq
CARICO PERMANENTE NON STRUTTURALE INTERNO	300 kg/mq
CARICO VARIABILE	200 kg/mq

CARICHI BALCONI

PESO PROPRIO	375 kg/mq
CARICO PERMANENTE NON STRUTTURALE	200 kg/mq
CARICO VARIABILE	400 kg/mq

CARICHI GRONDA

















PESO PROPRIO	375 kg/mq
CARICO PERMANENTE NON STRUTTURALE	100 kg/mq
CARICO VARIABILE	120 kg/mq

PER SPECIFICHE MATERIALI E DETTAGLI COSTRUTTIVI VEDERE TAVOLA ES-00-00, SPECIFICHE TECNICHE

ATTENZIONE! PER CORDOLO C3 SCALA VEDERE TAV.ES-07-00, VANO SCALA E ASCENSORE


ATTENZIONE! POSIZIONARE AI LATI DELLE FOROMETRIE NELLE TRAVI DUE STAFFE ACCOPIATE

COLONNA
Ø150
PIUVALE
Ø150

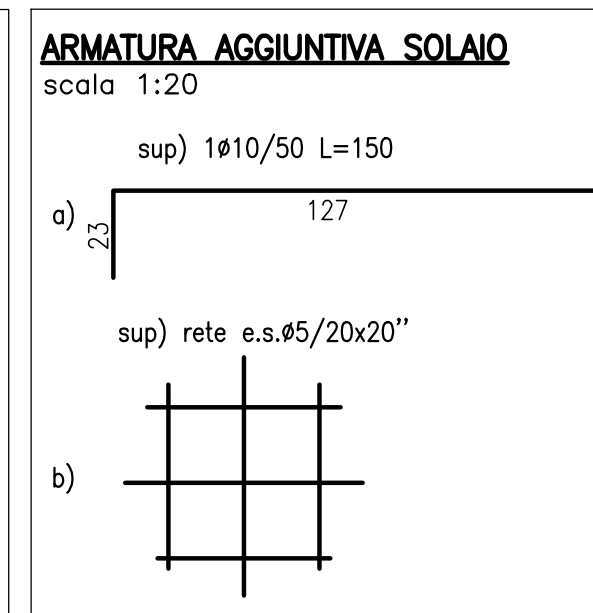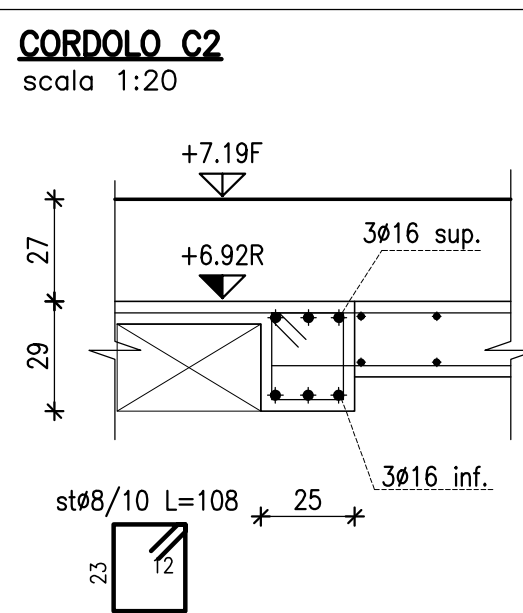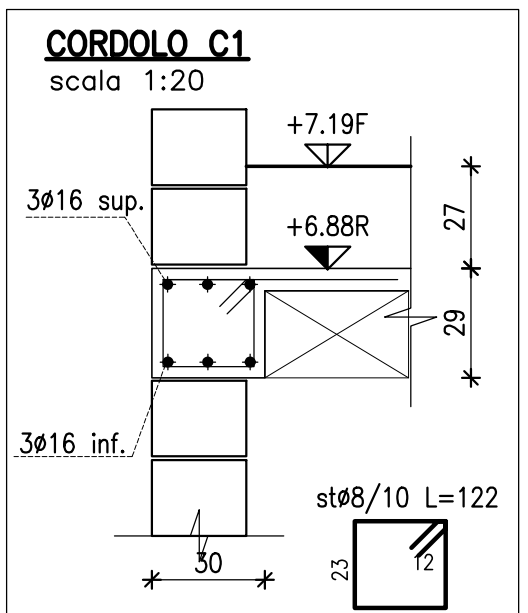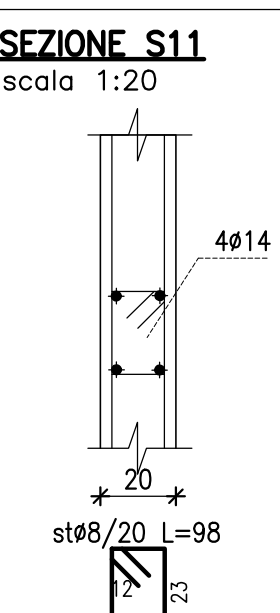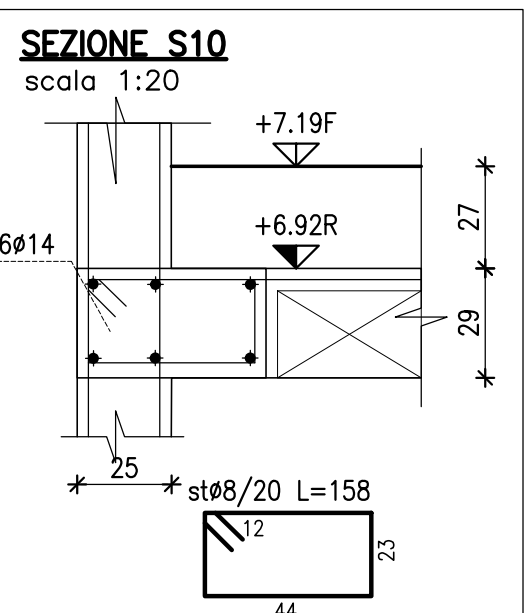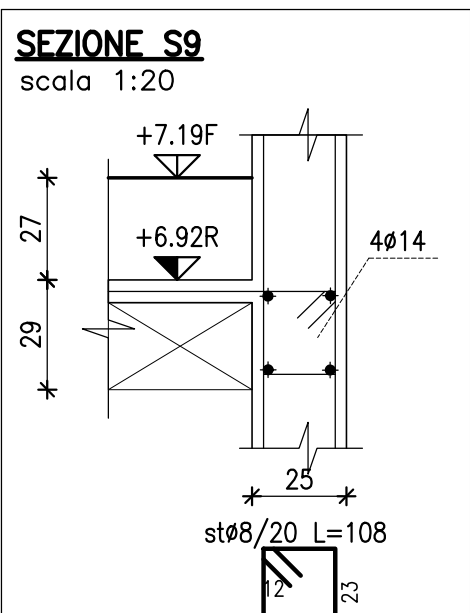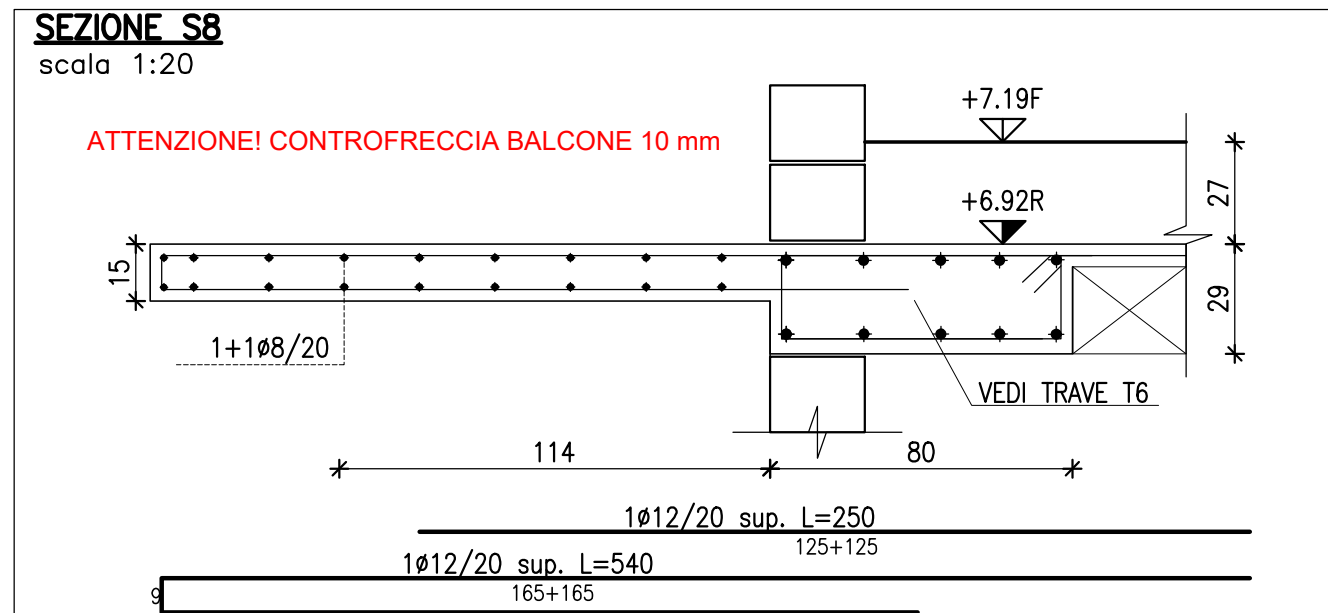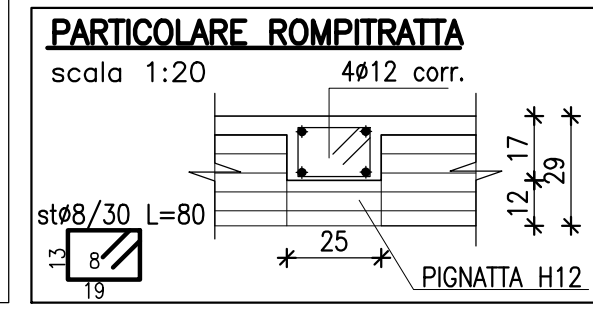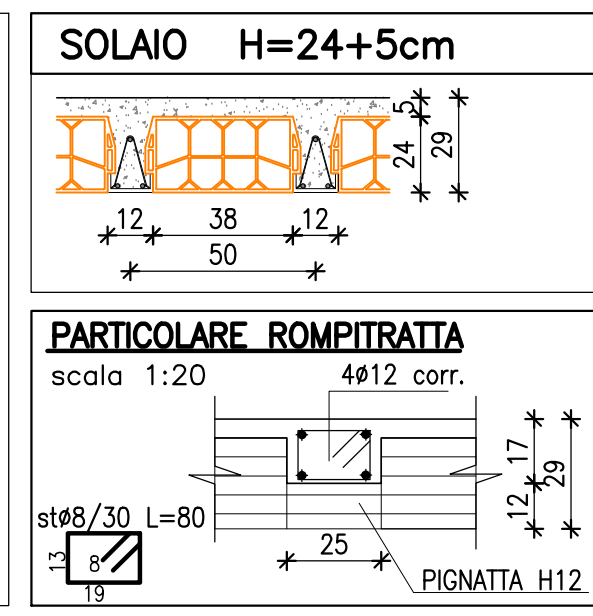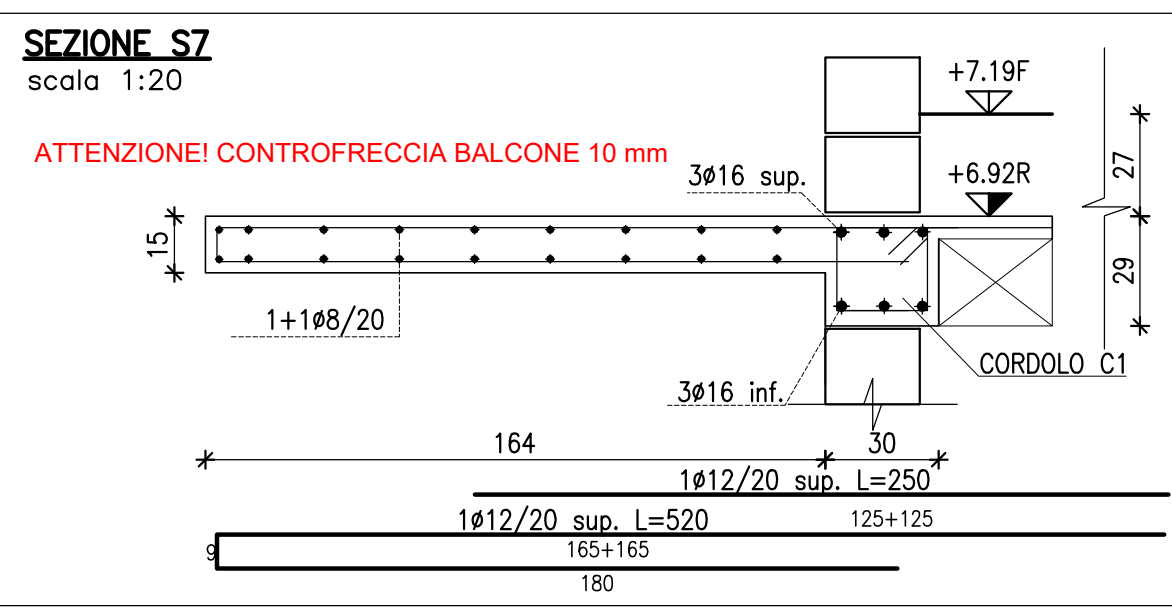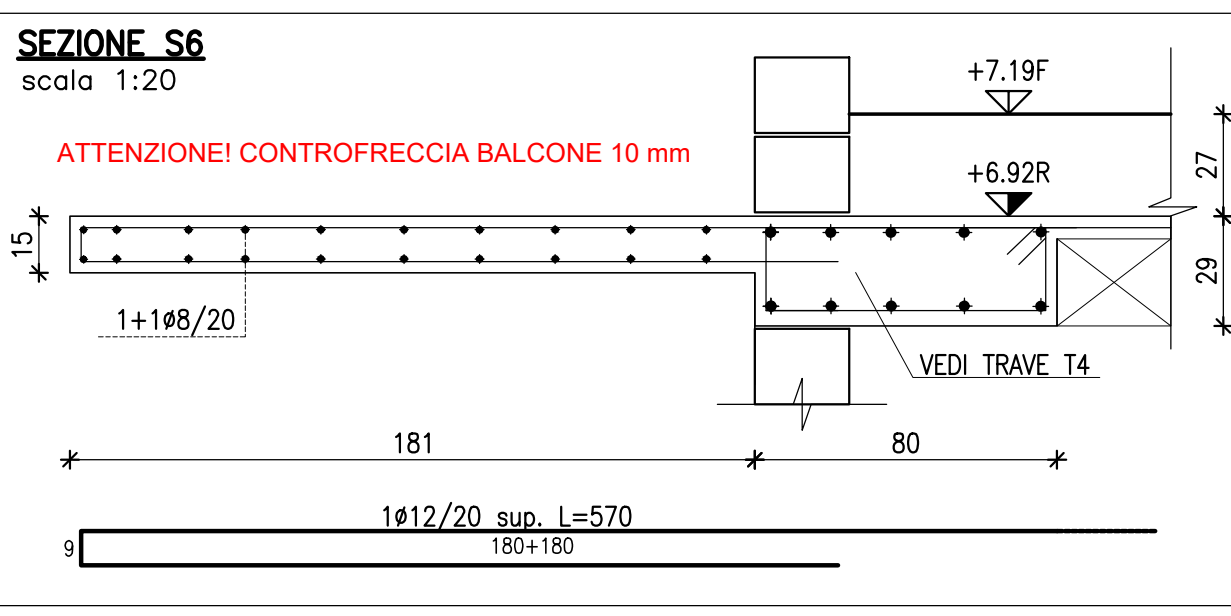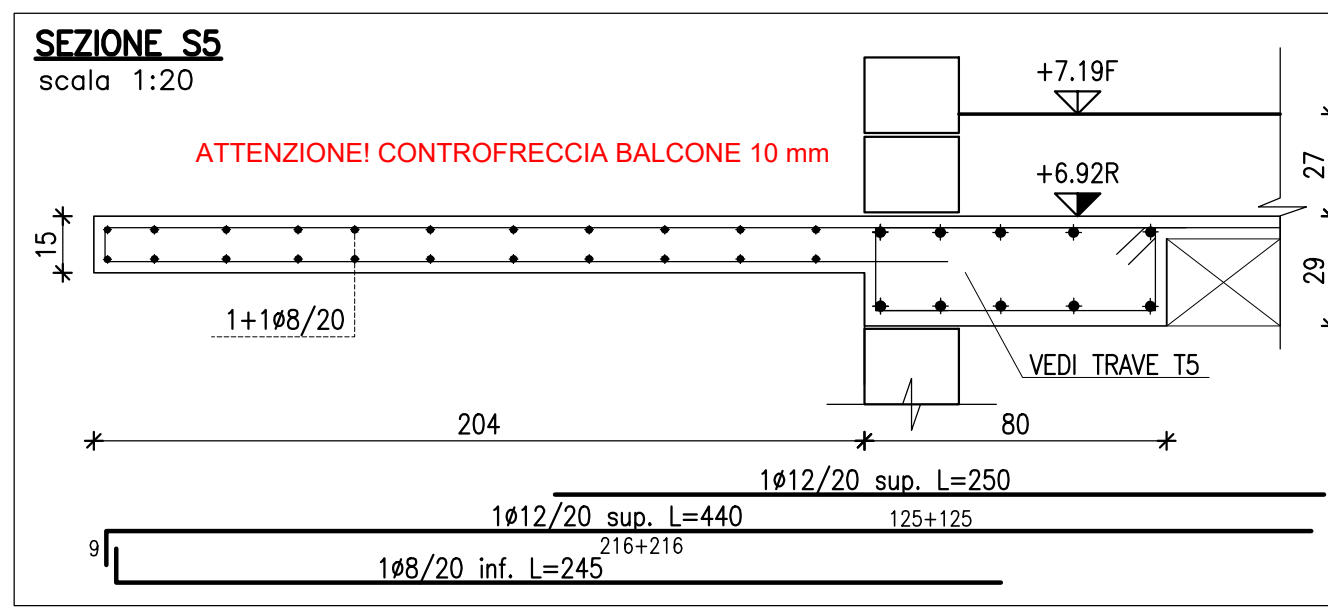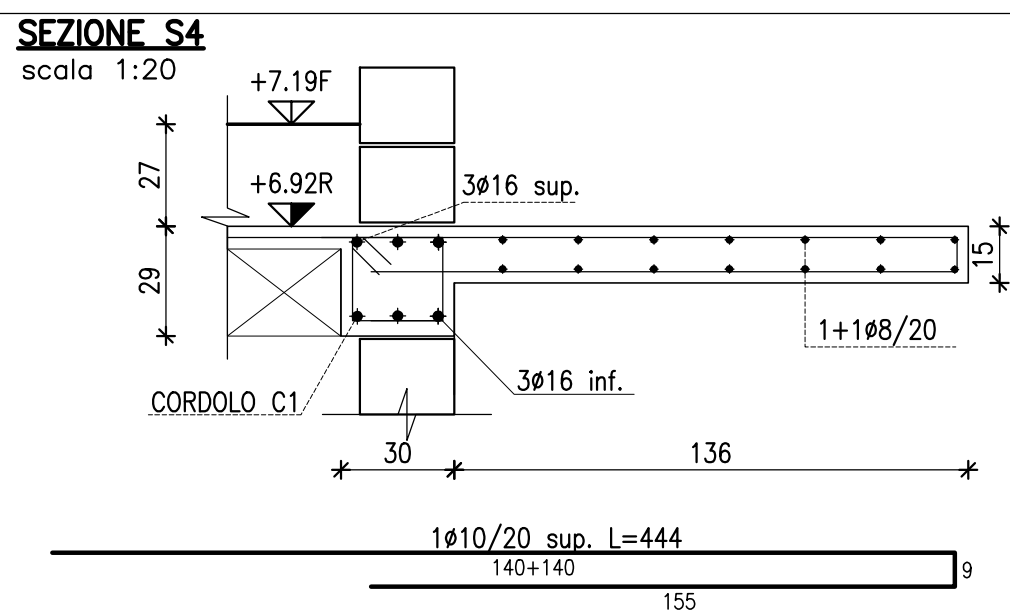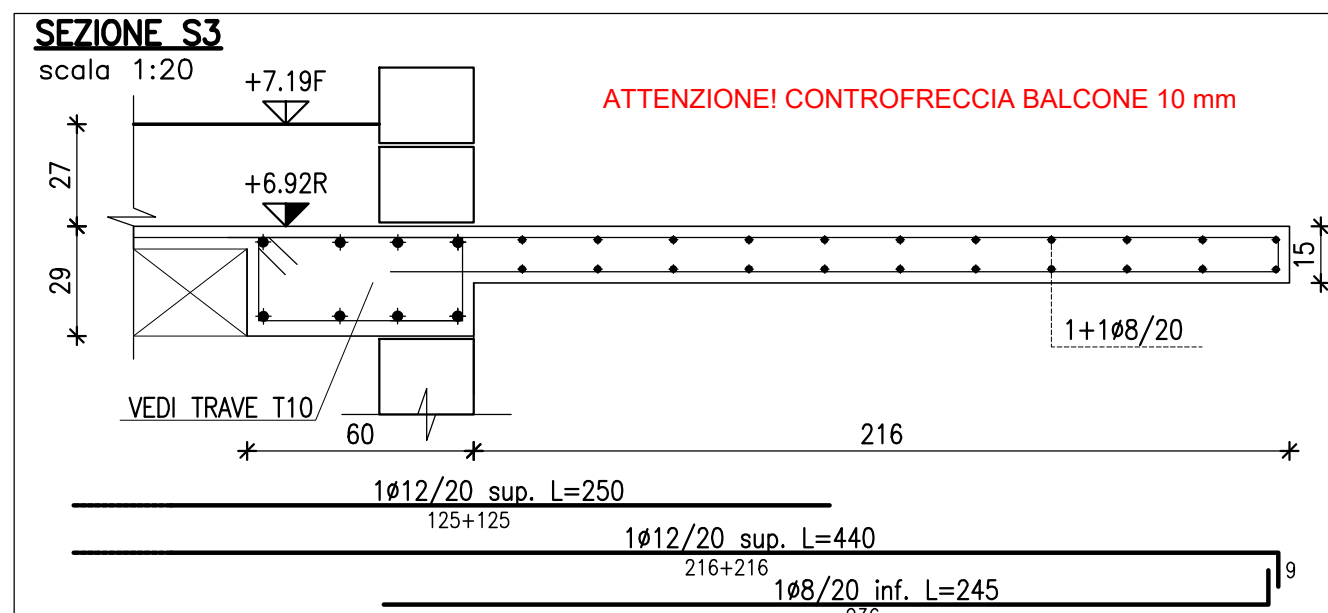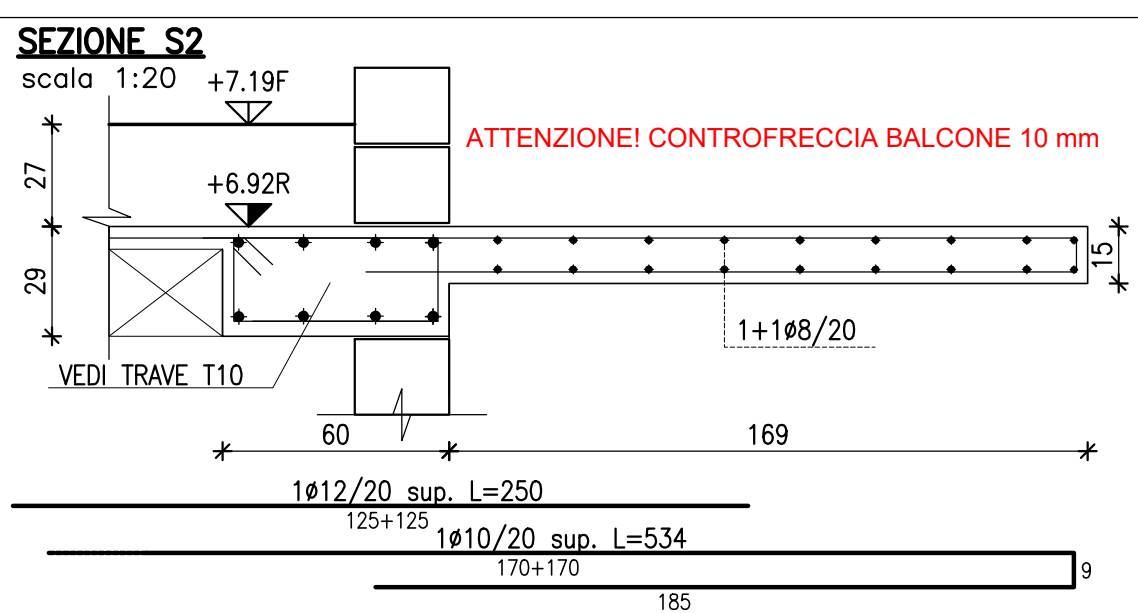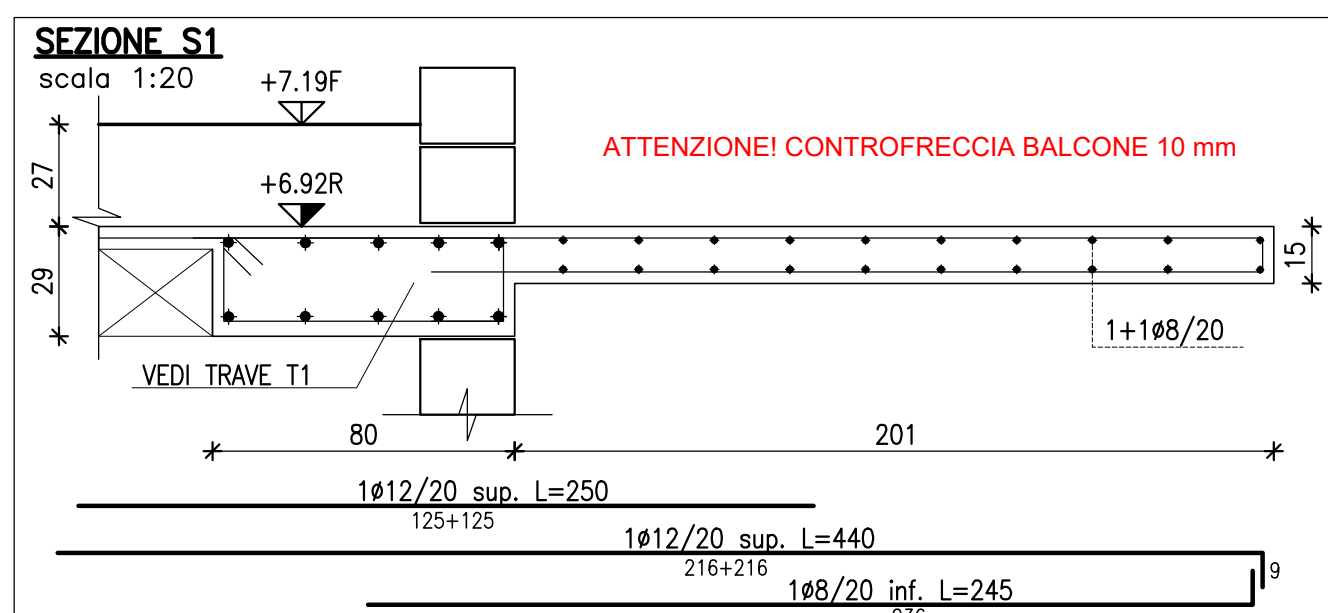

STRALCIO PIASTRA SECONDO IMPALCATO

scala 1:50

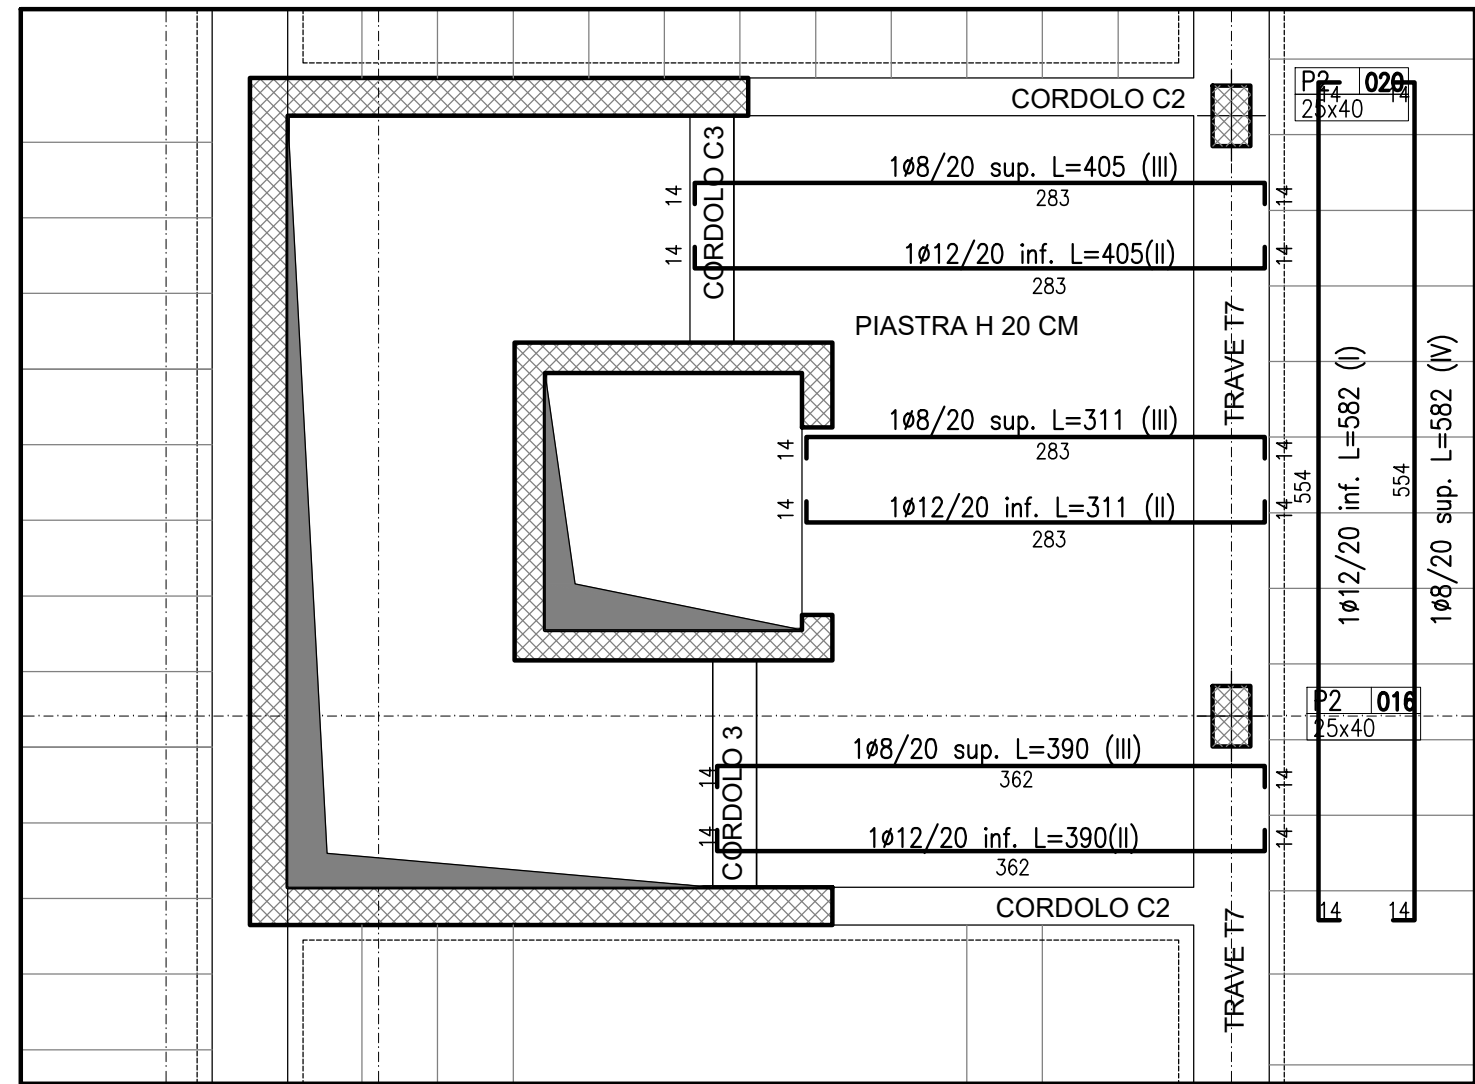

GB&PARTNERS
INGEGNERIA E PROGETTAZIONE
Piazzale Alpi, 2
25039 Travagliato (BS)
Cell. 3880777133
E-mail: alessandra@bertozzingeria.it

STEN
STRUCTURAL
INGEGNERIA

Progetto strutturale:
Ing. Alessandro Bertozzi
Piazzale Alpi, 2
25039 Travagliato (BS)
Cell. 3880777133
E-mail: alessandra@bertozzingeria.it

COMUNE DI COLOGNO MONZESE (MI)
AREA Ex TORRIANI ARAS 01
PROGETTO ESECUTIVO
Progetto Servizi Abitativi Pubblici di via Pergolesi

Il Progettista
Cologno Monzese
Gianpiero Bianchi

N°	DATA	DESCRIZIONE MOTIVAZIONE DELL'AGGIORNAMENTO	STUDIO	DIS.
00	22/05/2025	Prima emissione	STEN	ST
01	29/05/2025	Revisione generale	STEN	ST
02	09/06/2025	Forometrie	STEN	ST
03	26/01/2026	Aggiornamento architettonico 260118	STEN	ST
04	29/01/2026	Aggiornamento architettonico 260128	STEN	ST
05	05/02/2026	Modifica vano scala	STEN	ST

Il Proponente

Progetto
PROGETTO ESECUTIVO

Proponente
Officine Mak S.r.l.
Corso Europa, 10
Milano 20122

Scala
1:50

Servizi Abitativi Pubblici
Comune di Cologno Monzese(MI)

Data
05/02/2026

Tipo tavola
ESECUTIVI

Serie
STRUTTURE

Titolo
PIANTA SECONDO IMPALCATO

Tavola nr.
Tipo
Tavola
Sigla /
Serie
Numero /
Variante
Agg.

E
S
04
05

