
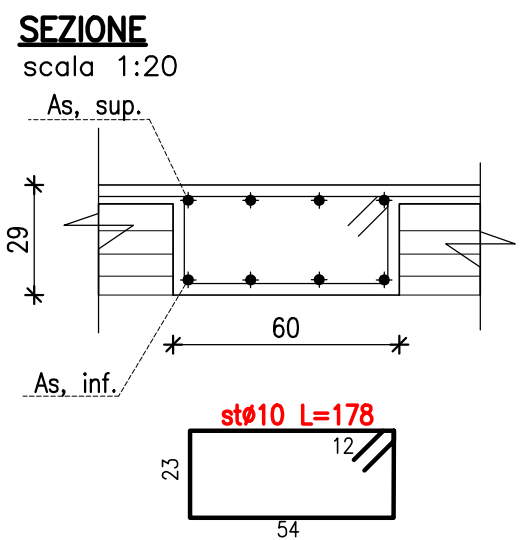
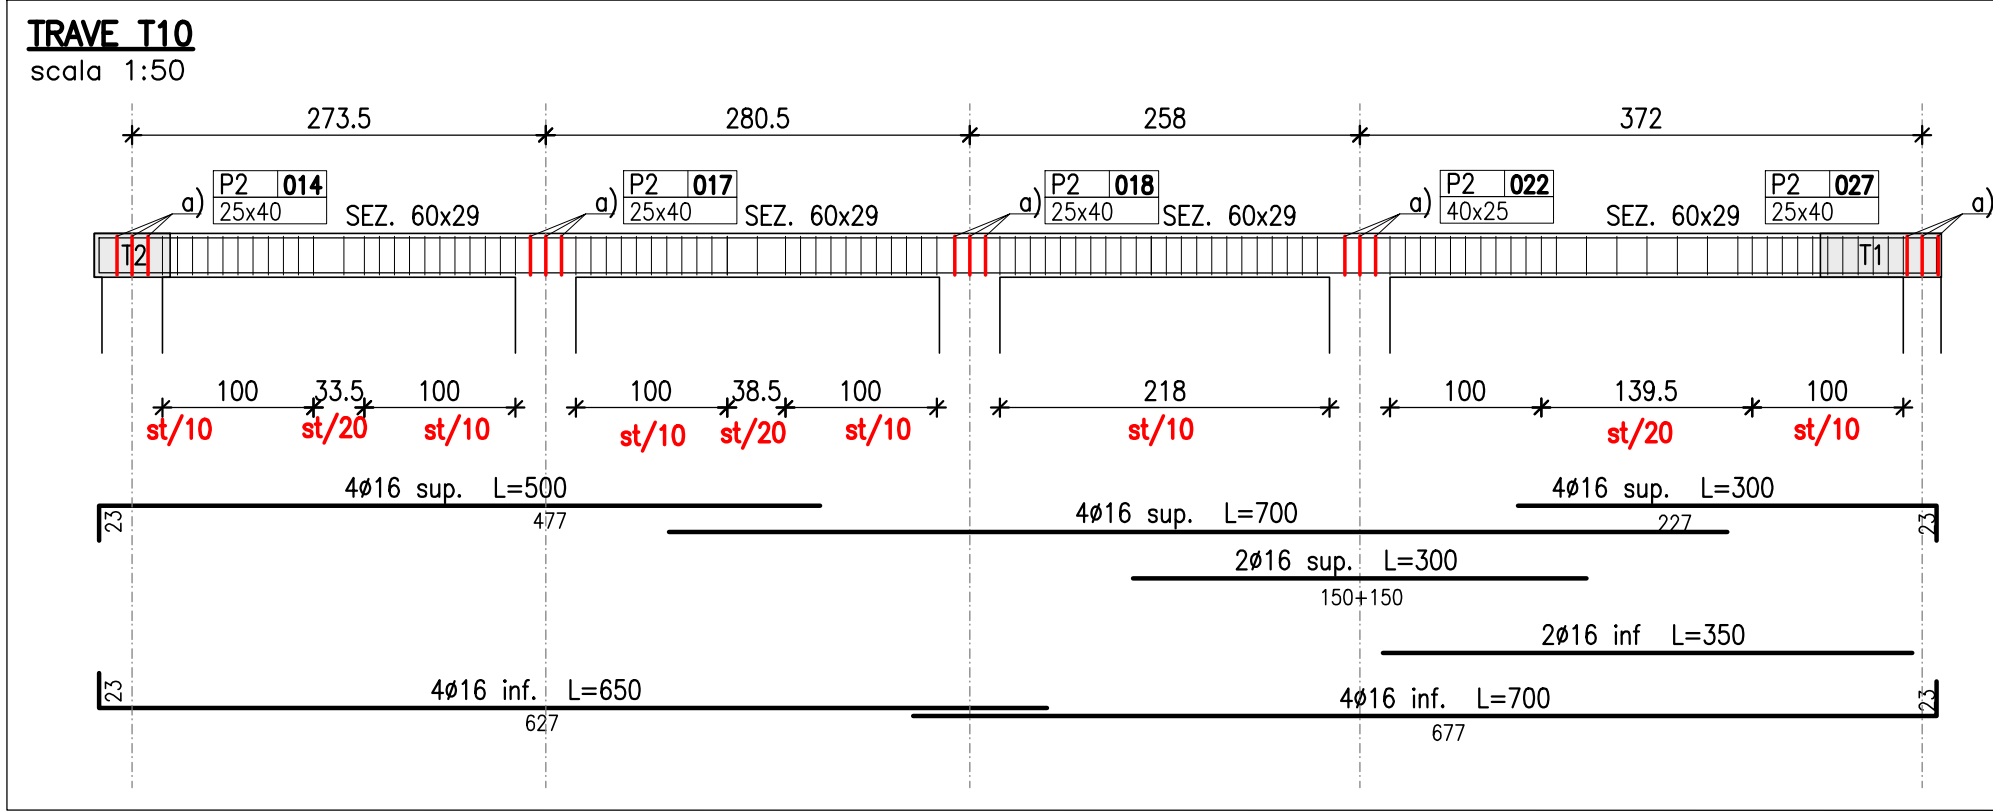
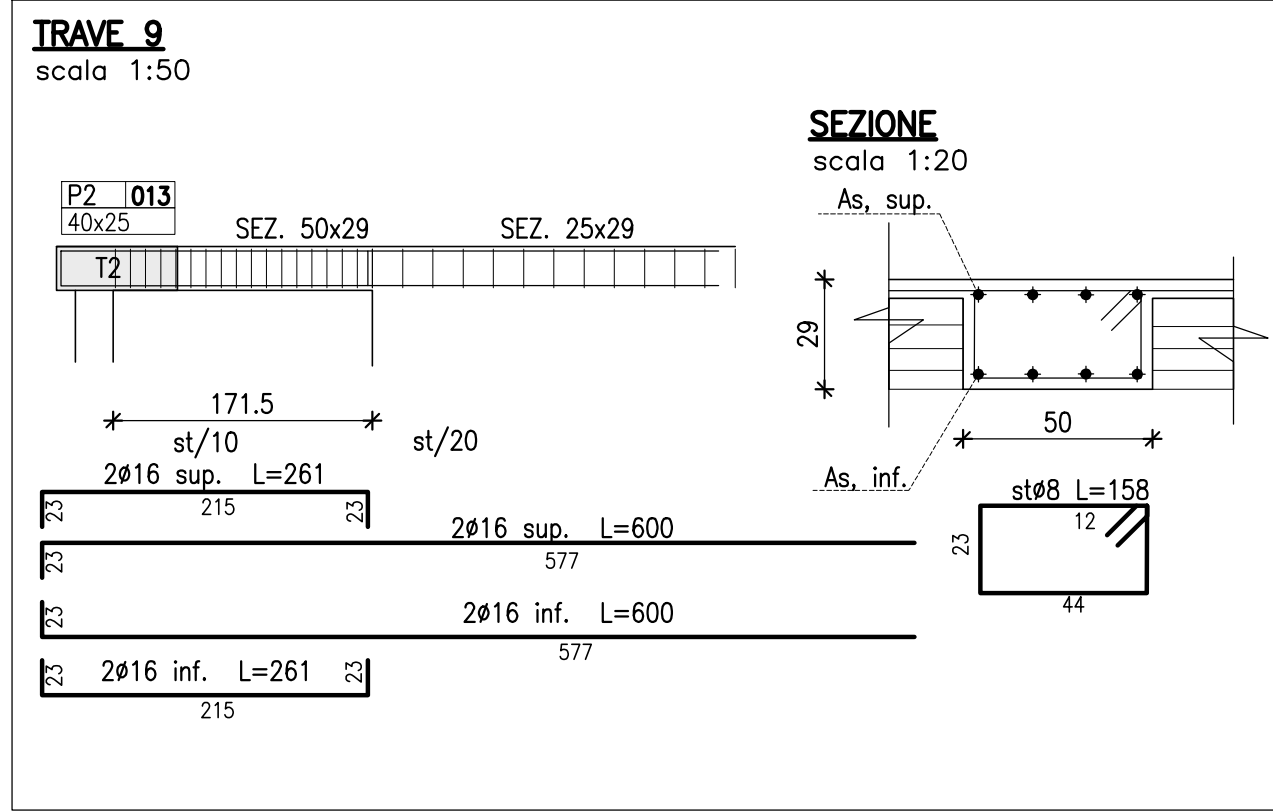
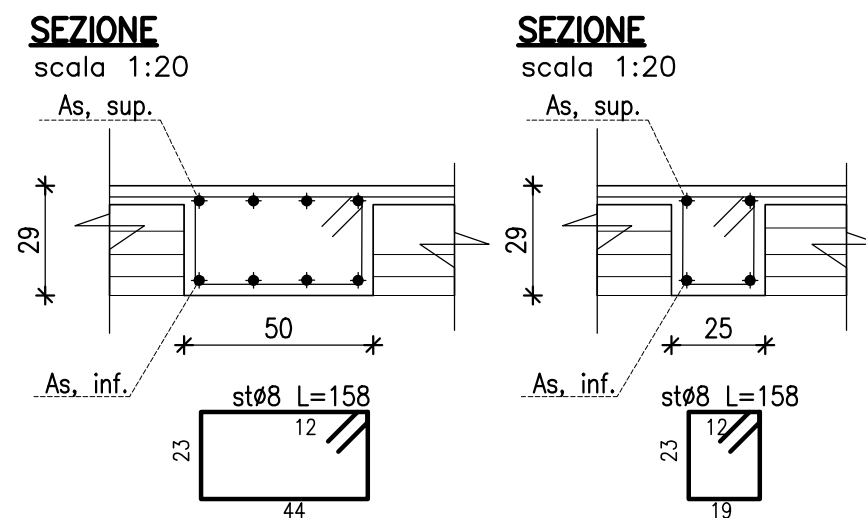
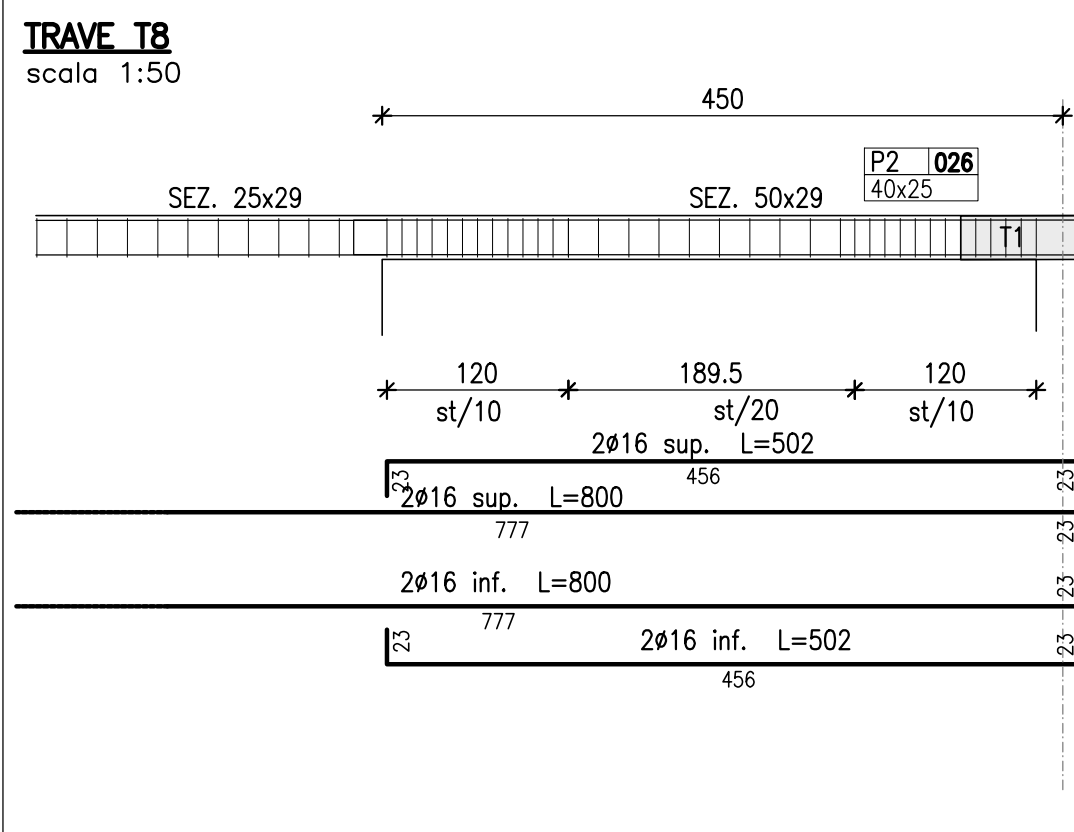
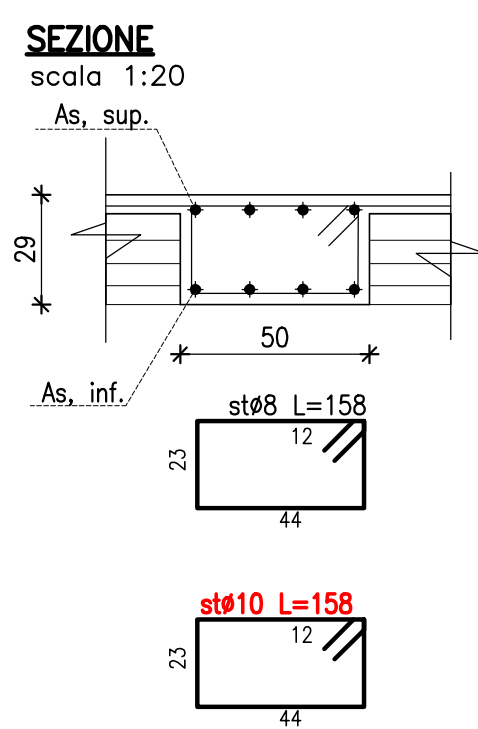
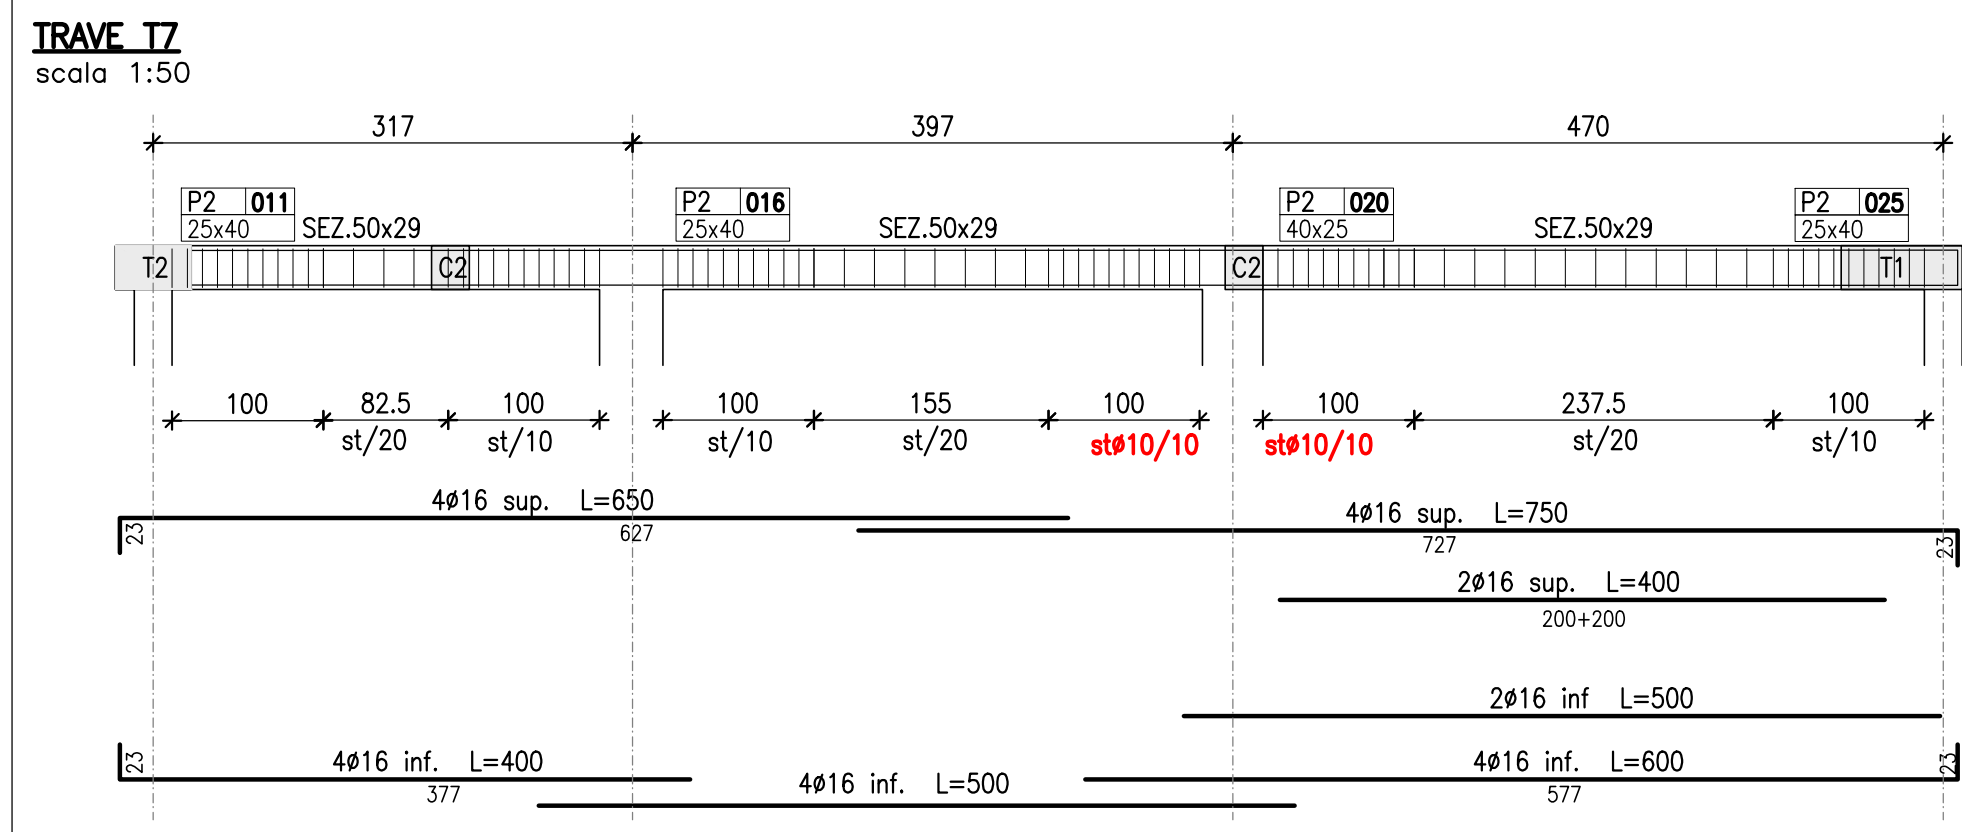
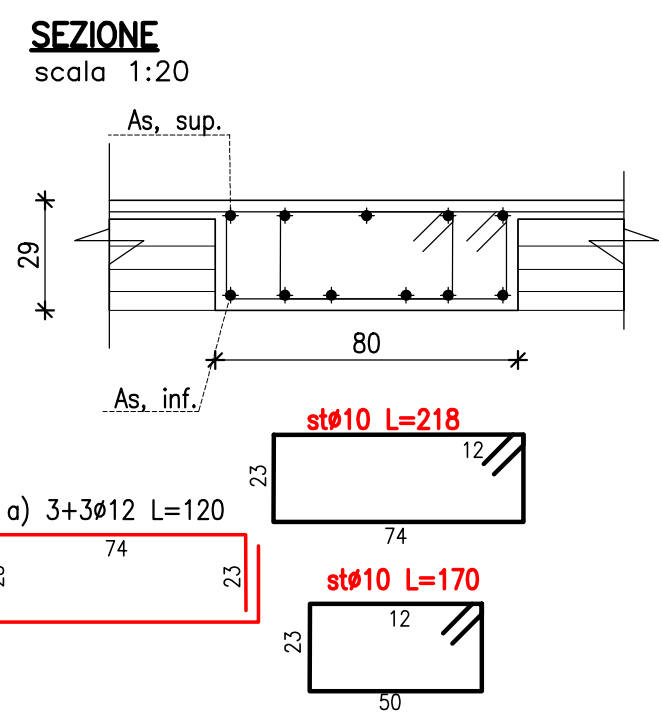
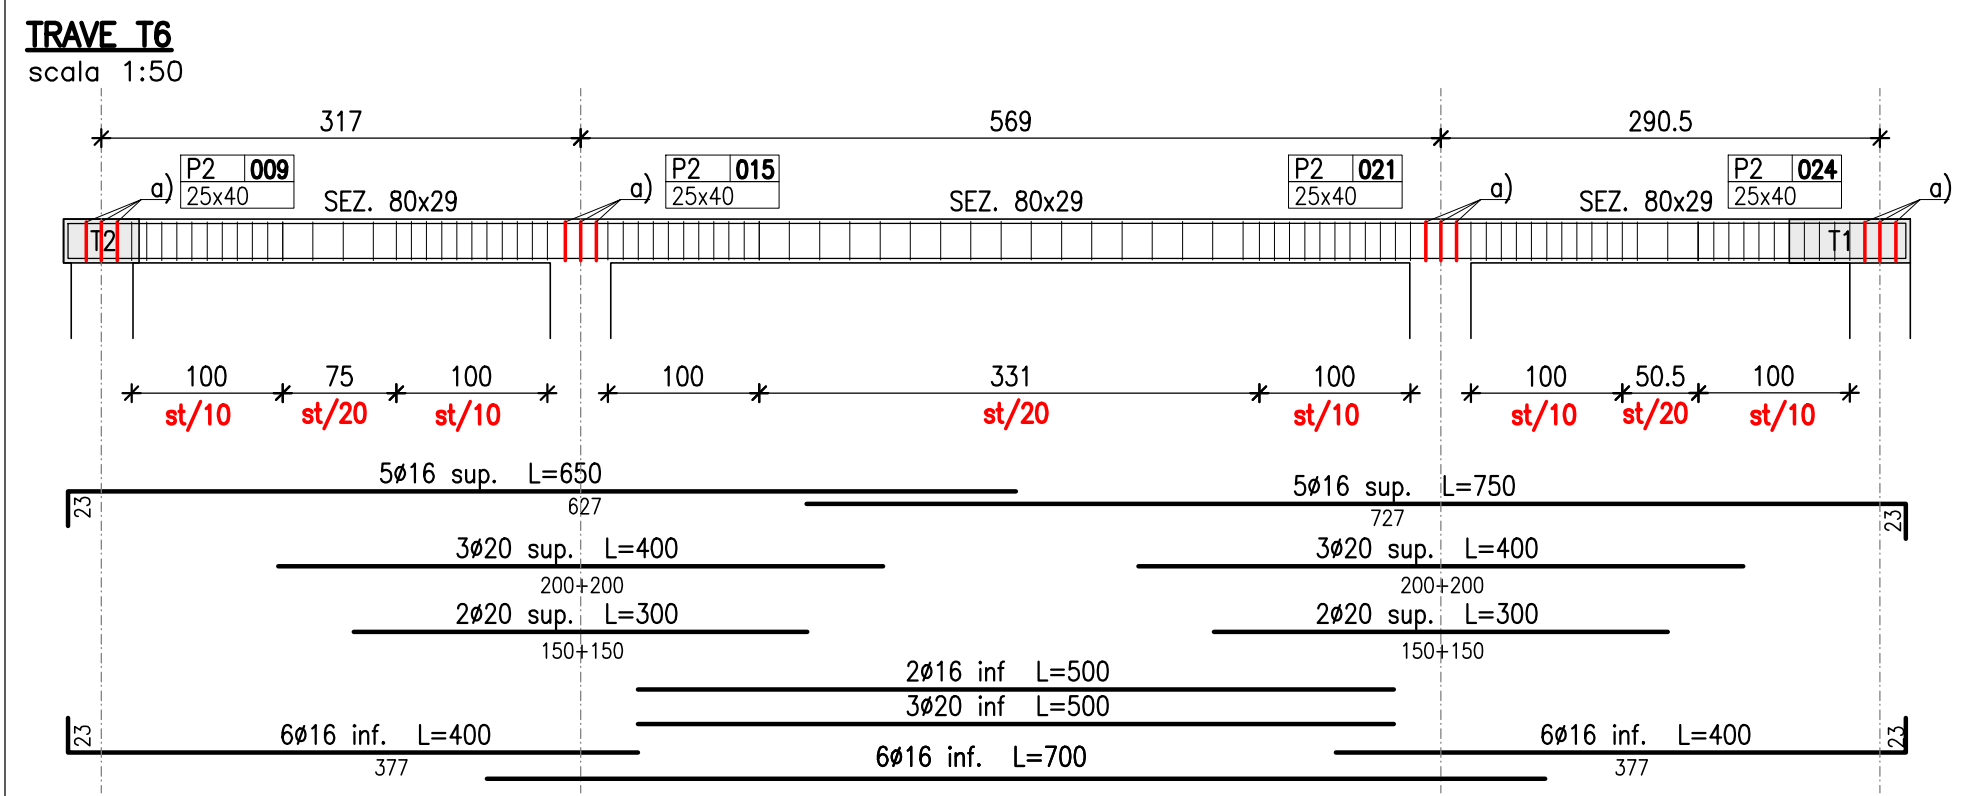
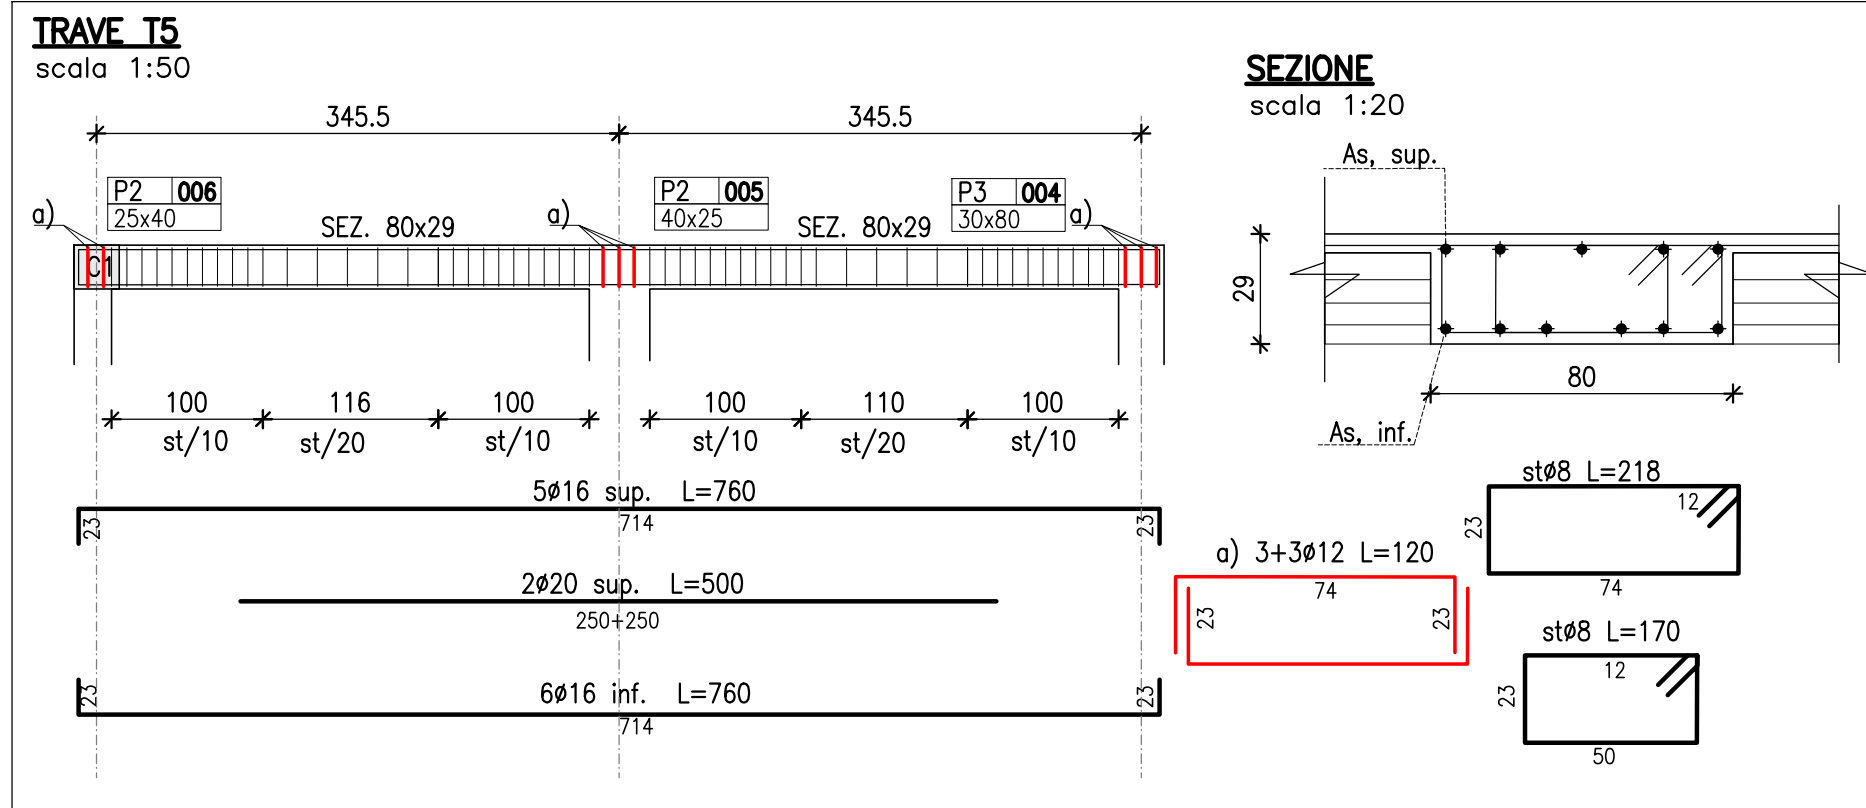
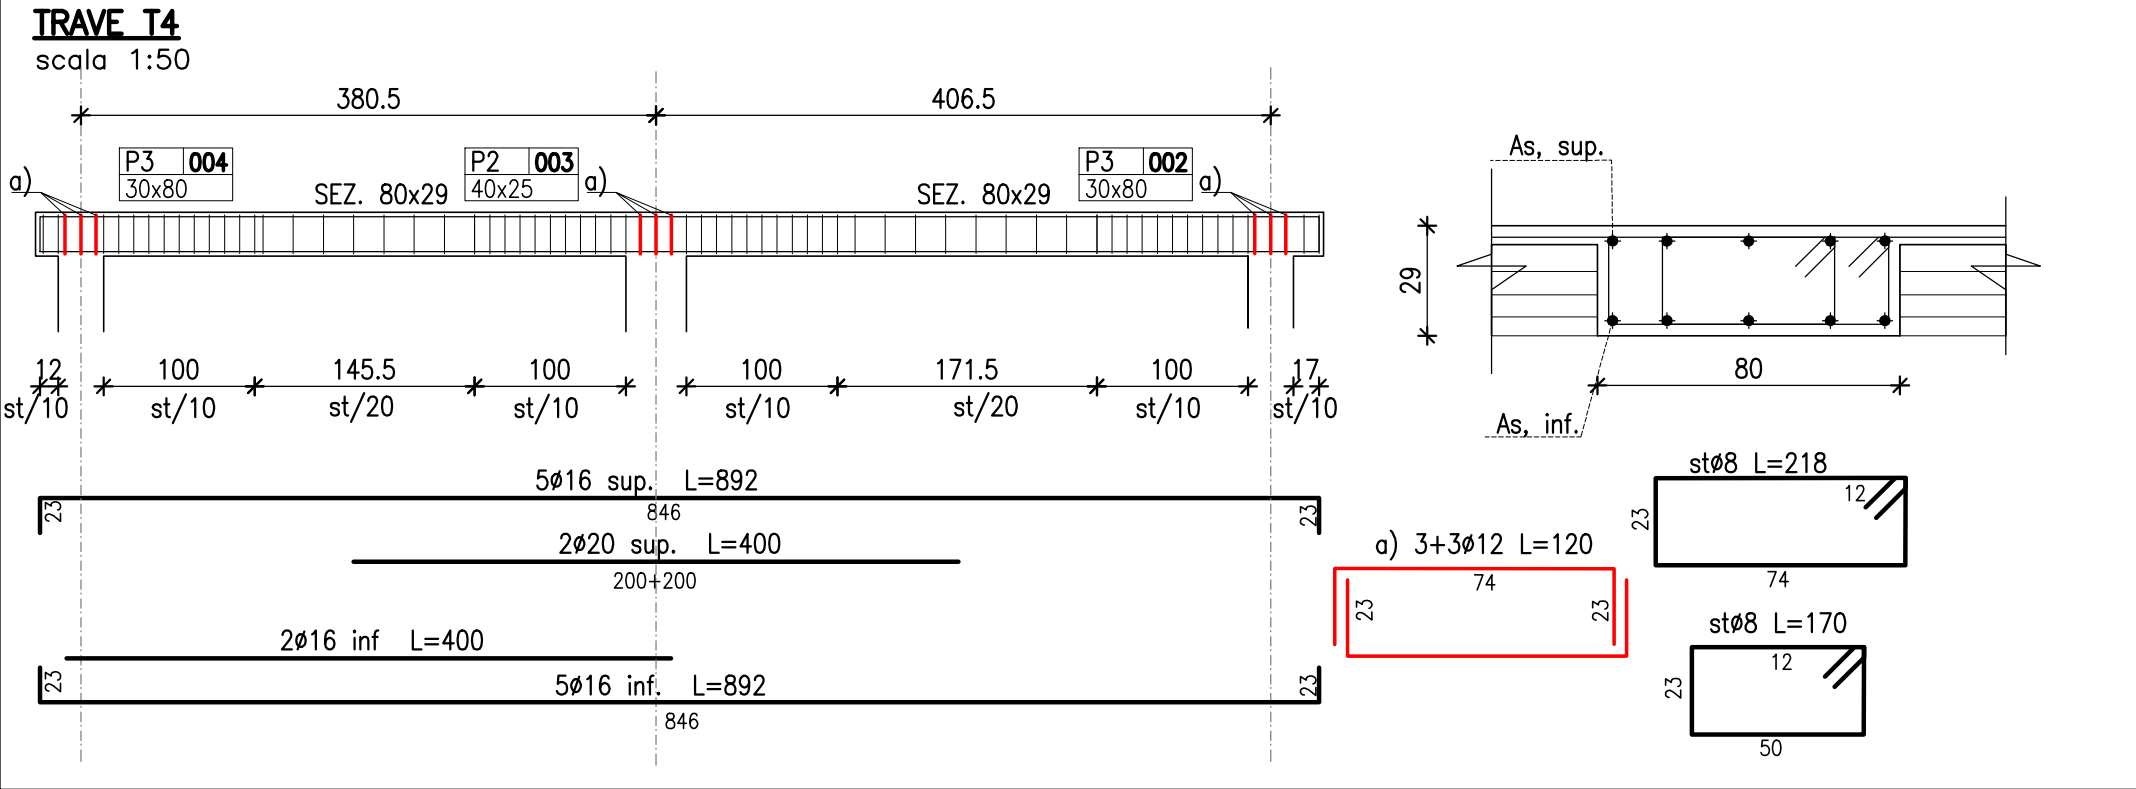
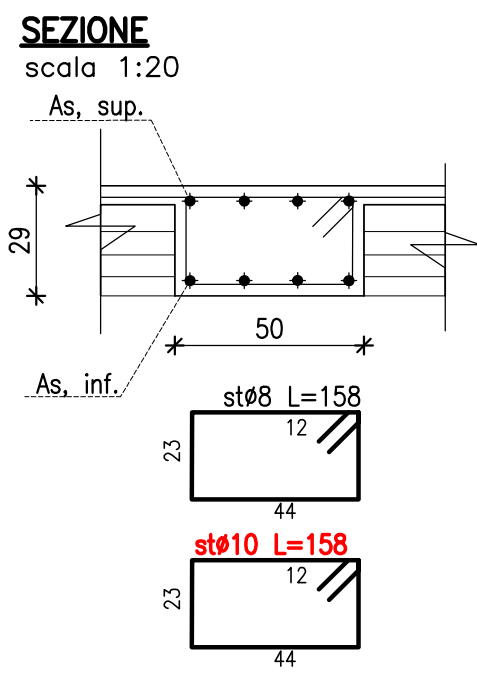
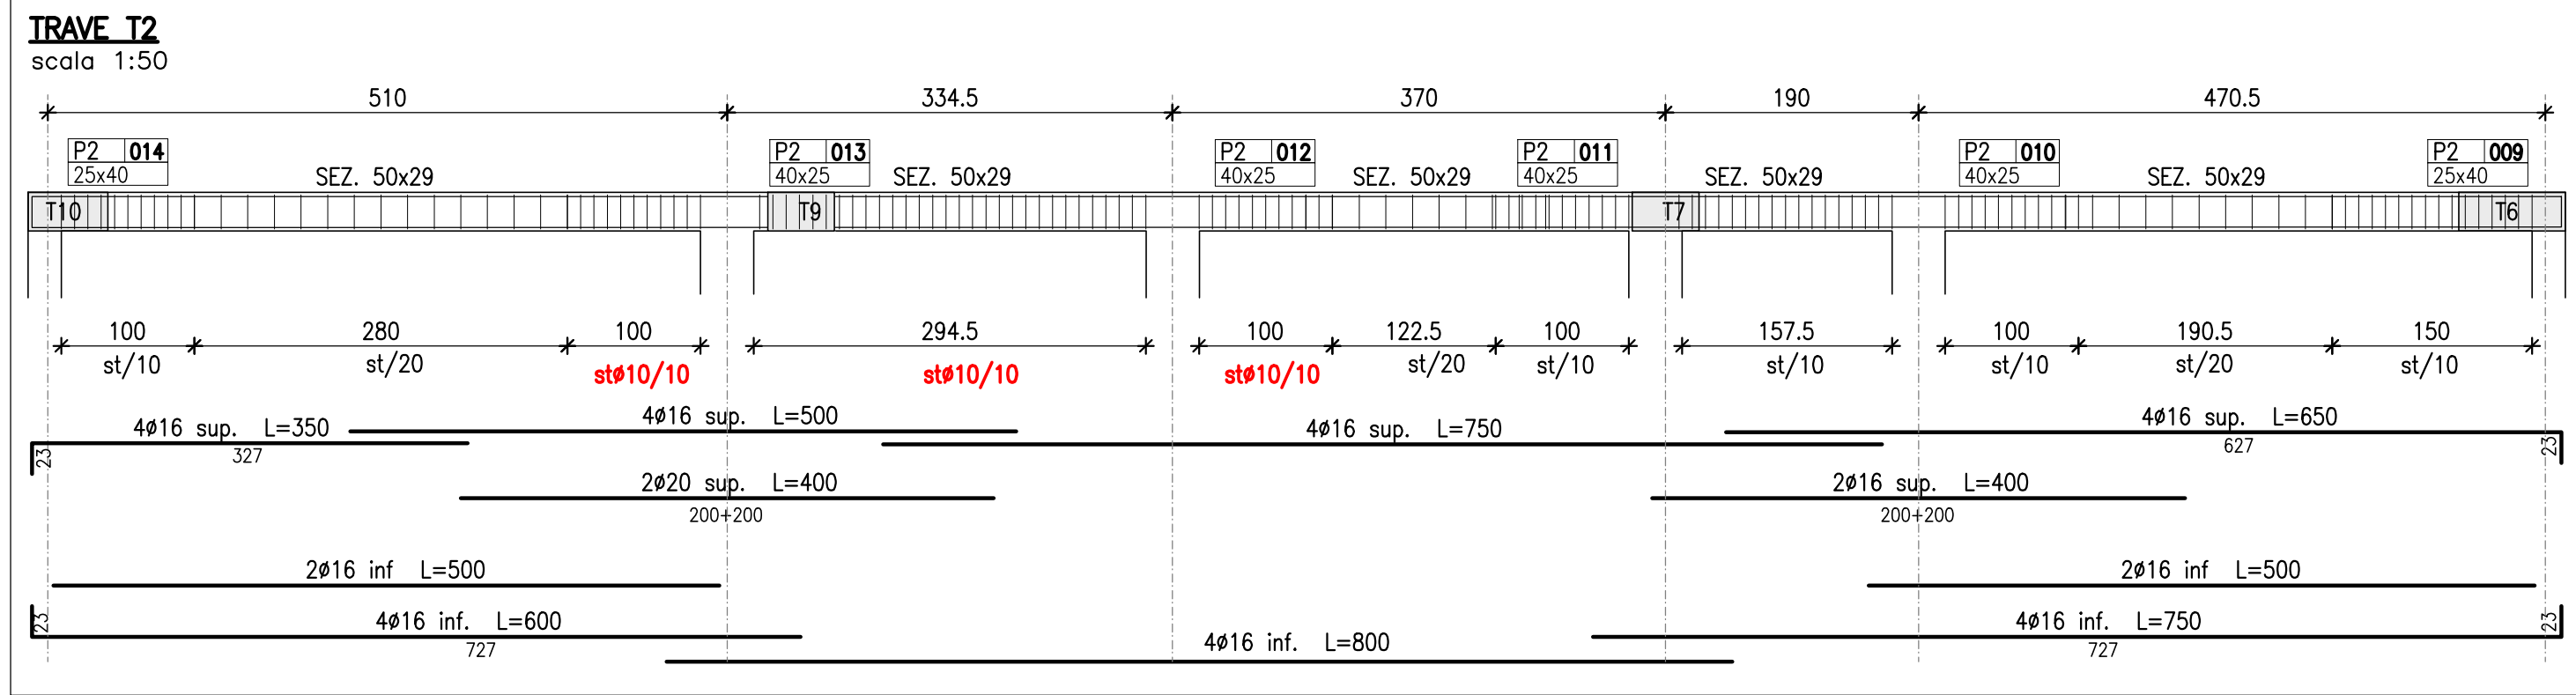
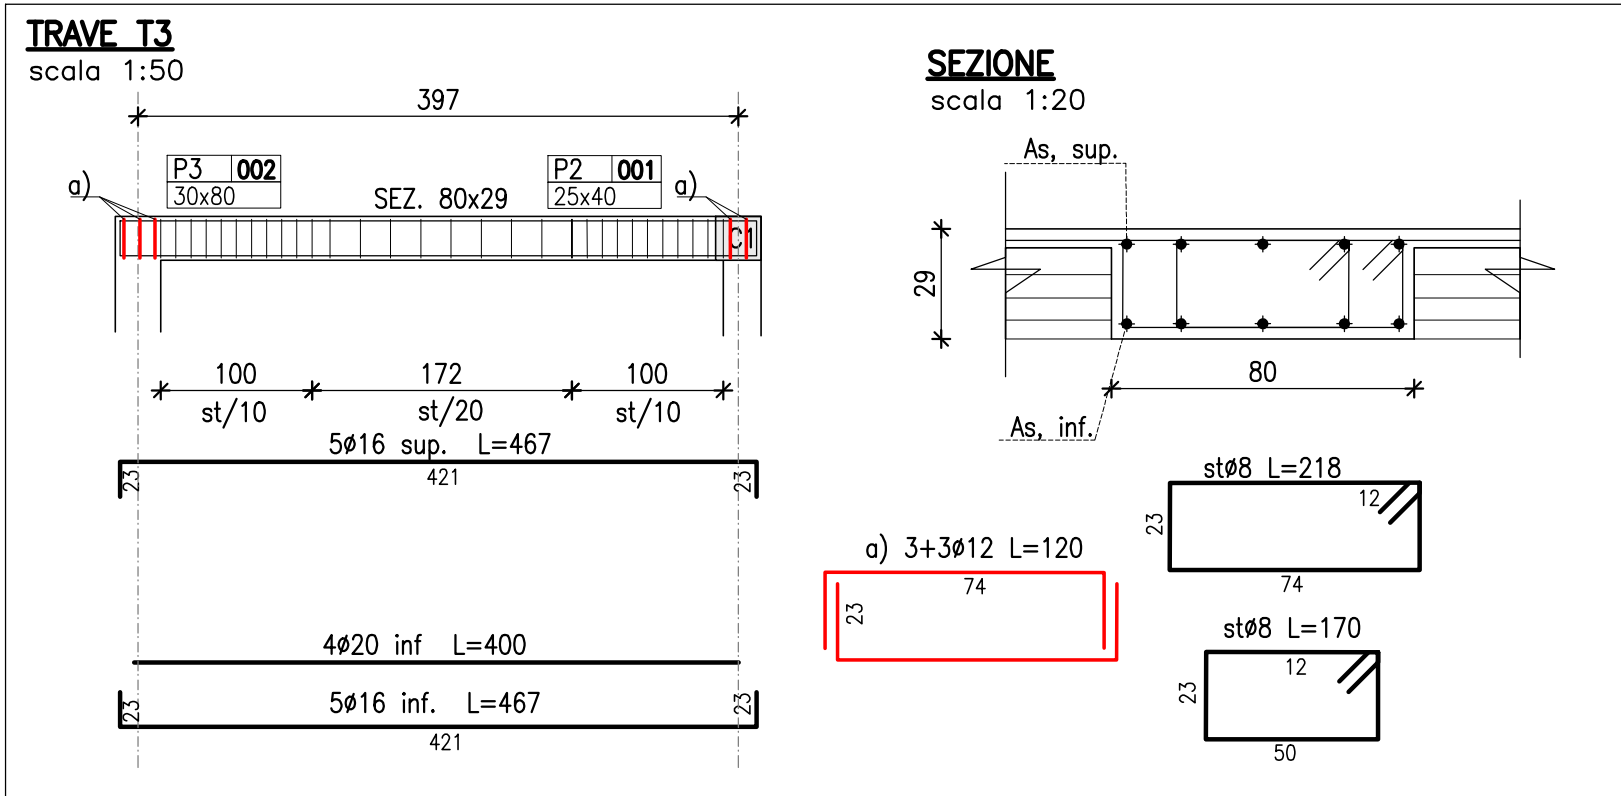
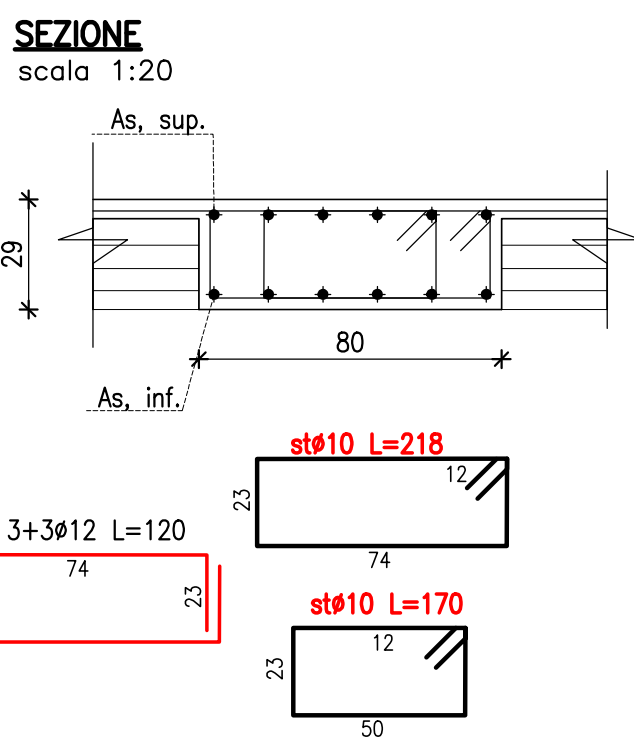


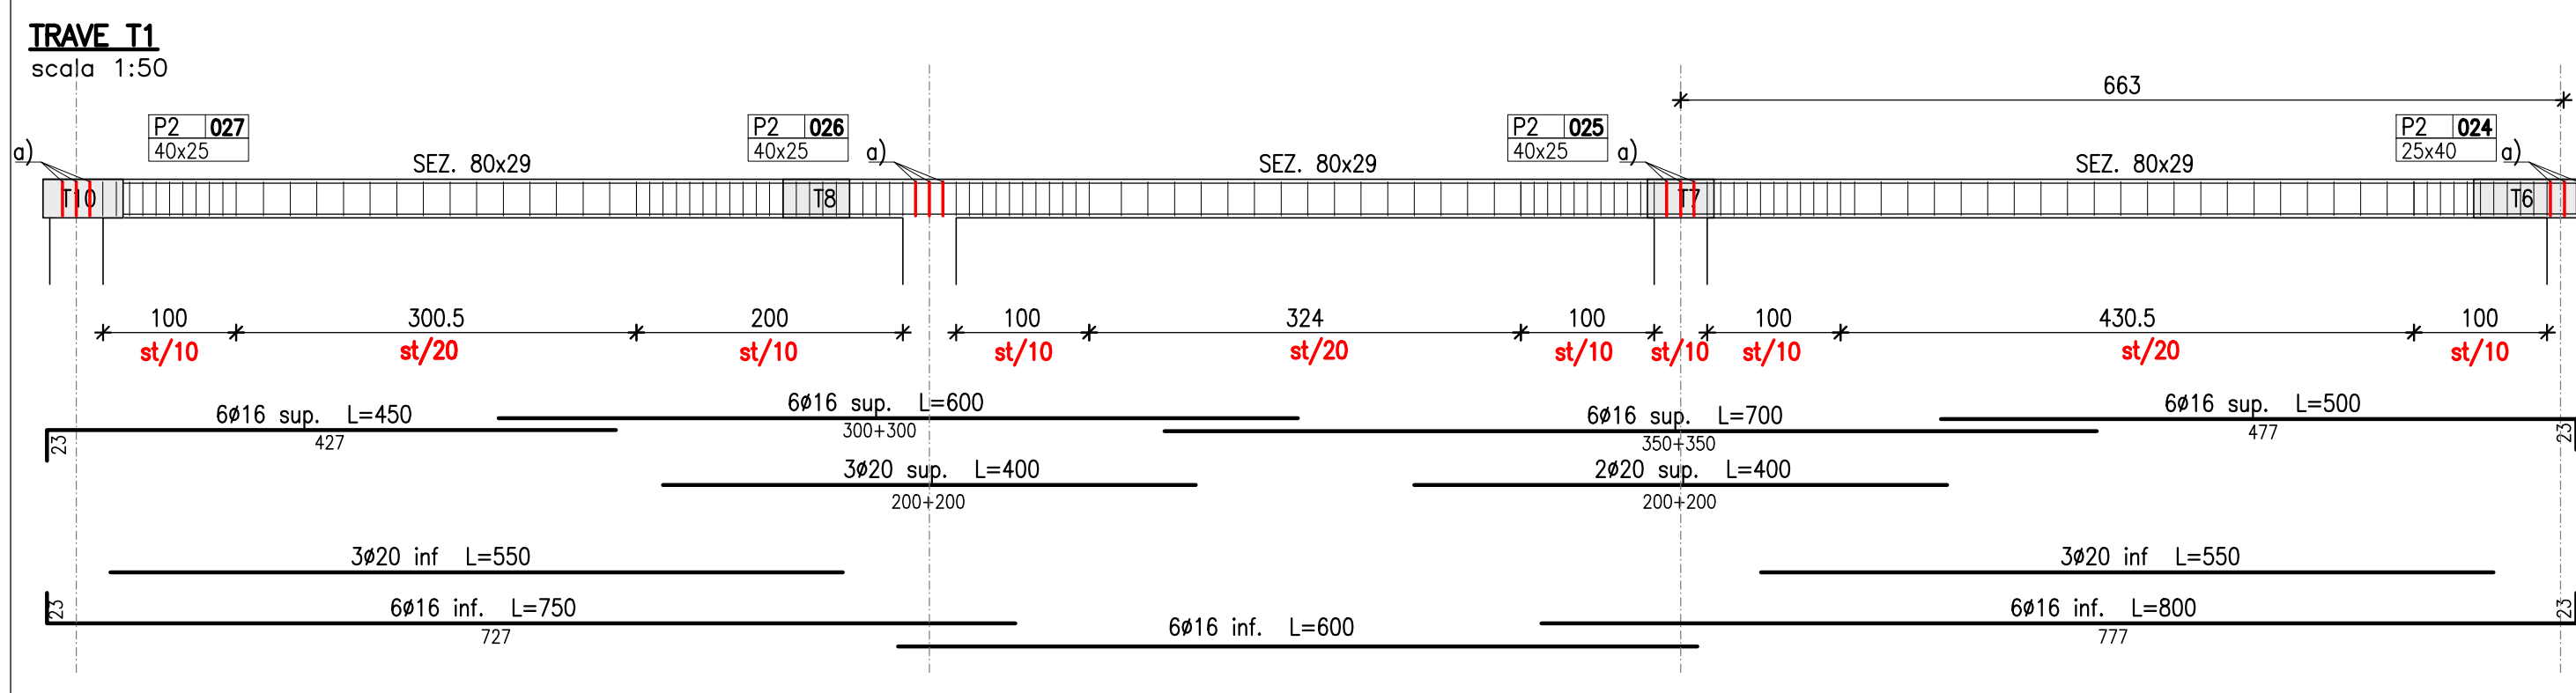

TAVOLE DI RIFERIMENTO		
S00		SPECIFICHE TECNICHE
S01		PIANTA TRACCIAMENTO
S02	*	PIANTA FONDAZIONI
S03	*	PIANTA PRIMO IMPALCATO
S04	*	PIANTA SECONDO IMPALCATO
	S04a	TRAVI SECONDO IMPALCATO
S05	*	PIANTA COPERTURA
S06		ABACO PILASTRI
S07		VANO SCALA E ASCENSORE
*		ATTENZIONE!!! BLOCCO TAVOLE ELEMENTO STRUTTURALE

PER SPECIFICHE MATERIALI E DETTAGLI COSTRUTTIVI VEDERE TAVOLA ES-00-00_SPECIFICHE TECNICHE

GB&PARTNERS
SCIENZE, PROGETTI, IMMOBILIARI
Architettura, Ingegneria, Urbanistica, Urbanistica, Urbanistica
Via S. Maria 10 - 20122 Milano
Tel. 02 58 39 07 77
E-mail: gb&partners@gb&partners.it

Progetto strutturale:
Ing. Alessandro Bertozzi
Piazza Alpi, 2
25039 Travagliato (BS)
Cell. 3890777193
E-mail: alessandro@bertozzingegneria.it

COMUNE DI COLOGNO MONZESE (MI)
AREA Ex TORRIANI ARAS 01
PROGETTO ESECUTIVO
Progetto Servizi Abitativi Pubblici di via Pergolesi

N°	DATA	DESCRIZIONE MOTIVAZIONE DELL'AGGIORNAMENTO	STUDIO	DIS.
00	22/05/2025	Prima emissione	STEN	ST
01	26/01/2026	Modifica architettonica 260118	STEN	ST

Progetto
PROGETTO ESECUTIVO

Servizi Abitativi Pubblici
Comune di Cologno Monzese(MI)

Proponente
Officine Mak S.r.l.
Corso Europa, 10
Milano 20122

Scala
1:50
Data
22/05/2025

Tipo tavola
ESECUTIVI
Serie
STRUTTURE
Titolo
TRAVI COPERTURA

Tavola nr.
Tipo
Tavola
Serie
Sigla /
Serie
Numero /
Variante
Abb.

E
S
05a
00

Orientamento