


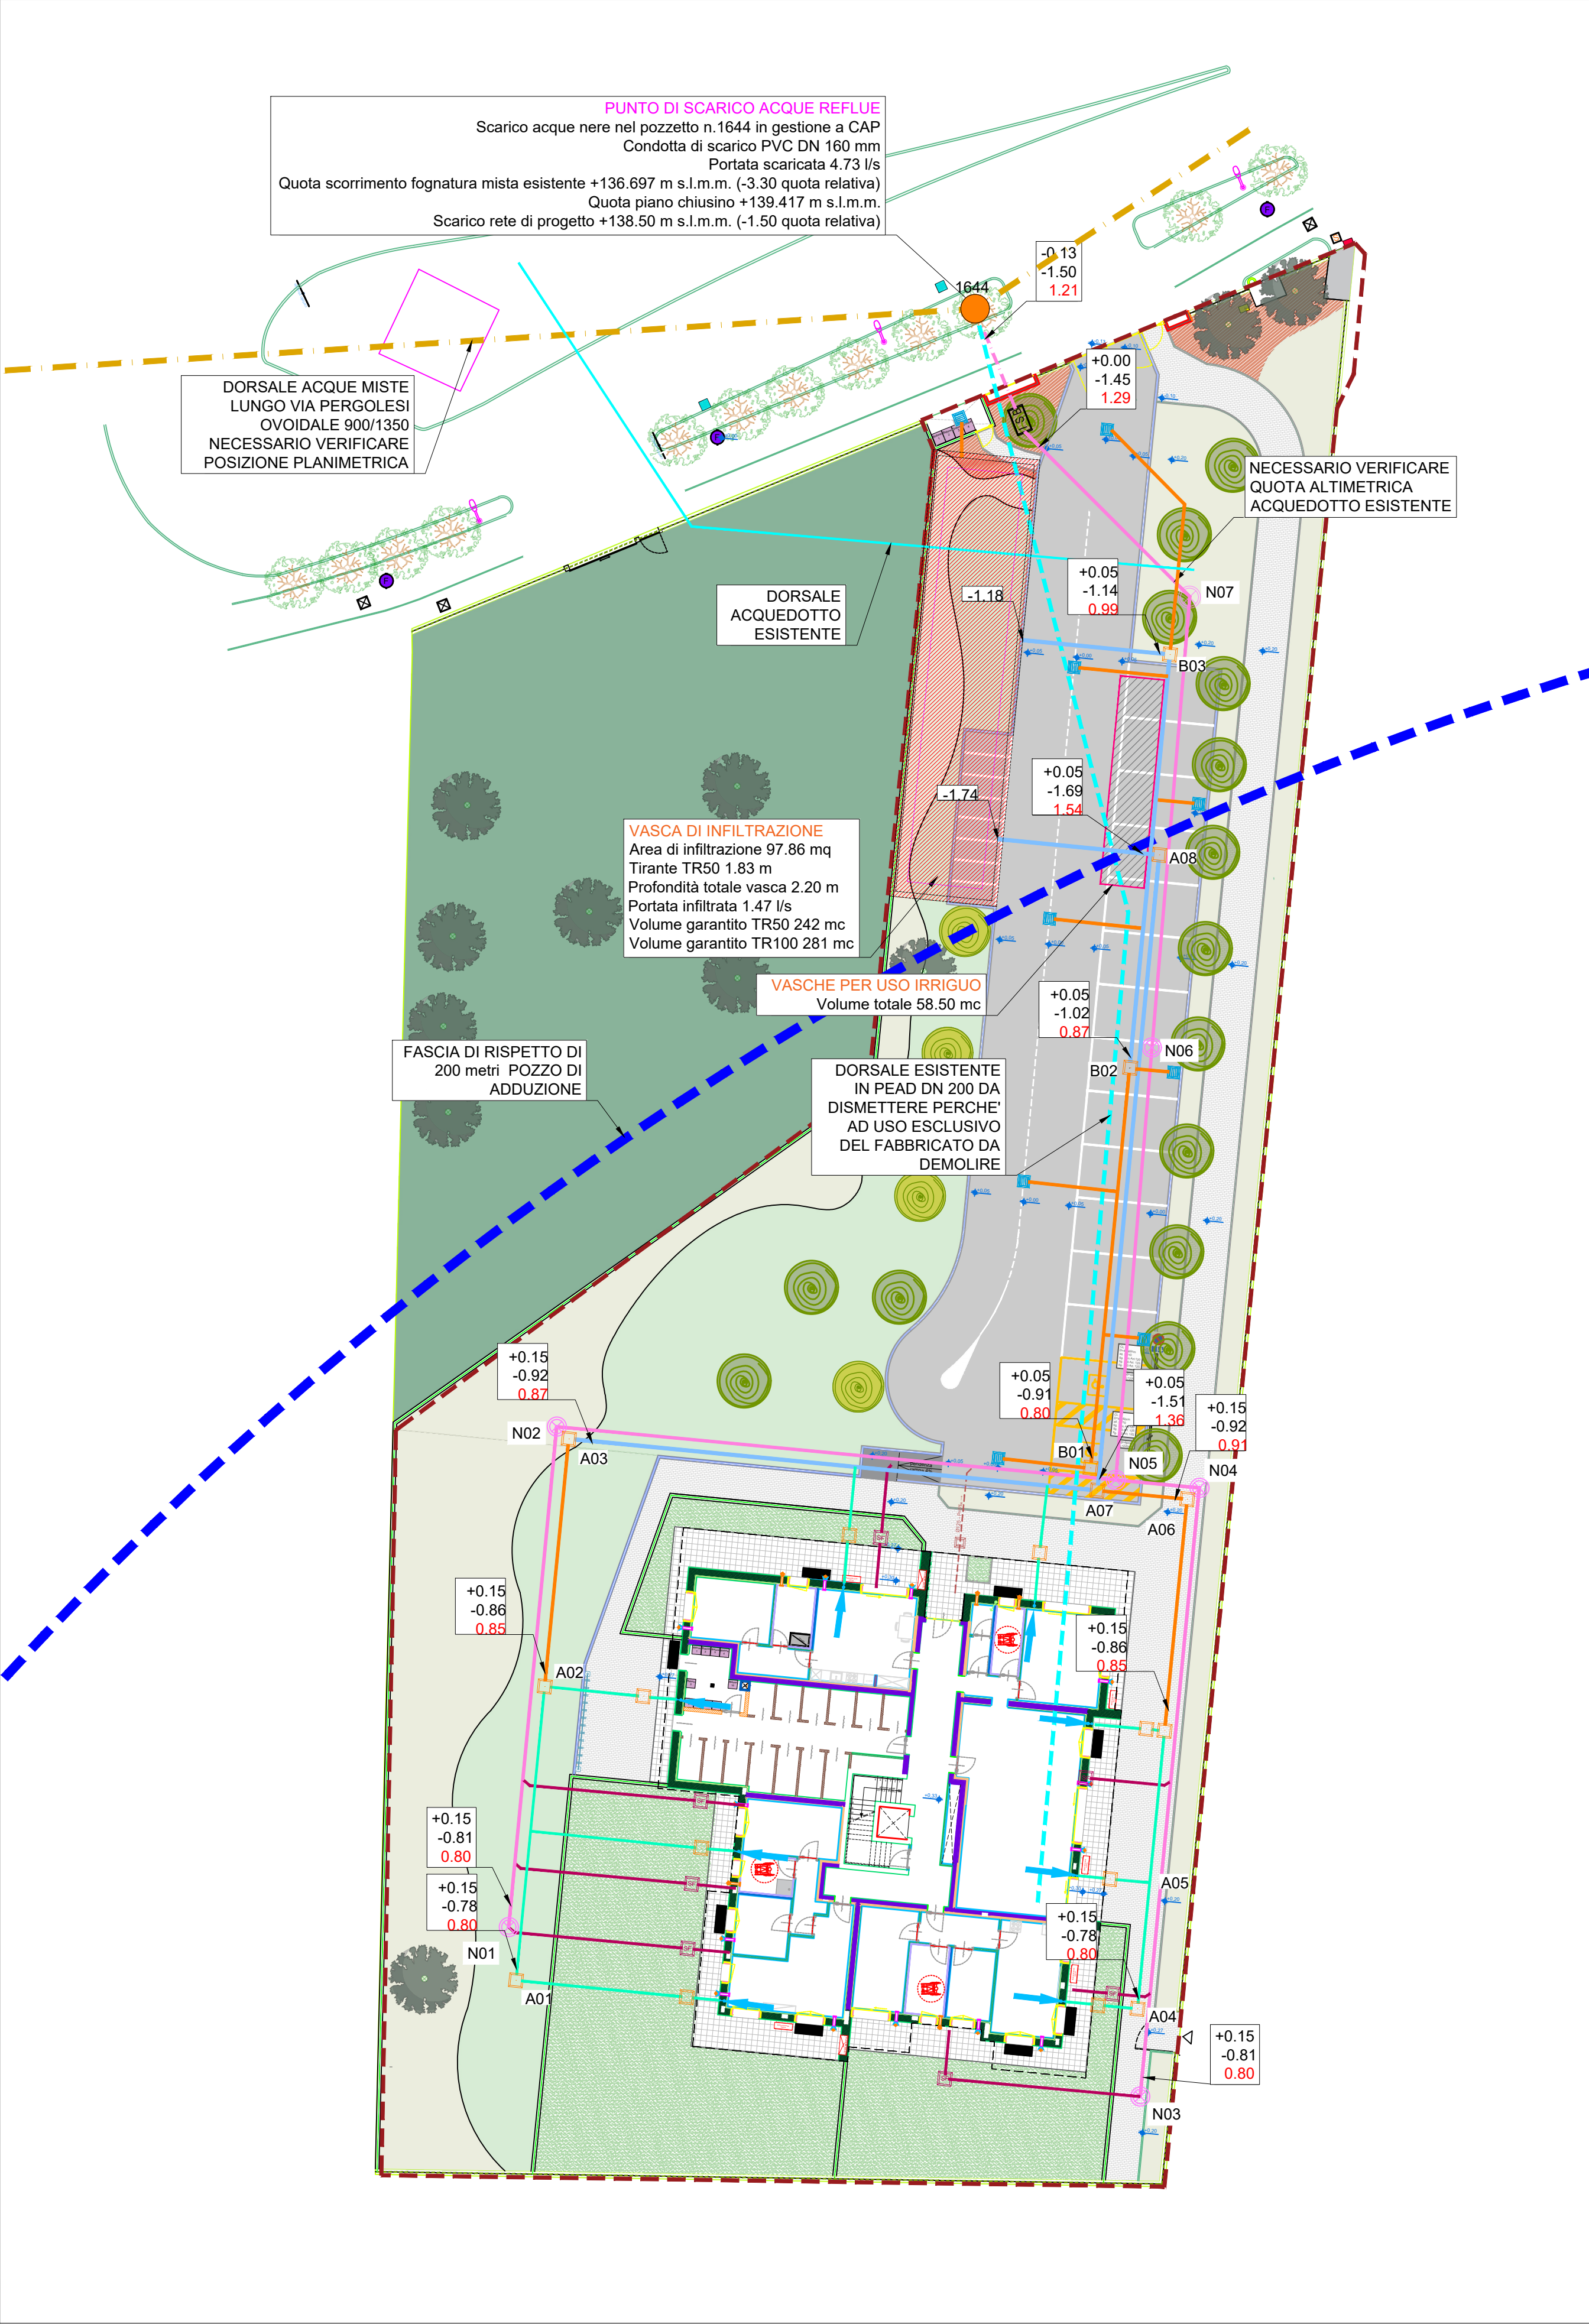

RETE ACQUE METEORICHE

- Area oggetto di intervento
- PVC 125, i=0.5%
- PVC 160, i=0.5%
- PVC 200, i=0.5%
- Condotta esistente acque miste PEAD DN 200 mm da smettere perchè a servizio del fabbricato da demolire
- Condotta esistente acque miste su via Pergolesi in cls ovoidale 900/1350
- Acquedotto esistente
- caditoia di progetto
- pozzetto di ispezione cls 60x60 cm
- immissione pluviale
- n. cameretta esistente su dorsale acque miste
- +0.40 Quota stato di progetto +0.00 = +140.00 m s.l.m.
- +0.273 Quota stato di fatto +0.00 = +140.00 m s.l.m.
- +0.14 Quota relativa di progetto
- 1.52 Quota scorrimento condotta
- 1.26 Ricoprimento

RETE ACQUE REFLUE

- collettore al piede della colonna di scarico PVC Ø 125 mm SN8 (acque nere)
- pozzetto 60x60 cm con sifone Firenze Ø 125 mm (acque nere)
- linea interna PVC Ø 160 mm SN8, i=0.5%
- pozzetto di ispezione cls Ø80 cm
- Condotta esistente acque miste su via Pergolesi in cls ovoidale 900/1350
- +0.05 Quota relativa di progetto
- 1.34 Quota relativa scorrimento condotta
- 1.13 Ricoprimento
- +0.40 Quota stato di progetto +0.00 = +140.00 m s.l.m.
- +0.273 Quota stato di fatto +0.00 = +140.00 m s.l.m.

GB&PARTNERS
SERVIZI E PROGETTI IMMOBILIARI

Via Virgilio 37, 20145 Codogno (LO)
Telefono 0377 436099 - 0377 34691 - Fax 0377 436654
E-mail amministrazione@gbpartners.it - tecnico@gbpartners.it
www.gbpartners.it

iscritto all'Albo dei Geometri n. 10092
Pavia (PA) - C.F. 01991590152
C.S. € 11.110,00

UNI EN ISO 9001:2015
UNI EN ISO 14001:2015

N°	DATA	DESCRIZIONE MOTIVAZIONE DELL'AGGIORNAMENTO	STUDIO	DIS.
00	26/06/2025	Prima emissione	AequaEng.	
01	23/01/2026	Revisione	AequaEng.	
02	03/02/2026	Revisione	AequaEng.	

Il Progettista

Aequa Engineering
Ing. GIUSEPPE BALDO
C.F. PAVA OBereggenze
GEOMETRI LEGALE ED OPERATIVA
Via Virgilio 1, 20145 Codogno (LO)
Tel/Fax +39 0377 436099
www.aequaeng.it

Progetto ARAS 01 AREA EX TORRIANI PIANO ATTUATIVO COMUNE DI COLOGNO MONZESE VIA PERGOLESI	Committente Officine Mak S.r.l. Corso Europa, 10 Milano 20122	Scala 1:250 Data 03/02/2026
---	--	--

Tipo tavola	Tavola nr.
Serie ESECUTIVO	Tipo ES
	Serie
	Numero 03
	Agg 00

Titolo
PLANIMETRIA RETI ACQUE METEORICHE E REFLUE

Orientamento